

ARCHITECT

CONSULTANTS

M/E/P ENGINEER

STRUCTURAL ENGINEER
(FOUNDATION)


BUILDING SHELL PRE-FAB +
SHELL STRUCTURAL ENGINEER

DRAWING INDEX

CS	COVER PAGE		
LS1	LIFE SAFETY PLAN		
AS1.1	ARCHITECTURAL SITE PLAN		
AS2.1	MENU SIGN DETAILS SINGLE/DOUBLE DRIVE-THRU		
AS2.2	SITE DETAILS - TRASH ENCLOSURE CMU		
AS2.3	SITE DETAILS		
AS2.4	SITE DETAILS		
A1	FLOOR PLAN AND SCHEDULES		
A2	EQUIPMENT PLAN AND SCHEDULE	S0.1	STRUCTURAL NOTES
A3	REFLECTED CEILING PLAN	S0.2	SPECIAL INSPECTIONS
A4	ROOF PLAN AND DETAILS	S1.1	FOUNDATION PLAN
A4.1	ROOF DETAILS	S1.2	STRUCTURAL FOUNDATION SECTIONS
A5	EXTERIOR ELEVATIONS		
A5.1	EXTERIOR ELEVATIONS	E1.0	ELECTRICAL GENERAL NOTES AND LEGEND
A6	BUILDING SECTIONS	E1.1	ELECTRICAL LIGHTING PLAN
A6.1	WALL SECTIONS	E1.2	ELECTRICAL POWER PLAN
A6.2	WALL SECTIONS	E1.3	ELECTRICAL ROOF PLAN
A6.3	WALL SECTIONS	E1.4	ELECTRICAL POS PLAN
A7	SECTION DETAILS	E1.5	ELECTRICAL SECURITY PLAN
A7.1	SECTION DETAILS	E1.6	ELECTRICAL FIRE ALARM PLAN
A7.2	PLAN DETAILS	ES0.1	ELECTRICAL SITE PLAN
A8	DETAILS	E2.1	ELECTRICAL SCHEDULES
A9	N/A	E2.1OPT	ELECTRICAL SCHEDULES
A9.1	INTERIOR ELEVATIONS	E3.1	ELECTRICAL DETAILS
A9.2	INTERIOR ELEVATIONS	E3.2	ELECTRICAL DETAILS
A9.3	WASHROOM DETAILS	E4.1	ELECTRICAL ENERGY CALCS
A10	TILE PLAN AND FINISHING SCHEDULE	E4.2	ELECTRICAL ENERGY CALCS
A11	DOOR AND WINDOW SCHEDULES	ES.1	ELECTRICAL SPECIFICATIONS
		ES.2	ELECTRICAL SPECIFICATIONS
SP1	ARCHITECTURAL SPECIFICATIONS		
SP2	ARCHITECTURAL SPECIFICATIONS	M1.1	MECHANICAL PLAN
SP3	ARCHITECTURAL SPECIFICATIONS	M1.2	MECHANICAL ROOF PLAN
SP4	ARCHITECTURAL SPECIFICATIONS	M2.1	MECHANICAL SCHEDULE
SP5	ARCHITECTURAL SPECIFICATIONS	M3.1	MECHANICAL HOOD DRAWINGS
SP6	ARCHITECTURAL SPECIFICATIONS	M3.2	MECHANICAL HOOD DRAWINGS
SP7	ARCHITECTURAL SPECIFICATIONS	M4.1	MECHANICAL DETAILS
		MS.1	MECHANICAL SPECIFICATIONS
FAB1	ELEVATIONS		
FAB2	BUILDING SECTIONS	P1.1	PLUMBING SCHEDULES AND NOTES
FAB3	WALL SECTIONS	P2.1	PLUMBING PLAN - SANITARY WASTE & VENT PLAN
		P2.2	PLUMBING PLAN - DOMESTIC WATER
FBS0	COVER SHEET	P2.3	PLUMBING PLAN - NATURAL GAS
FBS1	BOLT PLAN	P2.4	PLUMBING PLAN - STORM PIPING
FBS2	WALL FRAMING PLAN	P3.1	PLUMBING RISERS
FBS3	ROOF FRAMING PLAN	P4.1	PLUMBING DETAILS
FBS4	DETAILS	P4.2	PLUMBING DETAILS
FBS4.1	DETAILS	PS.1	PLUMBING SPECIFICATIONS

UTILITY SERVICE REQUIREMENTS

ELECTRICAL: (PROVIDING AGENCY) POWER: 208V / 3-PHASE / 4W / 600 AMPS TOTAL CONNECTION LOAD: 220.53 KVA TOTAL NOTE: SEE SHEET E3 FOR BREAKDOWN OF THE ELECTRICAL SERVICE CONNECTED LOAD.			
TELEPHONE: (PROVIDING AGENCY) 2" CONDUIT 25 PAIR WIRE - (OWNER REQUIREMENT)			
WATER: (PROVIDING AGENCY) WATER SERVICE: 11.5 DIAM 7.5 GPM			
IRRIGATION: (PROVIDING AGENCY) LANDSCAPING: (VERIFY WITH OWNER IF USED). SIZE PER ZONE - REFER TO PLAN FOR DESIGN			
SEWER: (PROVIDING AGENCY) WASTE SERVICE: SANITARY LINE: 4" DIAM. GREASE LINE: 4" DIAM.			
GAS: (PROVIDING AGENCY) NATURAL GAS SERVICE: 3" GAS LINE, 7" TO 8" WC OUTLET GAS LOAD: 1,700 MBH NOTE: SEE SHEET P3 FOR A BREAKDOWN OF THE GAS LOADS.			
GENERAL NOTE: VERIFY ALL SERVICE REQUIREMENTS WITH THE LOCAL UTILITY CITY AGENCIES.			

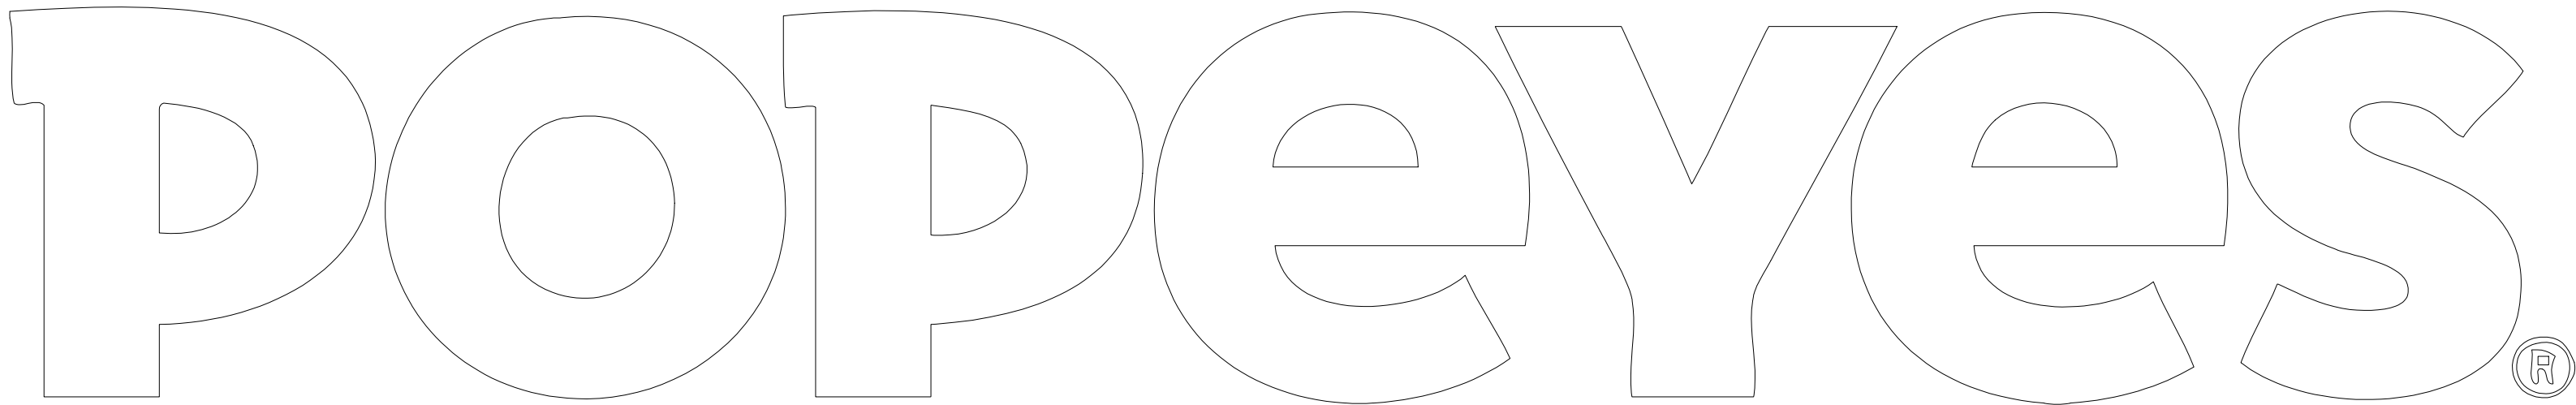

LOUISIANA KITCHEN
DTGO PROTOTYPE
ADDRESS
CITY, STATE

DESIGNER NOTES:
MODIFY PER SPECIFIC PROJECT

PROJECT RESPONSIBILITY CHART			
ITEM	SUPPLY		INSTALL
	OWNER	GC	OWNER GC
EQUIPMENT	●		●
SMALLWARE	●		●
EXTERIOR SIGNS (DIRECT, PYLON)	●		●
BLDG. SIGN INTERNALLY ILLUMINATED	●		●
DRINK SYSTEM	●		●
CO TANK (IF APPLICABLE)	●		●
SECURITY SYSTEMS	●		●
DRIVE THRU SYSTEM	●		●
POINT OF SALE SYSTEM	●		●
POPEYES RADIO - MUZAK / RETAIL RADIO	●		●
FLAT SCREEN TV (ORDER READY BRD.)	●		●
METAL PACKAGE: CLEARANCE BAR, DUMPSTER GATE, RAILING, SHUTTERS, AWNINGS, INTERIOR ROOF LADDER, DRIVE-THRU WINDOW CANOPY, AND REAR ENCLOSURE GATE.	●		●
CORNER GUARDS	●		●
BUILDING SIGN (VERIFY WITH OWNER)	●		●
FRONT COUNTERS/SOLID SURFACES AND MATCHING BACKSPLASH	●		●
DRIVE-THRU WINDOW		●	●
RESTROOM FIXTURES & ACCESSORIES - SEE SHEET A9.3		●	●
HVAC SYSTEM		●	●
LIGHTING PACKAGE		●	●
ROOFING		●	●
INTR. DECOR/FURNITURE SUPPLIER: SEATING PACKAGE, ARTWORK, OFFICE CABINETS, WD. WALL FRAMES, WINDOW SILLS, AND P.-RING	●		●
STOREFRONT		●	●
FACE BRICK/THIN BRICK		●	●
NICHHA VENEER		●	●
EIFS/STUCCO		●	●
PAINT/STAINS		●	●
FRYER GREASE REMOVAL SYSTEM (IF NEW) (VERIFY WITH OWNER)	●		●
WATER HEATER		●	●
20 GA S/S AT DRIVE THRU		●	●
S/S CEILING PANELS AND TRIM (VERIFY SIZE WITH LOCAL AUTHORITY)		●	●
MENUBOARDS (DIGITAL.)	●		●
MENUBOARDS (D.T. - PREVIEW BD.)	●		●
DRIVE-THRU LOOP SYSTEM	●		●
INTERIOR SIGNS	●		●
INTERIOR TILE		●	●
DOOR AND DOOR HARDWARE		●	●
RESPONSIBILITY MATRIX NOTES: 1. GC PROJECT RESPONSIBILITIES TO BE VERIFIED AND FINALIZED WITH OWNER PRIOR TO BIDDING AND AT PRE-CONSTRUCTION MEETING. 2. TYPE OF BUILDING SIGN TO BE DECIDED DURING THE PRE-CONSTRUCTION MEETING. 3. FURNITURE SUPPLIER TO INCLUDE ALL WINDOW SILLS AND WOOD CORNER GUARDS IN DINING AREA. 4. PAPER TOWELS AND SOAP REPLENISHMENT ARE THE RESPONSIBILITY OF THE OWNER UNDER A SEPARATE AGREEMENT WITH A SUPPLIER.			

ABBREVIATIONS

BOH:	BACK OF HOUSE	N/A:	NOT APPLICABLE
C/W:	COMPLETE WITH	O.C.	ON CENTER
CL:	CENTER LINE	OH:	OPPOSITE
CONC:	CONCRETE	P-LAM:	PLASTIC LAMINATE
CPM:	CONSTRUCTION PROJECT MANAGER	S.F.C:	STORE FIXTURE COMPANY
CT:	CERAMIC TILE	SPEC:	SPECIFICATION
DMB:	DIGITAL MENU BOARD	SIM.:	SIMILAR
EQ:	EQUAL	T/O:	TOP OF
FOH:	FRONT OF HOUSE	T.B.A:	TO BE DETERMINED
G.C:	GENERAL CONTRACTOR	TYP.:	TYPICAL
MAX.:	MAXIMUM	U/S:	UNDERSIDE
MIN.:	MINIMUM	WRM.:	WASHROOM

CODE INFORMATION																													
FIRM NAME:		THE ARCHITECT NOTED ABOVE HAS EXERCISED RESPONSIBLE CONTROL, WITH RESPECT TO DESIGN ACTIVITIES.																											
NAME OF PROJECT: POPEYES - DTGO MODEL																													
LOCATION: ADDRESS																													
1	APPLICABLE CODES	BUILDING : PLUMBING : FIRE : MECHANICAL : ELECTRICAL : ACCESSIBILITY : ENERGY :	2024 INTERNATIONAL BUILDING CODE 2024 INTERNATIONAL PLUMBING CODE 2024 INTERNATIONAL FIRE CODE 2024 INTERNATIONAL MECHANICAL CODE 2023 NATIONAL ELECTRICAL CODE, NFPA 70 2017 ICC/A117.1 ACCESSIBILITY 2024 INTERNATIONAL ENERGY CONSERVATION CODE																										
2	ZONING CLASSIFICATION	C1 - COMMERCIAL																											
3	OCCUPANCY CLASSIFICATION	B - (COMMERCIAL KITCHEN) WITH NO MIXED USE OCCUPANCIES																											
4	CONSTRUCTION TYPE	V-B COMBUSTIBLE MATERIALS, UNPROTECTED																											
5	BUILDING AREA	ALLOWED : 9,000 SQ. FT.	PROVIDED : 1,828 SQ. FT.																										
6	BUILDING HEIGHT	ALLOWED : 40'-0" HIGH	PROVIDED : 18'-0" HIGH																										
7	SCOPE OF WORK STATEMENT	NEW BUILD CONSTRUCTION																											
8	OCCUPANCY CALCULATIONS	<table><thead><tr><th>FLOOR</th><th>USE</th><th>SQUARE FOOTAGE</th><th>OCCUPANT LOAD FACTOR</th><th>NUMBER OF OCCUPANTS</th></tr></thead><tbody><tr><td>1 OF 1</td><td>KITCHEN</td><td>1183 SQ. FT</td><td>200 GROSS</td><td>6</td></tr><tr><td>1 OF 1</td><td>TOILET ROOM</td><td>56 SQ. FT</td><td>150 GROSS</td><td>1</td></tr><tr><td>1 OF 1</td><td>STORAGE</td><td>140 SQ. FT</td><td>300 GROSS</td><td>1</td></tr><tr><td colspan="4">TOTAL NUMBER OF OCCUPANTS:</td><td>8</td></tr></tbody></table>			FLOOR	USE	SQUARE FOOTAGE	OCCUPANT LOAD FACTOR	NUMBER OF OCCUPANTS	1 OF 1	KITCHEN	1183 SQ. FT	200 GROSS	6	1 OF 1	TOILET ROOM	56 SQ. FT	150 GROSS	1	1 OF 1	STORAGE	140 SQ. FT	300 GROSS	1	TOTAL NUMBER OF OCCUPANTS:				8
FLOOR	USE	SQUARE FOOTAGE	OCCUPANT LOAD FACTOR	NUMBER OF OCCUPANTS																									
1 OF 1	KITCHEN	1183 SQ. FT	200 GROSS	6																									
1 OF 1	TOILET ROOM	56 SQ. FT	150 GROSS	1																									
1 OF 1	STORAGE	140 SQ. FT	300 GROSS	1																									
TOTAL NUMBER OF OCCUPANTS:				8																									
9	EGRESS CALCULATION	TOTAL OCCUPANTS 8	CALCULATED MIN. EGRESS (1005.1) 20' X 8' = 168' "	MIN. EGRESS WIDTH REQUIRED (32" MIN.) 78' "																									
10	EXITS	TOTAL REQUIRED : 1	TOTAL PROVIDED : 2	EGRESS WIDTH PER EXIT : 33" CLEAR & 45" CLEAR																									
11	FIRE RESISTIVE REQUIREMENTS	LOSS OF ONE REQUIRED MEANS OF EGRESS SHALL NOT REDUCE THE EGRESS CAPACITY TO LESS THAN 50% OF REQUIRED																											
		EXTERIOR BEARING WALL : ROOF CONSTRUCTION : CEILING :	(0 HOUR) (0 HOUR) (0 HOUR)																										
12	SPRINKLER SYSTEM	___ ENTIRE BUILDING (EXISTING) ___ IN LIEU OF ROOF RATING ___ BASEMENT ONLY ___X_ NOT REQUIRED / NOT PROVIDED																											
13	FIRE ALARM	NOT REQUIRED																											
14	MAX. TRAVEL DISTANCE	200'																											
15	PLUMBING REQUIREMENT	WATER CLOSETS LAVATORIES SERVICE SINK DRINKING FOUNTAIN PUBLIC ACCESS UNISEX IS PERMITTED	MALE 1 PER 25 FOR THE FIRST 50 & 1 PER 50 FOR THE REMAINDER EXCEEDING 50 - 1 REQUIRED 1 PER 40 FOR THE FIRST 80 & 1 PER 80 FOR THE REMAINDER EXCEEDING 80 - 1 REQUIRED 1 SERVICE SINK REQUIRED NOT REQUIRED NA YES	FEMALE 1 PER 25 FOR THE FIRST 50 & 1 PER 50 FOR THE REMAINDER EXCEEDING 50 - 1 REQUIRED 1 PER 40 FOR THE FIRST 80 & 1 PER 80 FOR THE REMAINDER EXCEEDING 80 - 1 REQUIRED NOT REQUIRED NA YES																									

DESIGNER NOTES: MODIFY CODE AND SECTION AS REQUIRED PER SPECIFIC PROJECT
DESIGNER NOTES: ADD KEY PLAN PER SPECIFIC PROJECT
KEY PLAN N.T.S.

CONTRACTORS NOTE

CONTRACTORS ARE TO CONTACT THE CONSTRUCTION PROJECT MANAGER AS INDICATED IN THE WRITTEN SCOPE OF WORK FOR BIDDERS LIST. FOR APPROVED SUPPLIERS LIST, NATIONAL ACCOUNT PHONE NUMBERS AND CONTRACTORS REFER TO SPECIFICATION DRAWINGS.

DESIGNER NOTES:
MODIFY PER SPECIFIC PROJECT


PROJECT NO.: XXXXXX
POPEYES NO.: RN.XXXXXX

DESIGNER NOTES:
ANY REQUEST OR REQUIREMENTS FOR DESIGN REVISIONS THAT DEVIATE FROM THE PROVIDED PROTOTYPE DRAWING SET WILL REQUIRE THE ARCHITECT OR ENGINEER OF RECORD TO SUBMIT THE REQUESTED REVISIONS TO THE POPEYE'S DESIGN TEAM AT (DESIGNTEAM@POPEYES.COM) FOR REVIEW AND APPROVAL PRIOR TO SUBMISSION FOR PERMITS.

DESIGNER NOTES:
THESE DOCUMENTS ARE NOT FOR PERMIT OR CONSTRUCTION.

THESE DOCUMENTS MUST BE COMPLETED AND/OR MODIFIED BY A LICENSED ARCHITECT AND ENGINEER TO CONFORM TO ALL LOCAL AND APPLICABLE CODES AND SPECIFIC SITE CONDITIONS. THERE IS NO WARRANTY, WHETHER IMPLIED OR EXPRESSED, THAT THESE DOCUMENTS MEET THE APPLICABLE CODE REQUIREMENTS. LIABILITY FOR THE DESIGN AND ANY USE OF DOCUMENTS IS THE SOLE RESPONSIBILITY OF THE ARCHITECT AND ENGINEER OF RECORD.

ISSUE TABLE		
No.	Date (mm/dd/yy)	Description
01	09-26-25	DTGO PROTOTYPE DOCUMENTS
REVISIONS		
No.	Date	Description
DRAWINGS REVISED AS PER DESIGN BULLETIN		
No.	Date	Description
THIS DRAWING IS OWNED BY OR LICENSED FOR USE BY POPEYES LOUISIANA KITCHEN (OR ITS AFFILIATED OR RELATED COMPANIES) AND MAY NOT BE REPRODUCED, USED, DOWNLOADED, DISSEMINATED, PUBLISHED, OR TRANSFERRED IN ANY FORM OR BY ANY MEANS, EXCEPT WITH THE PRIOR WRITTEN CONSENT OF POPEYES LOUISIANA KITCHEN. COPYRIGHT INFRINGEMENT IS A VIOLATION OF FEDERAL LAW SUBJECT TO CRIMINAL AND CIVIL PENALTIES.		
THE CONTRACTOR IS TO VERIFY ALL DIMENSIONS AND CONDITIONS ON THE PROJECT AND TO REPORT ANY DISCREPANCIES TO THE POPEYES LOUISIANA KITCHEN REPRESENTATIVE PRIOR TO COMMENCING WORK. THESE DRAWINGS ARE NOT TO BE USED FOR CONSTRUCTION PURPOSES UNLESS INDICATED BY POPEYES LOUISIANA KITCHEN AS "ISSUED FOR CONSTRUCTION".		
Professional Seal DESIGNER NOTES: DESIGN GUIDELINE ONLY - NOT FOR PERMIT OR CONSTRUCTION THESE DOCUMENTS MUST BE COMPLETED AND / OR MODIFIED BY A LICENSED ARCHITECT AND ENGINEER TO CONFORM TO ALL APPLICABLE CODES, AND SPECIFIC SITE CONDITIONS. THERE IS NO WARRANTY, WHETHER IMPLIED OR EXPRESSED, THAT THESE DOCUMENTS MEET THE APPLICABLE CODE REQUIREMENTS. LIABILITY FOR THE DESIGN AND ANY USE OF THE DOCUMENTS IS THE SOLE RESPONSIBILITY OF THE ARCHITECT AND ENGINEER OF RECORD.		
Company Logo		
Project		
Store Type US DTGO PROTOTYPE		
Location PROTOTYPE DTGO (U.S.) CITY, STATE		
Drawing Title COVER PAGE		
Drawn XX	Checked XX	
Scale 1/4"=1'-0"	Date ###.###.####	
Project No. XX	Drawing No. CS	

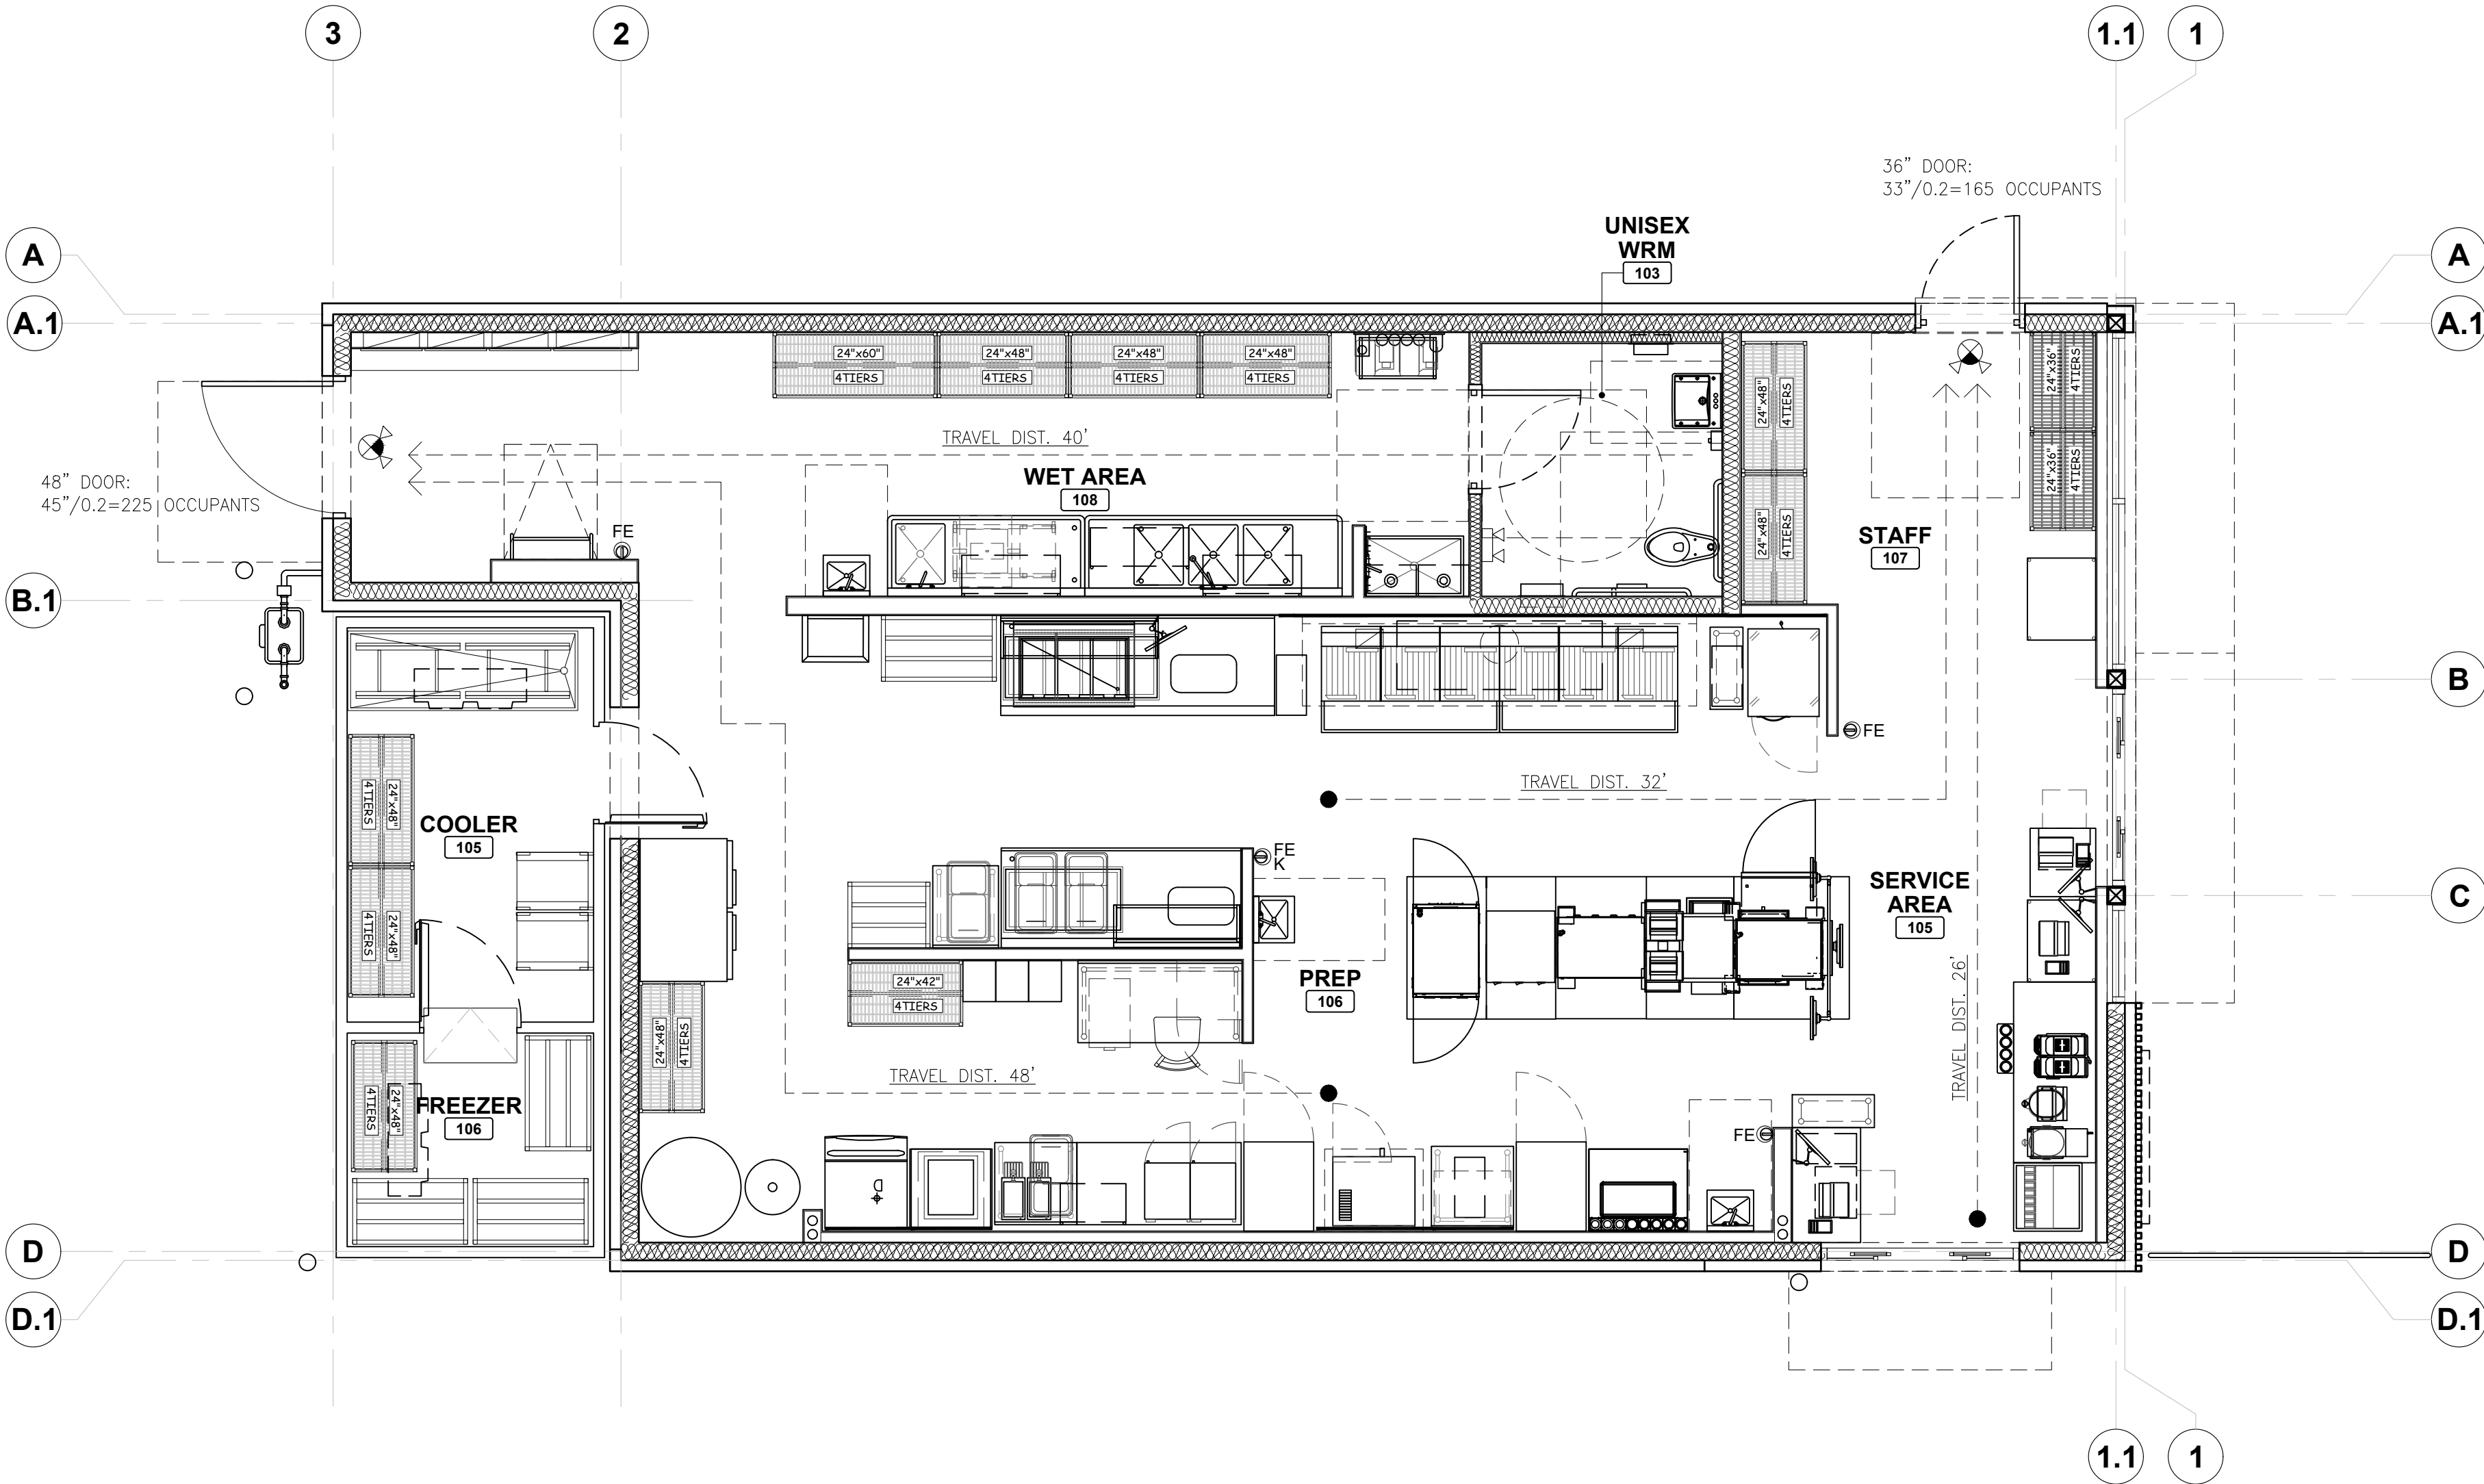

1 LIFE SAFETY FLOOR PLAN
SCALE: 1/4"=1'-0"

LEGEND

	ILLUMINATED EXIT SIGN, ARROW (IF REQUIRED) DENOTES DIRECTION OF EGRESS
	WALL MOUNTED FIRE EXTINGUISHER. FINAL LOCATION BY FIRE INSPECTOR. (K TAG DENOTES K-TYPE EXTINGUISHER)
	EMERGENCY BATTERY PACKS
	PATH OF EGRESS & DISTANCE TO EXIT DOOR

FIRE EXTINGUISHER NOTES

GENERAL PURPOSE FIRE EXTINGUISHER TO BE PROVIDED IN BUILDING, AND WITHIN 75 FEET MAX. TRAVEL DISTANCE FROM ANY POINT.

COOKING EQUIPMENT TYPE FIRE EXTINGUISHER, CLASS K-RATED, TO BE PROVIDED WITHIN 30 FEET MAX. TRAVEL DISTANCE FROM COOKING EQUIPMENT.

FIRE EXTINGUISHER TO BE PROVIDED AS PER THE APPLICABLE NFPA 101 FIRE CODE, APPLICABLE INTERNATIONAL BUILDING CODE (SECTION 906), AND LOCAL JURISDICTIONAL AMENDMENTS, WHICHEVER IS MOST STRINGENT. SEE COVER SHEET FOR CODES.

BASIS OF DESIGN:
GENERAL PURPOSE:
ACTION AIR, SENTRY 10, MODEL AA10S (436500), 10-LB ABC
COOKING EQUIPMENT:
ACTION AIR, K-GUARD, MODEL K01-3 (434909), 6-L ANSULEX LO PH.

FIRE PROTECTION
N/A

FIRE ALARM SYSTEM
FIRE ALARM TO BE PROVIDED. FIRE ALARM SHALL BE EXECUTED AS A DESIGN BUILD COMPONENT FOR THE PROJECT IN ITS ENTIRETY. THE FIRE ALARM CONTRACTOR TO WORK WITH THE GENERAL CONTRACTOR FOR COORDINATING FULL SCOPE OF THE SYSTEM. THE CONTRACTOR SHALL PROVIDE COMPLETE SHOP DRAWINGS AND SPECIFICATIONS FOR THE FIRE ALARM SYSTEM AND BE SUBMITTED TO THE AHJ (AUTHORITY HAVING JURISDICTION) FOR ALL APPROVAL PRIOR TO ANY INSTALLATION.

EMERGENCY LIGHTING
SEE ELECTRICAL SHEETS FOR EMERGENCY LIGHTING AND LAYOUT.

- DOORS**
- ALL EGRESS DOORS DISCHARGE TO THE EXTERIOR AT GRADE LEVEL.
 - ALL DOORS REQUIRED AS EXITS SWING IN THE DIRECTION OF EGRESS, WHERE THERE IS AN OCCUPANT LOAD OF 50 OR MORE (IBC 1010.1.2.1).
 - THE MANUAL PUSH OR PULL ON AN INTERIOR DOOR IN ROUTE OF TRAVEL, OTHER THAN FIRE DOORS, SHALL NOT EXCEED 5 LBS TO OPERATE DOOR (IBC 101.1.3).
- PARTIAL ACCESSIBILITY NOTES**
- ALL AREAS WITHIN PROJECT SCOPE TO BE 100% HANDICAP ACCESSIBLE PER 2017 ICC/A117.1 ACCESSIBILITY CODE.
 - PROJECT HAS TWO (2) FULLY ACCESSIBLE MEANS OF EGRESS.
 - EACH REQUIRED MEANS OF EGRESS SHALL BE CONTINUOUS TO A PUBLIC WAY COMPLYING WITH IBC SECTION 1104.
 - PROJECT HAS FULLY ACCESSIBLE ROUTE FROM MAIN ENTRY TO ALL ACCESSIBLE AREAS (PER IBC 1009.2).
 - PROJECT HAS ONE (1) ACCESSIBLE TOILET ROOMS.

CALCULATIONS

OCCUPANCY CALCULATIONS	FLOOR	USE	SQUARE FOOTAGE	OCCUPANT LOAD FACTOR	NUMBER OF OCCUPANTS
	1 OF 1	KITCHEN	1183 SQ. FT	200 GROSS	6
	1 OF 1	TOILET ROOM	56 SQ. FT	150 GROSS	1
	1 OF 1	STORAGE	140 SQ. FT	300 GROSS	1
	TOTAL NUMBER OF OCCUPANTS:				8
EGRESS CALCULATION	TOTAL OCCUPANTS	CALCULATED MIN. EGRESS (1005.1)	MIN. EGRESS WIDTH REQUIRED	TOTAL EGRESS WIDTH PROVIDED	
	8	20' X 8' = 16.7'	16' (32' MIN.)	75'	
	TOTAL REQUIRED : 1	TOTAL PROVIDED : 2	EGRESS WIDTH PER EXIT : 33' CLEAR (REAR DOOR) 45' CLEAR (SIDE DOOR)		
	LOSS OF ONE REQUIRED MEANS OF EGRESS SHALL NOT REDUCE THE EGRESS CAPACITY TO LESS THAN 50% OF REQUIRED				

ISSUE TABLE

No.	Date (mm/dd/yy)	Description
01	09-26-25	DTGO PROTOTYPE DOCUMENTS

REVISIONS

No.	Date	Description

DRAWINGS REVISED AS PER DESIGN BULLETIN

No.	Date	Description

NOT FOR CONSTRUCTION

THIS DRAWING IS OWNED BY OR LICENSED FOR USE BY POPEYES LOUISIANA KITCHEN (OR ITS AFFILIATED OR RELATED COMPANIES) AND MAY NOT BE REPRODUCED, USED, DOWNLOADED, DISSEMINATED, PUBLISHED, OR TRANSFERRED IN ANY FORM OR BY ANY MEANS, EXCEPT WITH THE PRIOR WRITTEN CONSENT OF POPEYES LOUISIANA KITCHEN. COPYRIGHT INFRINGEMENT IS A VIOLATION OF FEDERAL LAW SUBJECT TO CRIMINAL AND CIVIL PENALTIES.

THE CONTRACTOR IS TO VERIFY ALL DIMENSIONS AND CONDITIONS ON THE PROJECT AND TO REPORT ANY DISCREPANCIES TO THE POPEYES LOUISIANA KITCHEN REPRESENTATIVE PRIOR TO COMMENCING WORK. THESE DRAWINGS ARE NOT TO BE USED FOR CONSTRUCTION PURPOSES UNLESS INDICATED BY POPEYES LOUISIANA KITCHEN AS "ISSUED FOR CONSTRUCTION".

Professional Seal

DESIGNER NOTES:
DESIGN GUIDELINE ONLY - NOT FOR PERMIT OR CONSTRUCTION

THESE DOCUMENTS MUST BE COMPLETED AND / OR MODIFIED BY A LICENSED ARCHITECT AND ENGINEER TO CONFORM TO ALL APPLICABLE CODES, AND SPECIFIC SITE CONDITIONS. THERE IS NO WARRANTY, WHETHER IMPLIED OR EXPRESSED THAT THESE DOCUMENTS MEET THE APPLICABLE CODE REQUIREMENTS. THE LIABILITY FOR THE DESIGN AND ANY USE OF THE DOCUMENTS IS THE SOLE RESPONSIBILITY OF THE ARCHITECT AND ENGINEER OF RECORD.

Company Logo

Project

Store Type

US DTGO PROTOTYPE

Location

PROTOTYPE DTGO (U.S.)


CITY, STATE

Drawing Title

LIFE SAFETY FLOOR PLAN

Drawn	XX	Checked	XX
Scale	1/4"=1'-0"	Date	##.##.####
Project No.	XX	Drawing No.	LS1


POPEYES LOUISIANA KITCHEN MODEL DTGO, ADDRESS, CITY, STATE, DTGO PROTOTYPE DOCUMENTS (OCTOBER, 2025) STORE NO. XXXX

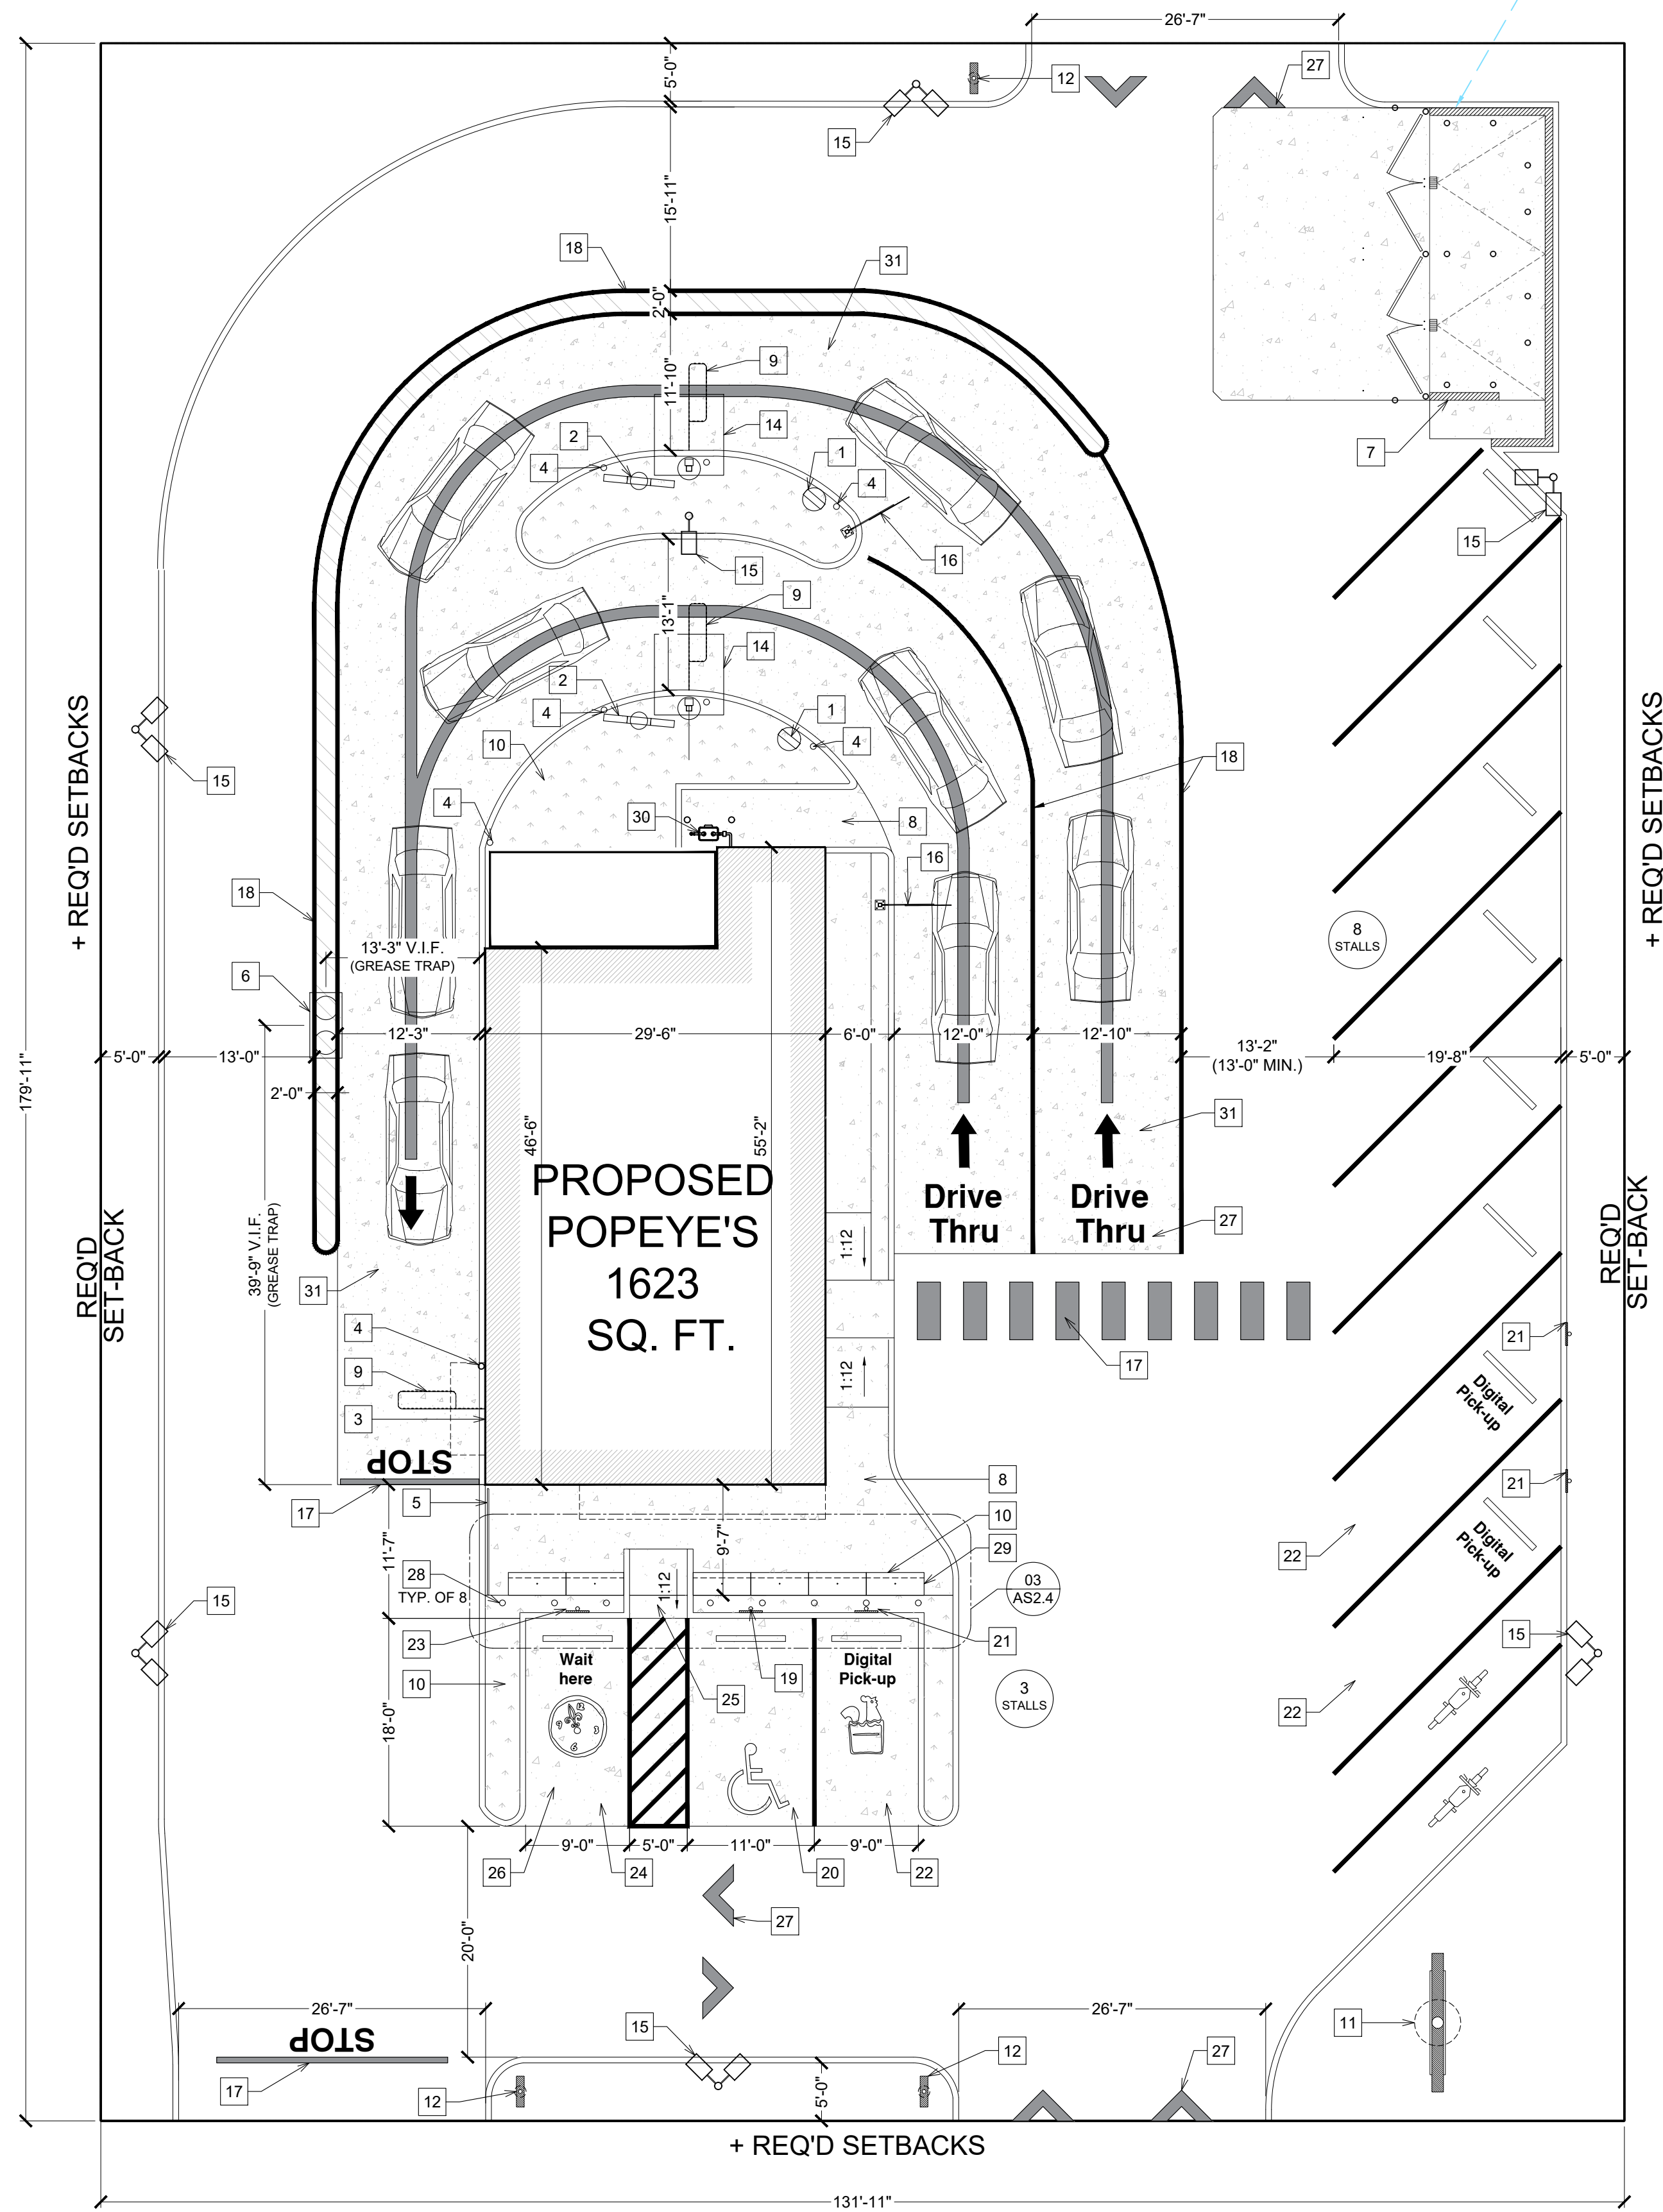

NOTE: SIGNAGE, LANDSCAPING, AND CIVIL DRAWINGS; ALL SUBMITTED UNDER SEPARATE COVERS.

MAIN ROAD

23,734 sqft = 0.544 acre

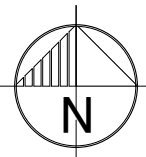

GENERAL NOTE

ARCHITECTURAL SITE PLAN IS TO BE USED FOR GUIDELINE REFERENCE ONLY. ALL SITE SPECIFIC INFORMATION AND REQUIREMENTS IS TO BE COORDINATED WITH ARCHITECT, MECHANICAL, ELECTRICAL, PLUMBING, STRUCTURAL AND CIVIL ENGINEER OF RECORD.

NOTES

- 1 DT DIGITAL PRE-SELL MENU BOARD LOCATION. REFER TO DETAILS ON SHEET 2/AS2.1.
- 2 DT DIGITAL MENU BOARD LOCATION. REFER TO DETAILS ON SHEET 3/AS2.1.
- 3 POPEYE'S RESTAURANT DRIVE THRU WINDOW LOCATION. SEE FLOOR PLAN ON SHEET A1 FOR ADDITIONAL INFORMATION.
- 4 6"Ø STEEL PIPE BOLLARD. REFER TO DETAIL 14/AS2.3.
- 5 PATIO RAILING - REFER TO DETAIL 2/A8.
- 6 APPROXIMATE LOCATION OF GREASE INTERCEPTOR BELOW SITE PAVING. COORDINATE EXACT LOCATOIN WITH PLUMBING & CIVIL DRAWINGS. REF: 3/AS2.3.
- 7 POPEYE'S DUMPSTER ENCLOSURE. COORDINATE EXACT LOCATION WITH CIVIL DRAWINGS. REFER TO ARCHITECTURAL SITE DETAILS AS2.2 FOR CONSTRUCTION.
- 8 SIDEWALK / SLAB. REFER TO CIVIL SITE PLAN DRAWINGS FOR LOCATION AND DIMENSIONS.
- 9 VEHICLE DETECTOR LOOP. REFER TO 5/AS2.1 FOR DETAIL.
- 10 ALL SITE PLAN ELEMENTS SHOWN MUST BE IN COMPLIANCE WITH POPEYES DESIGN TEAM APPROVED SITE PLAN. ARCHITECT OF RECORD, ENGINEERS OF RECORD, AND CIVIL ENGINEER OF RECORD ARE RESPONSIBLE FOR THIS COORDINATION AND COMPLIANCE.
- 11 MONUMENT SIGN / SIGN BASE. REFER TO SIGNAGE PACKAGE DRAWINGS.
- 12 DRIVE THRU DIRECTIONAL SIGNAGE BOARD. REFER TO DETAIL 9/AS2.1.
- 13 NOT USED.
- 14 DRIVE THRU CANOPY W/ INTEGRAL SPEAKER POST. REFER TO 1/AS2.1.
- 15 LIGHT POLE. REFER TO CIVIL SITE PLAN DRAWINGS FOR LOCATION AND DIMENSIONS. REFER TO 8/AS2.1
- 16 CLEARANCE BAR. REFER TO DETAIL ON SHEET 6/AS2.1
- 17 PEDESTRIAN WALKWAY MARKING AND STOP BAR MARKINGS. DESIGN BY CIVIL ENGINEER TO BE APPROVED BY POPEYE'S DESIGN. REFER TO 2/AS2.4
- 18 PAVEMENT STRIPPING. ADD BOLLARDS AS NECESSARY.
- 19 ACCESSIBLE PARKING SIGNAGE. SIGNAGE TO BE INSTALLED AS PER LOCAL JURISDICTION CODES.
- 20 ACCESSIBLE PARKING STALLS.
- 21 DIGITAL PARKING SIGNAGE.
- 22 DIGITAL PARKING STALLS.
- 23 PULL FORWARD PARKING SIGNAGE.
- 24 PULL FORWARD PARKING STALLS.
- 25 TACTILE WARNING PLATE/PAD AT CONCRETE SURFACE CURB RAMP. CURB RAMP SLOPE @ 1:12 MAX. REFER TO CIVIL + LOCAL JURISDICTION REQUIREMENTS.
- 26 DRIVE SURFACE AT THE ADA STALL + ADJACENT PARKING STALLS IN ROW TO BE CONCRETE. DESIGN BY CIVIL ENGINEER TO BE APPROVED BY POPEYE'S DESIGN.
- 27 PAVEMENT DIRECTIONAL MARKINGS, LETTERING, AND GRAPHICS. REFER TO 1/AS2.4
- 28 6"Ø STEEL PIPE BOLLARD AT FRONT OF BUILDING, PARKING STALLS FROM THE WALKWAY / BENCH SEATING, SPACED AT 4'-0" O.C. REFER TO DETAIL 15/AS2.3.
- 29 NEW CONCRETE SEAT WALL BENCH (LIGHTED) TO BE INSTALLED AT THE FRONT OF THE BUILDING. BENCHES TO BE GO PROVIDED (FROM POPEYES APPROVED VENDOR) AND GC INSTALLED. COORDINATE W/ ELECT SHEETS FOR CONDUIT AND FEEDER FOR LIGHTED BENCHES.
- 30 GAS METER. REFER TO MECHANICAL DRAWINGS. COORDINATE LOCATION WITH CIVIL DRAWINGS AND LOCAL UTILITY COMPANY. G.C TO COORDINATE WITH UTILITY COMPANIES FOR PLACEMENT / LOCATION OF BOLLARDS AT THE GAS METER. G.C TO PROVIDE 6" DIA. METAL BOLLARD FILL W/ CONCRETE AND PAINTED.
- 31 DRIVE SURFACE AT THE DRIVE-THRU LANES TO BE CONCRETE. DESIGN BY CIVIL ENGINEER TO BE APPROVED BY POPEYE'S DESIGN.

ISSUE TABLE

No.	Date (mm/dd/yy)	Description
01	09-26-25	DTGO PROTOTYPE DOCUMENTS

REVISIONS

No.	Date	Description

DRAWINGS REVISED AS PER DESIGN BULLETIN

No.	Date	Description

THIS DRAWING IS OWNED BY OR LICENSED FOR USE BY POPEYES LOUISIANA KITCHEN (OR ITS AFFILIATED OR RELATED COMPANIES) AND MAY NOT BE REPRODUCED, USED, DOWNLOADED, DISSEMINATED, PUBLISHED, OR TRANSFERRED IN ANY FORM OR BY ANY MEANS, EXCEPT WITH THE PRIOR WRITTEN CONSENT OF POPEYES LOUISIANA KITCHEN. COPYRIGHT INFRINGEMENT IS A VIOLATION OF FEDERAL LAW SUBJECT TO CRIMINAL AND CIVIL PENALTIES.

THE CONTRACTOR IS TO VERIFY ALL DIMENSIONS AND CONDITIONS ON THE PROJECT AND TO REPORT ANY DISCREPANCIES TO THE POPEYES LOUISIANA KITCHEN REPRESENTATIVE PRIOR TO COMMENCING WORK. THESE DRAWINGS ARE NOT TO BE USED FOR CONSTRUCTION PURPOSES UNLESS INDICATED BY POPEYES LOUISIANA KITCHEN AS "ISSUED FOR CONSTRUCTION".

Professional Seal

DESIGNER NOTES:
DESIGN GUIDELINE ONLY - NOT FOR PERMIT OR CONSTRUCTION

THESE DOCUMENTS MUST BE COMPLETED AND / OR MODIFIED BY A LICENSED ARCHITECT AND ENGINEER TO CONFORM TO ALL APPLICABLE CODES, AND SPECIFIC SITE CONDITIONS. THERE IS NO WARRANTY, WHETHER IMPLIED OR EXPRESSED THAT THESE DOCUMENTS MEET THE APPLICABLE CODE REQUIREMENTS. THE LIABILITY FOR THE DESIGN AND ANY USE OF THE DOCUMENTS IS THE SOLE RESPONSIBILITY OF THE ARCHITECT AND ENGINEER OF RECORD.

Company Logo



POPEYES.

Store Type

US DTGO PROTOTYPE

Location

PROTOTYPE
DTGO (U.S.)

CITY, STATE

Drawing Title

ARCHITECTURAL
SITE PLAN

Drawn

XX

Checked

XX

Scale

AS NOTED

Date

###.###

Project No.

XX

Drawing No.

AS1.1

MAIN ROAD

23,734 sqft = 0.544 acre

1	DT DIGITAL MENU BOARD LOCATION. REFER TO DETAILS ON SHEET 2/AS2.1.
2	DT DIGITAL MENU BOARD LOCATION. REFER TO DETAILS ON SHEET 3/AS2.1.
3	POPEYE'S RESTAURANT DRIVE THRU WINDOW LOCATION. SEE FLOOR PLAN ON SHEET A1 FOR ADDITIONAL INFORMATION.
4	6"Ø STEEL PIPE BOLLARD. REFER TO DETAIL 14/AS2.3.
5	PATIO RAILING - REFER TO DETAIL 2/A8.
6	APPROXIMATE LOCATION OF GREASE INTERCEPTOR BELOW SITE PAVING. COORDINATE EXACT LOCATION WITH PLUMBING & CIVIL DRAWINGS. REF: 3/AS2.3.
7	POPEYE'S DUMPSTER ENCLOSURE. COORDINATE EXACT LOCATION WITH CIVIL DRAWINGS. REFER TO ARCHITECTURAL SITE DETAILS AS2.2 FOR CONSTRUCTION.
8	SIDEWALK / SLAB. REFER TO CIVIL SITE PLAN DRAWINGS FOR LOCATION AND DIMENSIONS.
9	VEHICLE DETECTOR LOOP. REFER TO 5/AS2.1 FOR DETAIL.
10	ALL SITE PLAN ELEMENTS SHOWN MUST BE IN COMPLIANCE WITH POPEYE'S DESIGN TEAM APPROVED SITE PLAN. ARCHITECT OF RECORD, ENGINEERS OF RECORD, AND CIVIL ENGINEER OF RECORD ARE RESPONSIBLE FOR THIS COORDINATION AND COMPLIANCE.
11	MONUMENT SIGN / SIGN BASE. REFER TO SIGNAGE PACKAGE DRAWINGS.
12	DRIVE THRU DIRECTIONAL SIGNAGE BOARD. REFER TO DETAIL 9/AS2.1.
13	NOT USED.
14	DRIVE THRU CANOPY W/ INTEGRAL SPEAKER POST. REFER TO 1/AS2.1.
15	LIGHT POLE. REFER TO CIVIL SITE PLAN DRAWINGS FOR LOCATION AND DIMENSIONS. REFER TO 8/AS2.1
16	CLEARANCE BAR. REFER TO DETAIL ON SHEET 6/AS2.1
17	PEDESTRIAN WALKWAY MARKING AND STOP BAR MARKINGS. DESIGN BY CIVIL ENGINEER TO BE APPROVED BY POPEYE'S DESIGN. REFER TO 2/AS2.4
18	PAVEMENT STRIPPING. ADD BOLLARDS AS NECESSARY.
19	ACCESSIBLE PARKING SIGNAGE. SIGNAGE TO BE INSTALLED AS PER LOCAL JURISDICTION CODES.
20	ACCESSIBLE PARKING STALLS.
21	DIGITAL PARKING SIGNAGE.
22	DIGITAL PARKING STALLS.
23	PULL FORWARD PARKING SIGNAGE.
24	PULL FORWARD PARKING STALLS.
25	TACTILE WARNING PLATE/PAD AT CONCRETE SURFACE CURB RAMP. CURB RAMP SLOPE @ 1:12 MAX. REFER TO CIVIL + LOCAL JURISDICTION REQUIREMENTS.
26	DRIVE SURFACE AT THE ADA STALL + ADJACENT PARKING STALLS IN ROW TO BE CONCRETE. DESIGN BY CIVIL ENGINEER TO BE APPROVED BY POPEYE'S DESIGN.
27	PAVEMENT DIRECTIONAL MARKINGS, LETTERING, AND GRAPHICS. REFER TO 1/AS2.4
28	6"Ø STEEL PIPE BOLLARD AT FRONT OF BUILDING. PARKING STALLS FROM THE WALKWAY / BENCH SEATING, SPACED AT 4'-0" O.C.. REFER TO DETAIL 15/AS2.3.
29	NEW CONCRETE SEAT WALL BENCH (LIGHTED) TO BE INSTALLED AT THE FRONT OF THE BUILDING. BENCHES TO BE GC PROVIDED (FROM POPEYE'S APPROVED VENDOR) AND GC INSTALLED. COORDINATE W/ ELECT SHEETS FOR CONDUIT AND FEEDER FOR LIGHTED BENCHES.
30	GAS METER. REFER TO MECHANICAL DRAWINGS. COORDINATE LOCATION WITH CIVIL DRAWINGS AND LOCAL UTILITY COMPANY. G.C TO COORDINATE WITH UTILITY COMPANIES FOR PLACEMENT / LOCATION OF BOLLARDS AT THE GAS METER. G.C TO PROVIDE 6" DIA. METAL BOLLARD FILL W/ CONCRETE AND PAINTED.
31	DRIVE SURFACE AT THE DRIVE-THRU LANES TO BE CONCRETE. DESIGN BY CIVIL ENGINEER TO BE APPROVED BY POPEYE'S DESIGN.

Professional Seal

DESIGNER NOTES:
DESIGN GUIDELINE ONLY - NOT FOR PERMIT OR CONSTRUCTION

THESE DOCUMENTS MUST BE COMPLETED AND / OR MODIFIED BY A LICENSED ARCHITECT AND ENGINEER TO CONFORM TO ALL APPLICABLE CODES, AND SPECIFIC SITE CONDITIONS. THERE IS NO WARRANTY, WHETHER IMPLIED OR EXPRESSED THAT THESE DOCUMENTS MEET THE APPLICABLE CODE REQUIREMENTS. LIABILITY FOR THE DESIGN AND ANY USE OF THE DOCUMENTS IS THE SOLE RESPONSIBILITY OF THE ARCHITECT AND ENGINEER OF RECORD.




Company Logo	
Project	
	
Store Type	US DTGO PROTOTYPE
Location	PROTOTYPE DTGO (U.S.) CITY, STATE
Drawing Title	
ARCHITECTURAL SITE PLAN	
Drawn	Checked
XX	XX
Scale	Date
AS NOTED	##.##.####
Drawing No.	Drawing No.
XX	AS1.1



NOTE
1. THE DISTANCE FROM THE PICK UP WINDOW TO THE CENTER OF THE ORDER STATION MAY NEED TO BE INCREASED TO ACCOMMODATE 6/7TH CAR ORDER, IF SPACING PERMITS. 2. THE DRIVE-AISLE WIDTHS MAY NEED TO BE INCREASED TO ACCOMMODATE TURNING MOVEMENTS. 3. DISTANCE BETWEEN THE CANOPY POST AND THE PRESALE MENU BOARD MAY NEED TO BE ADJUSTED DUE TO SITE SPECIFIC CONDITIONS.




7 NOT USED
AS2.1

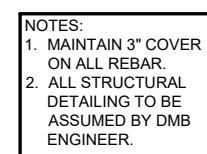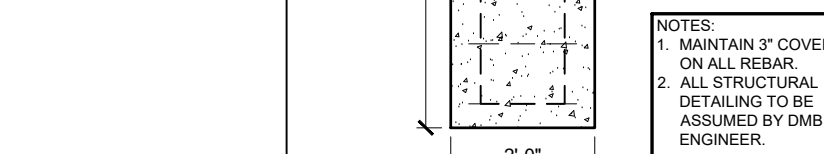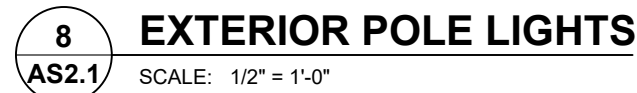


SIGNAGE VENDOR TO CONFIRM MINIMAL FOUNDATION REQUIREMENTS PROVIDED ON THIS SHEET, PER THE ACTUAL SIGNAGE EQUIPMENT DESIGN. STRICTER DESIGN BETWEEN THIS SHEET AND THE SIGNAGE VENDOR SHOP DRAWINGS TO BE UTILIZED.


Drawn XX	Checked XX
Scale AS NOTED	Date ##.##.##
Project No. XX	Drawing No. AS2

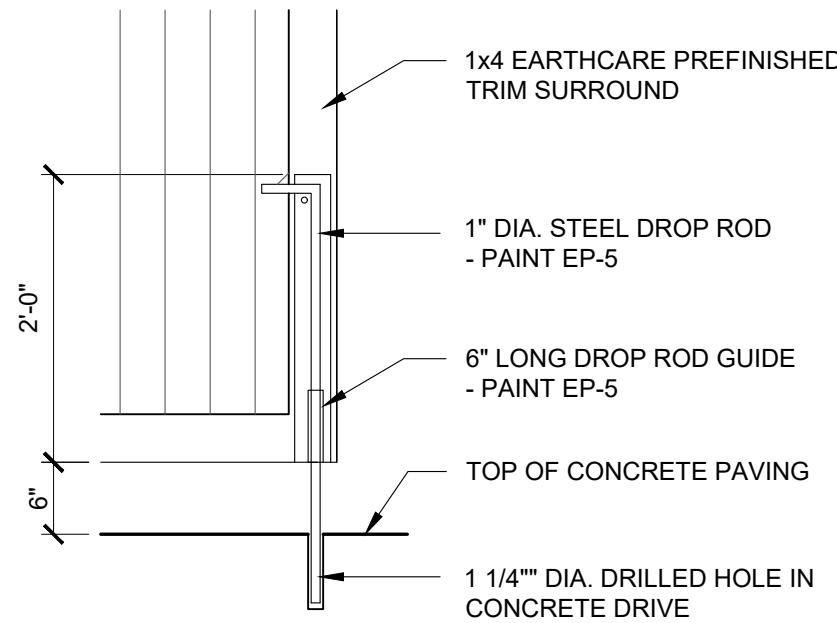


4 DROP ROD DETAIL
SCALE: 3/4" = 1'-0"

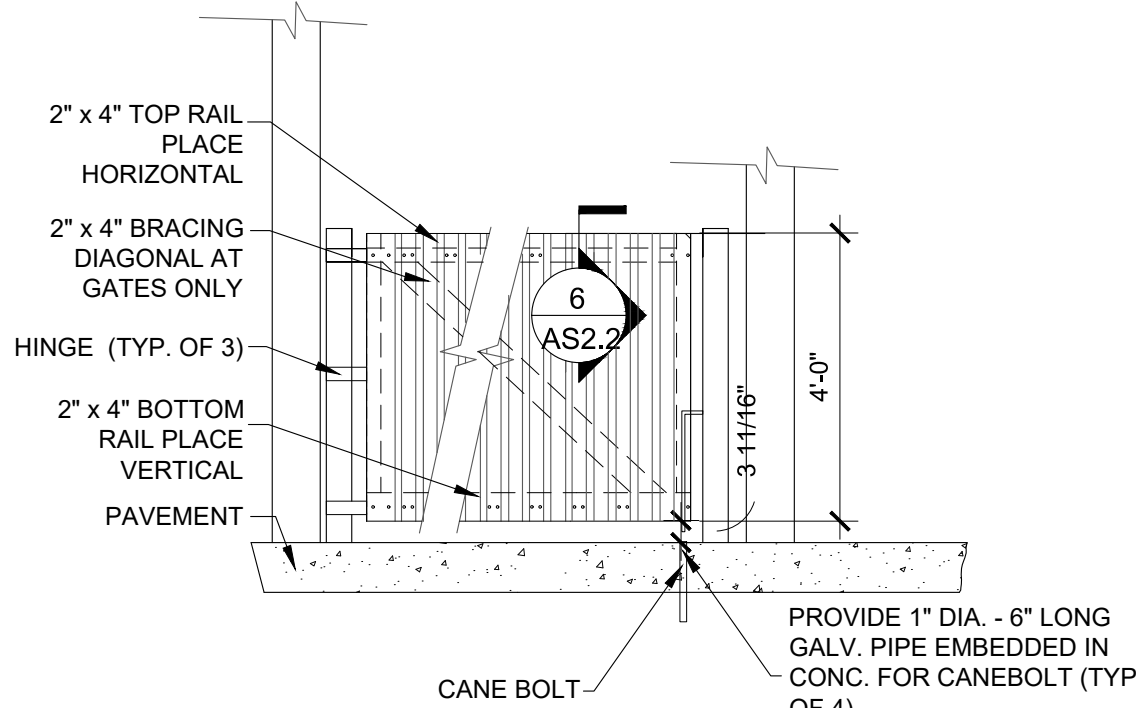


5 GATE DETAIL AT REAR ENCLOSURE
SCALE: 3/8" = 1'-0"

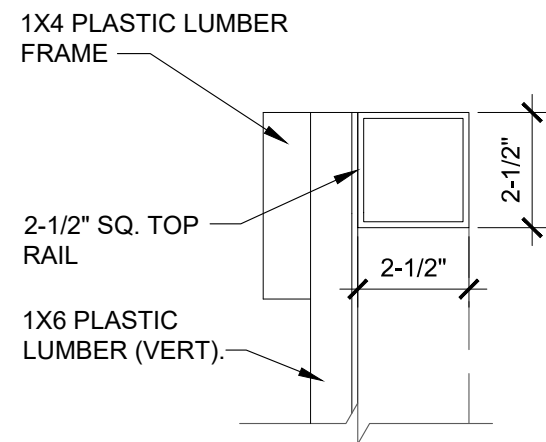


6 FLASHING DETAIL
SCALE: 3/8" = 1'-0"

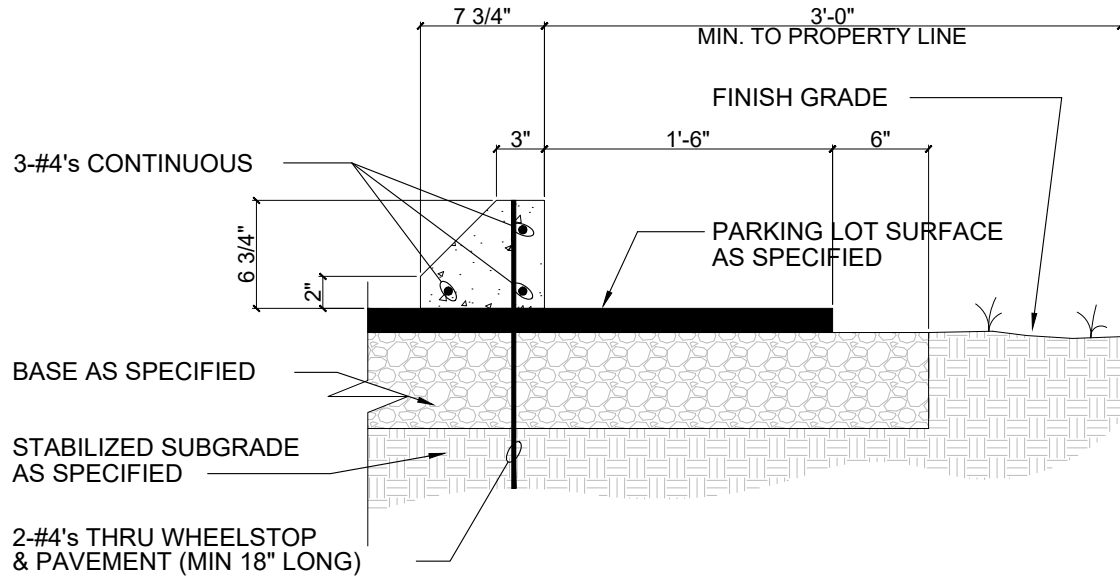


7 WHEELSTOP (PRECAST)
SCALE: 1" = 1'-0"

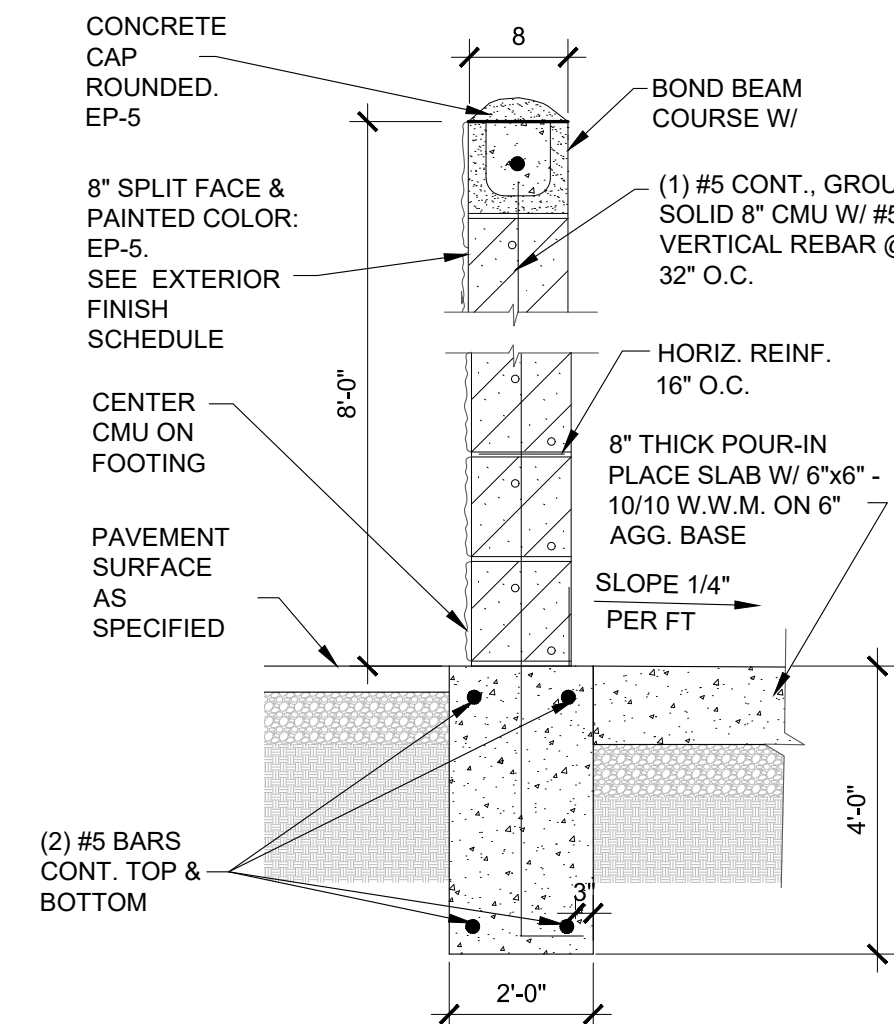


8 DUMPSTER WALL SECTION
SCALE: 3/8" = 1'-0"

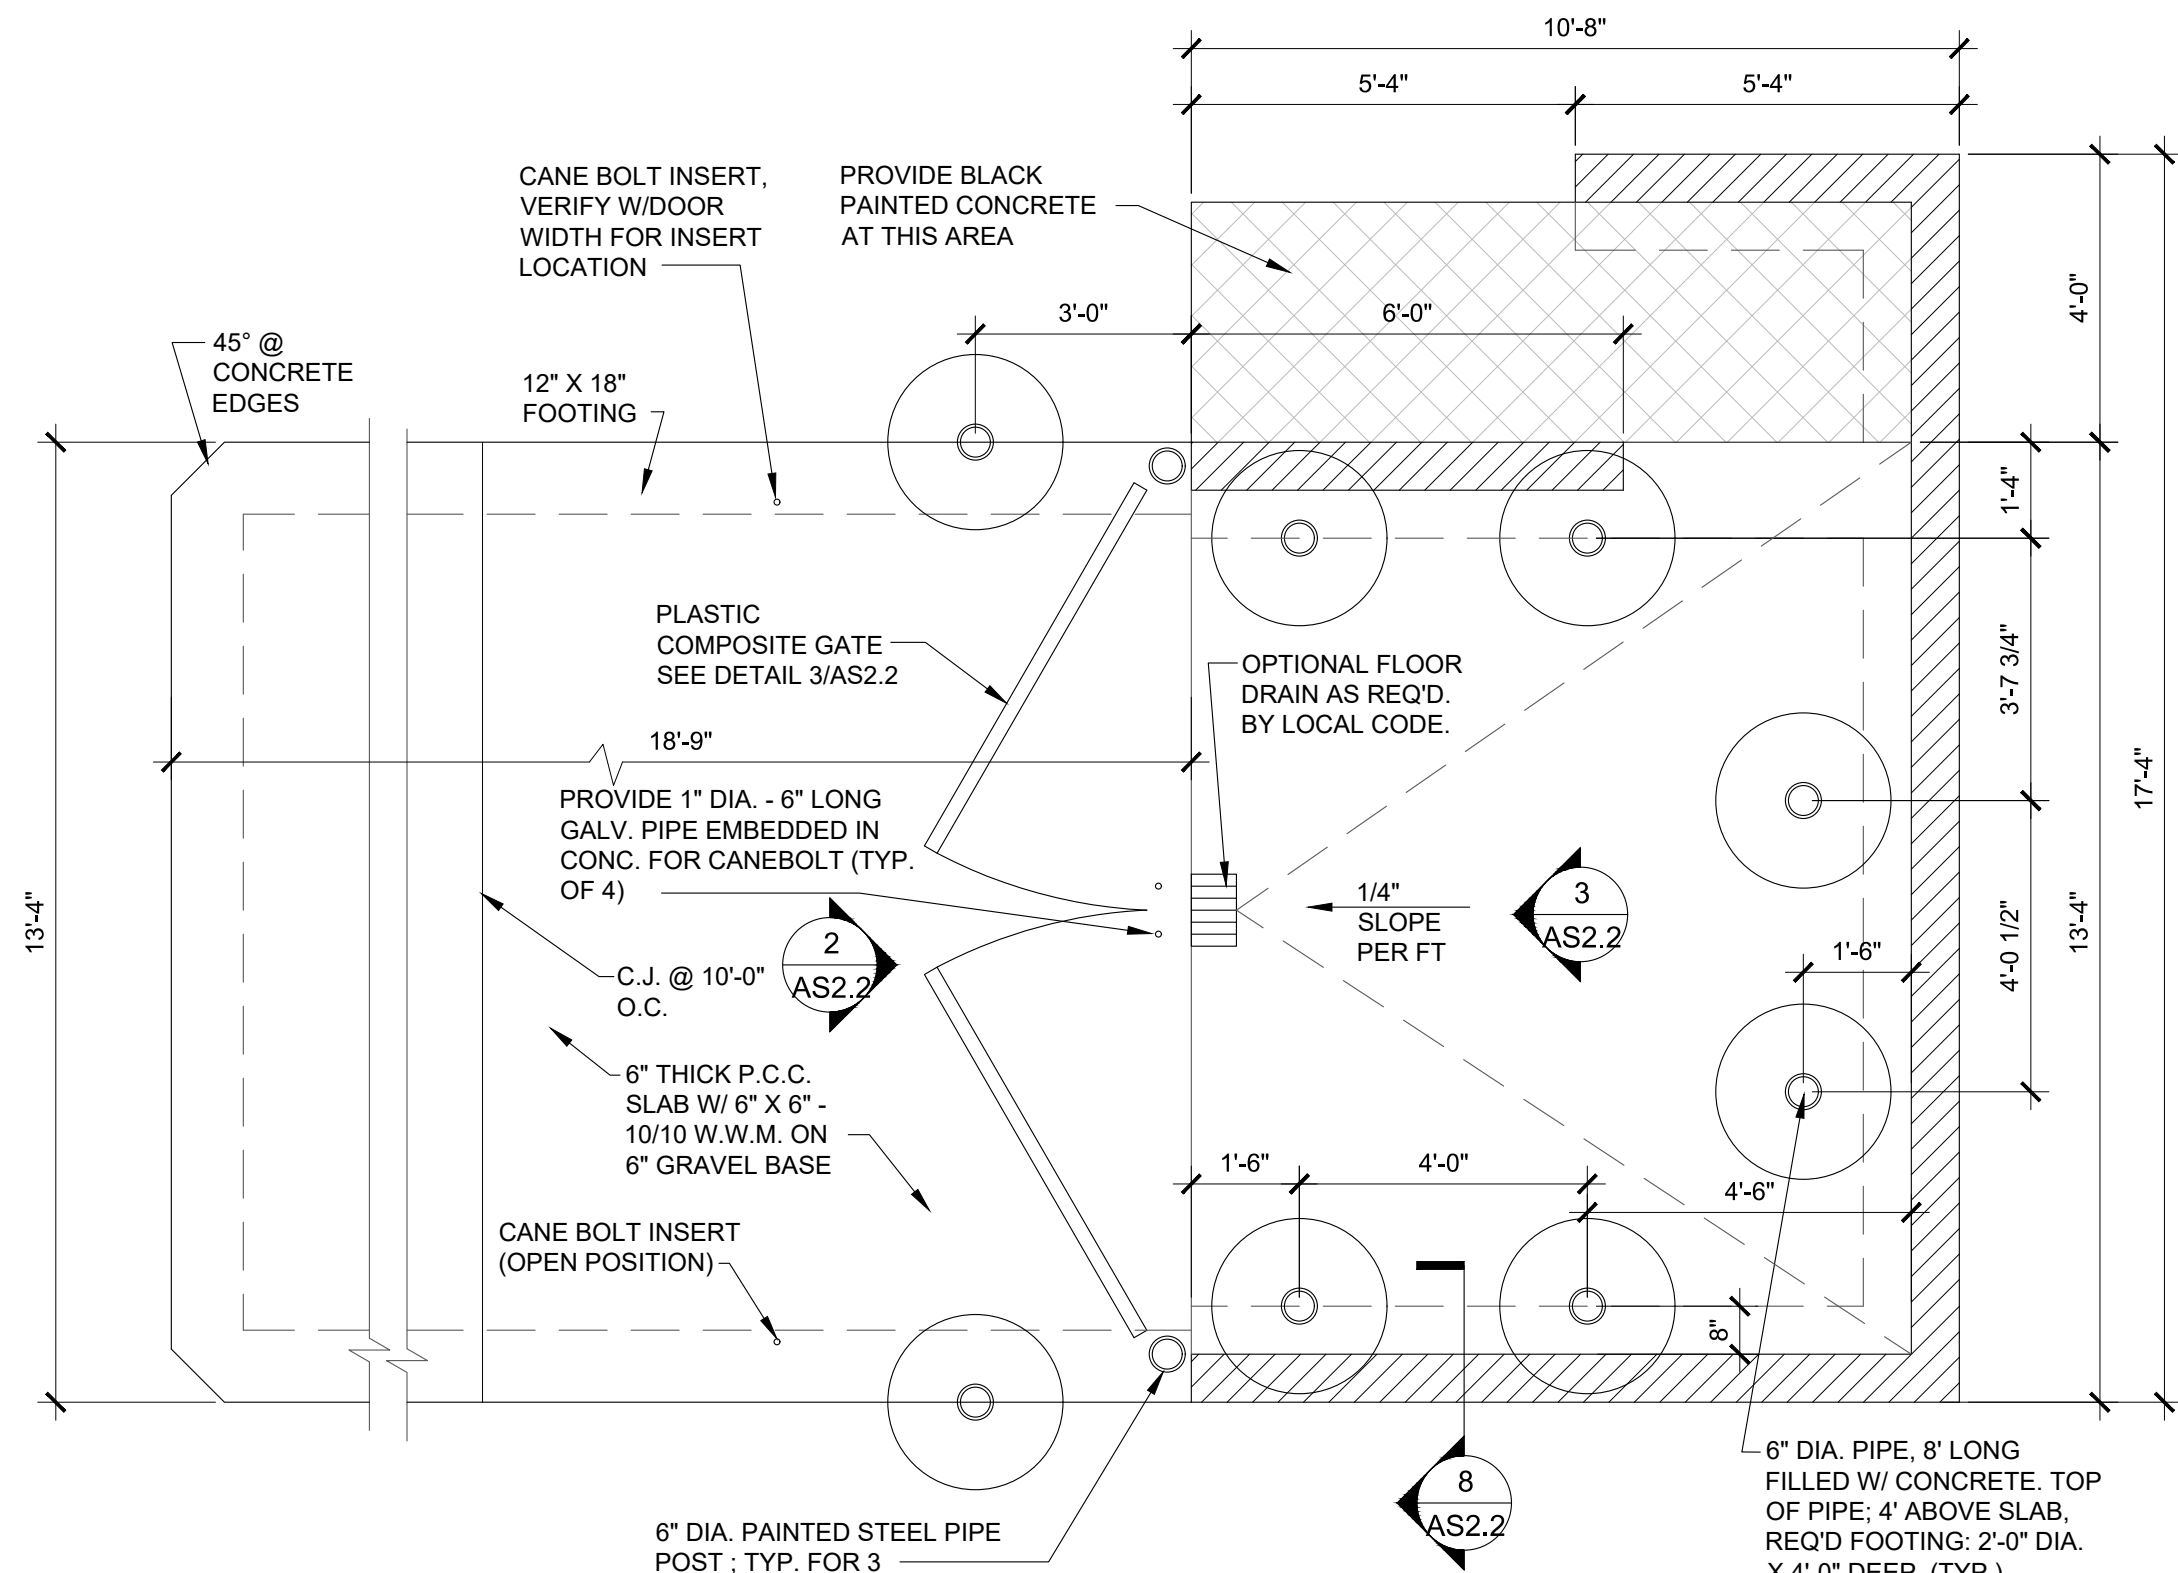

1 STANDARD DUMPSTER ENCLOSURE (SINGLE)
SCALE: 3/8" = 1'-0"

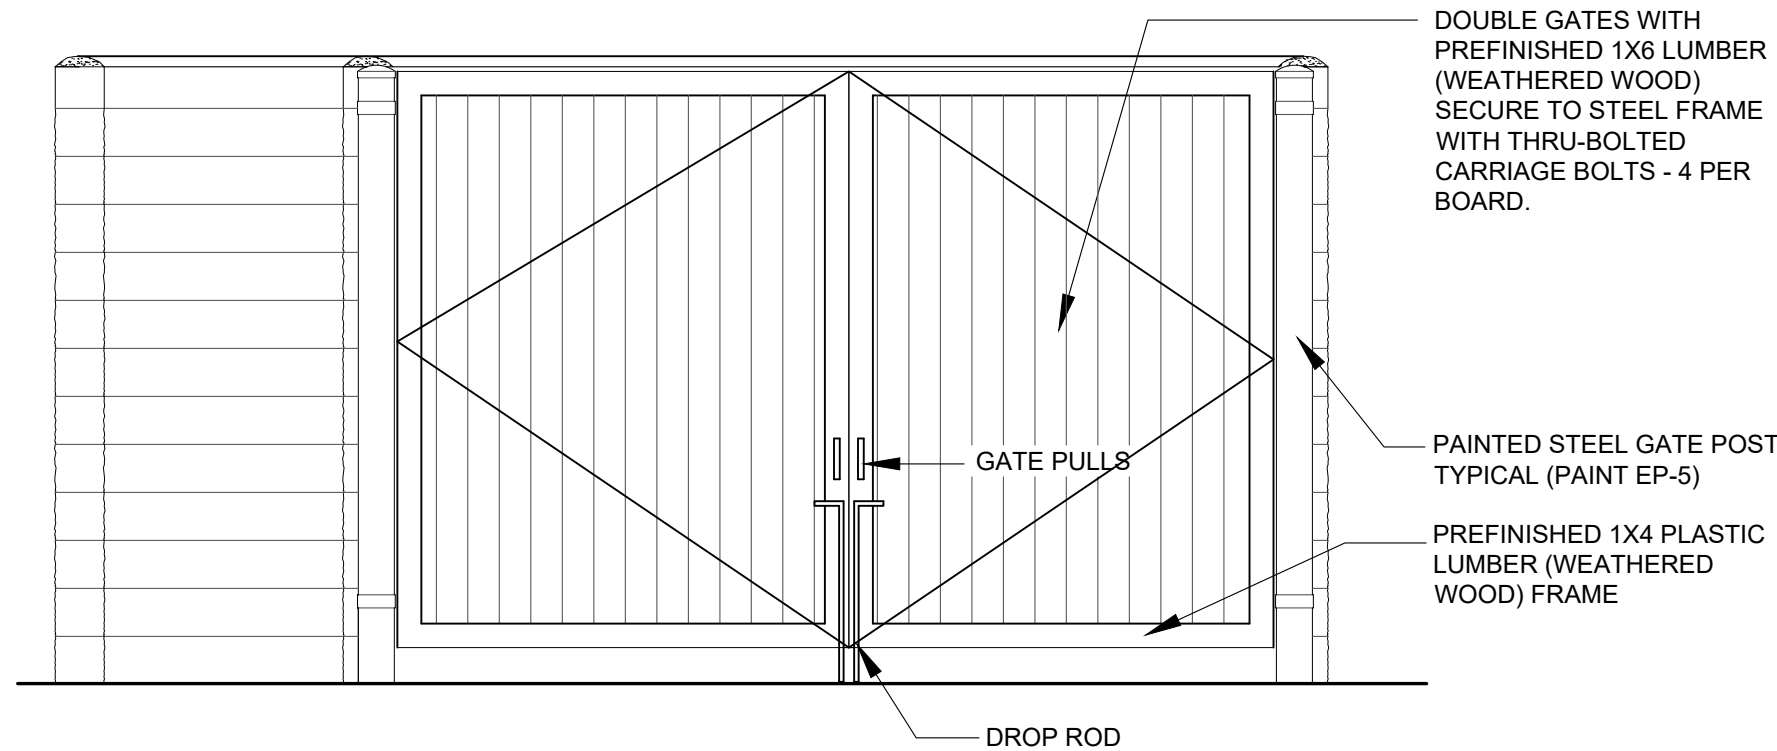


2 DUMPSTER ENCLOSURE & GATE EXT. ELEV.
SCALE: 3/8" = 1'-0"

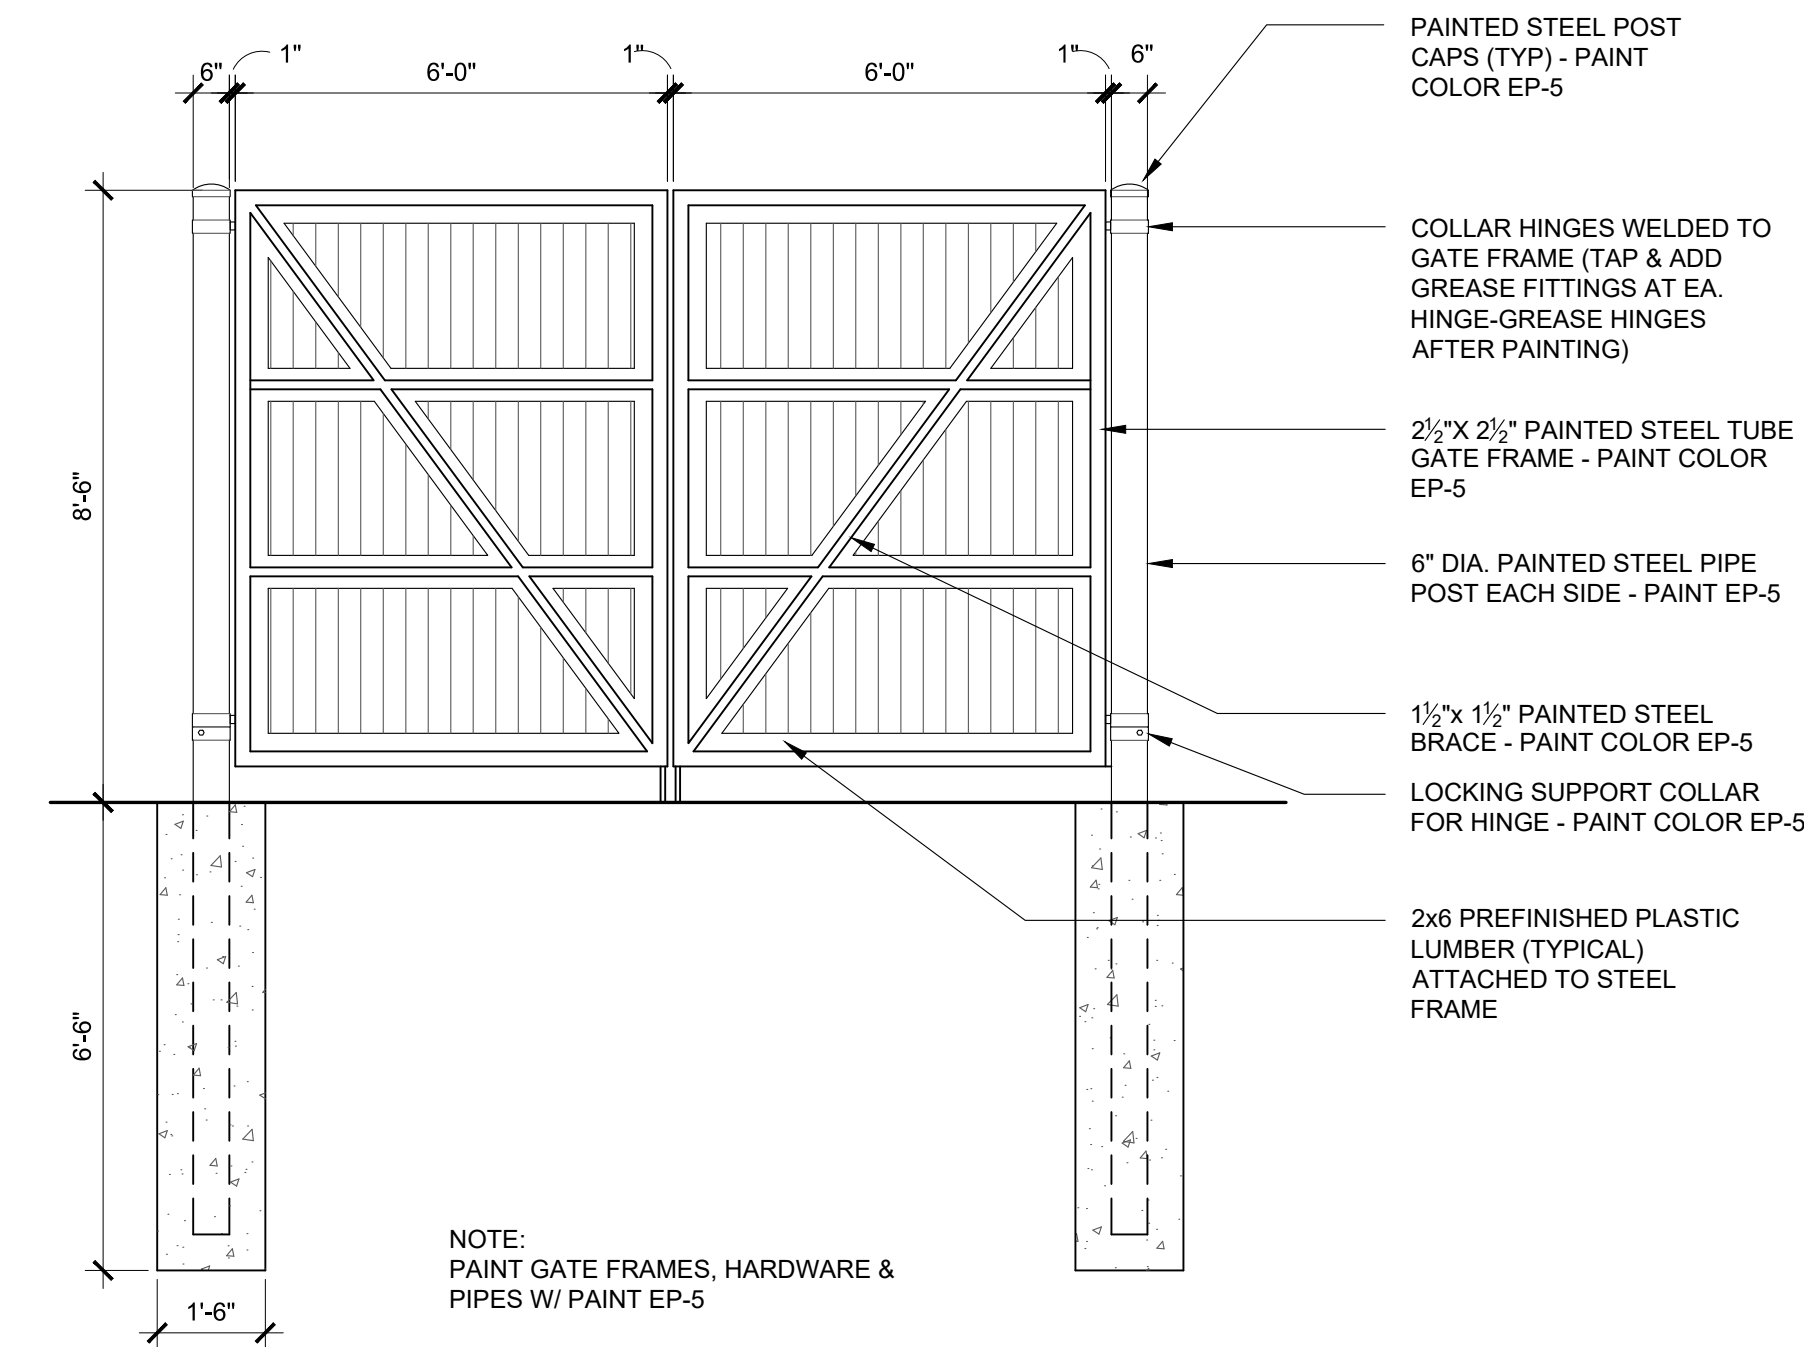


3 DUMPSTER ENCLOSURE & GATE INT. ELEV.
SCALE: 3/8" = 1'-0"


ISSUE TABLE		
No.	Date (mm/dd/yy)	Description
01	09-26-25	DTGO PROTOTYPE DOCUMENTS
REVISIONS		
No.	Date	Description
DRAWINGS REVISED AS PER DESIGN BULLETIN		
No.	Date	Description
THIS DRAWING IS OWNED BY OR LICENSED FOR USE BY POPEYES LOUISIANA KITCHEN (OR ITS AFFILIATED OR RELATED COMPANIES) AND MAY NOT BE REPRODUCED, USED, DOWNLOADED, DISSEMINATED, PUBLISHED, OR TRANSFERRED IN ANY FORM OR BY ANY MEANS, EXCEPT WITH THE PRIOR WRITTEN CONSENT OF POPEYES LOUISIANA KITCHEN. COPYRIGHT INFRINGEMENT IS A VIOLATION OF FEDERAL LAW SUBJECT TO CRIMINAL AND CIVIL PENALTIES.		
THE CONTRACTOR IS TO VERIFY ALL DIMENSIONS AND CONDITIONS ON THE PROJECT AND TO REPORT ANY DISCREPANCIES TO THE POPEYES LOUISIANA KITCHEN REPRESENTATIVE PRIOR TO COMMENCING WORK. THESE DRAWINGS ARE NOT TO BE USED FOR CONSTRUCTION PURPOSES UNLESS INDICATED BY POPEYES LOUISIANA KITCHEN AS "ISSUED FOR CONSTRUCTION".		
Professional Seal		
DESIGNER NOTES: DESIGN GUIDELINE ONLY - NOT FOR PERMIT OR CONSTRUCTION		
THESE DOCUMENTS MUST BE COMPLETED AND / OR MODIFIED BY A LICENSED ARCHITECT AND ENGINEER TO CONFORM TO ALL APPLICABLE CODES, AND SPECIFIC SITE CONDITIONS. THERE IS NO WARRANTY, WHETHER IMPLIED OR EXPRESSED THAT THESE DOCUMENTS MEET THE APPLICABLE CODE REQUIREMENTS. LIABILITY FOR THE DESIGN AND ANY USE OF THE DOCUMENTS IS THE SOLE RESPONSIBILITY OF THE ARCHITECT AND ENGINEER OF RECORD.		
Company Logo		
Project		
Store Type		
Location		
Drawing Title		
Drawn		
Scale		
Project No.		
Checked		
Date		
Drawing No.		

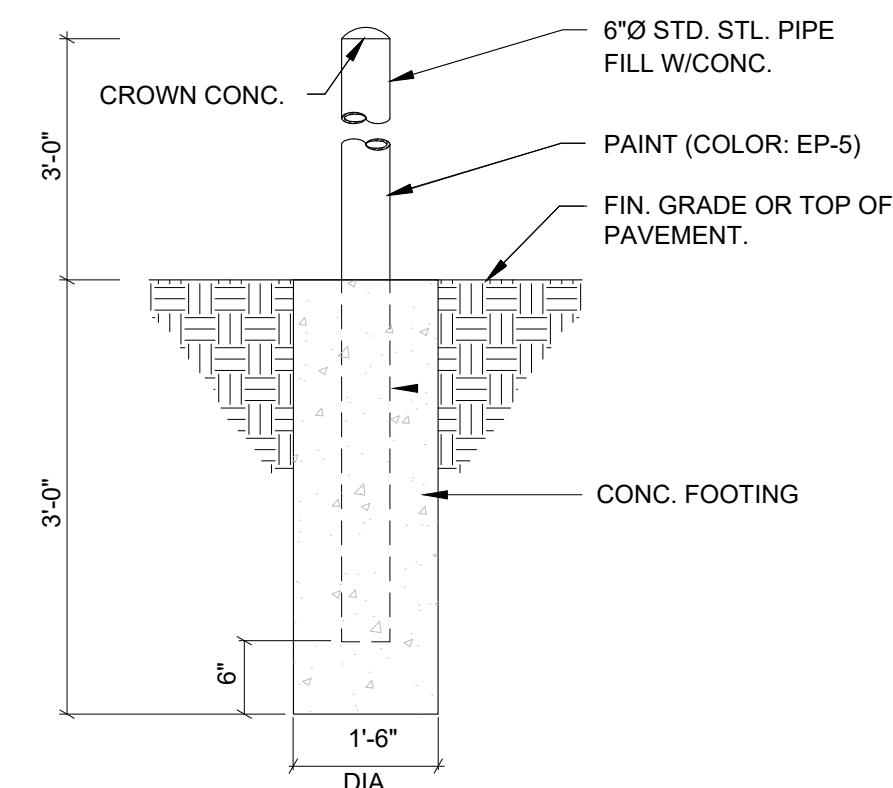


15 BOLLARD DETAIL
AS2.3 SCALE: 3/8" = 1'-0"

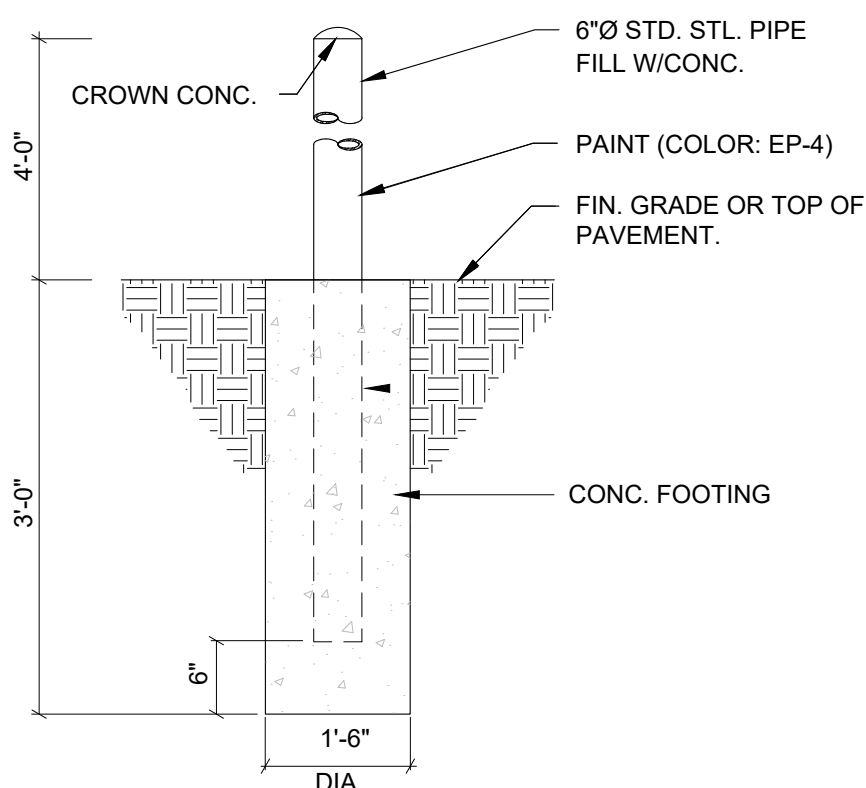


14 BOLLARD DETAIL
AS2.3 SCALE: 3/8" = 1'-0"

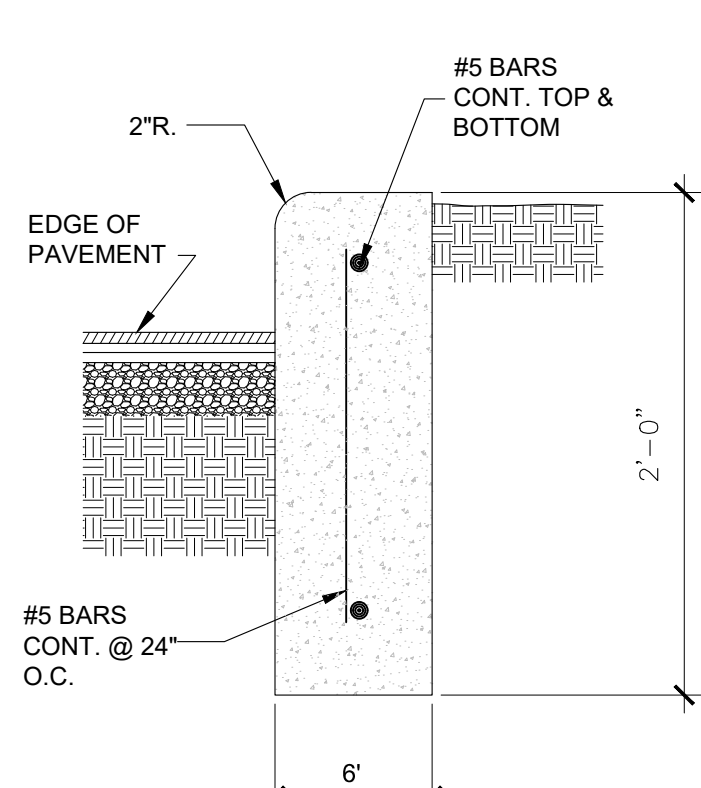


11 CURB DETAIL
AS2.3 SCALE: 3/8" = 1'-0"

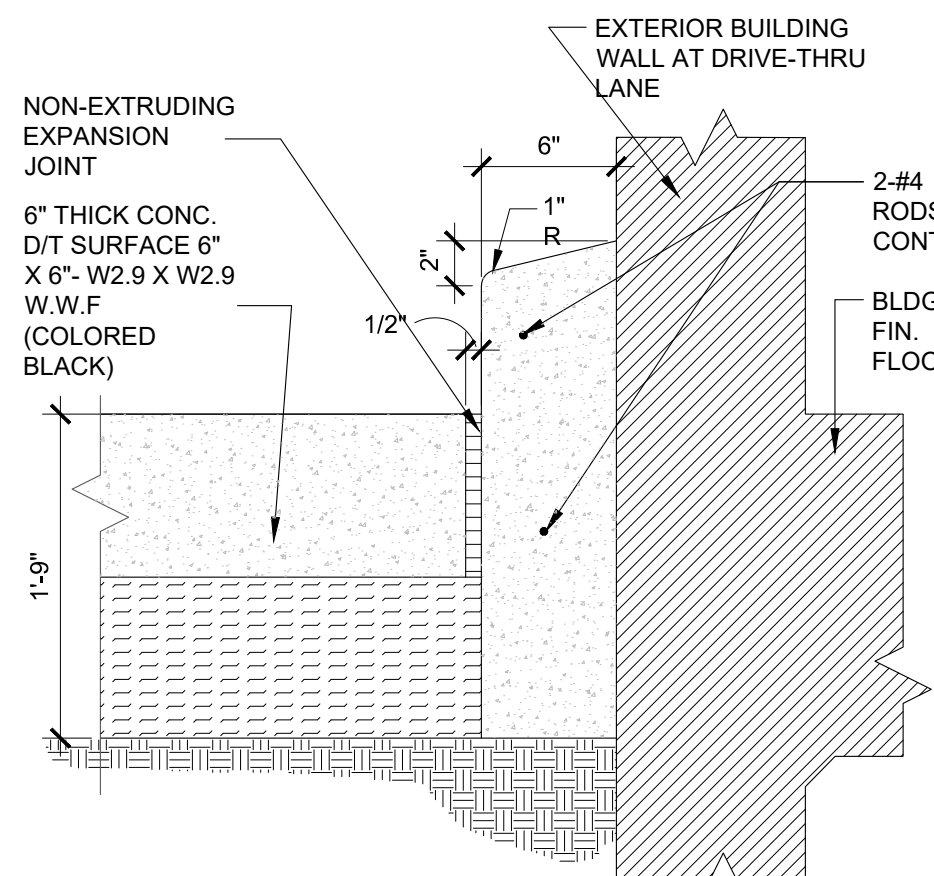




5 6" BARRIER CURB @ DRIVE-THRU WINDOW
AS2.3 SCALE: 3/8" = 1'-0"

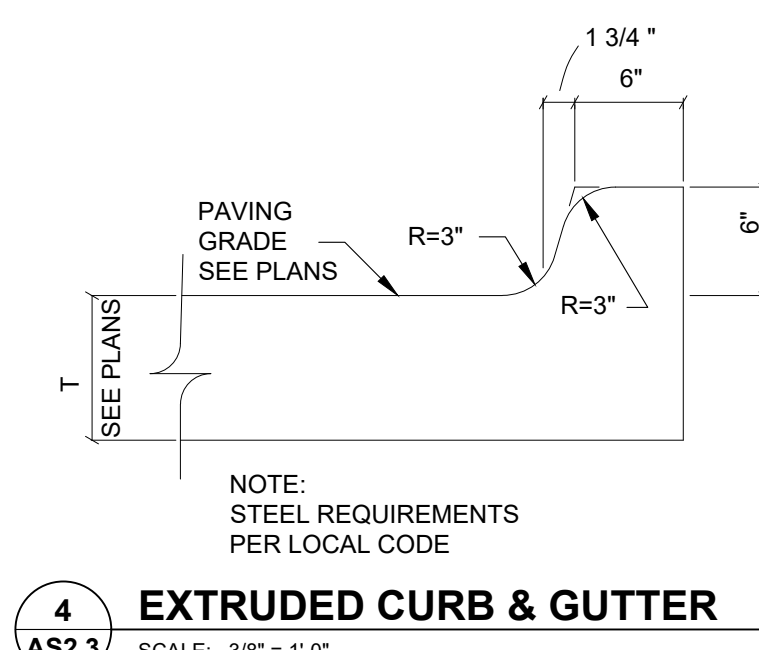


4 EXTRUDED CURB & GUTTER
AS2.3 SCALE: 3/8" = 1'-0"

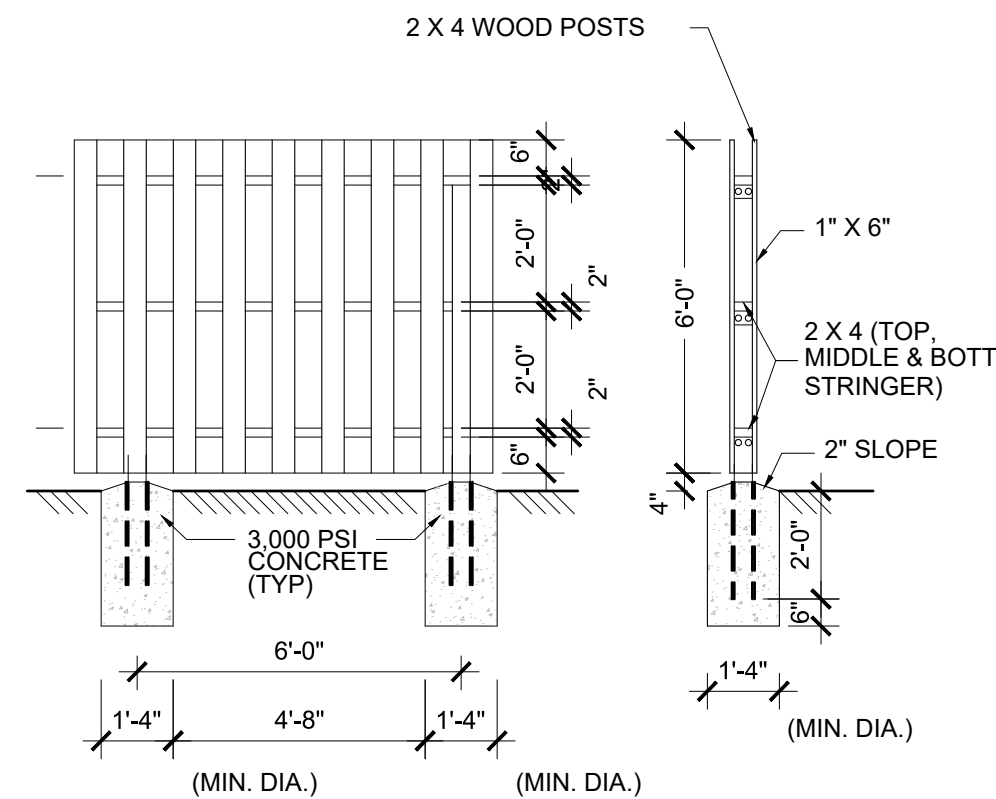


1 SHADOW BOX WOOD FENCE
AS2.3 SCALE: 3/8" = 1'-0"

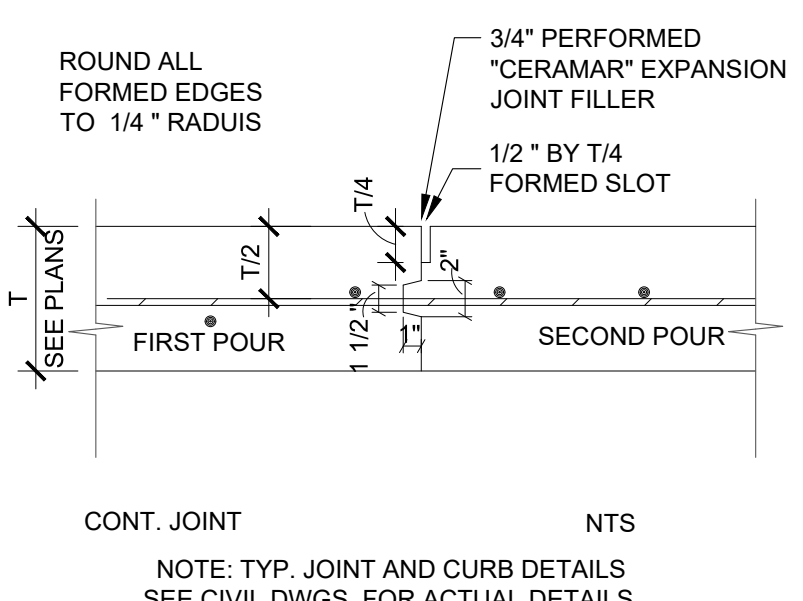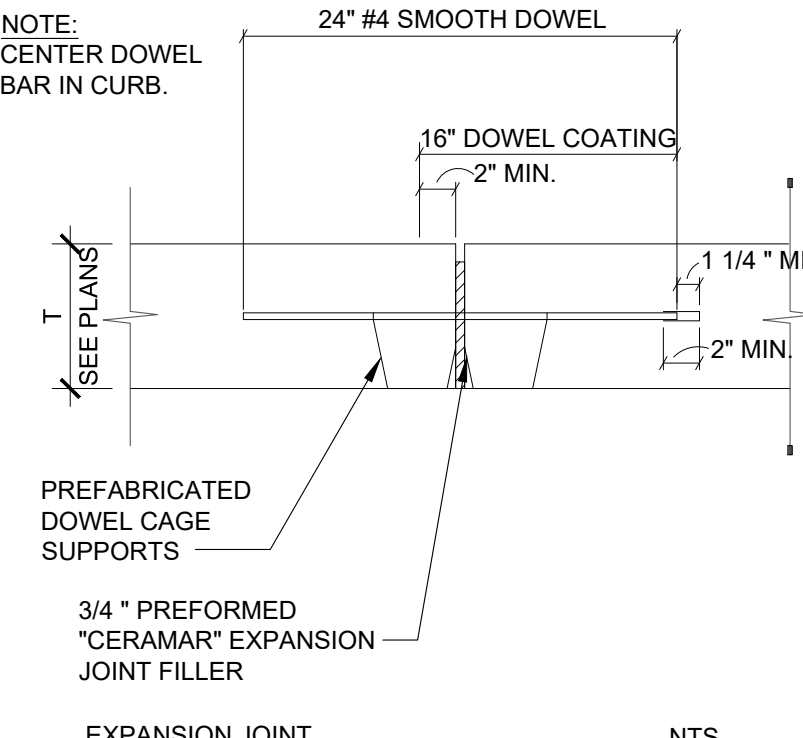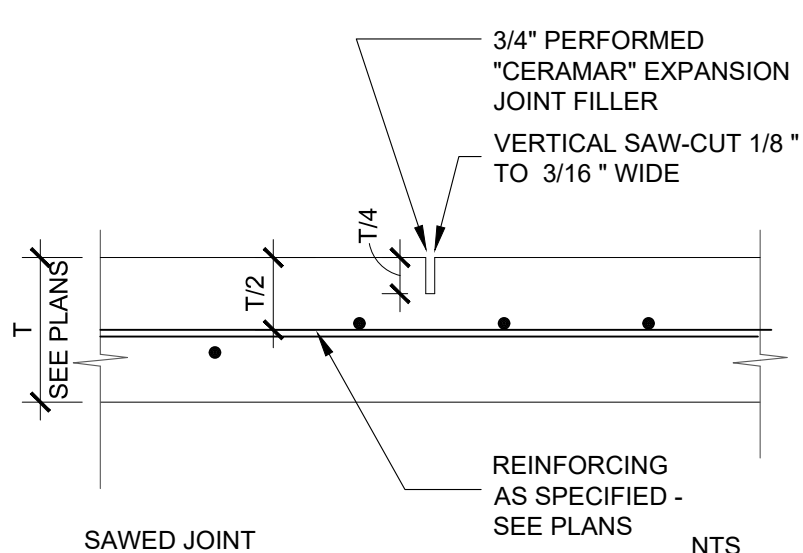

13 TYPICAL JOINT DETAILS
AS2.3 SCALE: 3/8" = 1'-0"

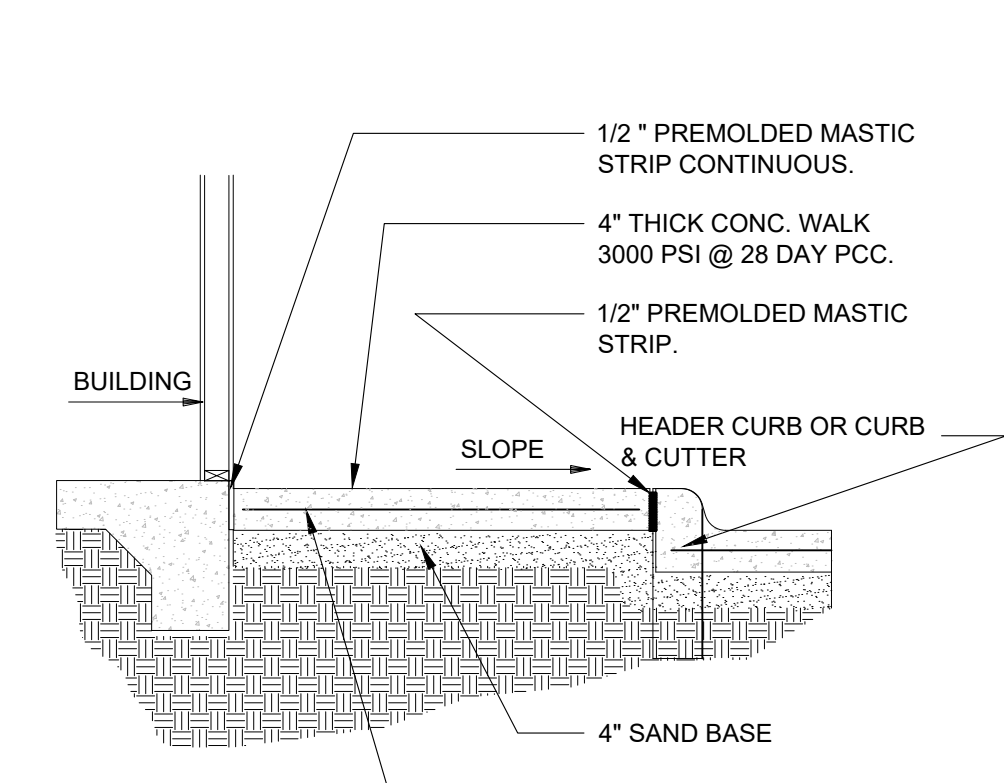

9 SIDEWALK DETAIL
AS2.3 SCALE: 3/8" = 1'-0"

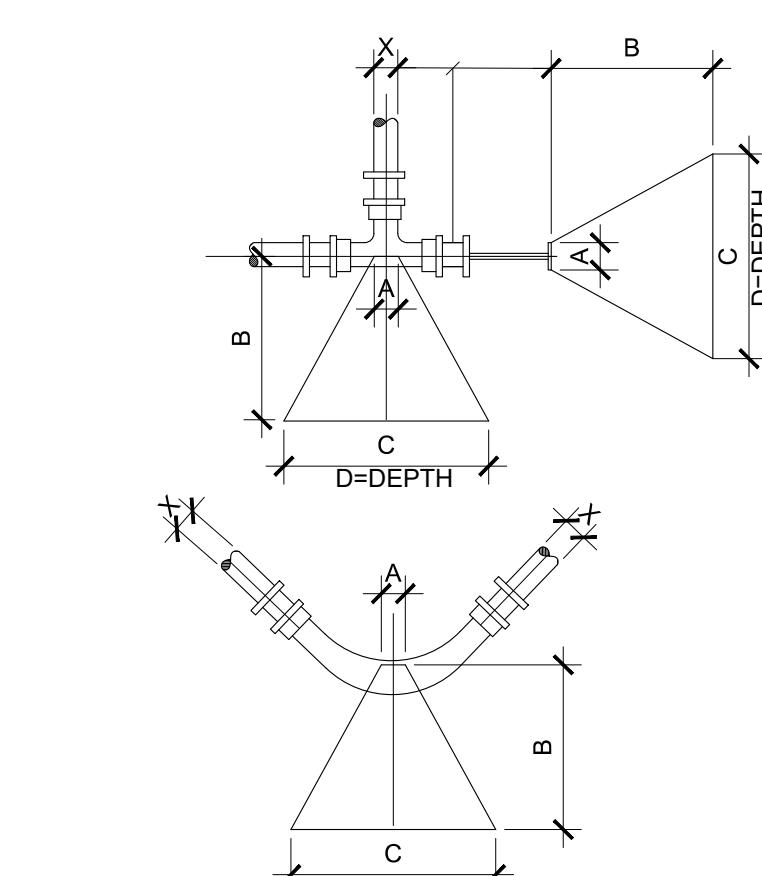


10 THRUST BLOCKS
AS2.3 SCALE: 3/8" = 1'-0"

BLOCKING DIMENSIONS					
DEAD END AND TEES	X	A	B	C	D
8"	10"	2'-3"	3'-3"	2'-0"	
12"	12"	3'-0"	4'-6"	3'-0"	
90°	8"	10"	2'-9"	4'-0"	2'-3"
	12"	12"	4'-3"	6'-0"	3'-3"
45°	8"	10"	1'-6"	2'-6"	2'-0"
	12"	12"	1'-9"	3'-0"	1'-9"
BENDS	11/16"	8"	10"	0'-6"	1'-4"
	12"	12"	0'-6"	1'-9"	1'-6"

X= DIAMETER OF PIPE TO BE BLOCKED NOTE: BLOCKING SHALL BE CONSTRUCTED AS PER AWWA STD. 0600, SECTION 12.3, OR LATEST REVISION


- KEY TO TYPICAL PAVEMENT SECTIONS
- 1 2" ASPHALTIC CONCRETE.
 - 2 BITUMINOUS PRIME COAT AND TOPPING.
 - 3 6" BASE COURSE, REFER TO GEOTECHNICAL REPORT.
 - 4 CONCRETE SIDEWALK.

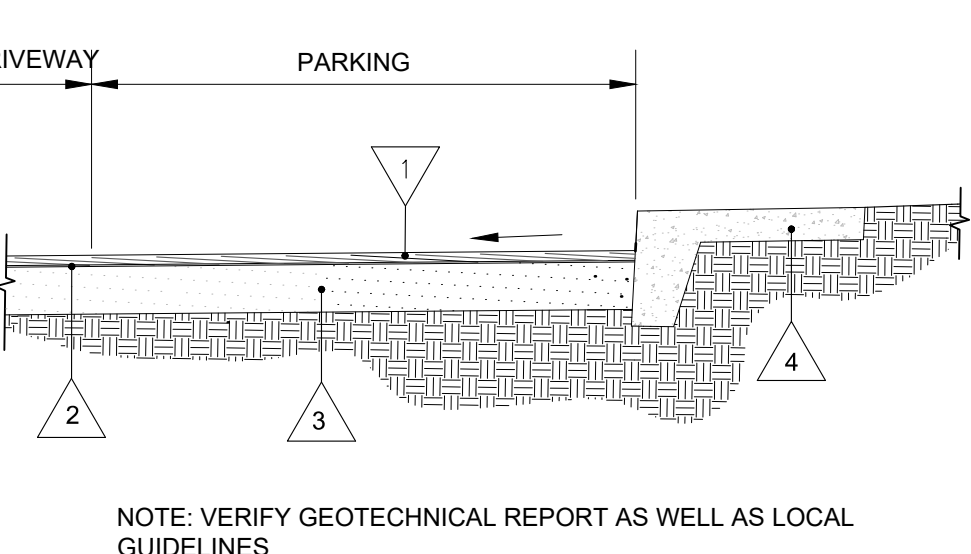


8 TYP. ASPHALT PAVEMENT DETAIL
AS2.3 SCALE: 3/8" = 1'-0"

GREASE TRAP SIZE TABLE		
G.T. SIZE	DIM "A"	DIM "B"
1000 GALLON	8'-2"	5'-1"
1200 GALLON	8'-6"	5'-9"


VERIFY PER LOCAL CODE

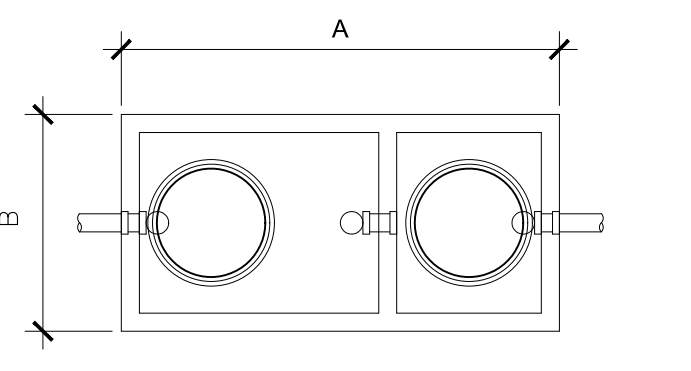


3 EXTERIOR GREASE TRAP
AS2.3 SCALE: 3/8" = 1'-0"

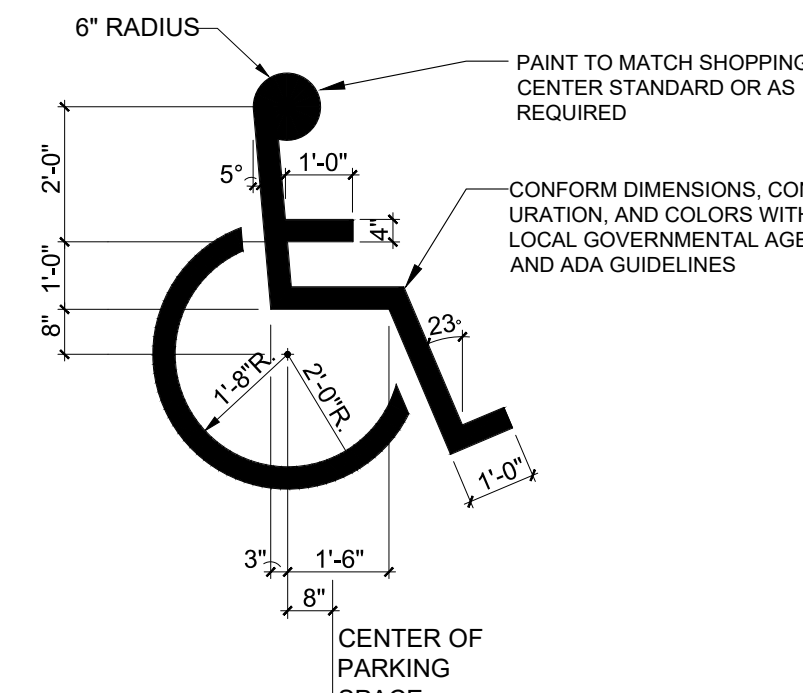


12 HANDICAP SYMBOL
AS2.3 SCALE: 3/8" = 1'-0"

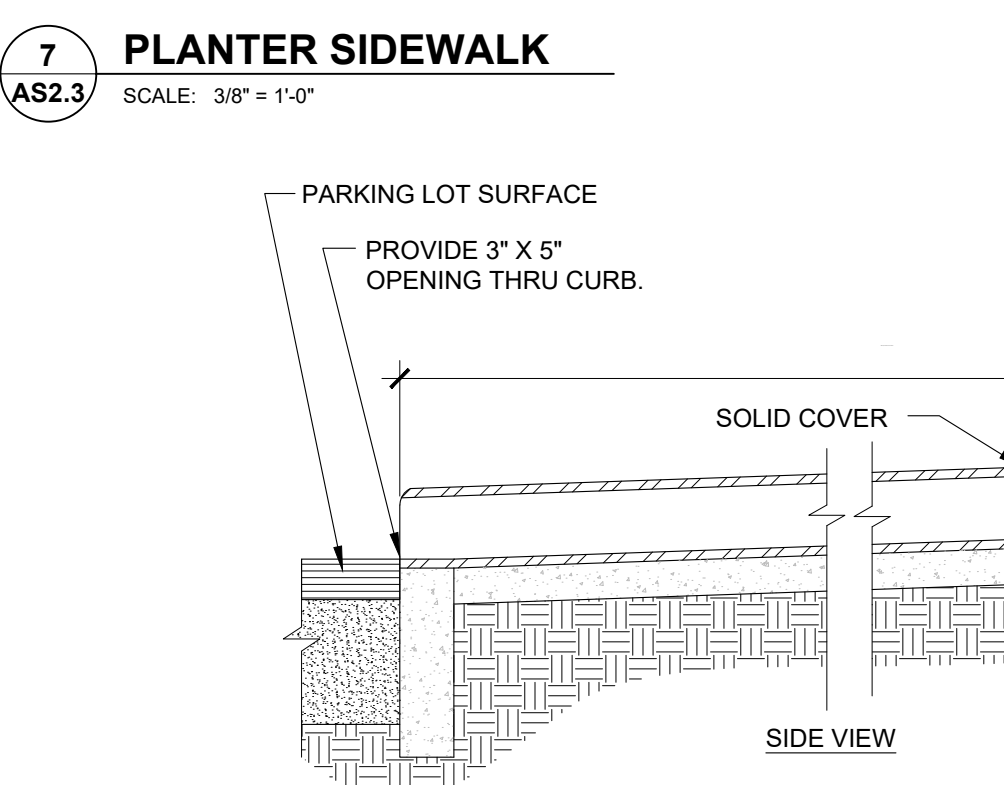

7 PLANTER SIDEWALK
AS2.3 SCALE: 3/8" = 1'-0"

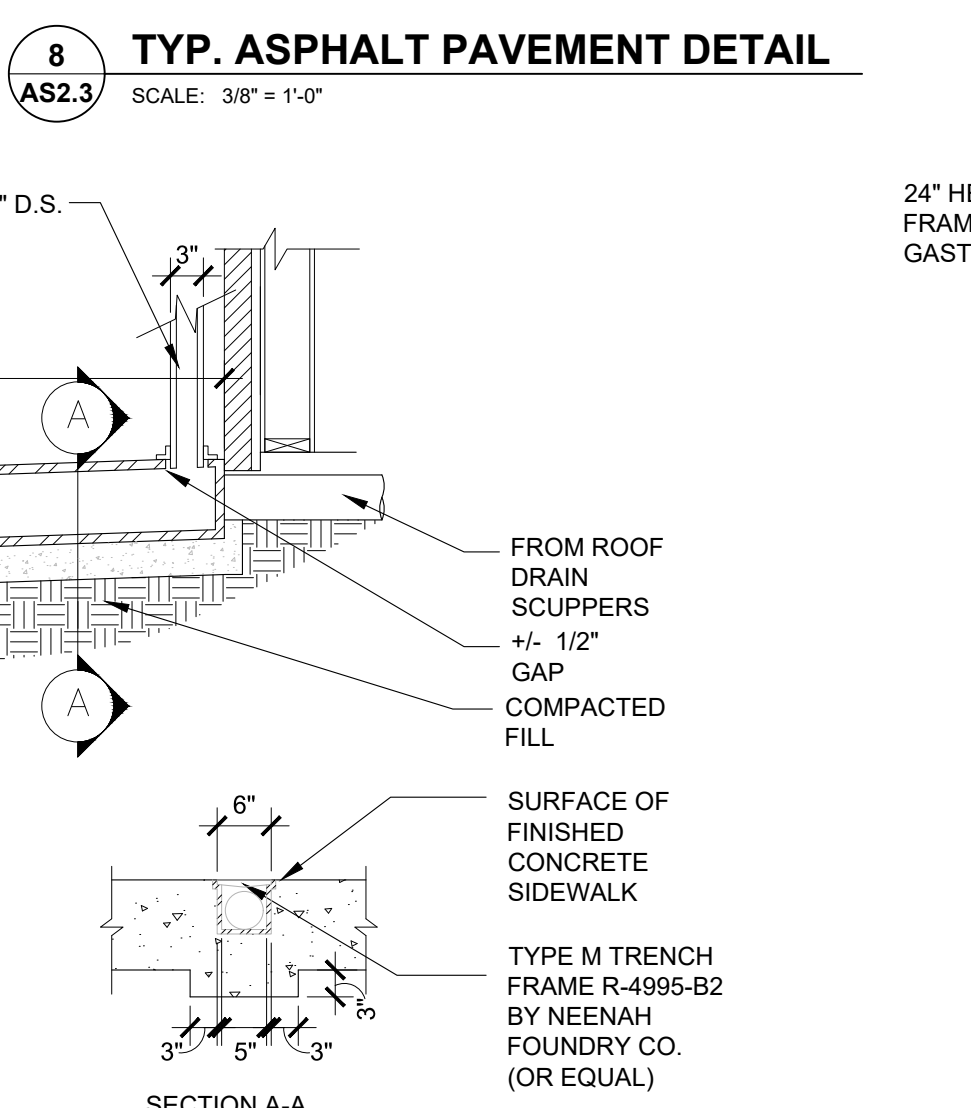

6 ROOF DRAIN FLUME
AS2.3 SCALE: 3/8" = 1'-0"

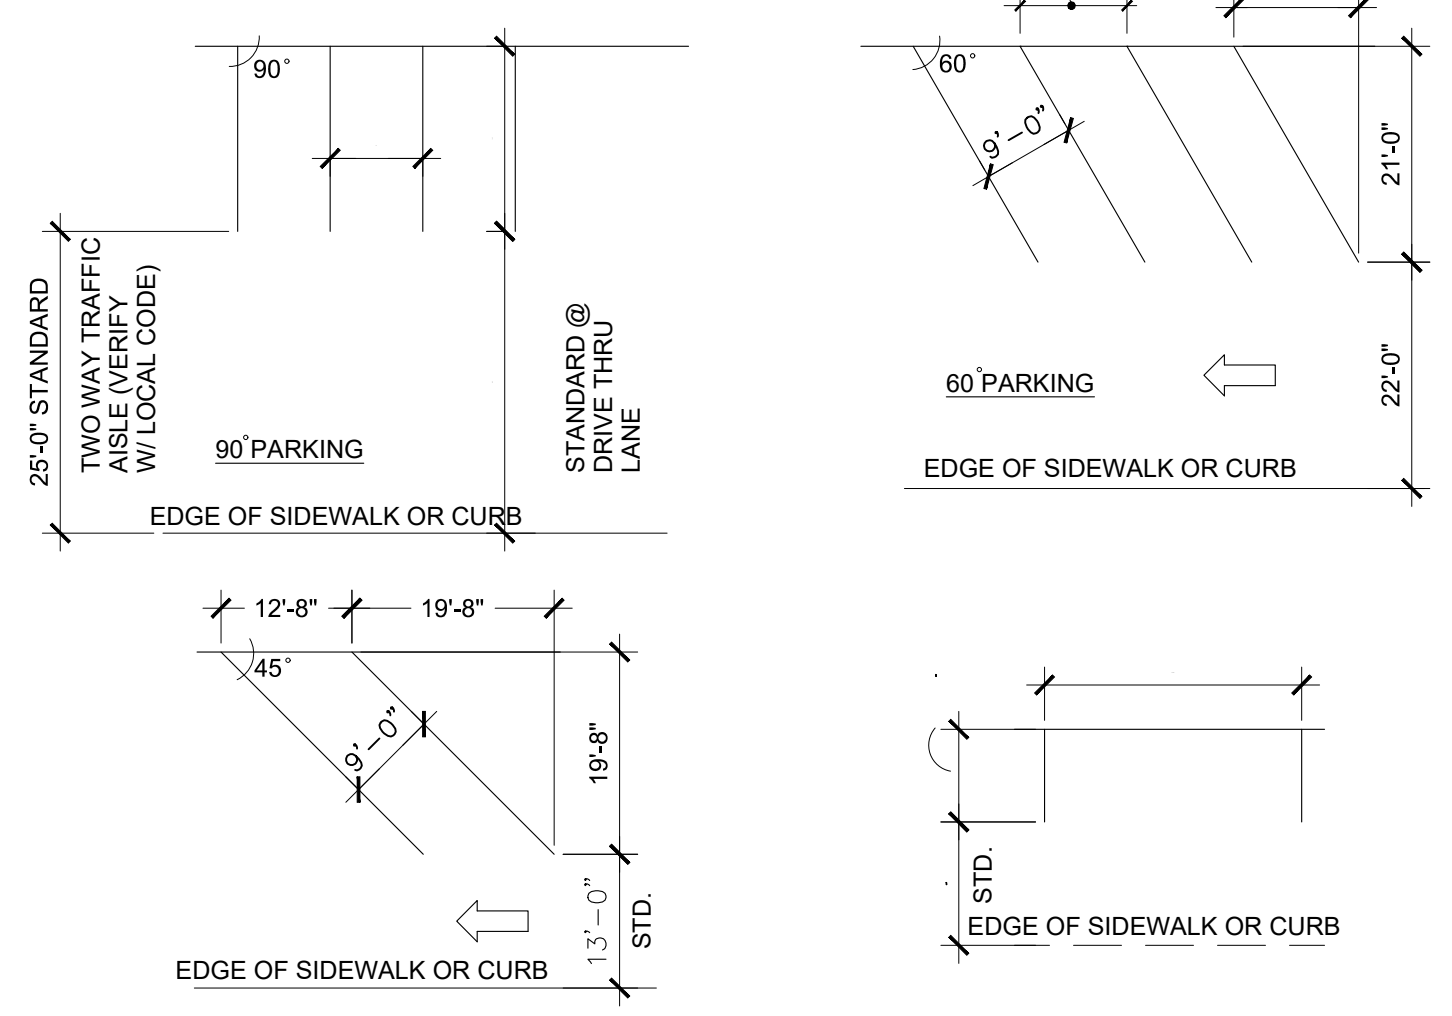

- NOTES:
1. WHEEL STOPS NOT TO BE USED UNLESS REQ'D FOR SAFETY REASONS.
 2. USE 90 DEGREE PARKING WHENEVER POSSIBLE.
 3. DIMENSIONS SHOWN ABOVE ARE BASED ON 9'X18' STALLS.

VERIFY DIMENSIONS WITH LOCAL REGULATORY AGENCY.



2 PARKING STALL STANDARDS
AS2.3 SCALE: 3/8" = 1'-0"

ISSUE TABLE

No.	Date (mm/dd/yy)	Description
01	09-26-25	DTGO PROTOTYPE DOCUMENTS

REVISIONS

No.	Date	Description
-----	------	-------------

DRAWINGS REVISED AS PER DESIGN BULLETIN

No.	Date	Description
-----	------	-------------

Professional Seal

DESIGNER NOTES:
DESIGN GUIDELINE ONLY - NOT FOR PERMIT OR CONSTRUCTION

THESE DOCUMENTS MUST BE COMPLETED AND / OR MODIFIED BY A LICENSED ARCHITECT AND ENGINEER TO CONFORM TO ALL APPLICABLE CODES, AND SPECIFIC SITE CONDITIONS. THERE IS NO WARRANTY, WHETHER IMPLIED OR EXPRESSED THAT THESE DOCUMENTS MEET THE APPLICABLE CODE REQUIREMENTS. THE LIABILITY FOR THE DESIGN AND ANY USE OF THE DOCUMENTS IS THE SOLE RESPONSIBILITY OF THE ARCHITECT AND ENGINEER OF RECORD.

Company Logo

Project


POPEYES

Store Type

US DTGO PROTOTYPE

Location

PROTOTYPE DTGO (U.S.)

CITY, STATE

Drawing Title

SITE DETAILS

Drawn

XX

Checked

XX

Scale

AS NOTED

Date



###.###

Project No.

XX

Drawing No.

AS2.3

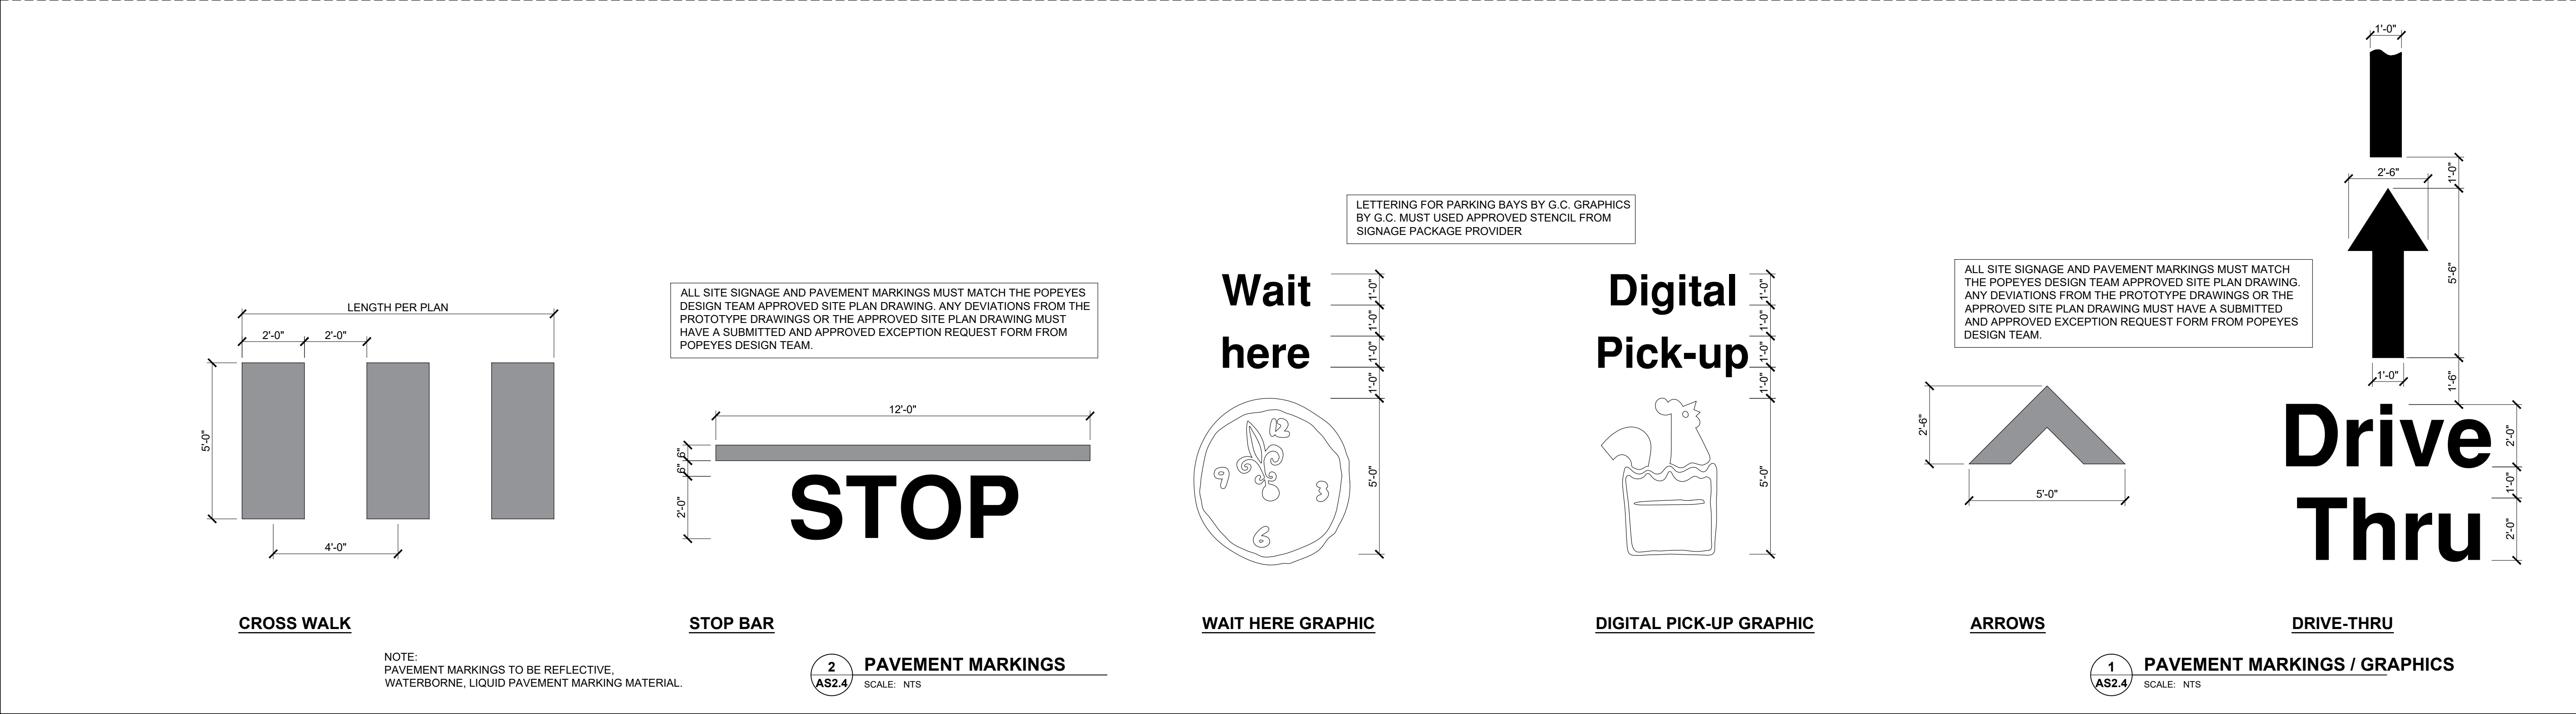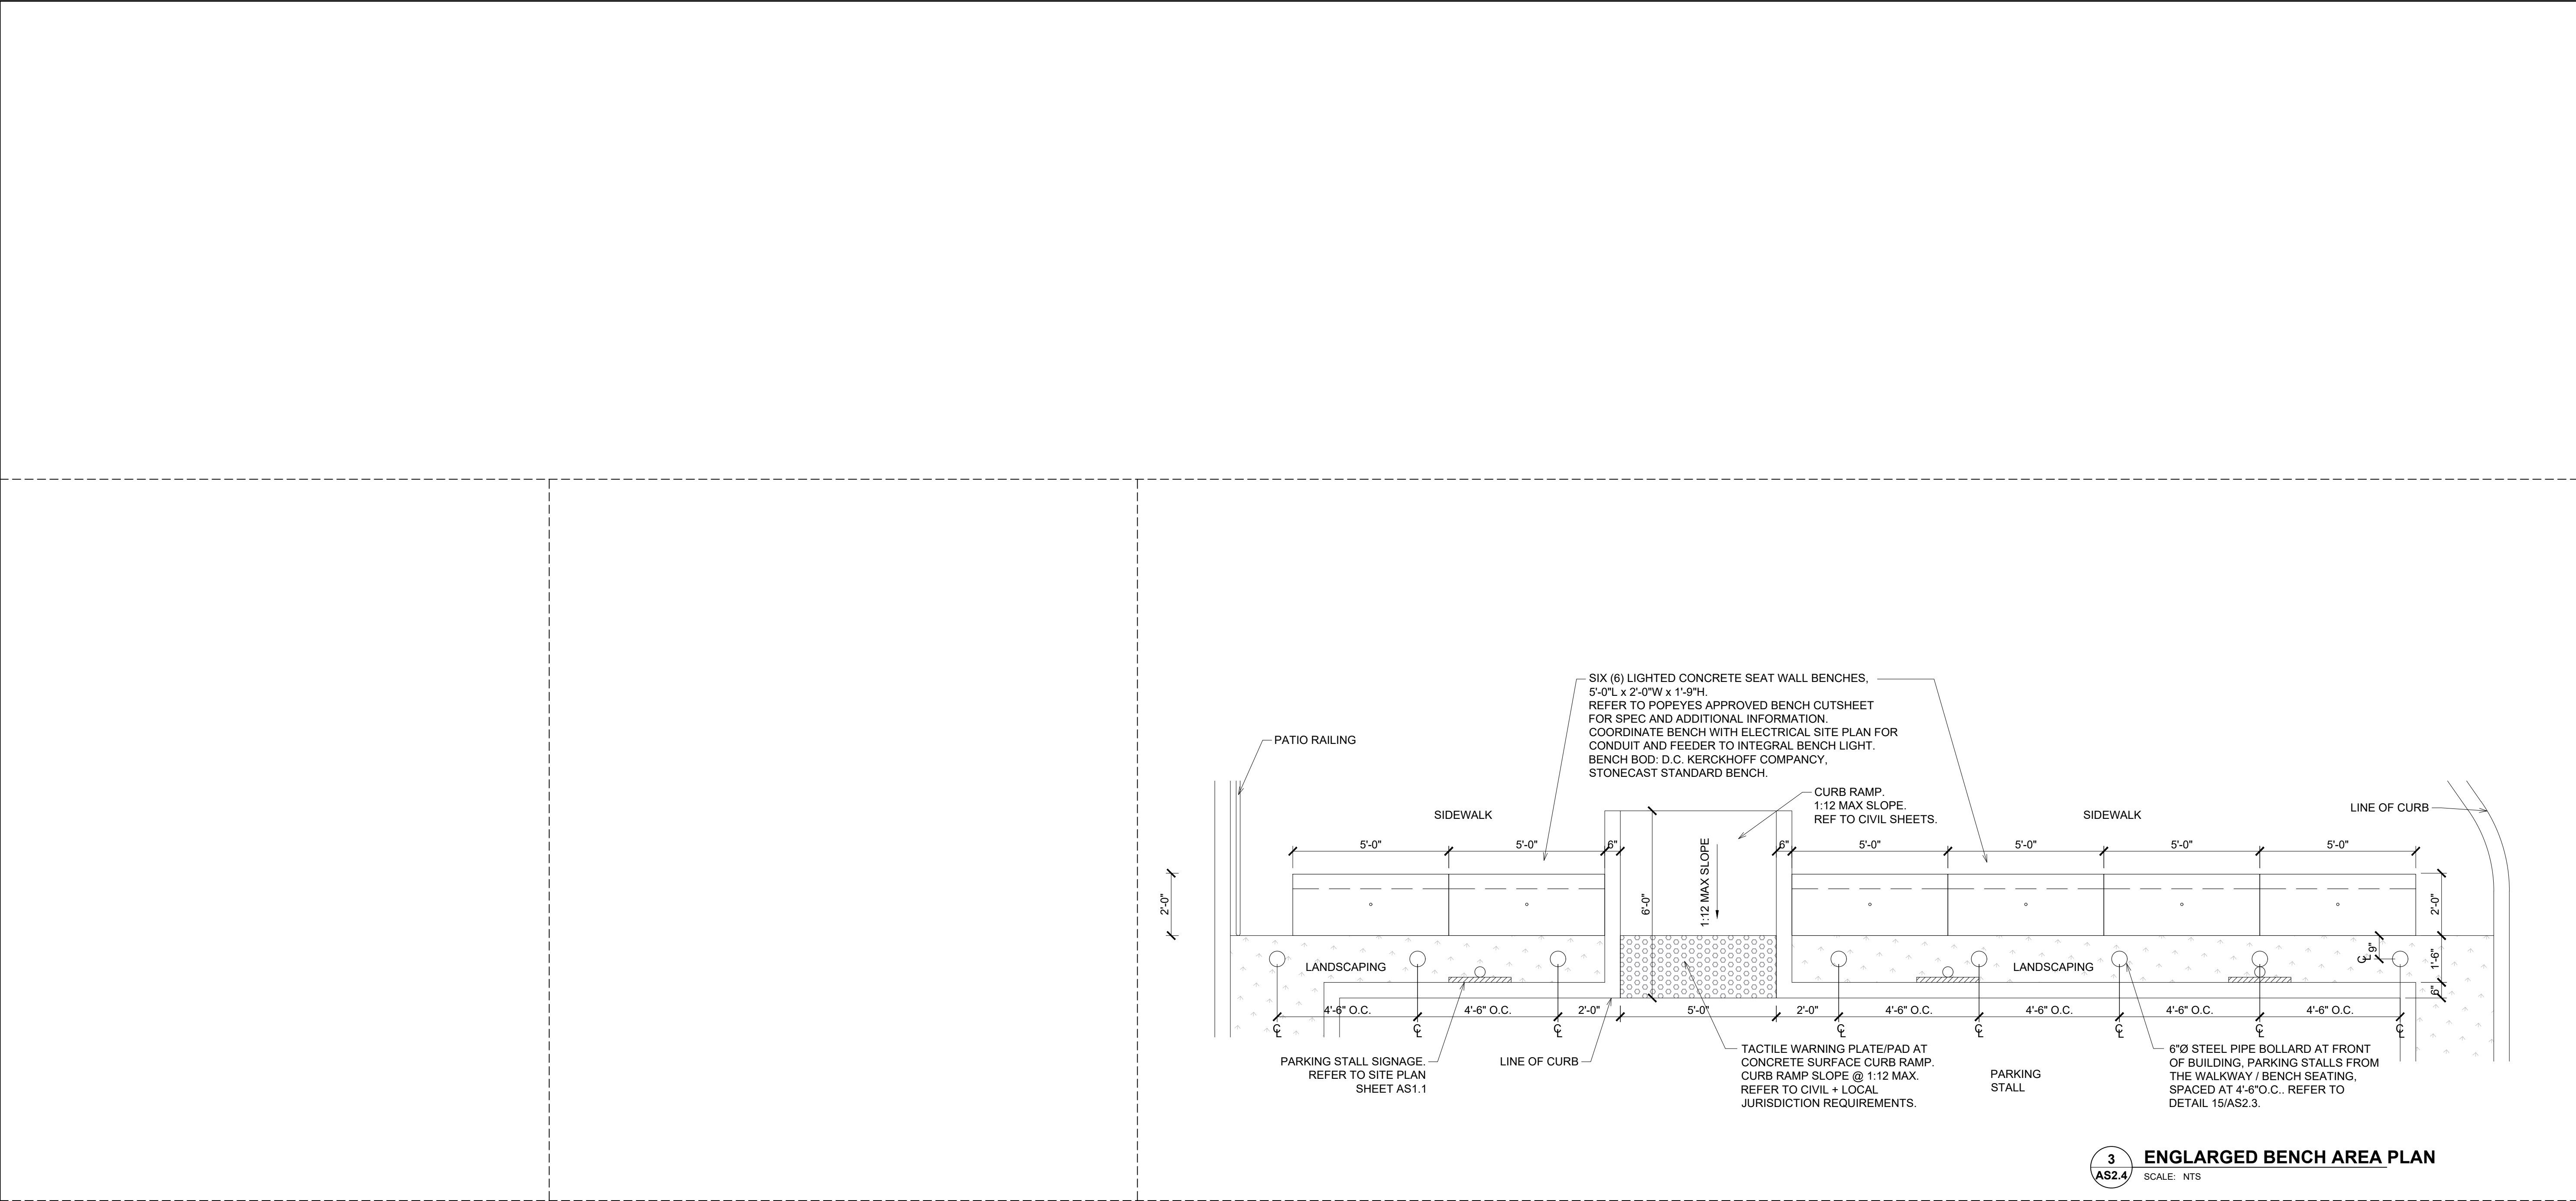

ISSUE TABLE		
No.	Date (mm/dd/yy)	Description
01	09-26-25	DTGO PROTOTYPE DOCUMENTS
REVISIONS		
No.	Date	Description
DRAWINGS REVISED AS PER DESIGN BULLETIN		
No.	Date	Description
THIS DRAWING IS OWNED BY OR LICENSED FOR USE BY POPEYES LOUISIANA KITCHEN (OR ITS AFFILIATED OR RELATED COMPANIES) AND MAY NOT BE REPRODUCED, USED, DOWNLOADED, DISSEMINATED, PUBLISHED, OR TRANSFERRED IN ANY FORM OR BY ANY MEANS, EXCEPT WITH THE PRIOR WRITTEN CONSENT OF POPEYES LOUISIANA KITCHEN. COPYRIGHT INFRINGEMENT IS A VIOLATION OF FEDERAL LAW SUBJECT TO CRIMINAL AND CIVIL PENALTIES.		
THE CONTRACTOR IS TO VERIFY ALL DIMENSIONS AND CONDITIONS ON THE PROJECT AND TO REPORT ANY DISCREPANCIES TO THE POPEYES LOUISIANA KITCHEN REPRESENTATIVE PRIOR TO COMMENCING WORK. THESE DRAWINGS ARE NOT TO BE USED FOR CONSTRUCTION PURPOSES UNLESS INDICATED BY POPEYES LOUISIANA KITCHEN AS "ISSUED FOR CONSTRUCTION".		
Professional Seal		
DESIGNER NOTES: DESIGN GUIDELINE ONLY - NOT FOR PERMIT OR CONSTRUCTION		
THESE DOCUMENTS MUST BE COMPLETED AND / OR MODIFIED BY A LICENSED ARCHITECT AND ENGINEER TO CONFORM TO ALL APPLICABLE CODES, AND SPECIFIC SITE CONDITIONS. THERE IS NO WARRANTY, WHETHER IMPLIED OR EXPRESSED THAT THESE DOCUMENTS MEET THE APPLICABLE CODE REQUIREMENTS. LIABILITY FOR THE DESIGN AND ANY USE OF THE DOCUMENTS IS THE SOLE RESPONSIBILITY OF THE ARCHITECT AND ENGINEER OF RECORD.		
Company Logo		
Project		
Store Type		
Location		
Drawing Title		
Drawn		Checked
Scale		Date
Project No.		Drawing No.



NOTE:

1. PROVIDE FULL PLYWOOD BACKING INSTEAD OF DRYLAY IN BACK OF HOUSE WHERE PERMITTED BY CODE.
2. G.C TO ENSURE THE FOLLOWING SHOP DRAWINGS ARE SUBMITTED:
 - ROOF ACCESS LADDER/CAGE/ROOF HATCH (P. ENG. STAMPED)
 - CURTAIN WALL (P. ENG. STAMPED)
 - LIST OF HARDWARE / DOORS
 - DRIVE THRU WINDOW
 - ROOFING MATERIALSREFER ALSO TO SPECIFICATION SECTIONS FOR SHOP DRAWINGS REQUIREMENTS.
3. PRIME CONSULTANT TO REQUEST THE FOLLOWING SHOP DRAWINGS TO THE RELATED VENDOR FOR REVIEW:
 - REFRIGERATION BOXES
 - MILLWORK
 - GRAPHICS
4. REFER TO MECHANICAL, ELECTRICAL AND STRUCTURAL DRAWINGS FOR MECHANICAL, ELECTRICAL AND STRUCTURAL REQUIREMENTS.

ING, UNLESS NOTED OTHERWISE. DIAGONALLY BRACE

NS FOR LAYOUT, DIMENSIONS, DETAILS, MATERIAL

SHEET A9 & A9.1 FOR WALL TILE LOCATIONS.

LOCATIONS WITH GYPSUM BOARD CEILING.

STRUCTION, IN ACCORDANCE WITH THE NYS ENERGY

IRE CAULK TOP & BOTTOM OF FIRE RATED

OF FIRE RATED SEPARATIONS.

FOR ALL INTERIOR PARTITIONS).

DRIVE THRU WINDOW UNIT AND INSULATE IT G.C.

7 PROVIDE MIN. 2" AIR SPACE BETWEEN COOLER / FREEZER AND FACE OF WALL.

8 N/A.

9 COOLER / FREEZER UNIT PROVIDED & INSTALLED BY MANUFACTURER. INTERIOR RAMP TO BE PROVIDED INSIDE FREEZER UNIT BY MANUFACTURER. G.C TO COORDINATE.

0 NOT USED.

1 CROSS HATCH INDICATES LOCATION OF SHEAR WALLS. REFER TO STRUCTURAL DRAWINGS.

2 3 5/8" METAL STUD @ 16" O.C. FUT-OUT WALL. WALL COMPLETE WITH 1/2" CEMENT BOARD EXTEND 24" A.F.F. AND 1/2" GWB EXTEND TO 6" ABOVE CEILING. PROVIDE PLYWOOD SHEATHING IN BETWEEN STUDS WHERE EQUIPMENT TO BE WALL MOUNTED.

3 N/A.

4 N/A.

5 G.C TO PROVIDE AND INSTALL S/S PANELS BEHIND AND BESIDE FRY STATION AS INDICATED. REFER TO DETAIL: 1/A8 AND INTERIOR ELEVATIONS 4/A9.1.

6 N/A

7 TELEPHONE PANEL BOARD. REFER TO ELECTRICAL DRAWINGS.

8 N/A.

9 WATER METER AND BACK FLOW PREVENTER. REFER TO PLUMBING DRAWINGS.

0 N/A.

1 FURR-OUT WALL WITH 1 LAYER OF 1/2" DUROCK NEXT GEN CEMENT BOARD UP TO 8" ABOVE CEILING ON 2" X 4" METAL STUDS @ 24" O.C. CARRY STUDS AND GYPSUM BOARD TO 6" ABOVE CEILING.

2 N/A.


3 HOSE BIB. REFER TO EXTERIOR ELEVATIONS AND MECHANICAL DRAWINGS. LOCATION TO BE COORDINATED AND VERIFIED WITH CIVIL PLAN AND OWNER.

4 G.C. TO PROVIDE FIRE ALARM ANNUNCIATOR PANEL ONLY IF REQUIRED BY AUTHORITY HAVING JURISDICTION. REFER TO ELECTRICAL DRAWINGS. (NOT SHOWN)

5 N/A.

6 WALL COVERING ON ALL WALLS IN DRESSING ROOM VESTIBULE. GC TO SUPPLY AN INSTALL THROUGH MAXIT SYSTEMS. GC TO ENSURE TO PROVIDE LEVEL 5 DRYWALL FINISH. REFER TO INTERIOR ELEVATIONS ON SHEET A9.1 AND FINISH SCHEDULE ON SHEET A10.

POPEYES LOUISIANA KITCHEN MODEL DTGO, ADDRESS, CITY, STATE: DTGO PROTOTYPE DOCUMENTS (OCTOBER, 2025) STORE NO. XXXXX

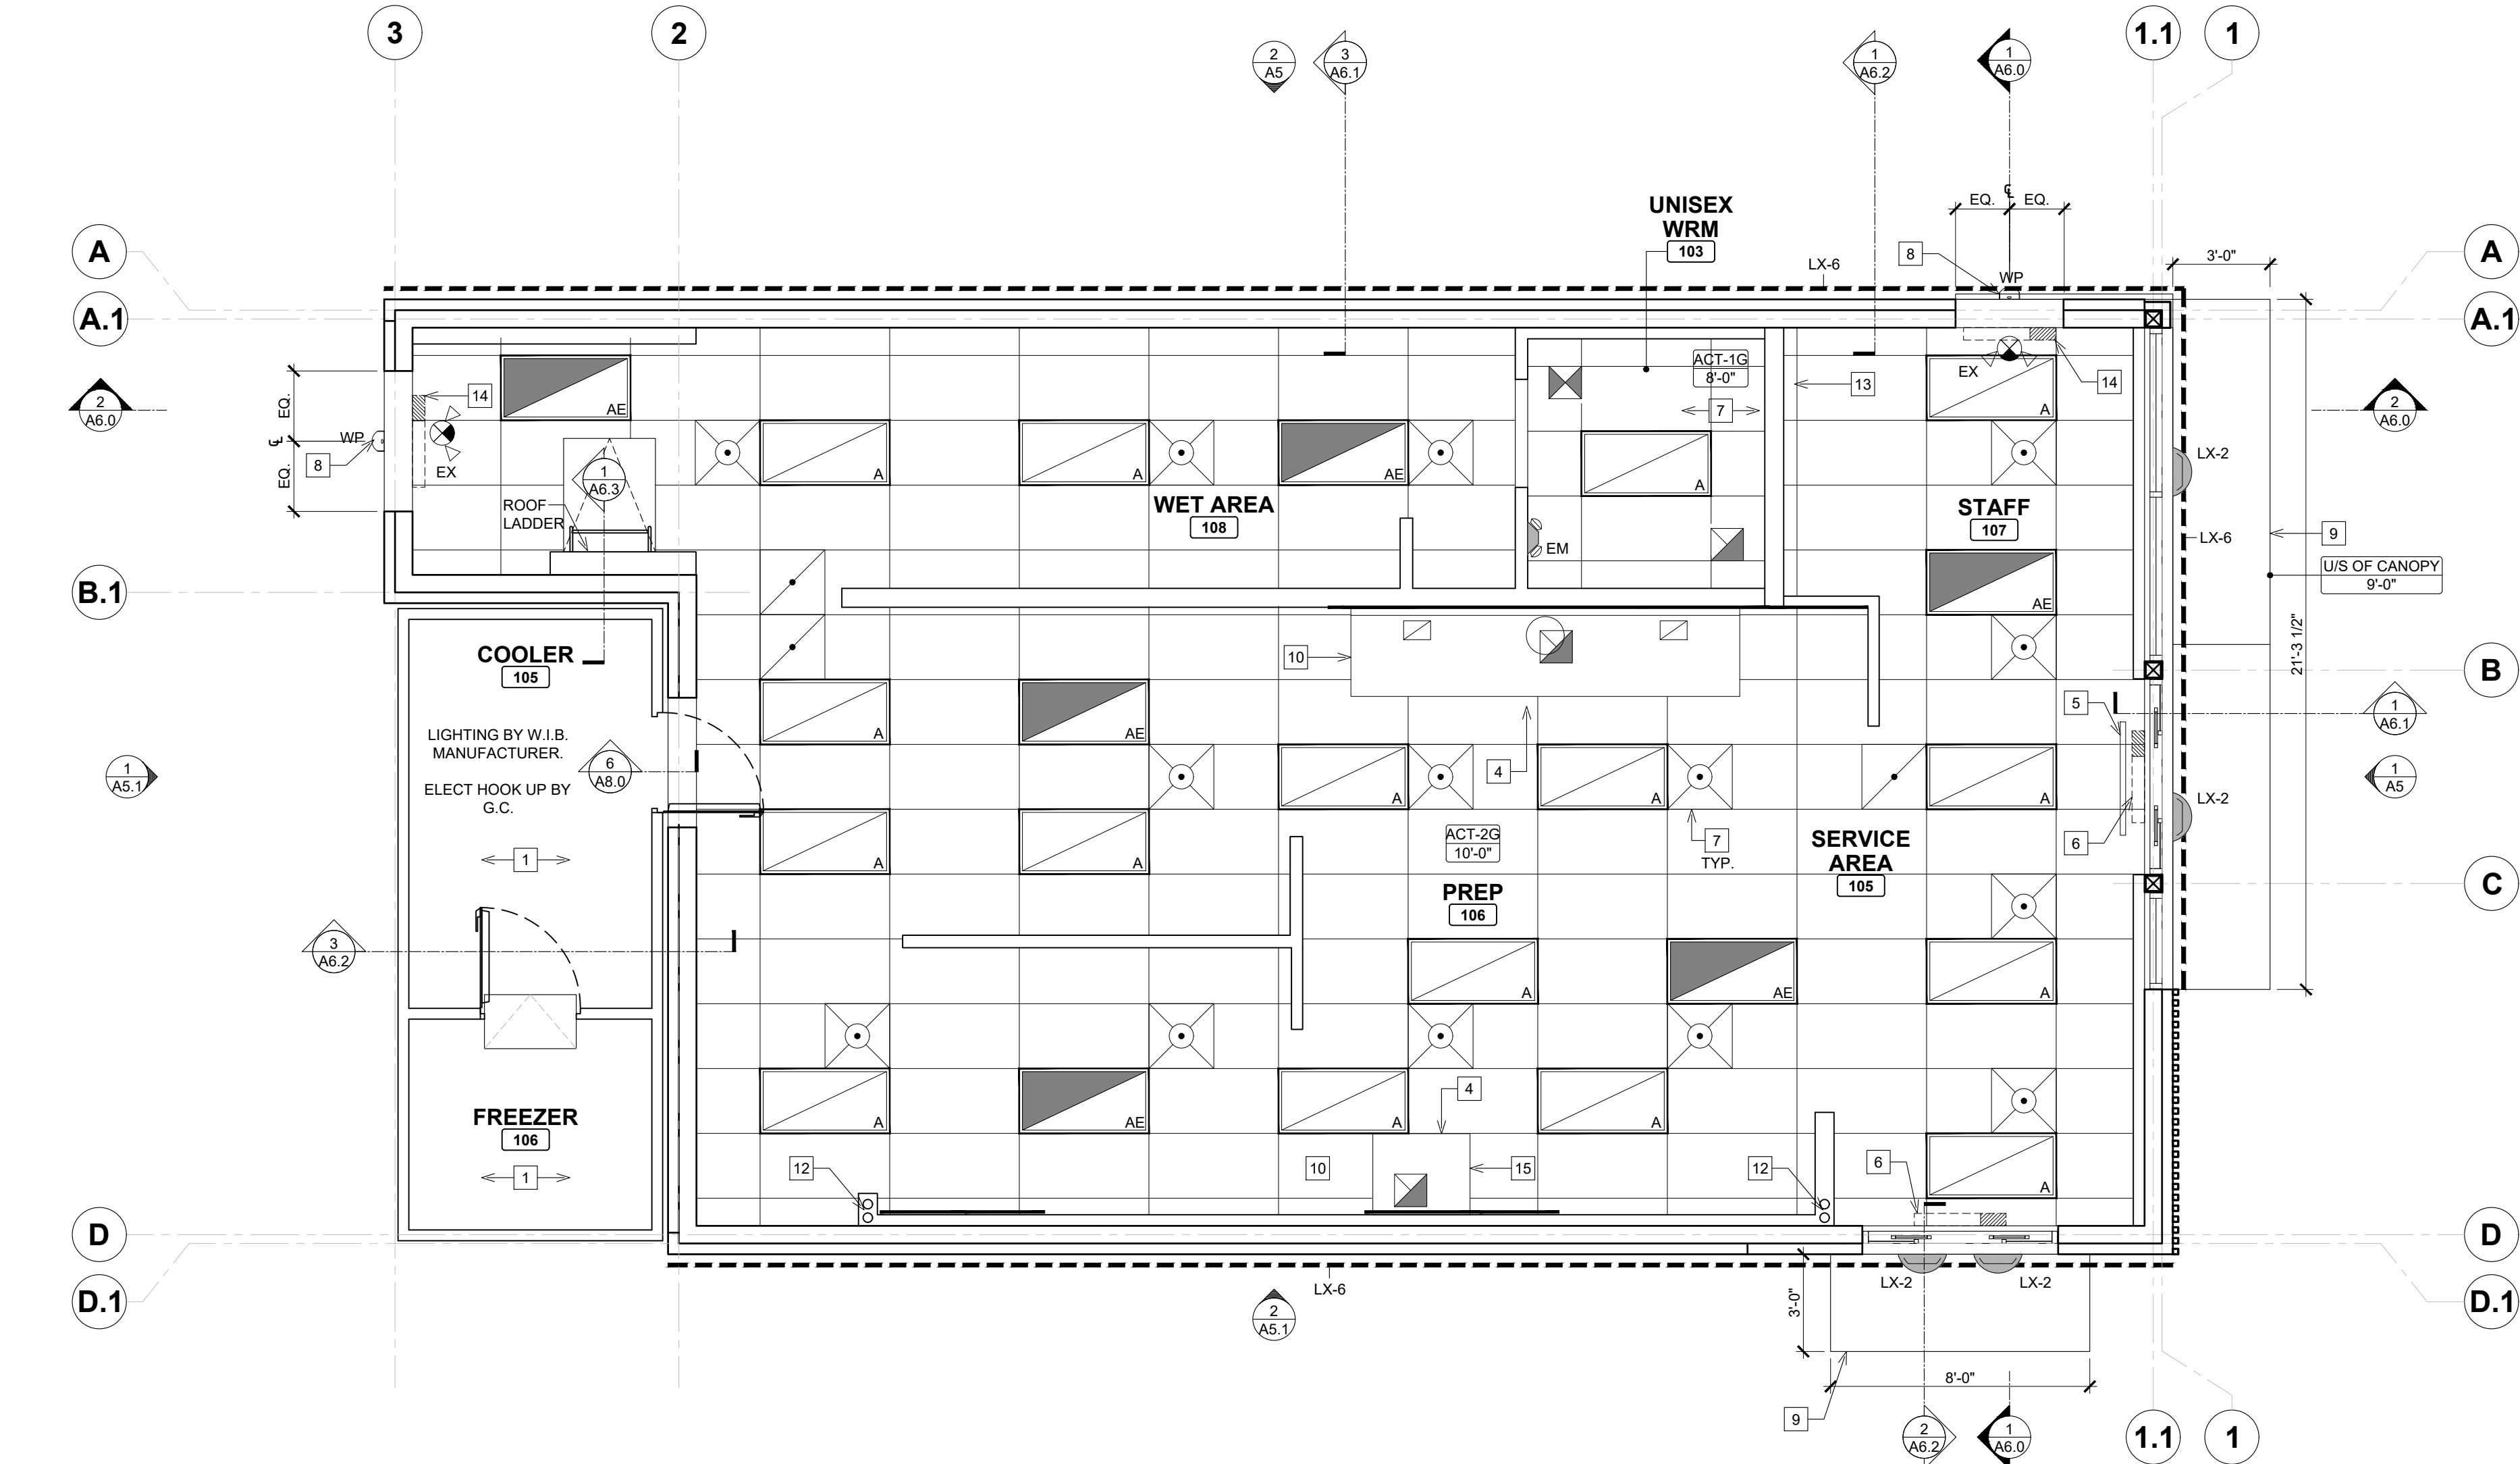

1
A3
REELECTED CEILING PLAN
SCALE: 1/4"=1'-0"

3
A3
N/A
SCALE: 2"=1'-0"

4
A3
N/A
SCALE: 1"=1'-0"

SECURITY CAMERA LEGEND (16.3)

CAP INDEX	SECURITY PACKAGE #	CAMERA #S
0<100	1	1-4
100<250	2	1-8
>250	3	1-12

NOTES:
- WITH PACKAGE #2 AND #3, 4 EXTRA CAMERAS ARE AVAILABLE TO BE LOCATED AT THE OWNERS DISCRETION
* IF A CAMERA IS INSTALLED IN STAFF AREA, OWNER IS TO INFORM STAFF. *

	CAMERAS	#	NUMBER OF CAMERAS
--	---------	---	-------------------



5
A3
N/A
SCALE: 2"=1'-0"

CEILING PLAN NOTES

- REFER TO WALK-IN FREEZER & COOLER MANUFACTURER FOR EVAPORATOR AND LIGHTING. FINAL CONNECTION BY G.C.
- N/A.
- N/A.
- EXHAUST HOODS SUPPLY BY OWNER AND INSTALL BY G.C.REFER TO MECHANICAL DRAWINGS.
- TRUSS HUNG LED SCREENS SUPPLIED BY POPEYES. AND INSTALLED BY G.C. REFER TO DETAIL S/A8. G.C TO PROVIDE & INSTALL ADEQUATE BLOCKING FOR SUPPORT.
- LOCATION OF AIR CURTAIN. REFER TO MECHANICAL/ELECTRICAL DRAWINGS. GC TO PROVIDE AND INSTALL ELECTRICAL POWER FOR AIR CURTAIN. OPERATORS TO BE PROVIDED AT DRIVE-THRU WINDOW FOR AIR CURTAIN. REFER TO ELECTRICAL DRAWINGS.
- ALL DIFFUSERS & RETURN AIR GRILLES TO BE WHITE.
- REFER TO EXTERIOR ELEVATIONS FOR MOUNTING LOCATION OF WALL MOUNTED LIGHT FIXTURES (TYP.)
- LINE OF CANOPY ABOVE. SUPPLY AND INSTALL BY G.C. REFER TO DETAILS AND STRUCTURAL DRAWINGS.
- G.C. TO SUPPLY AND INSTALL 20 GA. STAINLESS STEEL PANEL ON CEILING TILE W/ HOLD DOWN CLIP AROUND EXHAUST HOOD. DO NOT FASTEN TO EXHAUST FOOT. ANY DAMAGED TO THE EQUIPMENT HOOD WILL BE AT THE COST OF G.C.
- NOT USED
- RAINWATER LEADER. REFER TO MECHANICAL DRAWINGS.
- G.C. TO SUPPLY AND INSTALL EXHAUST FAN IN THE CABINET TO VENT ABOVE CEILING AT OFFICE DESK.
- AIR CURTAIN AT DOOR. GC TO PROVIDE AND INSTALL ELECTRICAL POWER FOR AIR CURTAIN. REFER TO ELECTRICAL DRAWINGS.
- HOOD USED ONLY WHERE THE CITY REQUESTS HOOD ABOVE EQUIPMENT.

NOTE:

1. THE GENERAL CONTRACTOR IS TO ENSURE THE FOLLOWING ITEMS ARE BUILT IN ACCORDANCE WITH STRUCTURAL DRAWINGS AND TO MEET CODE REQUIREMENTS (INCLUDING SEISMIC AND LATERAL RESTRAINT) AS REQUIRED:
- SUSPENDED SHELVING SUPPORTS
- SEISMIC AND LATERAL RESTRAINT FOR DUCTWORK
- SUSPENDED CEILING PANELS, GYPSUM BOARD / T-BAR CEILINGS IN RELATION TO SEISMIC AND LATER RESTRAINT.

2. THE GENERAL CONTRACTOR IS RESPONSIBLE THAT ALL SUB-TRADES HAVE RETAINED A QUALIFIED STRUCTURAL ENGINEER TO REVIEW THEIR APPROPRIATE WORK. STRUCTURAL ENGINEER(S) TO ISSUE LETTER (ON THEIR LETTERHEAD) STATING THAT ALL WORK MEETS THE REQUIREMENT OF BUILDING CODE FOR SEISMIC RESTRAINTS.

GRAPHIC SYMPOLES

TYPE	DESCRIPTION
	SECTION NUMBER DRAWING NUMBER
	NOTE REFERENCE
	DENOTES CEILING HT & MATERIAL.

RCP PLAN LEGEND

TYPE	DESCRIPTION
	24"X24" OR 12"X12" SUPPLY AIR GRILLE. REFER TO MECHANICAL DRAWINGS.
	24"X24" OR 12"X12" RETURN AIR GRILLE. REFER TO MECHANICAL DRAWINGS.
	EXHAUST FAN
	AIR TRANSFER DUCT. REFER TO MECHANICAL DRAWINGS.

LIGHT FIXTURE LEGEND

TYPE	DESCRIPTION
A	2'-0" X 4'-0" RECESSED LED TROFFER
AE	2'-0" X 4'-0" RECESSED LED TROFFER W/ BATTERY BACKUP
EX	EXIT SIGN AND EMERGENCY LIGHTING WITH BATTERY BACKUP
EM	EMERGENCY BATTERY LIGHT FIXTURE
WP	LED WALL PACK WITH PHOTOCELL
LX-2	FLUSH MOUNT LED LIGHT FIXTURE AT CANOPIES
LX8	LINEAR PERIMETER PARAPET DOWNLIGHT

ISSUE TABLE		
No.	Date (mm/dd/yy)	Description
01	09-26-25	DTGO PROTOTYPE DOCUMENTS
REVISIONS		
No.	Date	Description
DRAWINGS REVISED AS PER DESIGN BULLETIN		
No.	Date	Description

THIS DRAWING IS OWNED BY OR LICENSED FOR USE BY POPEYES LOUISIANA KITCHEN (OR ITS AFFILIATED OR RELATED COMPANIES) AND MAY NOT BE REPRODUCED, USED, DOWNLOADED, DISSEMINATED, PUBLISHED, OR TRANSFERRED IN ANY FORM OR BY ANY MEANS, EXCEPT WITH THE PRIOR WRITTEN CONSENT OF POPEYES LOUISIANA KITCHEN. COPYRIGHT INFRINGEMENT IS A VIOLATION OF FEDERAL LAW SUBJECT TO CRIMINAL AND CIVIL PENALTIES.

THE CONTRACTOR IS TO VERIFY ALL DIMENSIONS AND CONDITIONS ON THE PROJECT AND TO REPORT ANY DISCREPANCIES TO THE POPEYES LOUISIANA KITCHEN REPRESENTATIVE PRIOR TO COMMENCING WORK. THESE DRAWINGS ARE NOT TO BE USED FOR CONSTRUCTION PURPOSES UNLESS INDICATED BY POPEYES LOUISIANA KITCHEN AS "ISSUED FOR CONSTRUCTION".

Professional Seal

DESIGNER NOTES:
DESIGN GUIDELINE ONLY - NOT FOR PERMIT OR CONSTRUCTION

THESE DOCUMENTS MUST BE COMPLETED AND / OR MODIFIED BY A LICENSED ARCHITECT AND ENGINEER TO CONFORM TO ALL APPLICABLE CODES, AND SPECIFIC SITE CONDITIONS. THERE IS NO WARRANTY, WHETHER IMPLIED OR EXPRESSED THAT THESE DOCUMENTS MEET THE APPLICABLE CODE REQUIREMENTS. THE LIABILITY FOR THE DESIGN AND ANY USE OF THE DOCUMENTS IS THE SOLE RESPONSIBILITY OF THE ARCHITECT AND ENGINEER OF RECORD.

Company Logo


Project

Store Type
US DTGO PROTOTYPE

Location
CITY, STATE


Drawing Title
REFLECTED CEILING PLAN

Drawn XX	Checked XX
Scale 1/4"=1'-0"	Date ###.##.####
Project No. XX	Drawing No. A3

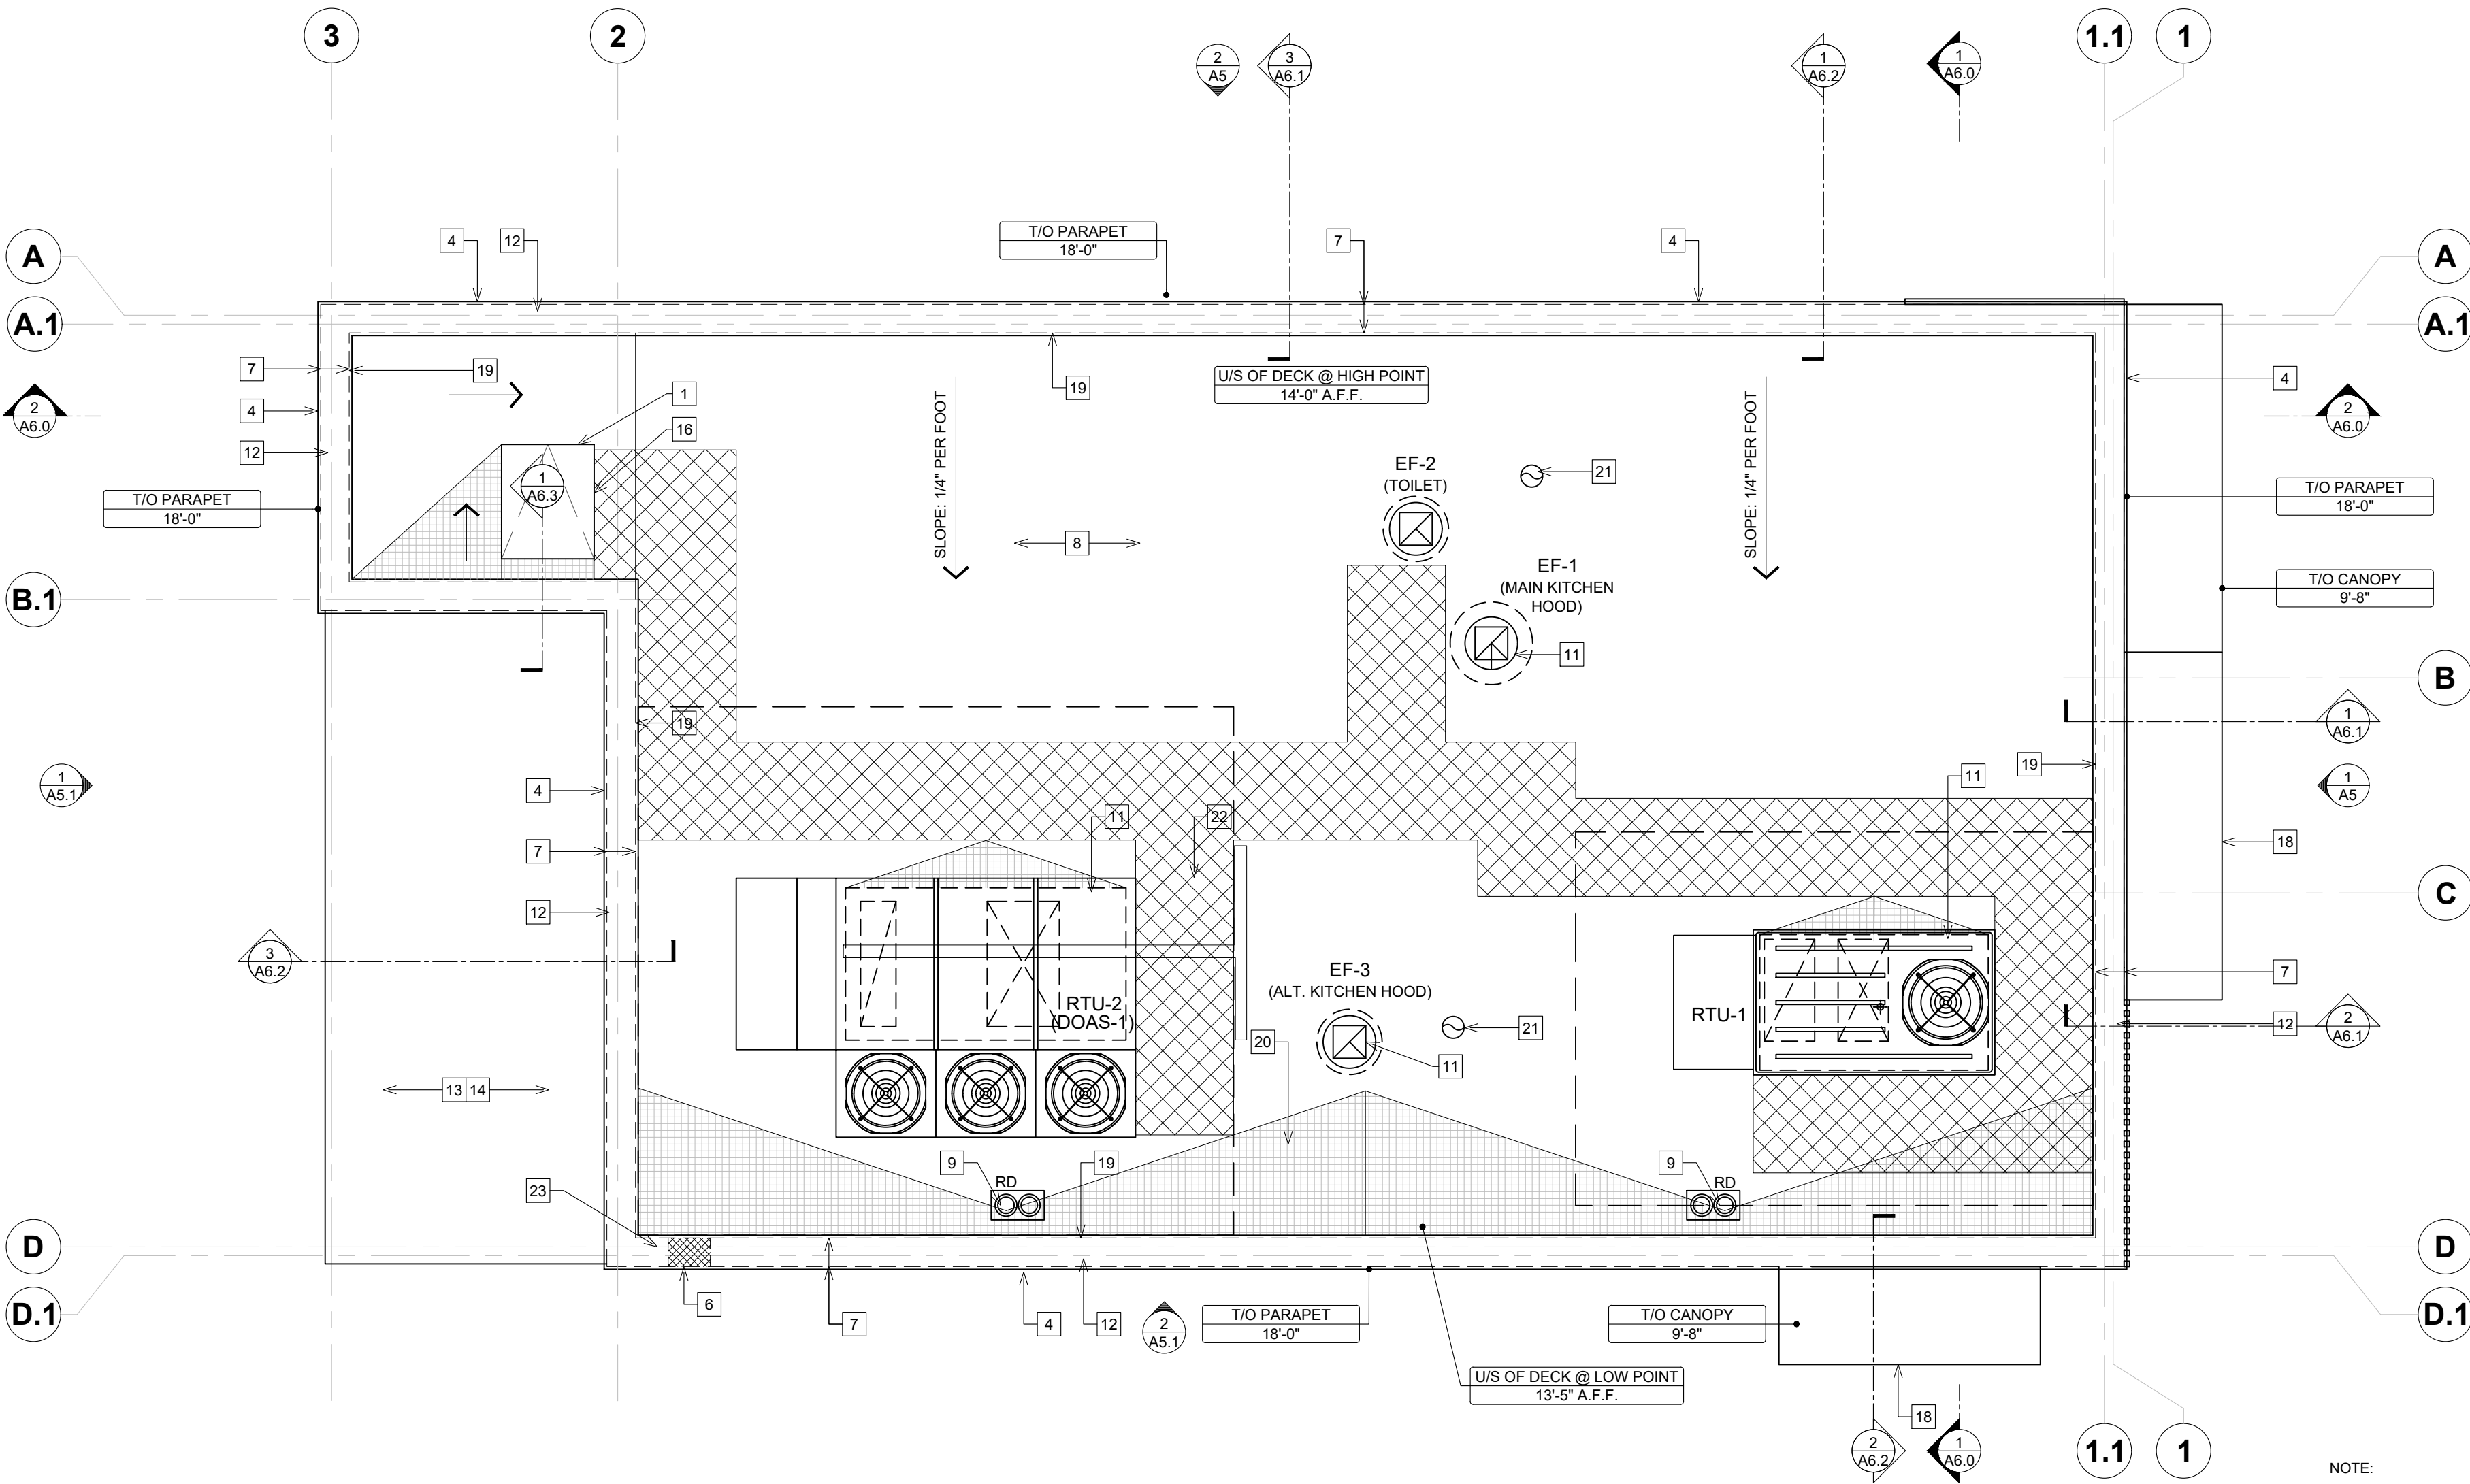


1 ROOF PLAN
SCALE: 1/4"=1'-0"


- NOTE:
- ALL ROOFING TO BE IN STRICT ACCORDANCE WITH THE NATIONAL ROOFING CONTRACTORS ASSOCIATION ROOFING MANUAL.
 - G.C IS RESPONSIBLE FOR SEALING ALL ROOF PENETRATIONS UPON COMPLETION OF THE PROJECT.

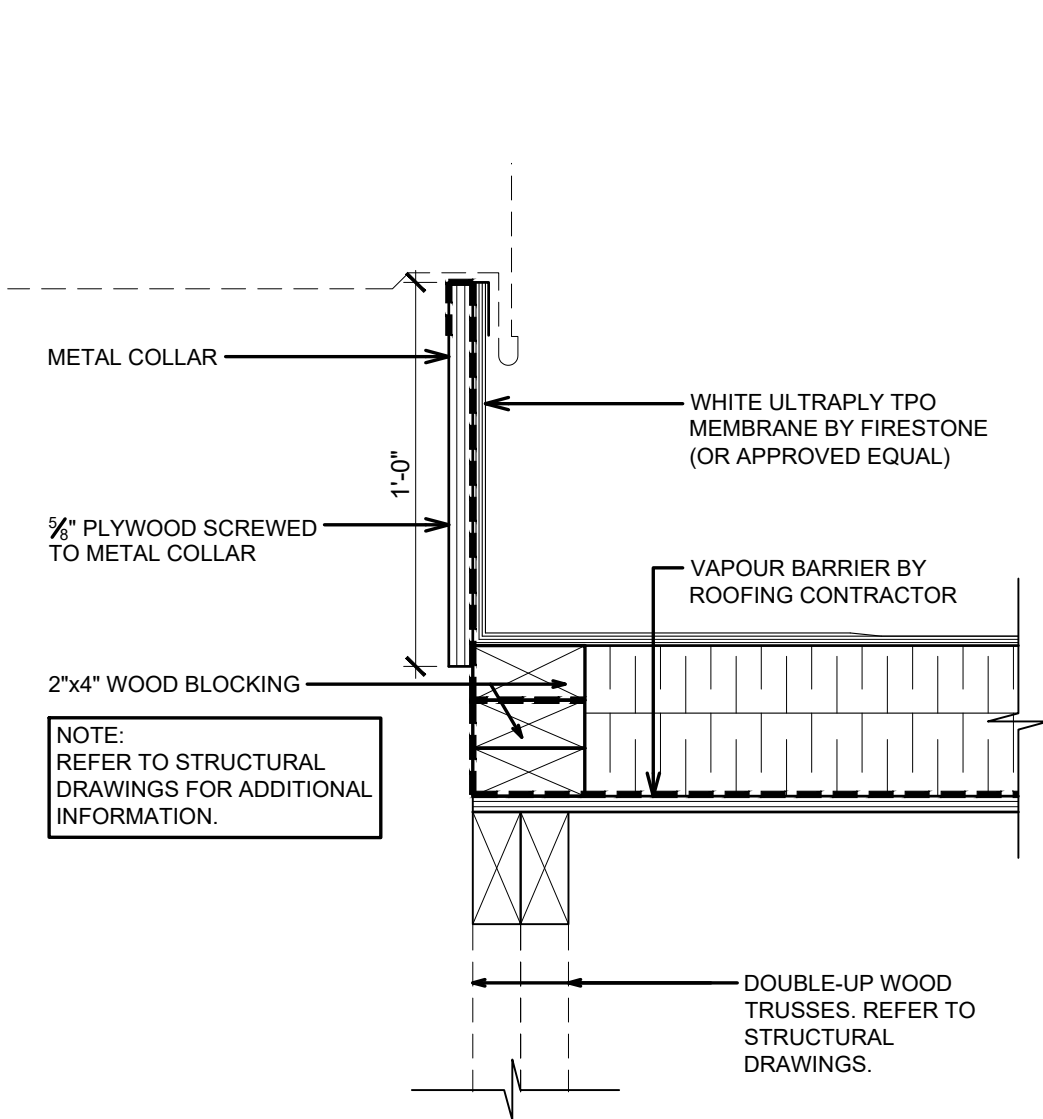

2 TYPICAL ROOF CURB DETAIL
SCALE: 2"=1'-0"

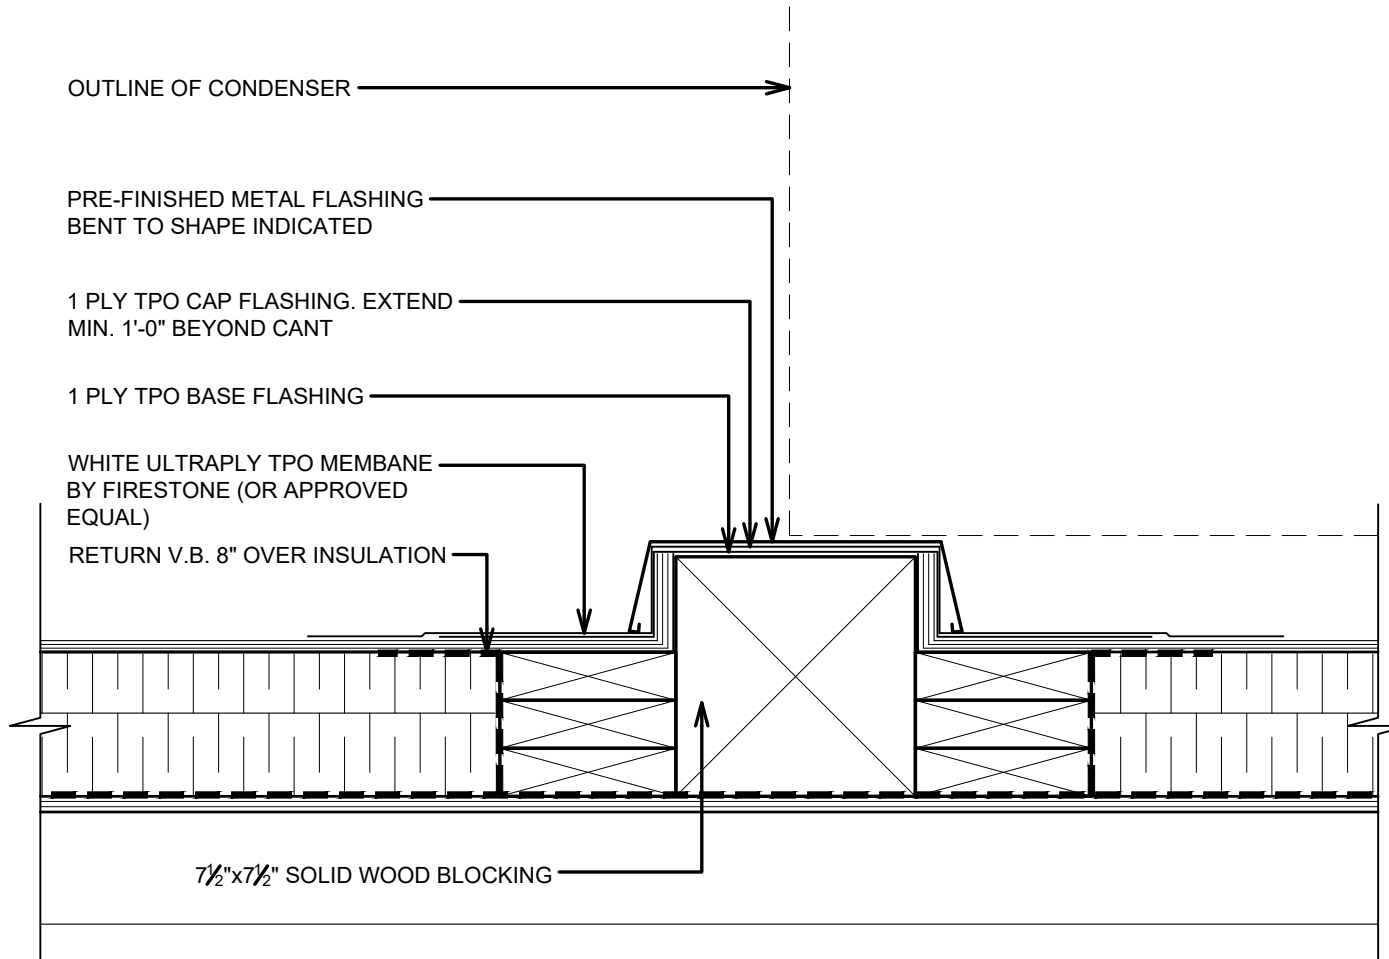

3 TYPICAL SLEEPER DETAIL
SCALE: 2"=1'-0"

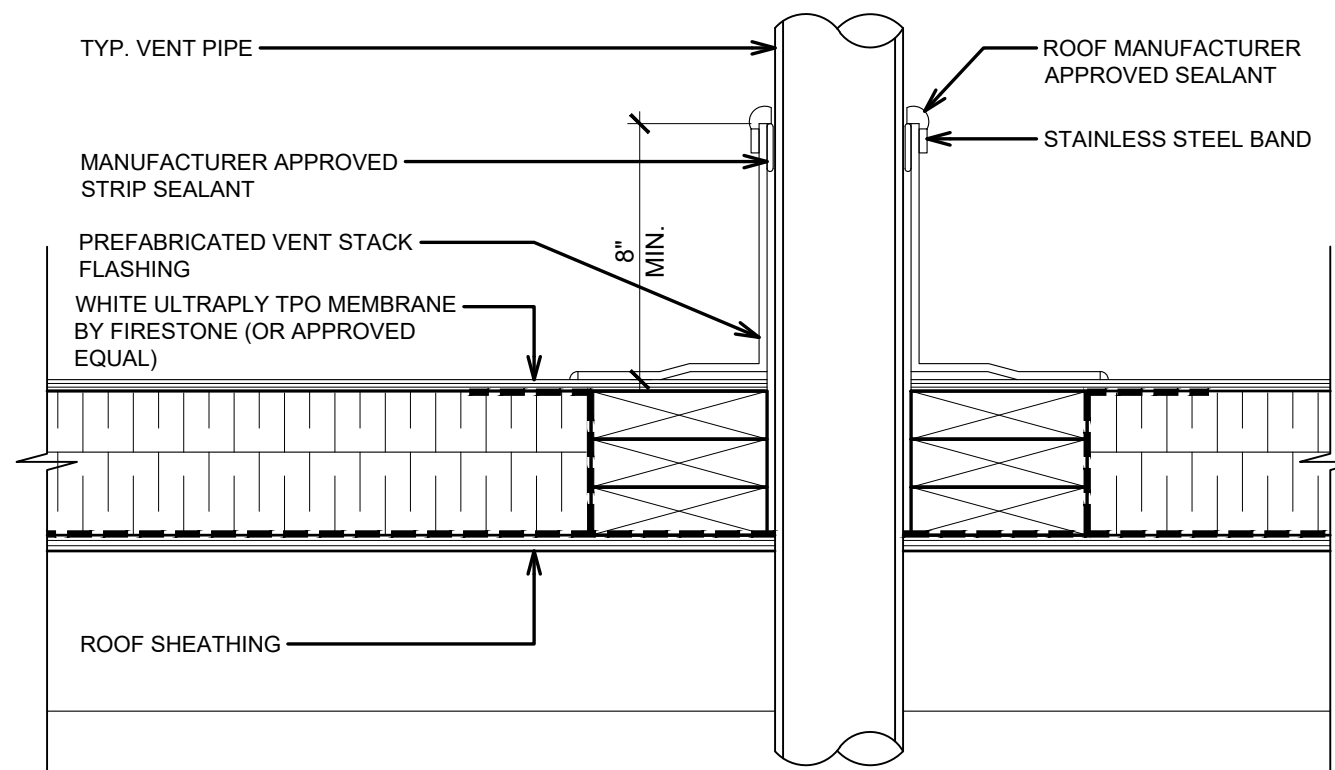

4 VENT PENETRATION DETAIL
SCALE: 2"=1'-0"

SYMBOL LEGEND

- 1 A1 DETAIL NUMBER
DRAWING NUMBER
- 1 NOTE REFERENCE

ROOF TYPE LEGEND

ROOF ASSEMBLY:

- MAS 60mil WHITE ULTRAPLY TPO MEMBRANE (OR APPROVED EQUAL)
- 2 LAYERS OF RIGID INSULATION (R-30.0 MIN.)
- 10mil VAPOUR RETARDER
- WOOD ROOF DECK
- WOOD TRUSS (AS PER NRCA STANDARDS)

DESIGNER NOTES:
VERIFY R-VALUE PER
PROJECT LOCATION

CALCULATED ROOF AREA

HORIZONTAL ROOF SURFACE (S.F.) 1,305
VERTICAL SURFACE 50% AREA (S.F.) 567
TOTAL PROJECTED ROOF AREA (S.F.) 1,872

DRAINAGE CALCULATIONS:

(SIZE OF VERTICAL CONDUCTORS AND LEADERS)

100 YEAR, 1 HOUR RAIN FALL (IN.) 3"

(PER FIGURE 1106.1, 2024 INTERNATIONAL PLUMBING CODE)

VERTICAL LEADER SIZE (RECTANGULAR) 3-1/2" X 4"

SPECIFIED LEADER CAPACITY (SINGLE) 5300 S.F.

(PER TABLE 1106.2(2), 2024 INTERNATIONAL PLUMBING CODE)


REQUIRED OVERFLOW SCUPPER SIZE (SINGLE) 1" X 10.7"

VERTICAL LEADER (X2) CAPACITY PROVIDED 10,600 S.F.


ROOF PLAN NOTES

- ROOF ACCESS HATCH TO MATCH PRE-FINISHED METAL CAP FLASHING. REFER TO DETAIL 1/A6.3.
- N/A.
- N/A.
- LINE OF PARAPET. REFER TO DETAILS ON SHEET A7.0.
- N/A.
- PRE-FINISHED EMERGENCY OVERFLOW SCUPPER. REFER TO DETAIL 2/A4.1.
- LINE OF WALL BELOW.
- WHITE ULTRAPLY TPO MEMBRANE BY FIRESTONE (OR APPROVED EQUAL). REFER TO ROOF TYPE SCHEDULE & SPECIFICATIONS.
- PRIMARY ROOF DRAIN, WITH COMBINATION OVERFLOW DRAIN, REFER MECHANICAL DRAWINGS.
- N/A.
- H.V.A.C. UNITS AND EXHAUST FANS AS PER MECHANICAL DRAWINGS. PROVIDE CURB WHERE REQUIRED. REFER TO DETAIL 2/A4.
- PRE-FINISHED METAL CAP FLASHING. REFER TO EXTERIOR FINISH SCHEDULE ON SHEET A5 FOR COLOUR AND TYPE.
- PROVIDE SLEEPERS FOR WALK-IN COOLER/FREEZER CONDENSER. SLEEPERS TO SPAN ACROSS JOISTS BELOW. REFER TO DETAIL 3/A4 & STRUCTURAL DRAWINGS.
- EXTERIOR WALK-IN COOLER/FREEZER ROOF.
- G.C TO PROVIDE AND INSTALL DOUBLE PIPE PORTAL (PART NO. 36002) C/W C-126 & C-212 CAP FOR PCL LINES MECH EQUIPMENT. ROOF OPENING (2'-3" X1'-0") AND ROOF CURBS TO BE PROVIDED AND FURNISHED BY G.C. REFER TO DETAIL 4/A4 & 1/A4.1.
- PROVIDE & INSTALL 3M NON-SLIP TAPE ON FLASHING AT LADDER LOCATION.
- NOT USED.
- CANOPY BELOW. REFER TO EXTERIOR ELEVATIONS.
- EXTEND ROOF MEMBRANE UP PARAPET WALL AND OVER TOP OF FRAMING (TYP.). SECURE PREFABRICATED ROOF EDGE CLEATS THROUGH MEMBRANE AS SPECIFIED BY MANUFACTURER. REFER TO WALL SECTIONS AND DETAILS.
- CROSS HATCH INDICATES TAPERED INSULATION OVER SPECIFIED RIGID THERMAL INSULATION (TYP.) FIELD VERIFY ROOF DRAIN LOCATIONS PRIOR TO INSTALLATION & INSTALL PER ROOF MANUFACTURER SPECIFICATIONS. G.C TO COORDINATE ACTUAL EXTENTS OF TAPERED INSULATION MATERIALS WITH ROOF INSTALLER & VERIFY INSTALLED COUNTER SLOPE OF 1/2" PER FOOT (MIN., AS MEASURED FROM LEVEL PLANE) TO DIRECT STORM WATER TOWARD ROOF DRAINS AS INDICATED ON PLAN.
- VENTS. REFER TO MECHANICAL DRAWINGS & DETAIL 4/A4.
- TPO WALK WAY PADS OR X-TREADS. REFER TO SPECIFICATIONS. CUT TPO WALK WAY PAD ROLLS TO MAXIMUM OF 9'-10". LEAVE A GAP OF 1" BETWEEN PIECES TO ALLOW FOR WATER DRAINAGE.
- EMERGENCY THRU-WALL SCUPPER W/ METAL FLANGE BY ROOFING MANUFACTURER. BOTTOM OF SCUPPER OPENING TO BE 2" ABOVE THE ADJACENT ROOF SURFACE. SECONDARY ROOF DRAIN SYSTEMS SHALL HAVE THE END POINT OF DISCHARGE SEPARATE FROM THE PRIMARY SYSTEM. DISCHARGE SHALL BE ABOVE GRADE. VERIFY OPENING REQUIREMENTS WITH LOCAL CONDITIONS.

ISSUE TABLE		
No.	Date (mm/dd/yy)	Description
01	09-26-25	DTGO PROTOTYPE DOCUMENTS
REVISIONS		
No.	Date	Description
DRAWINGS REVISED AS PER DESIGN BULLETIN		
No.	Date	Description
THIS DRAWING IS OWNED BY OR LICENSED FOR USE BY POPEYES LOUISIANA KITCHEN (OR ITS AFFILIATED OR RELATED COMPANIES) AND MAY NOT BE REPRODUCED, USED, DOWNLOADED, DISSEMINATED, PUBLISHED, OR TRANSFERRED IN ANY FORM OR BY ANY MEANS, EXCEPT WITH THE PRIOR WRITTEN CONSENT OF POPEYES LOUISIANA KITCHEN. COPYRIGHT INFRINGEMENT IS A VIOLATION OF FEDERAL LAW SUBJECT TO CRIMINAL AND CIVIL PENALTIES.		
THE CONTRACTOR IS TO VERIFY ALL DIMENSIONS AND CONDITIONS ON THE PROJECT AND TO REPORT ANY DISCREPANCIES TO THE POPEYES LOUISIANA KITCHEN REPRESENTATIVE PRIOR TO COMMENCING WORK. THESE DRAWINGS ARE NOT TO BE USED FOR CONSTRUCTION PURPOSES UNLESS INDICATED BY POPEYES LOUISIANA KITCHEN AS "ISSUED FOR CONSTRUCTION".		
Professional Seal		
DESIGNER NOTES: DESIGN GUIDELINE ONLY - NOT FOR PERMIT OR CONSTRUCTION		
THESE DOCUMENTS MUST BE COMPLETED AND / OR MODIFIED BY A LICENSED ARCHITECT AND ENGINEER TO CONFORM TO ALL APPLICABLE CODES, AND SPECIFIC SITE CONDITIONS. THERE IS NO WARRANTY, WHETHER IMPLIED OR EXPRESSED, THAT THESE DOCUMENTS MEET THE APPLICABLE CODE REQUIREMENTS. LIABILITY FOR THE DESIGN AND ANY USE OF THE DOCUMENTS IS THE SOLE RESPONSIBILITY OF THE ARCHITECT AND ENGINEER OF RECORD.		
Company Logo		
Project		
Store Type		
US DTGO PROTOTYPE		
Location		
PROTOTYPE DTGO (U.S.)		
CITY, STATE		
Drawing Title		
ROOF PLAN AND DETAILS		
Drawn	XX	Checked XX
Scale	1/4"=1'-0"	Date ###.###.####
Project No.	XX	Drawing No. A4

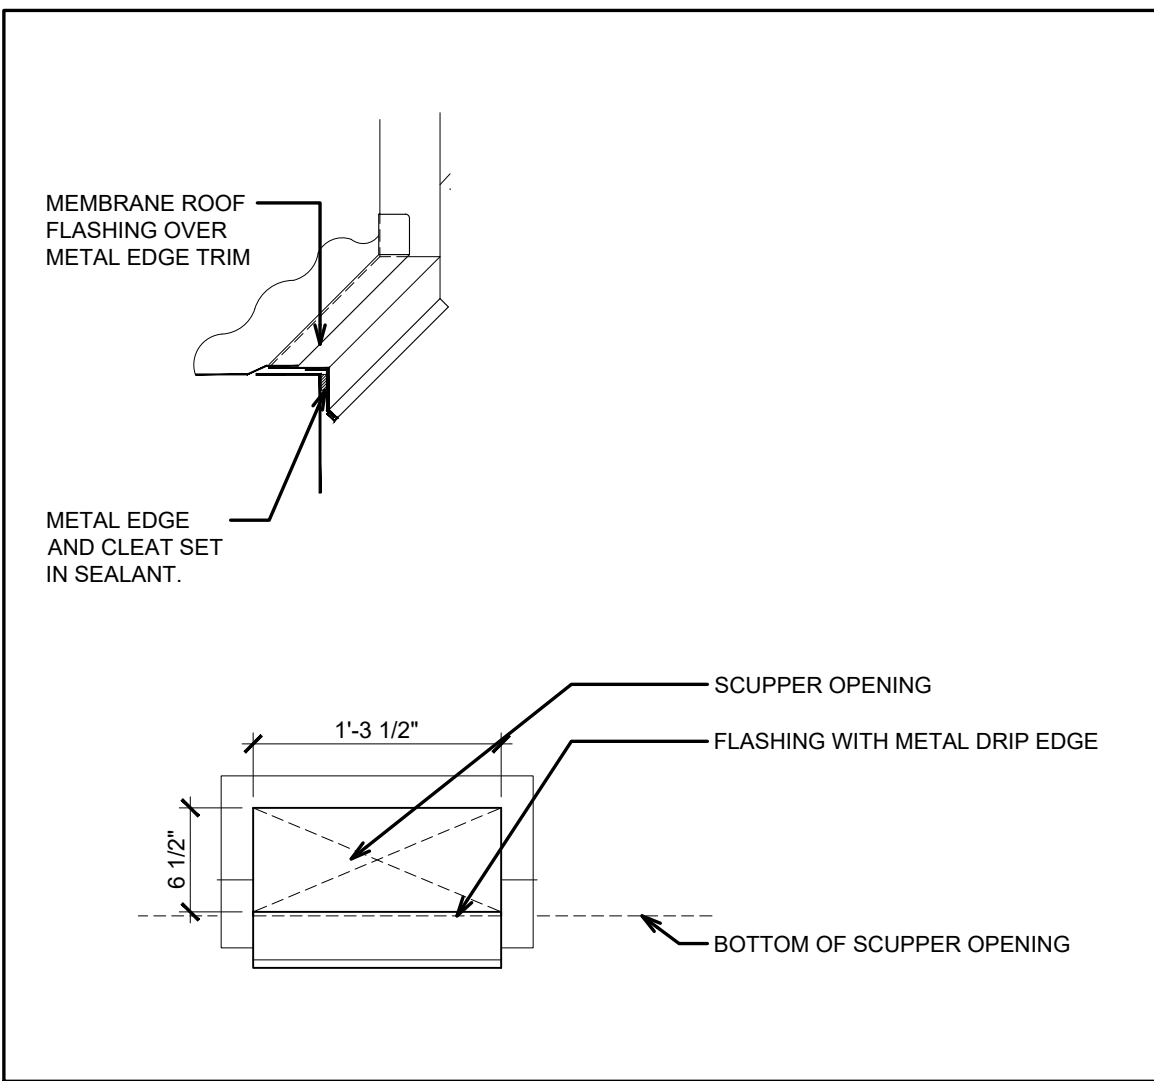

2
A4.1 **EMERGENCY OVERFLOW SCUPPER DETAIL**
SCALE: 1"=1'-0"

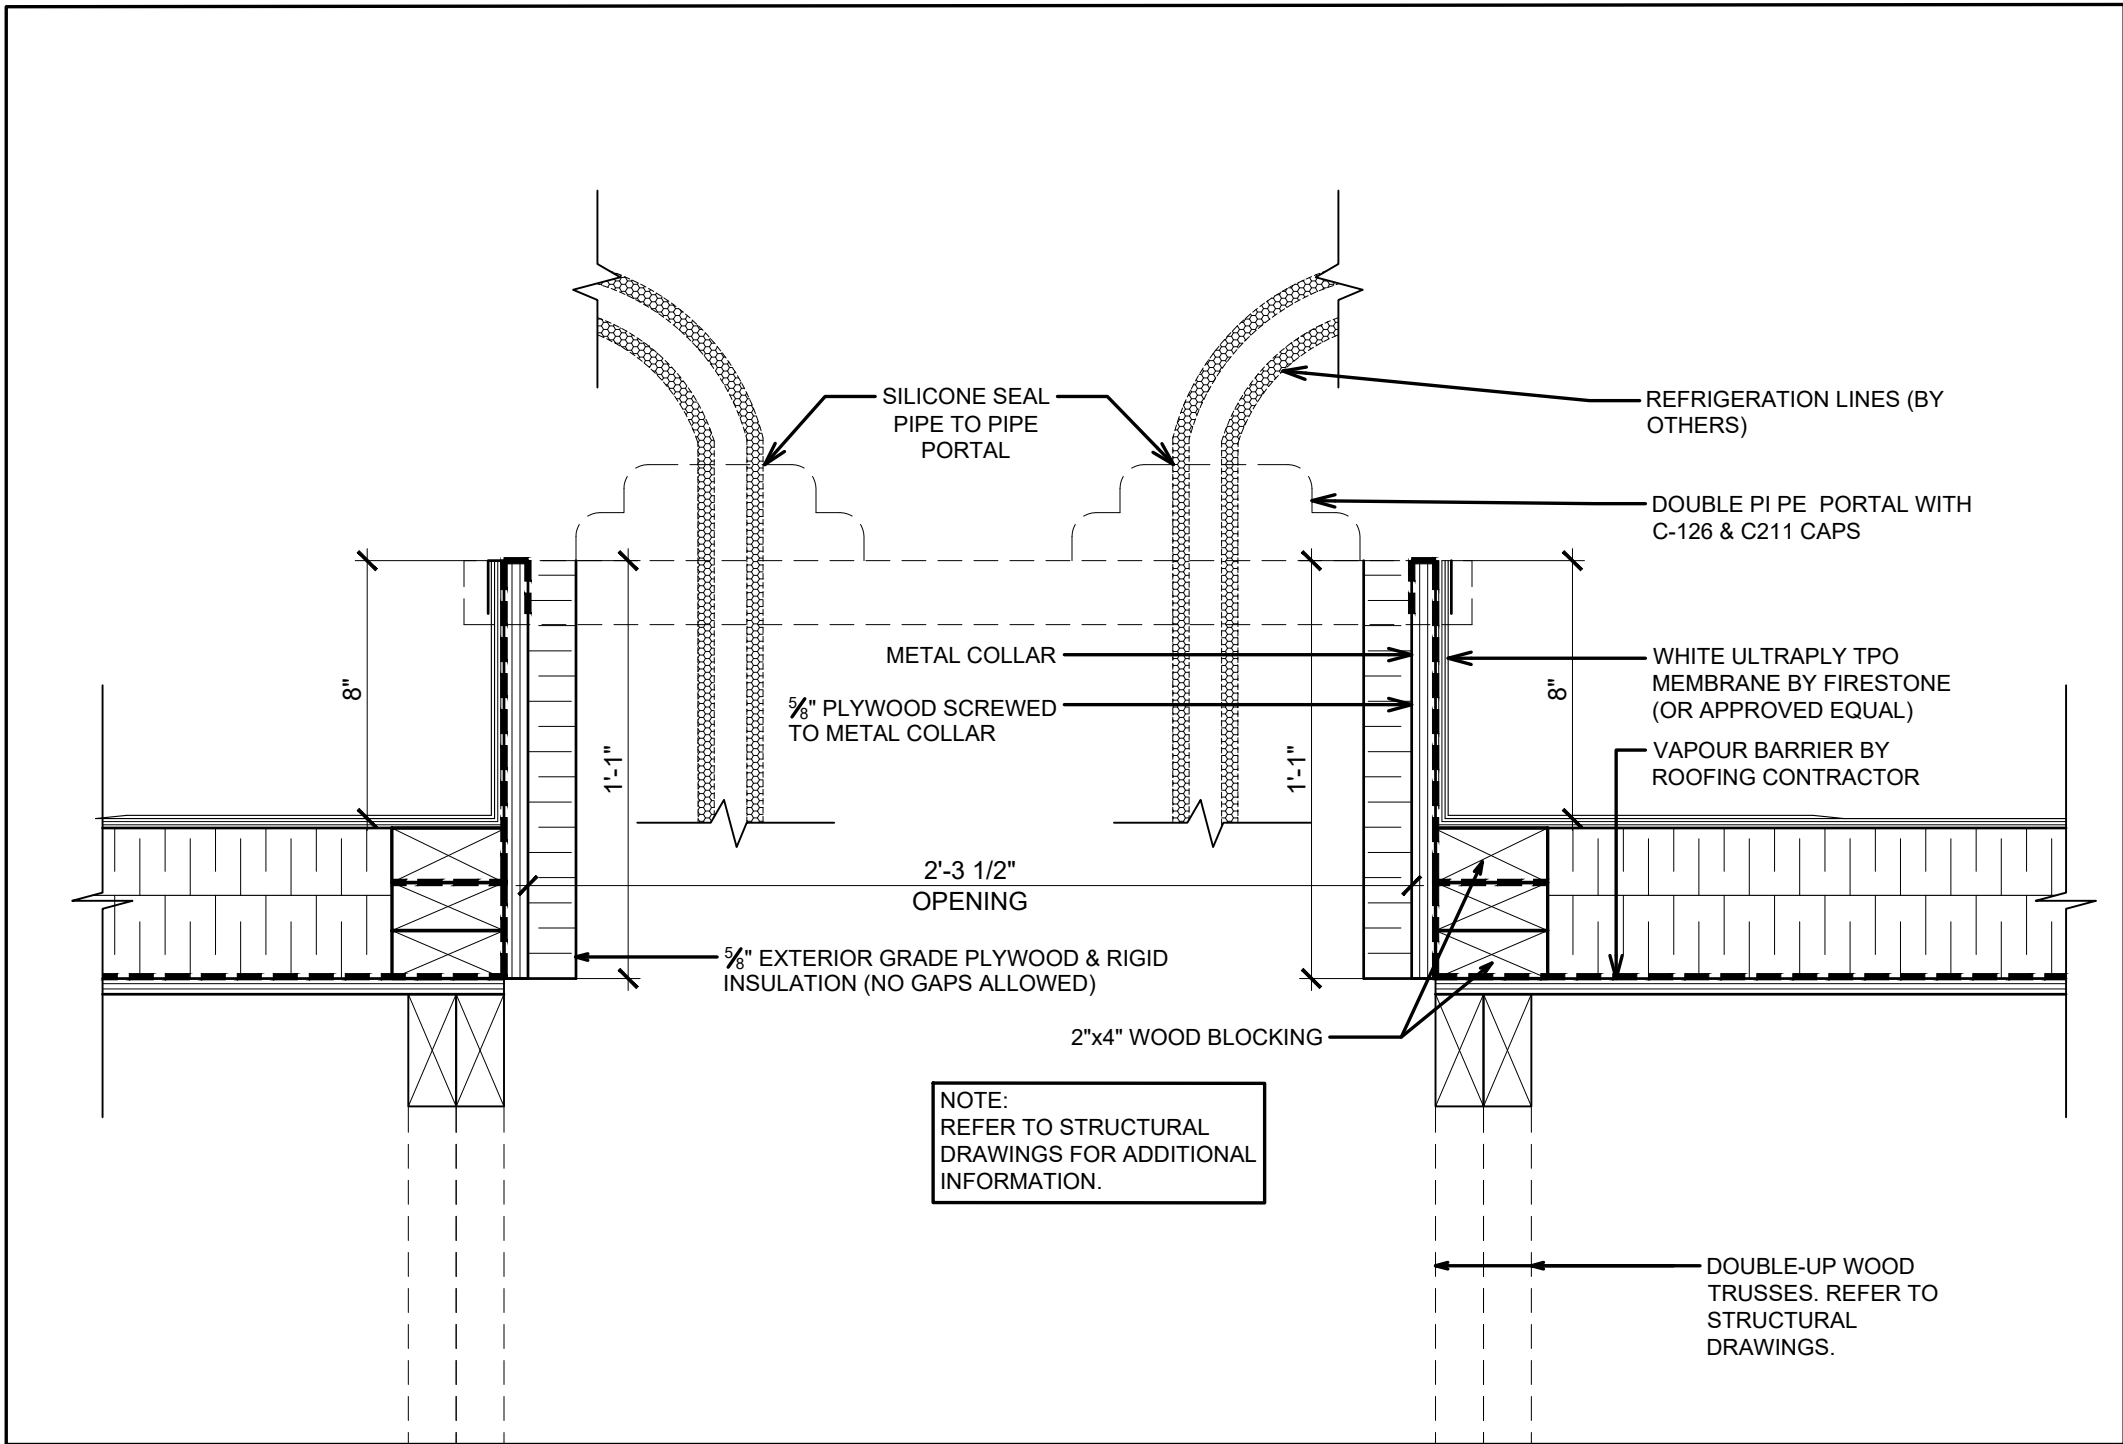

1
A4.1 **TYPICAL ROOF OPENING DETAIL AT PIPE PORTAL**
SCALE: 2"=1'-0"

ISSUE TABLE		
No.	Date (mm/dd/yy)	Description
01	09-26-25	DTGO PROTOTYPE DOCUMENTS

REVISIONS		
No.	Date	Description

DRAWINGS REVISED AS PER DESIGN BULLETIN		
No.	Date	Description

THIS DRAWING IS OWNED BY OR LICENSED FOR USE BY POPEYES LOUISIANA KITCHEN (OR ITS AFFILIATED OR RELATED COMPANIES) AND MAY NOT BE REPRODUCED, USED, DOWNLOADED, DISSEMINATED, PUBLISHED, OR TRANSFERRED IN ANY FORM OR BY ANY MEANS, EXCEPT WITH THE PRIOR WRITTEN CONSENT OF POPEYES LOUISIANA KITCHEN. COPYRIGHT INFRINGEMENT IS A VIOLATION OF FEDERAL LAW SUBJECT TO CRIMINAL AND CIVIL PENALTIES.

THE CONTRACTOR IS TO VERIFY ALL DIMENSIONS AND CONDITIONS ON THE PROJECT AND TO REPORT ANY DISCREPANCIES TO THE POPEYES LOUISIANA KITCHEN REPRESENTATIVE PRIOR TO COMMENCING WORK. THESE DRAWINGS ARE NOT TO BE USED FOR CONSTRUCTION PURPOSES UNLESS INDICATED BY POPEYES LOUISIANA KITCHEN AS "ISSUED FOR CONSTRUCTION".

Professional Seal

DESIGNER NOTES:
DESIGN GUIDELINE ONLY - NOT FOR PERMIT OR CONSTRUCTION

THESE DOCUMENTS MUST BE COMPLETED AND / OR MODIFIED BY A LICENSED ARCHITECT AND ENGINEER TO CONFORM TO ALL APPLICABLE CODES, AND SPECIFIC SITE CONDITIONS. THERE IS NO WARRANTY, WHETHER IMPLIED OR EXPRESSED THAT THESE DOCUMENTS MEET THE APPLICABLE CODE REQUIREMENTS. LIABILITY FOR THE DESIGN AND ANY USE OF THE DOCUMENTS IS THE SOLE RESPONSIBILITY OF THE ARCHITECT AND ENGINEER OF RECORD.

Company Logo




Store Type
US DTGO PROTOTYPE


Location
**PROTOTYPE
DTGO (U.S.)**
CITY, STATE

Drawing Title
ROOF DETAILS

Drawn XX	Checked XX
Scale 1/4"=1'-0"	Date ##.##.####
Project No. XX	Drawing No. A4.1

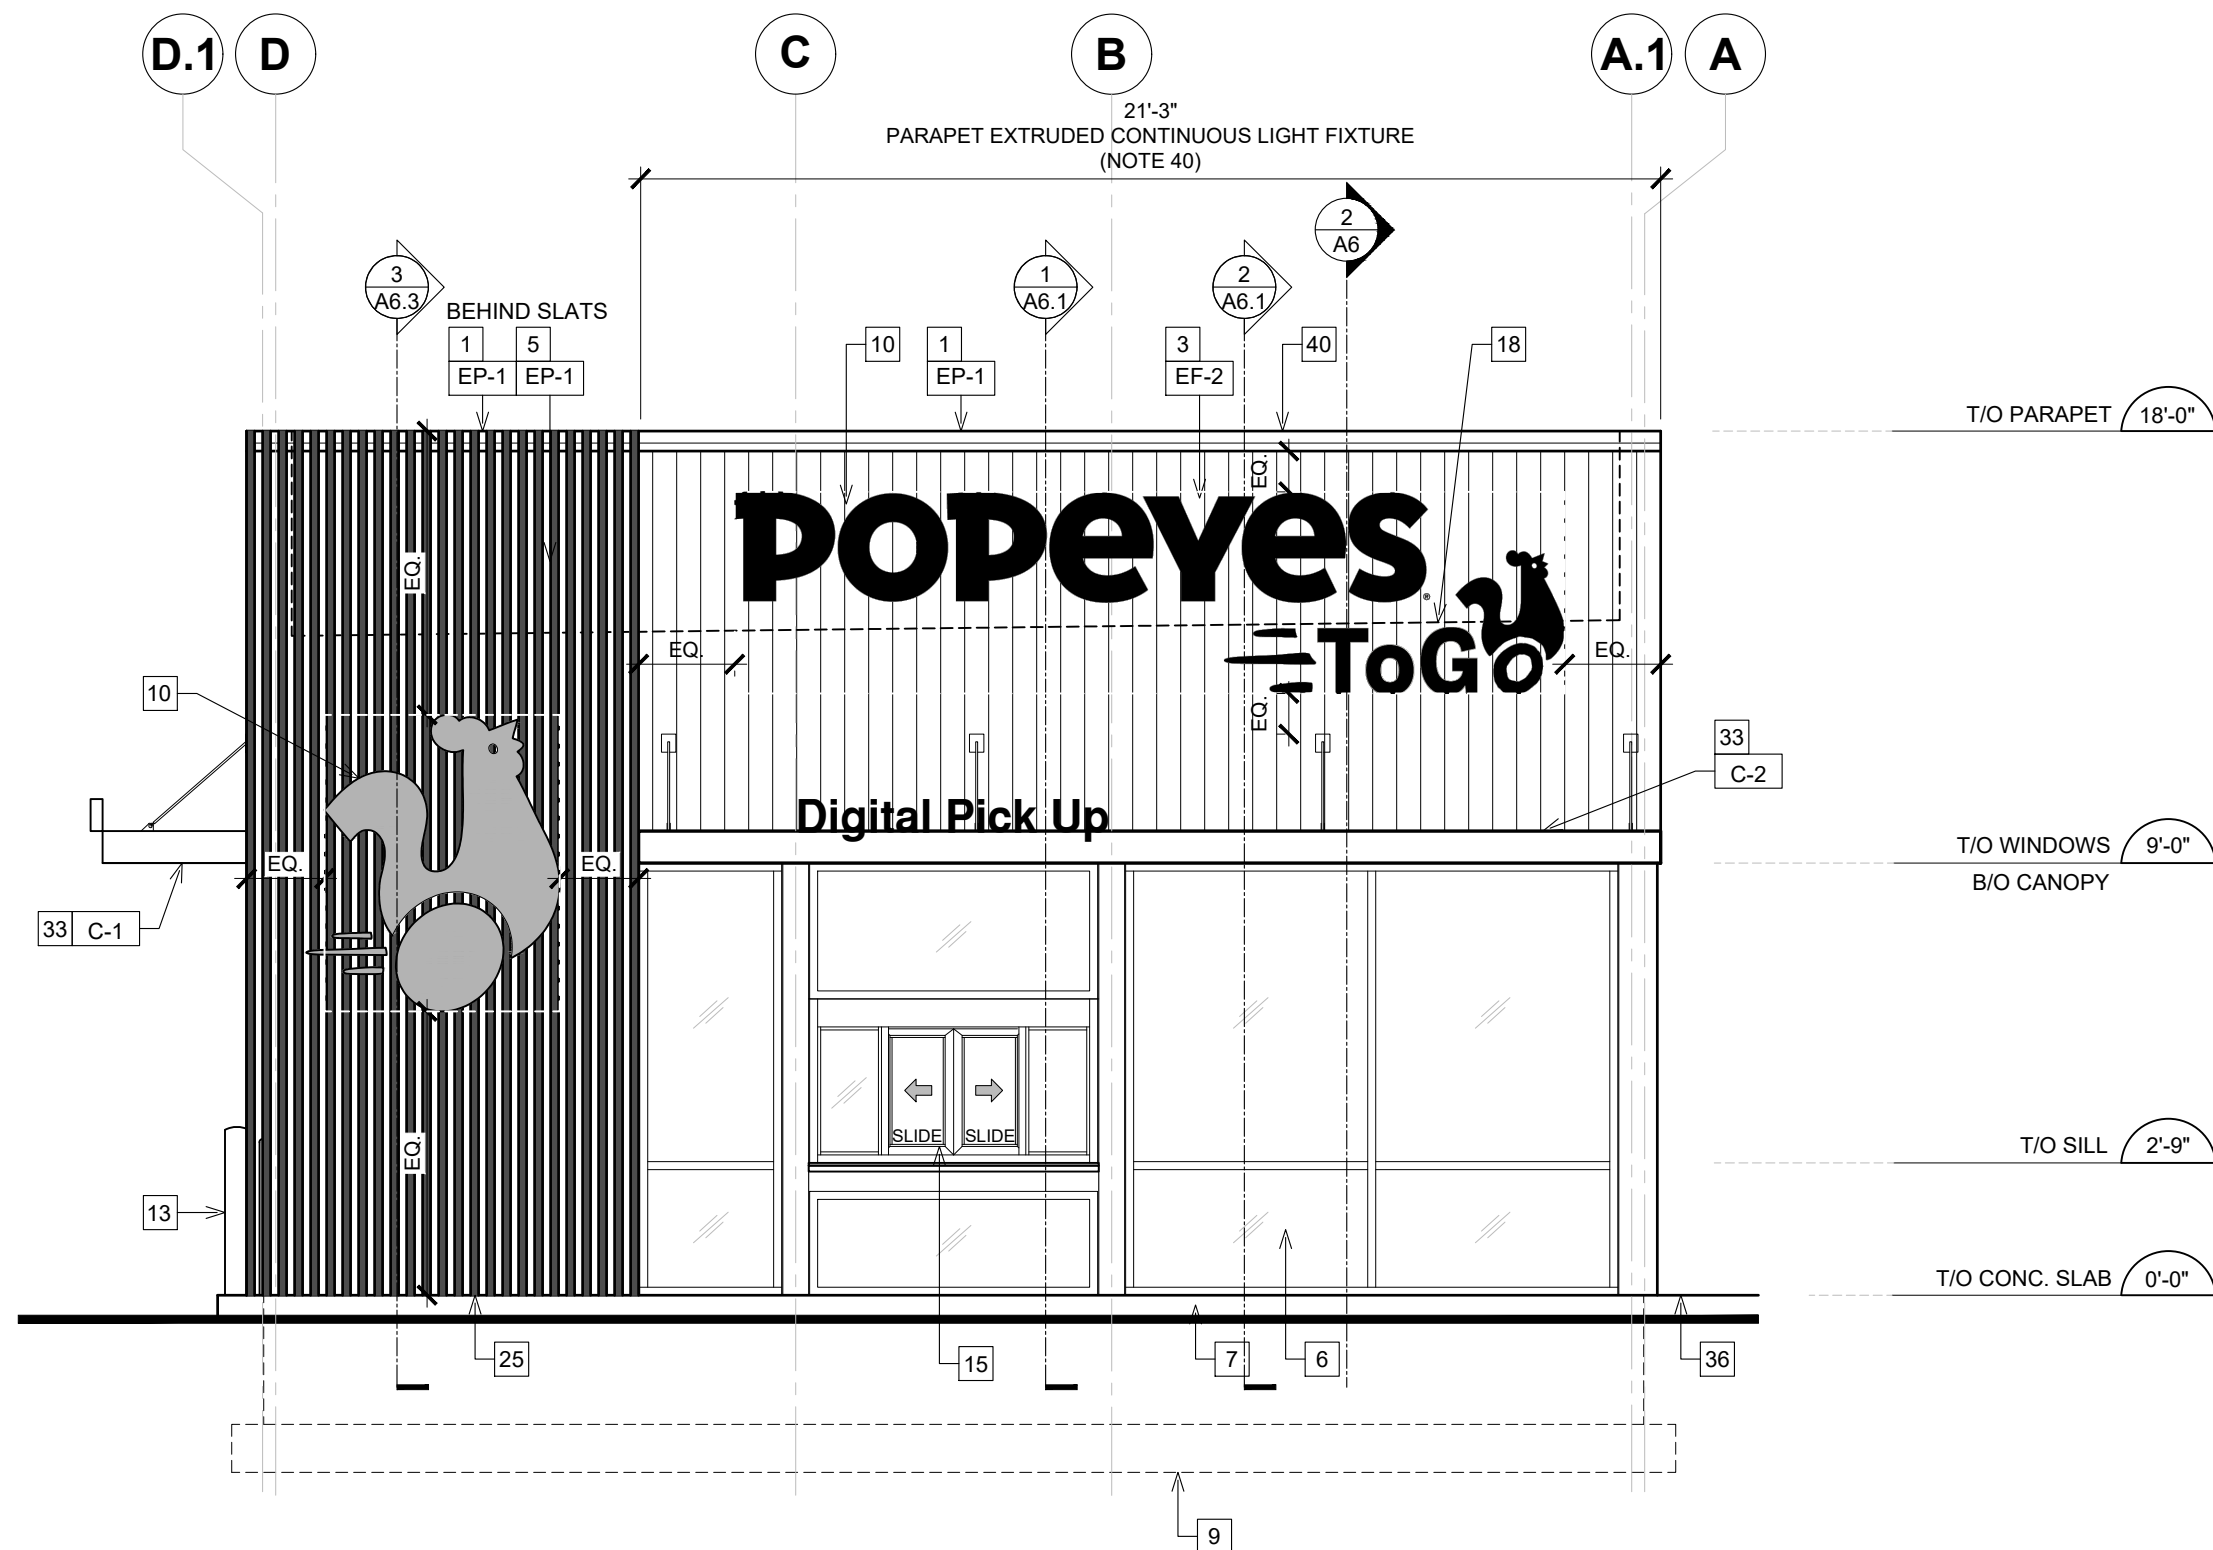

1 PROPOSED FRONT ELEVATION
A5
SCALE: 1/4"=1'-0"

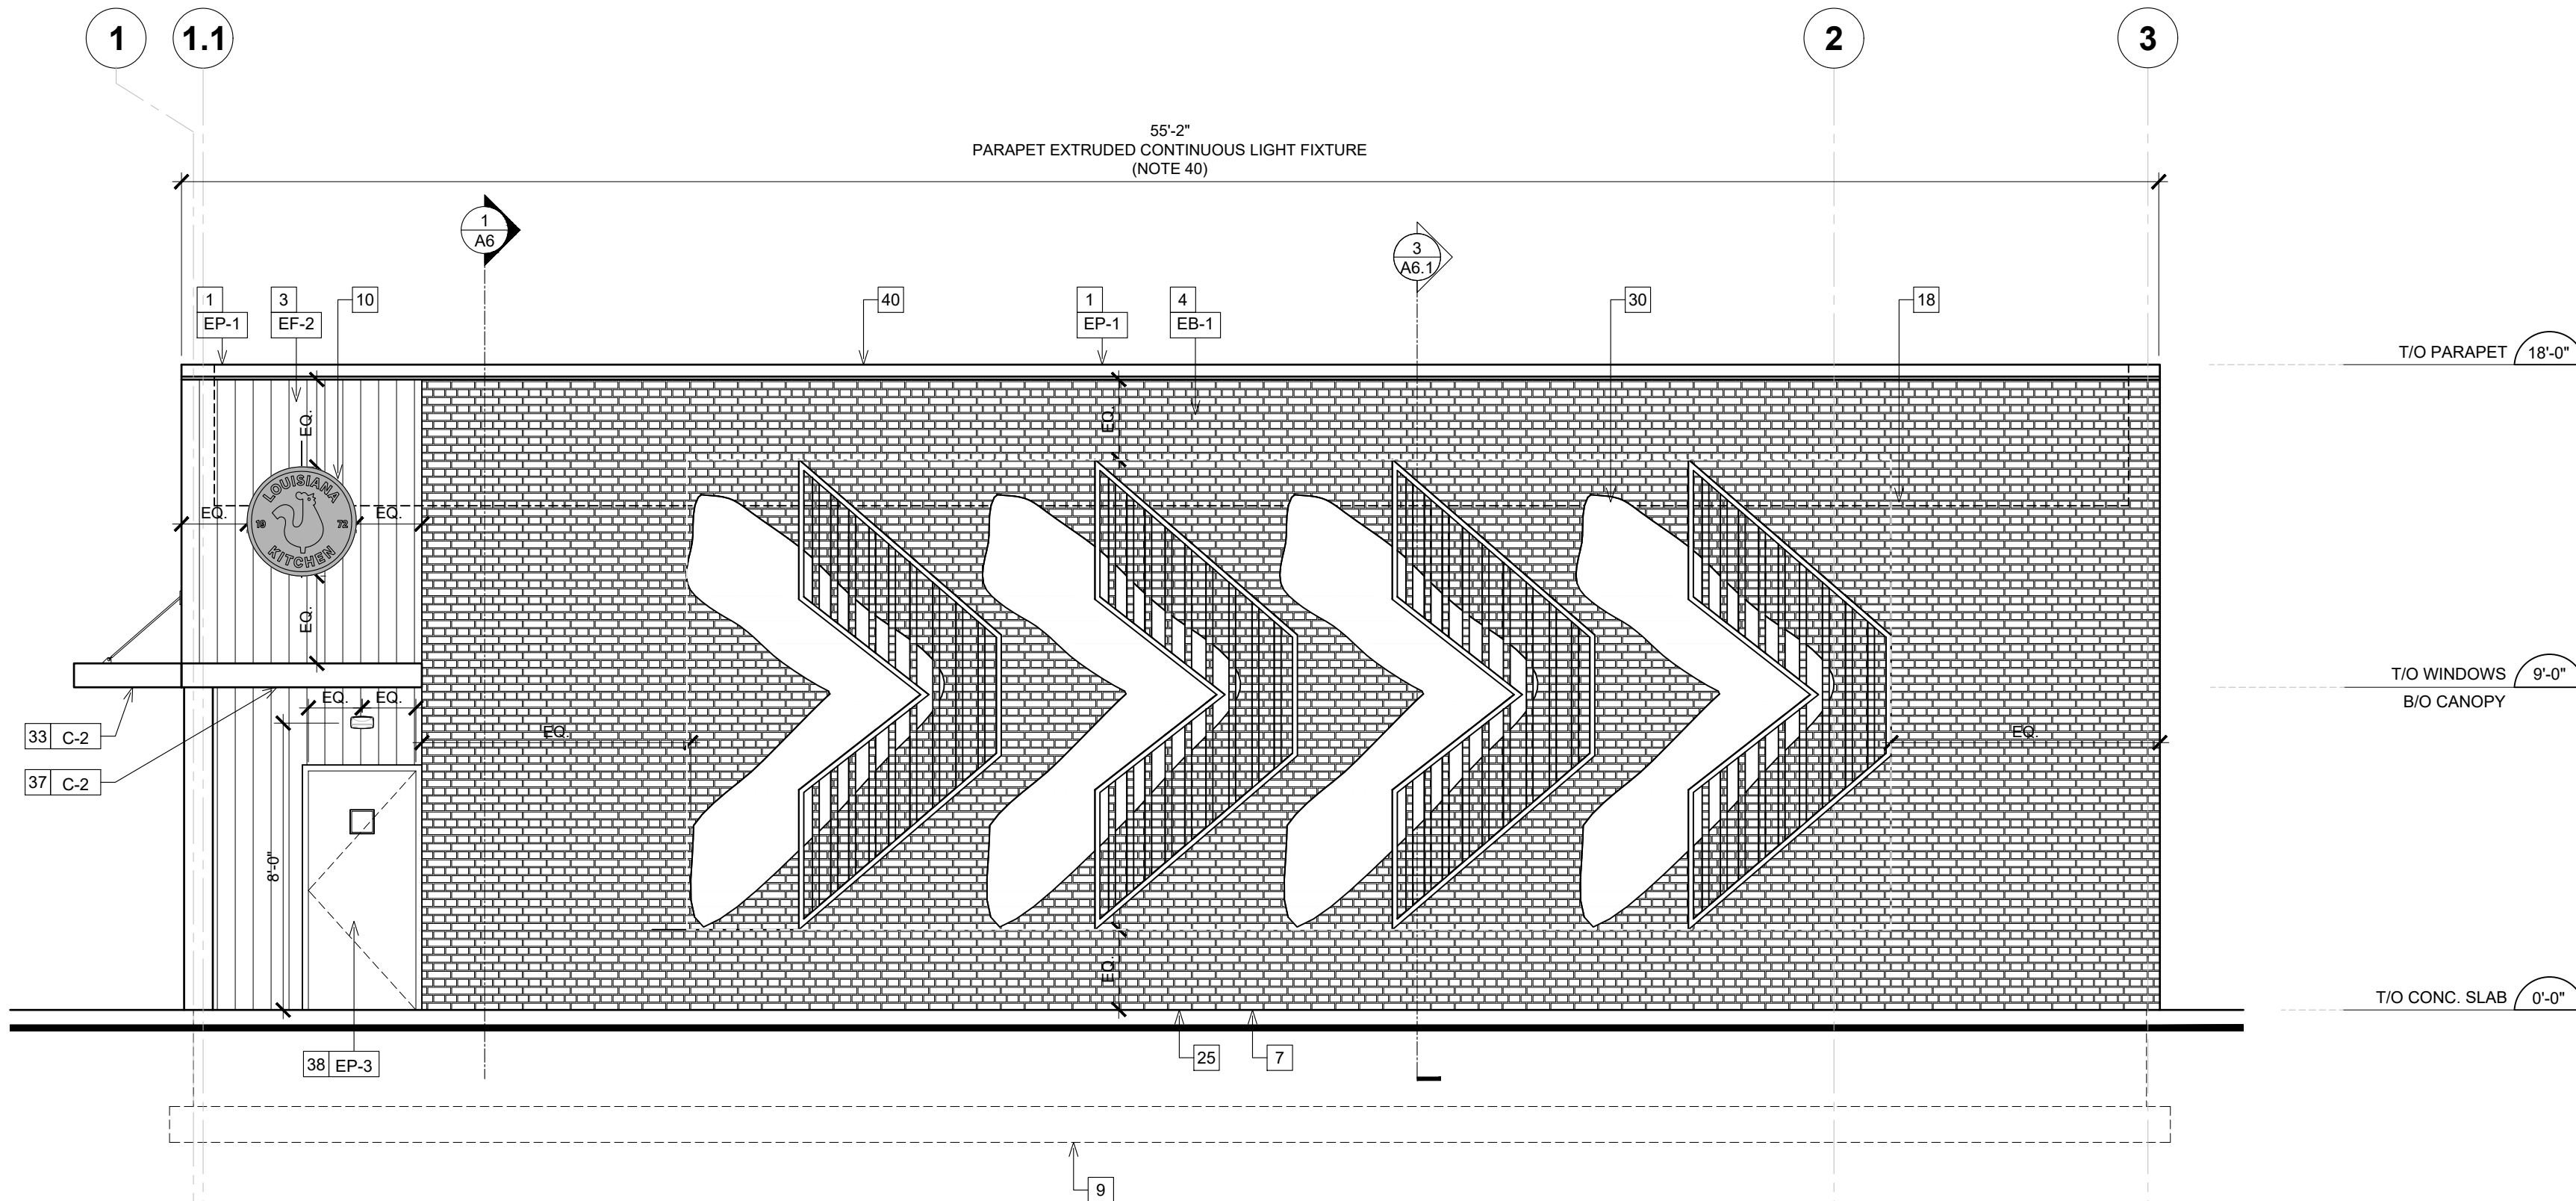

2 PROPOSED SIDE (NON-DT) ELEVATION
A5
SCALE: 1/4"=1'-0"

KEYNOTES (SHEETS A5 & A5.1)

- PRE-FINISHED METAL CAP FLASHING C/W DRIP.
- N/A.
- REFER TO POPEYES PLK FINISH SCHEDULE AND 'FAB' SHEETS. FIBER CEMENT WALL PANEL SYSTEM, NICHHA LATURA V GROOVE, AS PER THE PRE-FABRICATION VENDOR.
- REFER TO POPEYES PLK FINISH SCHEDULE AND 'FAB' SHEETS. BRICK VENEER, NICHHA VINTAGE BRICK OR GLEN-GERY FACEBRICK, AS PER THE PRE-FABRICATION VENDOR. REFER TO POPEYES PLK FINISH SCHEDULE AND 'FAB' SHEETS.
- EIFS, AS PER THE PRE-FABRICATED VENDOR. REFER TO POPEYES PLK FINISH SCHEDULE AND 'FAB' SHEETS.
- PRE-FINISHED 'BLACK ANODIZED' ALUMINUM STOREFRONT SYSTEM WITH INSULATED GLAZING.
- EXPOSED FOUNDATION TO BE PARGED AND FREE OF IMPERFECTIONS.
- GAS METER. REFER TO MECHANICAL DRAWINGS. COORDINATE LOCATION WITH CIVIL DRAWINGS AND LOCAL UTILITY COMPANY.
- REFER TO STRUCTURAL DRAWINGS FOR FOUNDATION WALL AND FOOTING DETAILS.
- INTERNALLY ILLUMINATED BUILDING SIGNAGE PROVIDED AND INSTALLED BY SIGN COMPANY. G.C TO PROVIDE AND INSTALL 3" EXTERIOR GRADE PRESSURE TREATED PLYWOOD BACKING AND ALL FINAL ELECTRICAL CONNECTION. SIGN MANUFACTURER SHALL OBTAIN STRUCTURALLY SEALED DRAWINGS AND SIGNAGE PERMITS FROM THE CITY BASED ON LOCAL REQUIREMENTS. G.C SHALL VERIFY ACTUAL LOCATION & SIZE OF SIGNS WITH SIGN MANUFACTURER'S APPROVED DRAWINGS AND COORDINATE LOCATIONS OF BLOCKING AND UTILITIES. G.C TO COORDINATE WITH SIGN INSTALLER TO USE VHM DRILL BIT WHILE DRILLING FOR ELECTRICAL FEED LINES AND SIGNAGE FASTENERS. ALL ELEMENTS PROVIDED BY SIGNAGE FABRICATOR TO BE REVIEWED AND APPROVED BY POPEYES PRIOR TO PRODUCTION.
- N/A.
- N/A.
- PROVIDE & INSTALL 6" DIAMETER STEEL PIPE BOLLARD TOP AT 4'-6" A.F.F. G.C. TO PAINT "SAFETY YELLOW". REFER TO POPEYES PLK FINISH SCHEDULE.
- ORANGE DRIVE-THRU WINDOW. REFER TO DRIVE-THRU AND WALK-UP WINDOW SCHEDULE ON SHEET A11.
- ORANGE WALK-UP WINDOW. REFER TO DRIVE-THRU AND WALK-UP WINDOW SCHEDULE ON SHEET A11.
- N/A.
- N/A.
- DASHED LINE INDICATES T/O OF ROOF BEHIND PARAPET.
- C/T CABINET AND METER. REFER TO ELECTRICAL DRAWINGS. (NOT SHOWN), TO BE COORDINATED W/ ELECTRICAL DRAWINGS AND UTILITY.
- N/A.
- GENERAL PURPOSE EXTERIOR LIGHTING FIXTURES.
- WALK-IN COOLER/FREEZER FINISH TO BE COMPLETED BY MANUFACTURER.
- METAL RAILING SUPPLIED AND INSTALLED BY G.C (ONLY IF REQUIRED) ARCHITECT TO COORDINATE WITH CIVIL ENGINEER ON THE SITE PLAN. REFER TO DETAIL 2/A8.
- PRE-FINISHED EMERGENCY OVERFLOW SCUPPER. REFER TO DETAIL 2/A4.1.

- ALL WALL BASE FLASHING TO MATCH THE COLOR OF THE ADJACENT FINISH MATERIAL AT THAT AREA.
- HOSE BIB. G.C. TO PAINT. COLOUR TO MATCH ADJACENT STUCCO COORDINATE EXACT LOCATION WITH G.C. REFER TO MECHANICAL DRAWINGS.
- N/A.
- N/A.
- G.C TO PROVIDE CONCRETE CURB ALONG DRIVE-THRU LANE. CURB TO PROJECT 8" FROM FACE OF PANELS AND LENGTH OF CURB IS EXTENT OF FEATURE WALL.
- BUILDING SIGNAGE PROVIDED AND INSTALLED BY SIGN COMPANY. SIGN MANUFACTURER SHALL OBTAIN STRUCTURALLY SEALED DRAWINGS AND SIGNAGE PERMITS FROM THE CITY BASED ON LOCAL REQUIREMENTS. G.C SHALL VERIFY ACTUAL LOCATION & SIZE OF SIGNS WITH SIGN MANUFACTURER'S APPROVED DRAWINGS AND COORDINATE LOCATIONS OF BLOCKING. ALL ELEMENTS PROVIDED BY SIGNAGE FABRICATOR TO BE REVIEWED AND APPROVED BY POPEYES PRIOR TO PRODUCTION.
- REAR EXIT DOOR. REFER TO POPEYES PLK FINISH SCHEDULE.
- NOT USED.
- OPEN BOTTOM ALUMINUM CANOPY WITH DOWNLIGHT LED LIGHT FIXTURE. SUPPLY BY SIGN COMPANY AND INSTALL BY G.C. ALL CANOPIES IN WALL SUPPORT BY G.C. REFER TO STRUCTURAL DRAWINGS.
- N/A.
- N/A.
- CONCRETE SIDEWALK (BY G.C). REFER TO SITE PLAN.
- N/A.
- NEW EXTERIOR DOOR. REFER TO POPEYES PLK FINISH SCHEDULE.
- N/A.
- PARAPET PERIMETER EXTRUDED CONTINUOUS DOWNLIGHT LIGHT FIXTURE. TO BE ATTACHED TO BUILDING PARAPET CORING, AS PER MANUFACTURER DIRECTIONS. FIXTURE COLOR TO MATCH ADJACENT PARAPET COLOR. REFER TO POPEYES MASTER LIGHT FIXTURE SCHEDULE. PARAPET LIGHTING MUST BE SUPPLIED BY POPEYES'S APPROVED DECOR VENDOR.
- OVERFLOW DOWNSPOUT NOZZLE. REF TO PLUMBING.

GENERAL NOTES

- SEALANT / CAULKING AROUND DOOR / WINDOW FRAMES. COLOR: TO MATCH WINDOW / DOOR FRAMES.
- THE CONTRACTOR SHALL BECOME FAMILIAR WITH AND FOLLOW ALL DRAWINGS AND SPECIFICATIONS.
- EXTERIOR ELEVATIONS MUST MATCH DESIGN TEAM APPROVED ELEVATION DRAWINGS. ANY DEVIATION FROM THE PROTOTYPE DRAWINGS OR THE APPROVED ELEVATION DRAWINGS MUST HAVE A SUBMITTED AND APPROVED EXCEPTION REQUEST FORM FROM POPEYES DESIGN TEAM.
- ALL PARAPETS SHALL BE PAINTED ACCORDING TO THE FACADE COLOR.
- ENSURE TO REFERENCE LATEST FINISH SCHEDULE IN THE DESIGN PORTAL ON A REGULAR BASIS.
- ALL CANOPIES TO BE TEAL, EXCEPT AT THE DRIVE-THRU WINDOW.
- BUILDING EXTERIOR AS PER PRE-FABRICATING VENDOR SYSTEM ASSEMBLY. REFER TO PRE-FAB SHELL DRAWINGS FOR SCOPE AND WALL CONSTRUCTION. NOTE: PRE-FAB WALL CONSTRUCTION LIMITS: INTERIOR SIDE FACE STUDS TO OUTSIDE FACE OF EXTERIOR FINISH.

SYMBOL LEGEND

- | | |
|-----|--|
| 1 | NOTE REFERENCE. REFER TO ELEVATION NOTES |
| FNB | FINISH TYPE |

ISSUE TABLE

No.	Date (mm/dd/yy)	Description
01	09-26-25	DTGO PROTOTYPE DOCUMENTS

REVISIONS

No.	Date	Description

DRAWINGS REVISED AS PER DESIGN BULLETIN

No.	Date	Description

THIS DRAWING IS OWNED BY OR LICENSED FOR USE BY POPEYES LOUISIANA KITCHEN (OR ITS AFFILIATED OR RELATED COMPANIES) AND MAY NOT BE REPRODUCED, USED, DOWNLOADED, DISSEMINATED, PUBLISHED, OR TRANSFERRED IN ANY FORM OR BY ANY MEANS, EXCEPT WITH THE PRIOR WRITTEN CONSENT OF POPEYES LOUISIANA KITCHEN. COPYRIGHT INFRINGEMENT IS A VIOLATION OF FEDERAL LAW SUBJECT TO CRIMINAL AND CIVIL PENALTIES.

THE CONTRACTOR IS TO VERIFY ALL DIMENSIONS AND CONDITIONS ON THE PROJECT AND TO REPORT ANY DISCREPANCIES TO THE POPEYES LOUISIANA KITCHEN REPRESENTATIVE PRIOR TO COMMENCING WORK. THESE DRAWINGS ARE NOT TO BE USED FOR CONSTRUCTION PURPOSES UNLESS INDICATED BY POPEYES LOUISIANA KITCHEN AS "ISSUED FOR CONSTRUCTION".

Professional Seal

DESIGNER NOTES:
DESIGN GUIDELINE ONLY - NOT FOR PERMIT OR CONSTRUCTION

THESE DOCUMENTS MUST BE COMPLETED AND / OR MODIFIED BY A LICENSED ARCHITECT AND ENGINEER TO CONFORM TO ALL APPLICABLE CODES, AND SPECIFIC SITE CONDITIONS. THERE IS NO WARRANTY, WHETHER IMPLIED OR EXPRESSED THAT THESE DOCUMENTS MEET THE APPLICABLE CODE REQUIREMENTS. LIABILITY FOR THE DESIGN AND ANY USE OF THE DOCUMENTS IS THE SOLE RESPONSIBILITY OF THE ARCHITECT AND ENGINEER OF RECORD.

Company Logo

Project



POPEYES.

Store Type
US DTGO PROTOTYPE

Location

PROTOTYPE
DTGO (U.S.)

CITY, STATE

Drawing Title

EXTERIOR
ELEVATIONS

Drawn

XX

Checked

XX

Scale

1/4"=1'-0"

Date


##.##.####

Project No.


XX

Drawing No.

A5

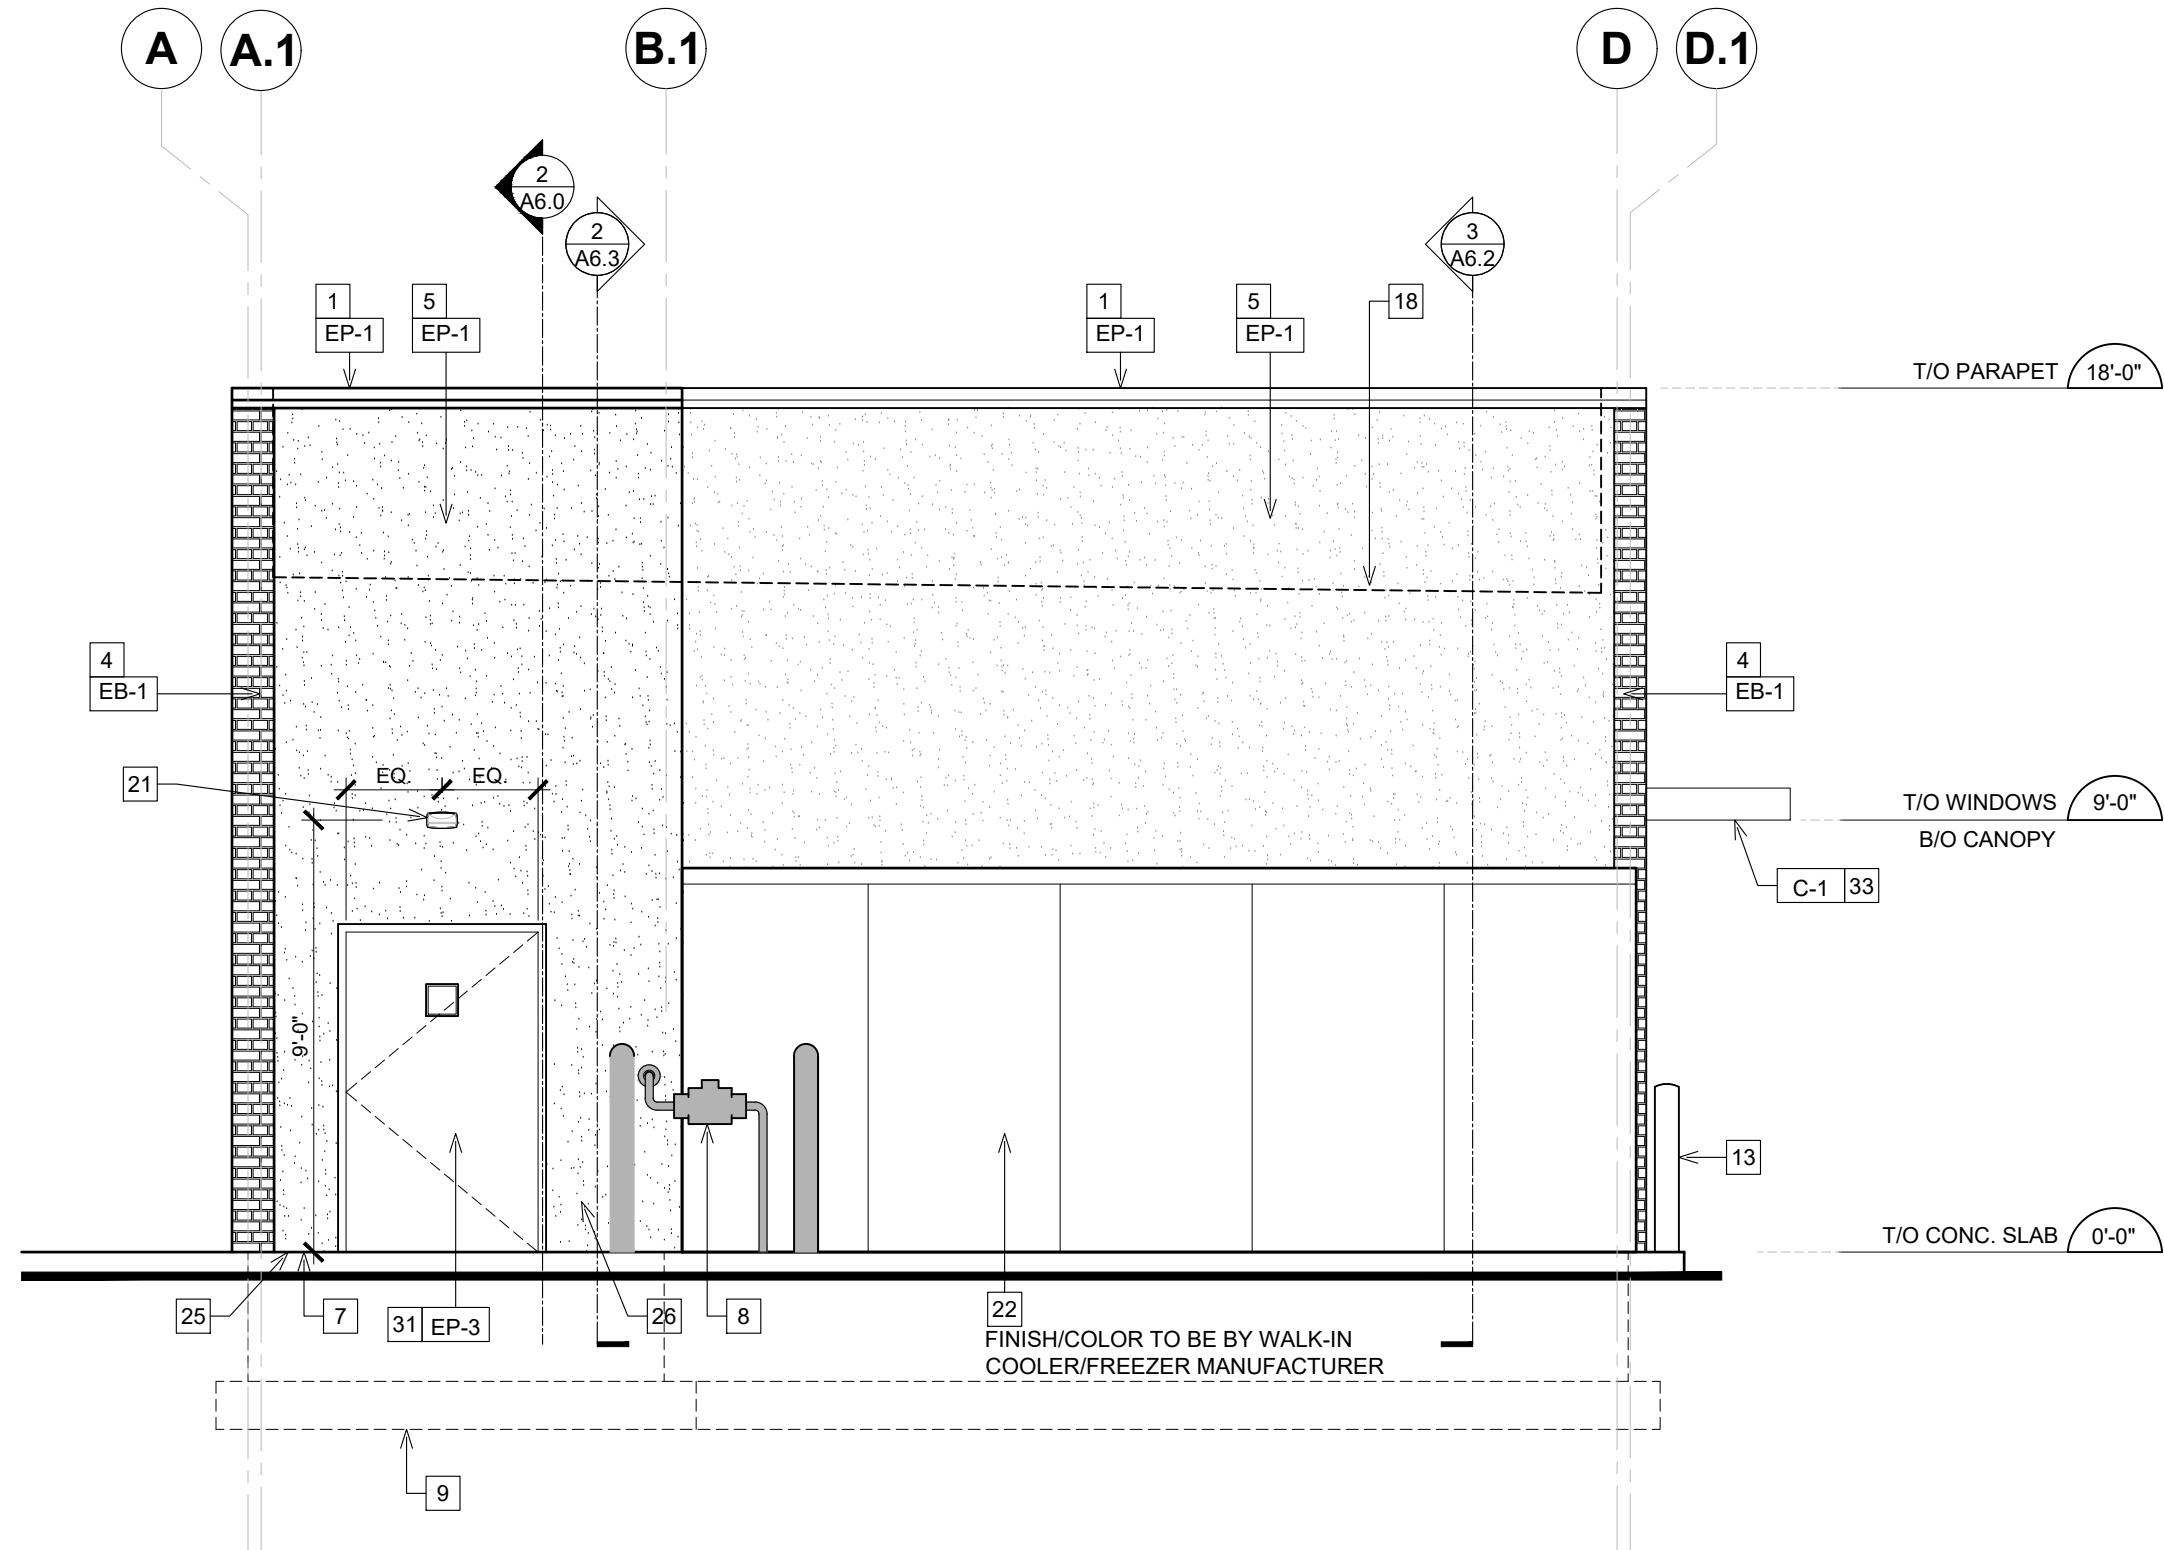

1
A5.1 **PROPOSED REAR ELEVATION**
SCALE: 1/4"=1'-0"

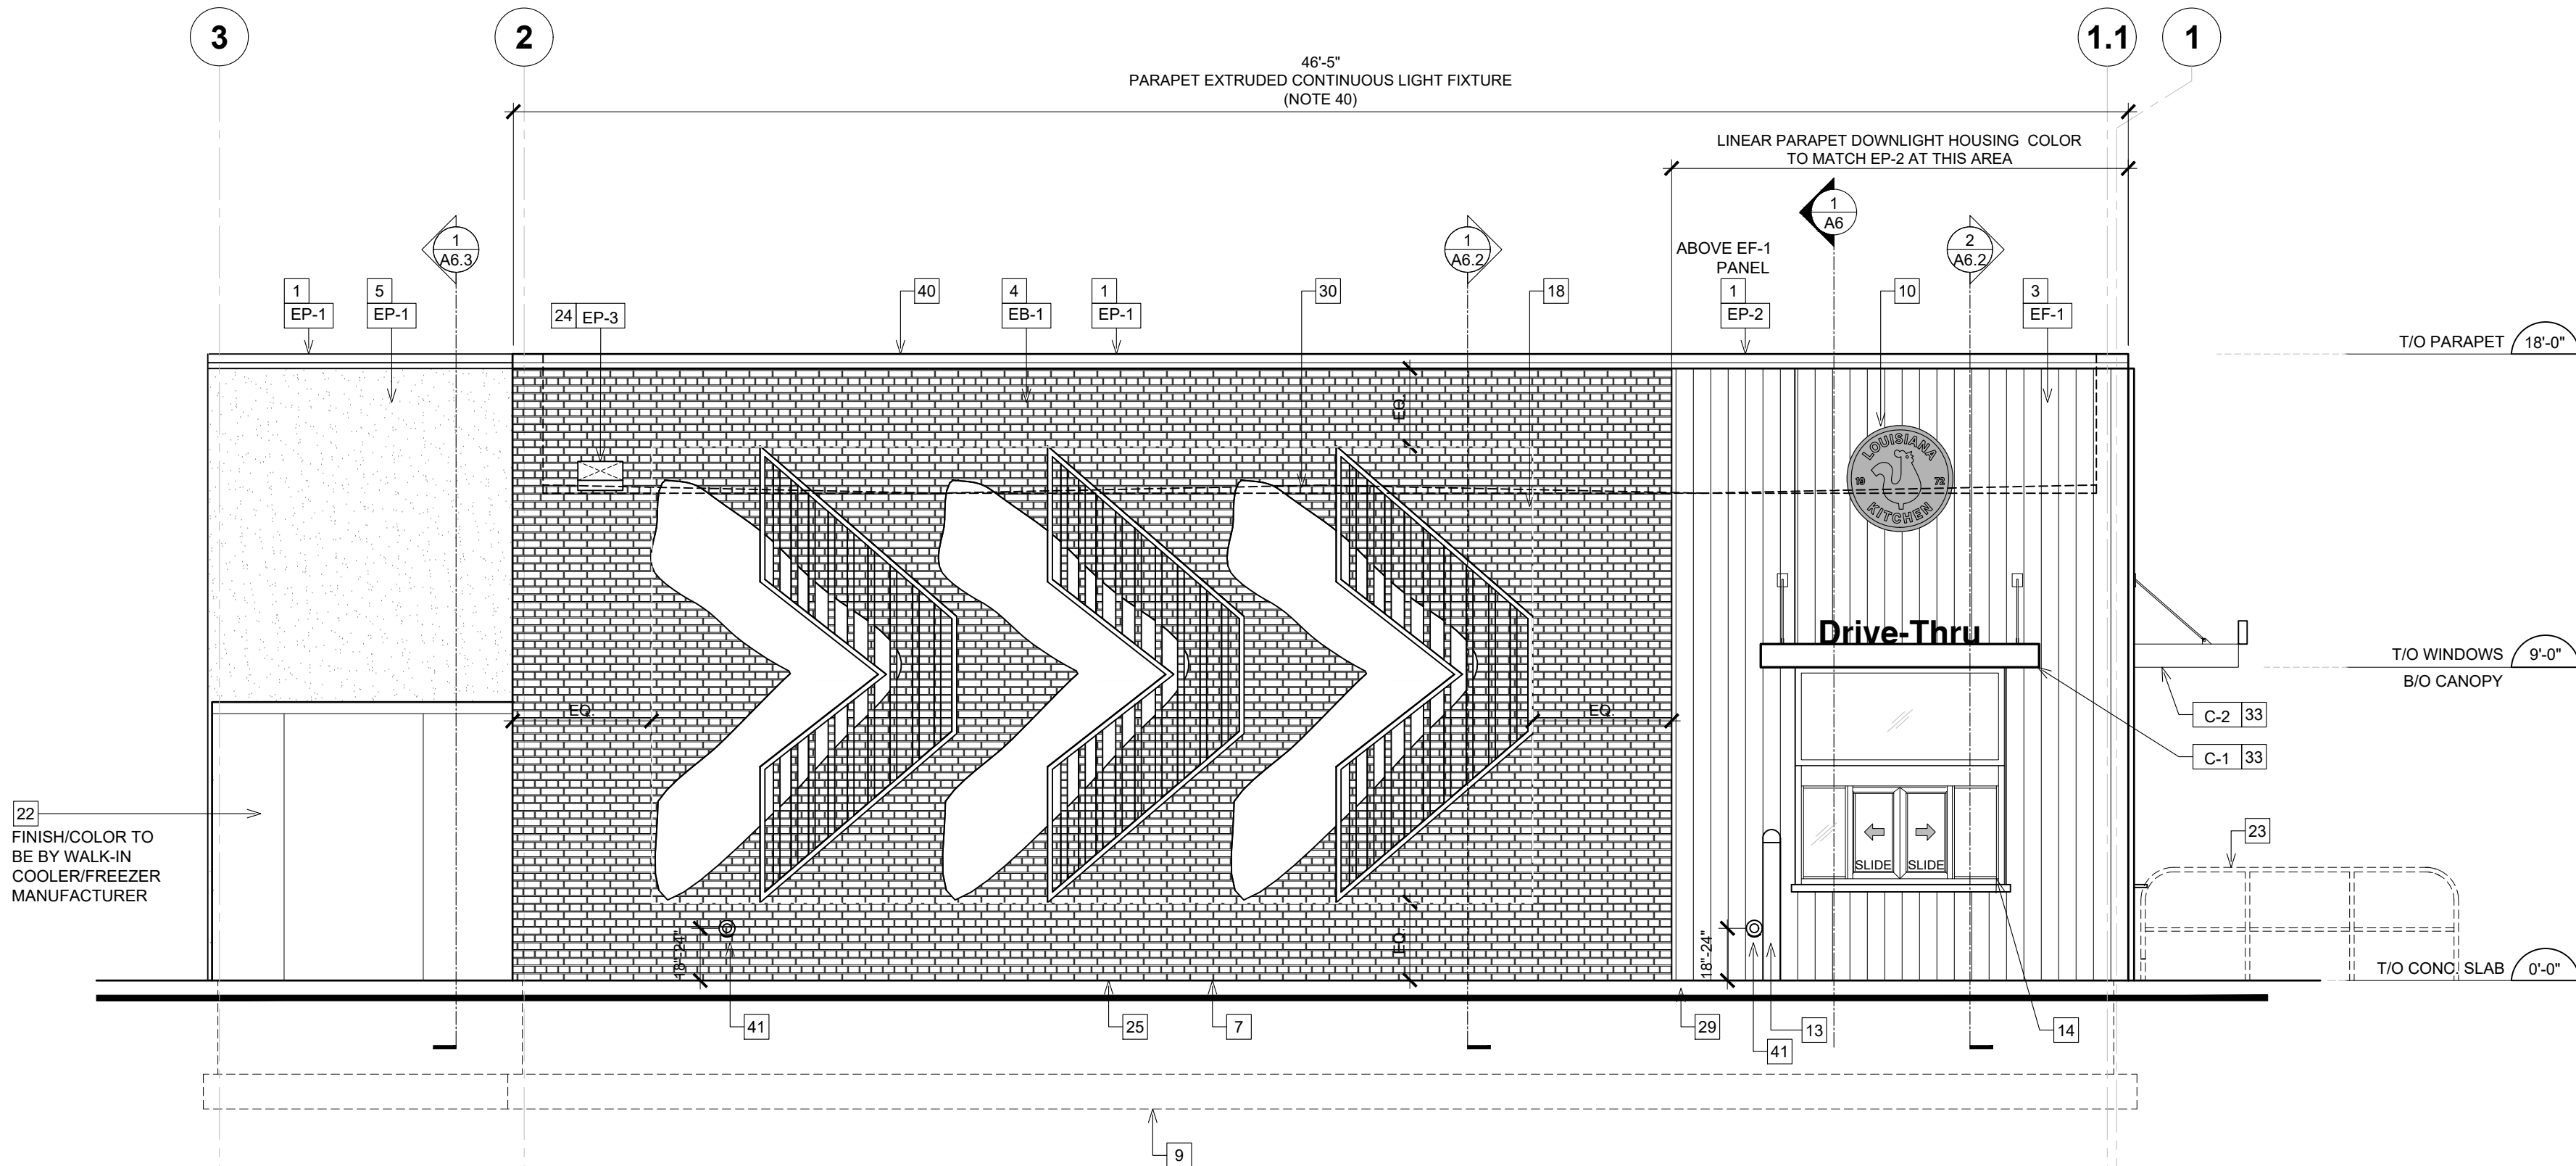

2
A5.1 **PROPOSED DT ELEVATION**
SCALE: 1/4"=1'-0"

KEYNOTES (SHEETS A5 & A5.1)

- PRE-FINISHED METAL CAP FLASHING C/W DRIP.
- N/A.
- REFER TO POPEYES PLK FINISH SCHEDULE AND 'FAB' SHEETS. FIBER CEMENT WALL PANEL SYSTEM, NICHHA LATURA V GROOVE, AS PER THE PRE-FABRICATION VENDOR.
- REFER TO POPEYES PLK FINISH SCHEDULE AND 'FAB' SHEETS. BRICK VENEER, NICHHA VINTAGE BRICK OR GLEN-GERY FACEBRICK, AS PER THE PRE-FABRICATION VENDOR. REFER TO POPEYES PLK FINISH SCHEDULE AND 'FAB' SHEETS.
- EIFS, AS PER THE PRE-FABRICATED VENDOR. REFER TO POPEYES PLK FINISH SCHEDULE AND 'FAB' SHEETS.
- PRE-FINISHED 'BLACK ANODIZED' ALUMINUM STOREFRONT SYSTEM WITH INSULATED GLAZING.
- EXPOSED FOUNDATION TO BE PARGED AND FREE OF IMPERFECTIONS.
- GAS METER. REFER TO MECHANICAL DRAWINGS. COORDINATE LOCATION WITH CIVIL DRAWINGS AND LOCAL UTILITY COMPANY.
- REFER TO STRUCTURAL DRAWINGS FOR FOUNDATION WALL AND FOOTING DETAILS.
- INTERNALLY ILLUMINATED BUILDING SIGNAGE PROVIDED AND INSTALLED BY SIGN COMPANY. G.C TO PROVIDE AND INSTALL 3" EXTERIOR GRADE PRESSURE TREATED PLYWOOD BACKING AND ALL FINAL ELECTRICAL CONNECTION. SIGN MANUFACTURER SHALL OBTAIN STRUCTURALLY SEALED DRAWINGS AND SIGNAGE PERMITS FROM THE CITY BASED ON LOCAL REQUIREMENTS. G.C SHALL VERIFY ACTUAL LOCATION & SIZE OF SIGNS WITH SIGN MANUFACTURER'S APPROVED DRAWINGS AND COORDINATE LOCATIONS OF BLOCKING AND UTILITIES. G.C TO COORDINATE WITH SIGN INSTALLER TO USE VHM DRILL BIT WHILE DRILLING FOR ELECTRICAL FEED LINES AND SIGNAGE FASTENERS. ALL ELEMENTS PROVIDED BY SIGNAGE FABRICATOR TO BE REVIEWED AND APPROVED BY POPEYES PRIOR TO PRODUCTION.
- N/A.
- N/A.
- PROVIDE & INSTALL 6" DIAMETER STEEL PIPE BOLLARD TOP AT 4'-6" A.F.F. G.C. TO PAINT "SAFETY YELLOW". REFER TO POPEYES PLK FINISH SCHEDULE.
- ORANGE DRIVE-THRU WINDOW. REFER TO DRIVE-THRU AND WALK-UP WINDOW SCHEDULE ON SHEET A11.
- ORANGE WALK-UP WINDOW. REFER TO DRIVE-THRU AND WALK-UP WINDOW SCHEDULE ON SHEET A11.
- N/A.
- N/A.
- DASHED LINE INDICATES T/O OF ROOF BEHIND PARAPET.
- C/T CABINET AND METER. REFER TO ELECTRICAL DRAWINGS. (NOT SHOWN), TO BE COORDINATED W/ ELECTRICAL DRAWINGS AND UTILITY.
- N/A.
- GENERAL PURPOSE EXTERIOR LIGHTING FIXTURES.
- WALK-IN COOLER/FREEZER FINISH TO BE COMPLETED BY MANUFACTURER.
- METAL RAILING SUPPLIED AND INSTALLED BY G.C (ONLY IF REQUIRED) ARCHITECT TO COORDINATE WITH CIVIL ENGINEER ON THE SITE PLAN. REFER TO DETAIL 2/A8.
- PRE-FINISHED EMERGENCY OVERFLOW SCUPPER. REFER TO DETAIL 2/A4.1.

- ALL WALL BASE FLASHING TO MATCH THE COLOR OF THE ADJACENT FINISH MATERIAL AT THAT AREA.
- HOSE BIB. G.C. TO PAINT. COLOUR TO MATCH ADJACENT STUCCO COORDINATE EXACT LOCATION WITH G.C. REFER TO MECHANICAL DRAWINGS.
- N/A.
- N/A.
- G.C TO PROVIDE CONCRETE CURB ALONG DRIVE-THRU LANE. CURB TO PROJECT 8" FROM FACE OF PANELS AND LENGTH OF CURB IS EXTENT OF FEATURE WALL.
- BUILDING SIGNAGE PROVIDED AND INSTALLED BY SIGN COMPANY. SIGN MANUFACTURER SHALL OBTAIN STRUCTURALLY SEALED DRAWINGS AND SIGNAGE PERMITS FROM THE CITY BASED ON LOCAL REQUIREMENTS. G.C SHALL VERIFY ACTUAL LOCATION & SIZE OF SIGNS WITH SIGN MANUFACTURER'S APPROVED DRAWINGS AND COORDINATE LOCATIONS OF BLOCKING. ALL ELEMENTS PROVIDED BY SIGNAGE FABRICATOR TO BE REVIEWED AND APPROVED BY POPEYES PRIOR TO PRODUCTION.
- REAR EXIT DOOR. REFER TO POPEYES PLK FINISH SCHEDULE.
- NOT USED.
- OPEN BOTTOM ALUMINUM CANOPY WITH DOWNLIGHT LED LIGHT FIXTURE. SUPPLY BY SIGN COMPANY AND INSTALL BY G.C. ALL CANOPIES IN WALL SUPPORT BY G.C. REFER TO STRUCTURAL DRAWINGS.
- N/A.
- N/A.
- CONCRETE SIDEWALK (BY G.C). REFER TO SITE PLAN.
- N/A.
- NEW EXTERIOR DOOR. REFER TO POPEYES PLK FINISH SCHEDULE.
- N/A.
- PARAPET PERIMETER EXTRUDED CONTINUOUS DOWNLIGHT LIGHT FIXTURE. TO BE ATTACHED TO BUILDING PARAPET CORING, AS PER MANUFACTURER DIRECTIONS. FIXTURE COLOR TO MATCH ADJACENT PARAPET COLOR. REFER TO POPEYES MASTER LIGHT FIXTURE SCHEDULE. PARAPET LIGHTING MUST BE SUPPLIED BY POPEYE'S APPROVED DECOR VENDOR.
- OVERFLOW DOWNSPOUT NOZZLE. REF TO PLUMBING.

GENERAL NOTES

- SEALANT / CAULKING AROUND DOOR / WINDOW FRAMES. COLOR: TO MATCH WINDOW / DOOR FRAMES.
- THE CONTRACTOR SHALL BECOME FAMILIAR WITH AND FOLLOW ALL DRAWINGS AND SPECIFICATIONS.
- EXTERIOR ELEVATIONS MUST MATCH DESIGN TEAM APPROVED ELEVATION DRAWINGS. ANY DEVIATION FROM THE PROTOTYPE DRAWINGS OR THE APPROVED ELEVATION DRAWINGS MUST HAVE A SUBMITTED AND APPROVED EXCEPTION REQUEST FORM FROM POPEYES DESIGN TEAM.
- ALL PARAPETS SHALL BE PAINTED ACCORDING TO THE FACADE COLOR.
- ENSURE TO REFERENCE LATEST FINISH SCHEDULE IN THE DESIGN PORTAL ON A REGULAR BASIS.
- ALL CANOPIES TO BE TEAL, EXCEPT AT THE DRIVE-THRU WINDOW.
- BUILDING EXTERIOR AS PER PRE-FABRICATING VENDOR SYSTEM ASSEMBLY. REFER TO PRE-FAB SHELL DRAWINGS FOR SCOPE AND WALL CONSTRUCTION. NOTE: PRE-FAB WALL CONSTRUCTION LIMITS: INTERIOR SIDE FACE STUDS TO OUTSIDE FACE OF EXTERIOR FINISH.

SYMBOL LEGEND

- | | |
|-----|--|
| 1 | NOTE REFERENCE. REFER TO ELEVATION NOTES |
| FNB | FINISH TYPE |

ISSUE TABLE

No.	Date (mm/dd/yy)	Description
01	09-26-25	DTGO PROTOTYPE DOCUMENTS

REVISIONS

No.	Date	Description

DRAWINGS REVISED AS PER DESIGN BULLETIN

No.	Date	Description

THIS DRAWING IS OWNED BY OR LICENSED FOR USE BY POPEYES LOUISIANA KITCHEN (OR ITS AFFILIATED OR RELATED COMPANIES) AND MAY NOT BE REPRODUCED, USED, DOWNLOADED, DISSEMINATED, PUBLISHED, OR TRANSFERRED IN ANY FORM OR BY ANY MEANS, EXCEPT WITH THE PRIOR WRITTEN CONSENT OF POPEYES LOUISIANA KITCHEN. COPYRIGHT INFRINGEMENT IS A VIOLATION OF FEDERAL LAW SUBJECT TO CRIMINAL AND CIVIL PENALTIES.

THE CONTRACTOR IS TO VERIFY ALL DIMENSIONS AND CONDITIONS ON THE PROJECT AND TO REPORT ANY DISCREPANCIES TO THE POPEYES LOUISIANA KITCHEN REPRESENTATIVE PRIOR TO COMMENCING WORK. THESE DRAWINGS ARE NOT TO BE USED FOR CONSTRUCTION PURPOSES UNLESS INDICATED BY POPEYES LOUISIANA KITCHEN AS "ISSUED FOR CONSTRUCTION".

Professional Seal

DESIGNER NOTES:
DESIGN GUIDELINE ONLY - NOT FOR PERMIT OR CONSTRUCTION

THESE DOCUMENTS MUST BE COMPLETED AND / OR MODIFIED BY A LICENSED ARCHITECT AND ENGINEER TO CONFORM TO ALL APPLICABLE CODES, AND SPECIFIC SITE CONDITIONS. THERE IS NO WARRANTY, WHETHER IMPLIED OR EXPRESSED, THAT THESE DOCUMENTS MEET THE APPLICABLE CODE REQUIREMENTS. LIABILITY FOR THE DESIGN AND ANY USE OF THE DOCUMENTS IS THE SOLE RESPONSIBILITY OF THE ARCHITECT AND ENGINEER OF RECORD.

Company Logo

Project



POPEYES.

Store Type
US DTGO PROTOTYPE

Location

**PROTOTYPE
DTGO (U.S.)**

CITY, STATE

Drawing Title

**EXTERIOR
ELEVATIONS**

Drawn

XX

Checked

XX

Scale

1/4"=1'-0"

Date


##.##.####

Project No.


XX

Drawing No.

A5.1

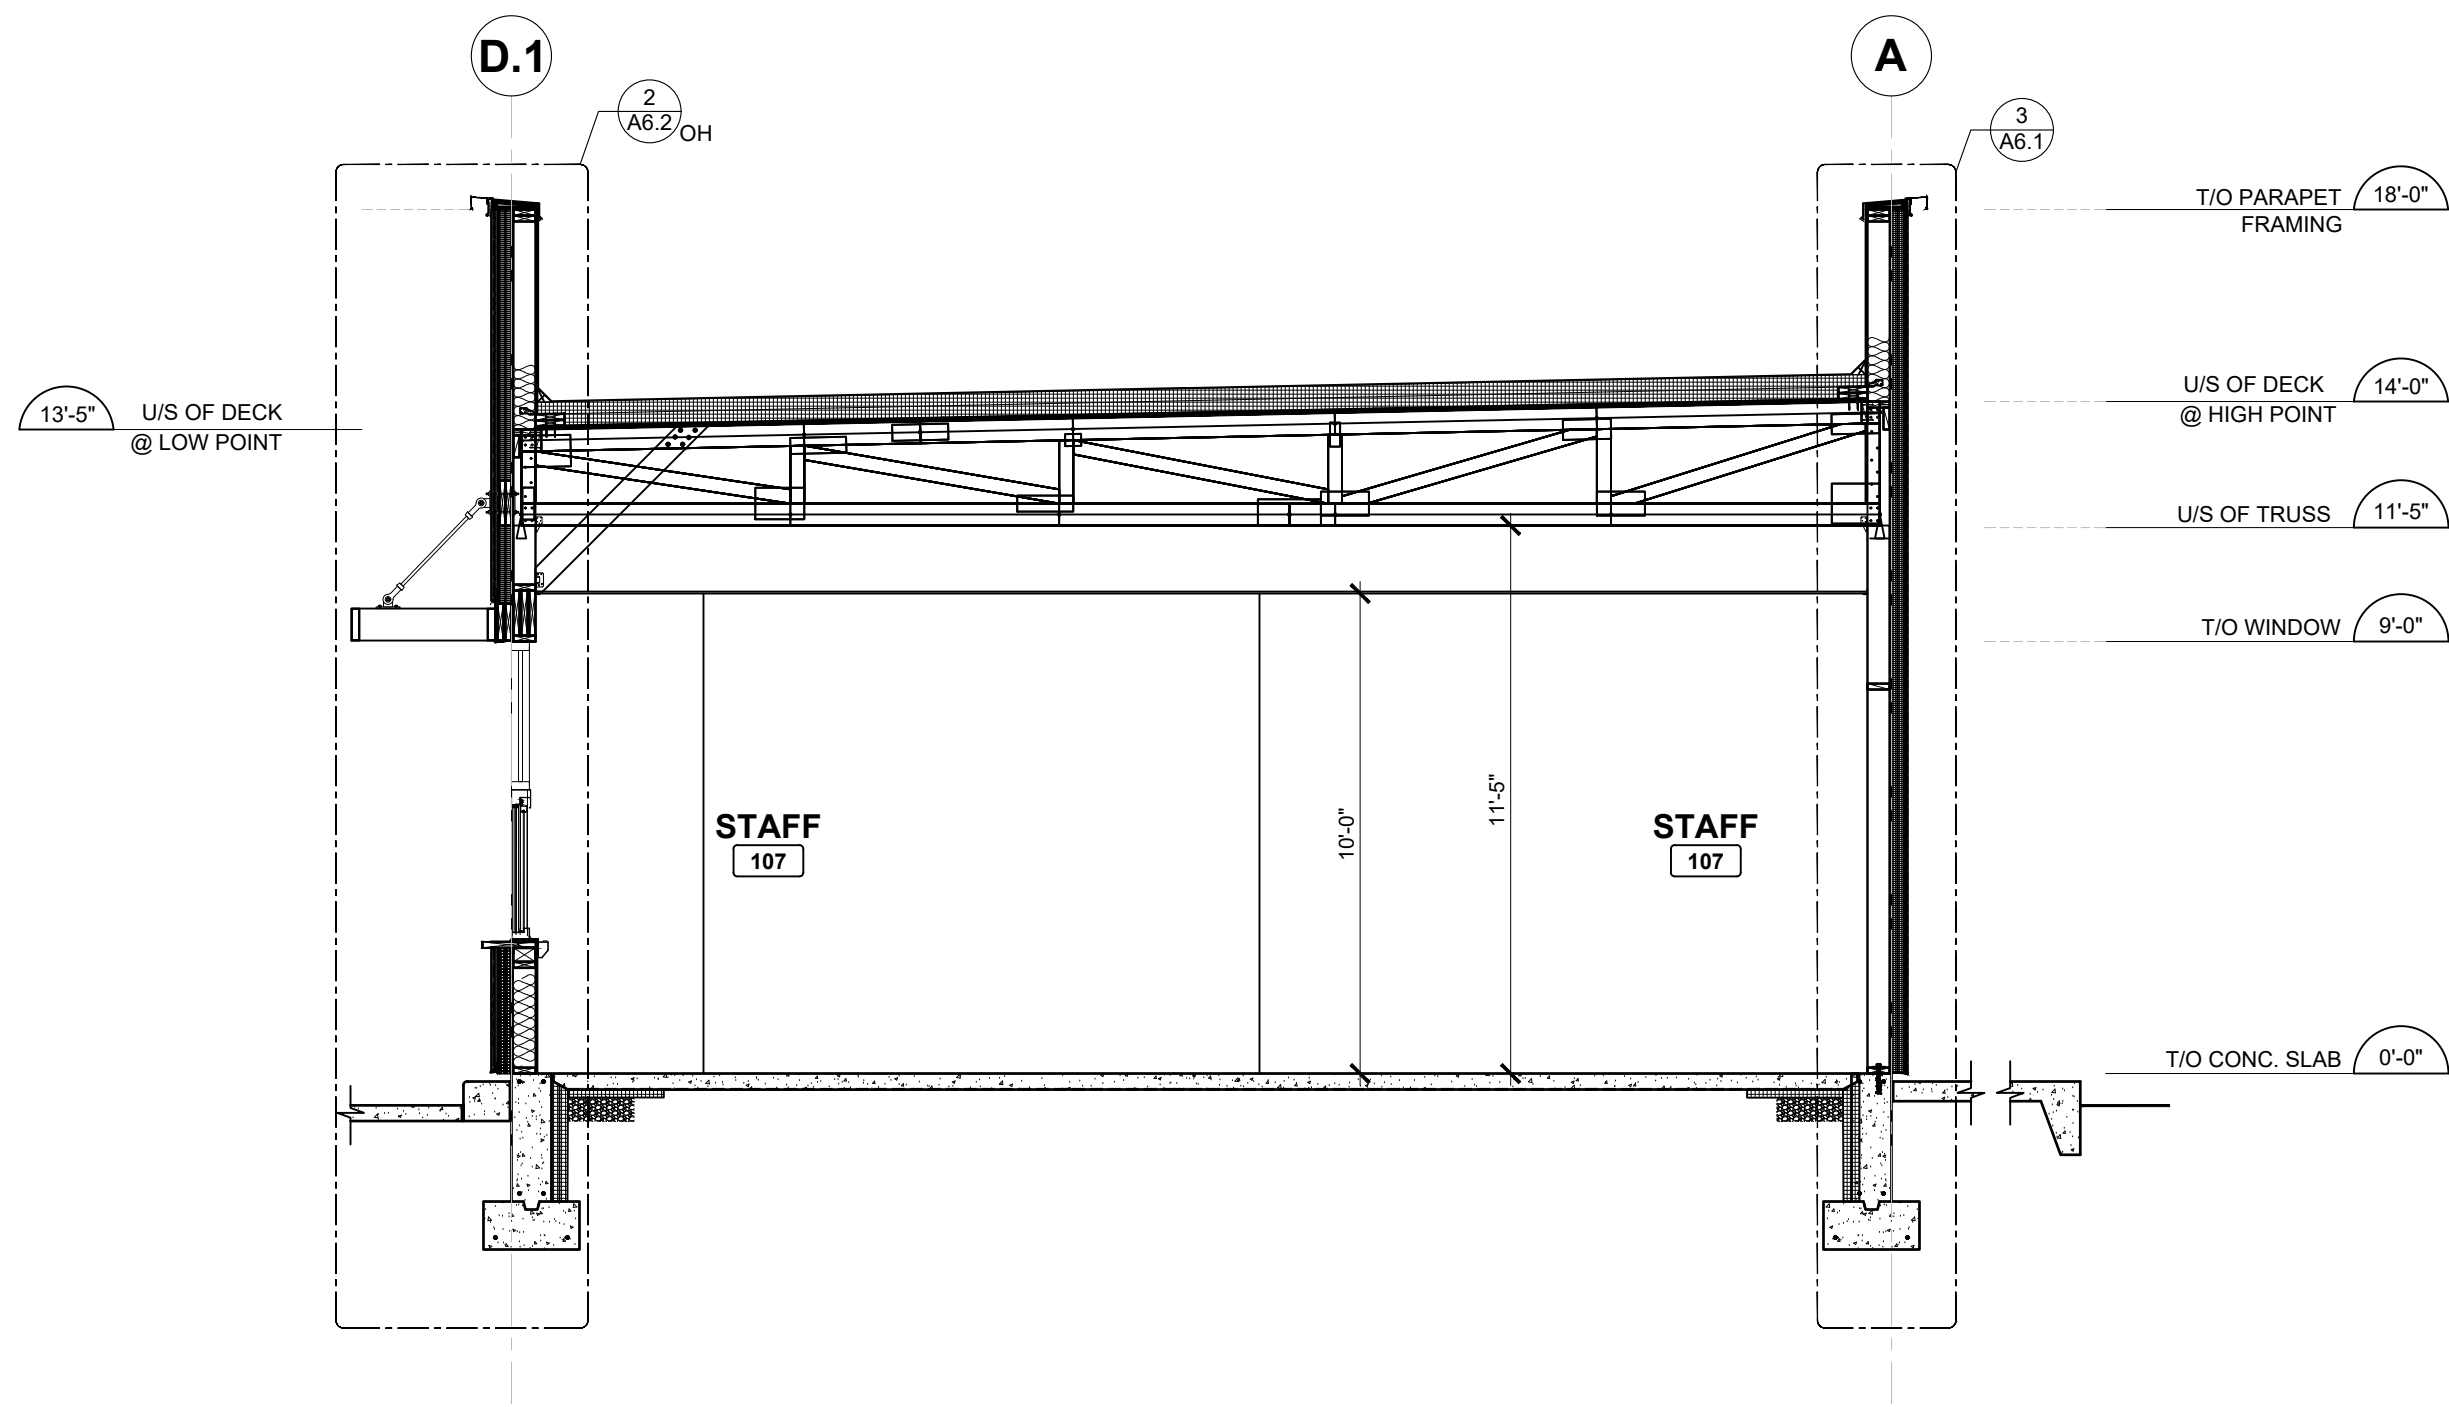

1 BUILDING SECTION
SCALE: 1/4" = 1'-0"

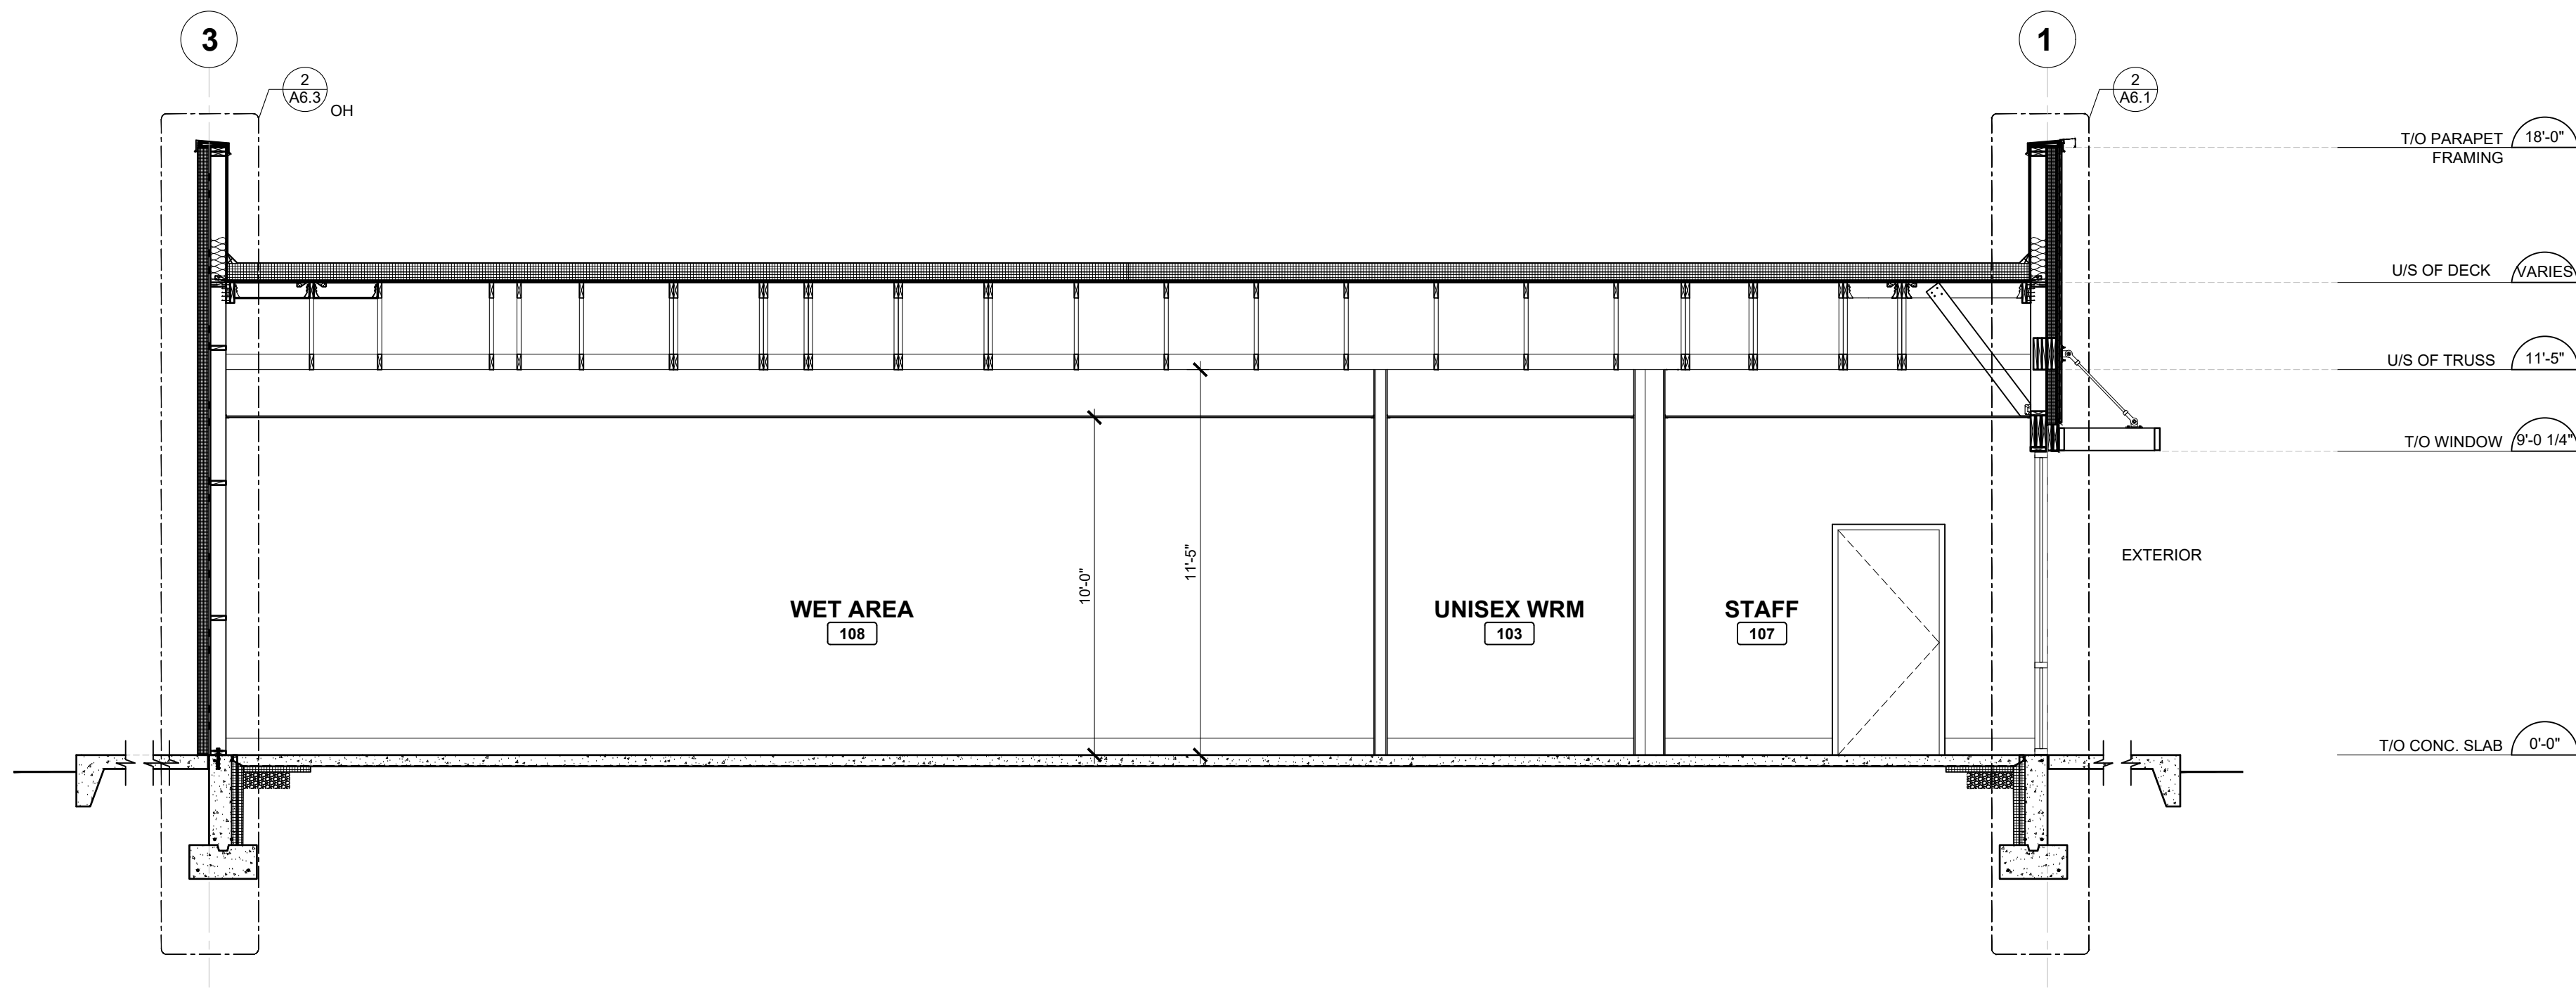

2 BUILDING SECTION
SCALE: 1/4" = 1'-0"

GENERAL NOTES:

1. CONTINUE GYPSUM BOARD TO U/S OF DECK & BETWEEN TRUSSES AT EXTERIOR WALLS (TYP.).
2. BUILDING EXTERIOR AS PER PRE-FABRICATION VENDOR SYSTEM ASSEMBLY. REFER TO PRE-FAB SHELL DRAWINGS FOR SCOPE AND WALL CONSTRUCTION.
NOTE: PRE-FAB WALL CONSTRUCTION LIMITS: INTERIOR SIDE FACE OF STUD TO OUTSIDE OF FACE OF EXTERIOR FINISH.

ISSUE TABLE

No.	Date (mm/dd/yy)	Description
01	09-26-25	DTGO PROTOTYPE DOCUMENTS

REVISIONS

No.	Date	Description

DRAWINGS REVISED AS PER DESIGN BULLETIN

No.	Date	Description

THIS DRAWING IS OWNED BY OR LICENSED FOR USE BY POPEYES LOUISIANA KITCHEN (OR ITS AFFILIATED OR RELATED COMPANIES) AND MAY NOT BE REPRODUCED, USED, DOWNLOADED, DISSEMINATED, PUBLISHED, OR TRANSFERRED IN ANY FORM OR BY ANY MEANS, EXCEPT WITH THE PRIOR WRITTEN CONSENT OF POPEYES LOUISIANA KITCHEN. COPYRIGHT INFRINGEMENT IS A VIOLATION OF FEDERAL LAW SUBJECT TO CRIMINAL AND CIVIL PENALTIES.

THE CONTRACTOR IS TO VERIFY ALL DIMENSIONS AND CONDITIONS ON THE PROJECT AND TO REPORT ANY DISCREPANCIES TO THE POPEYES LOUISIANA KITCHEN REPRESENTATIVE PRIOR TO COMMENCING WORK. THESE DRAWINGS ARE NOT TO BE USED FOR CONSTRUCTION PURPOSES UNLESS INDICATED BY POPEYES LOUISIANA KITCHEN AS "ISSUED FOR CONSTRUCTION".

Professional Seal

DESIGNER NOTES:
DESIGN GUIDELINE ONLY - NOT FOR PERMIT OR CONSTRUCTION

THESE DOCUMENTS MUST BE COMPLETED AND / OR MODIFIED BY A LICENSED ARCHITECT AND ENGINEER TO CONFORM TO ALL APPLICABLE CODES, AND SPECIFIC SITE CONDITIONS. THERE IS NO WARRANTY, WHETHER IMPLIED OR EXPRESSED THAT THESE DOCUMENTS MEET THE APPLICABLE CODE REQUIREMENTS. LIABILITY FOR THE DESIGN AND ANY USE OF THE DOCUMENTS IS THE SOLE RESPONSIBILITY OF THE ARCHITECT AND ENGINEER OF RECORD.

Company Logo

Project



Store Type

US DTGO PROTOTYPE

Location

PROTOTYPE
DTGO (U.S.)

CITY, STATE

Drawing Title

BUILDING SECTIONS

Drawn

XXXX

Checked

XX

Scale

AS NOTED

Date


##.##.####

Project No.


XX

Drawing No.


A6

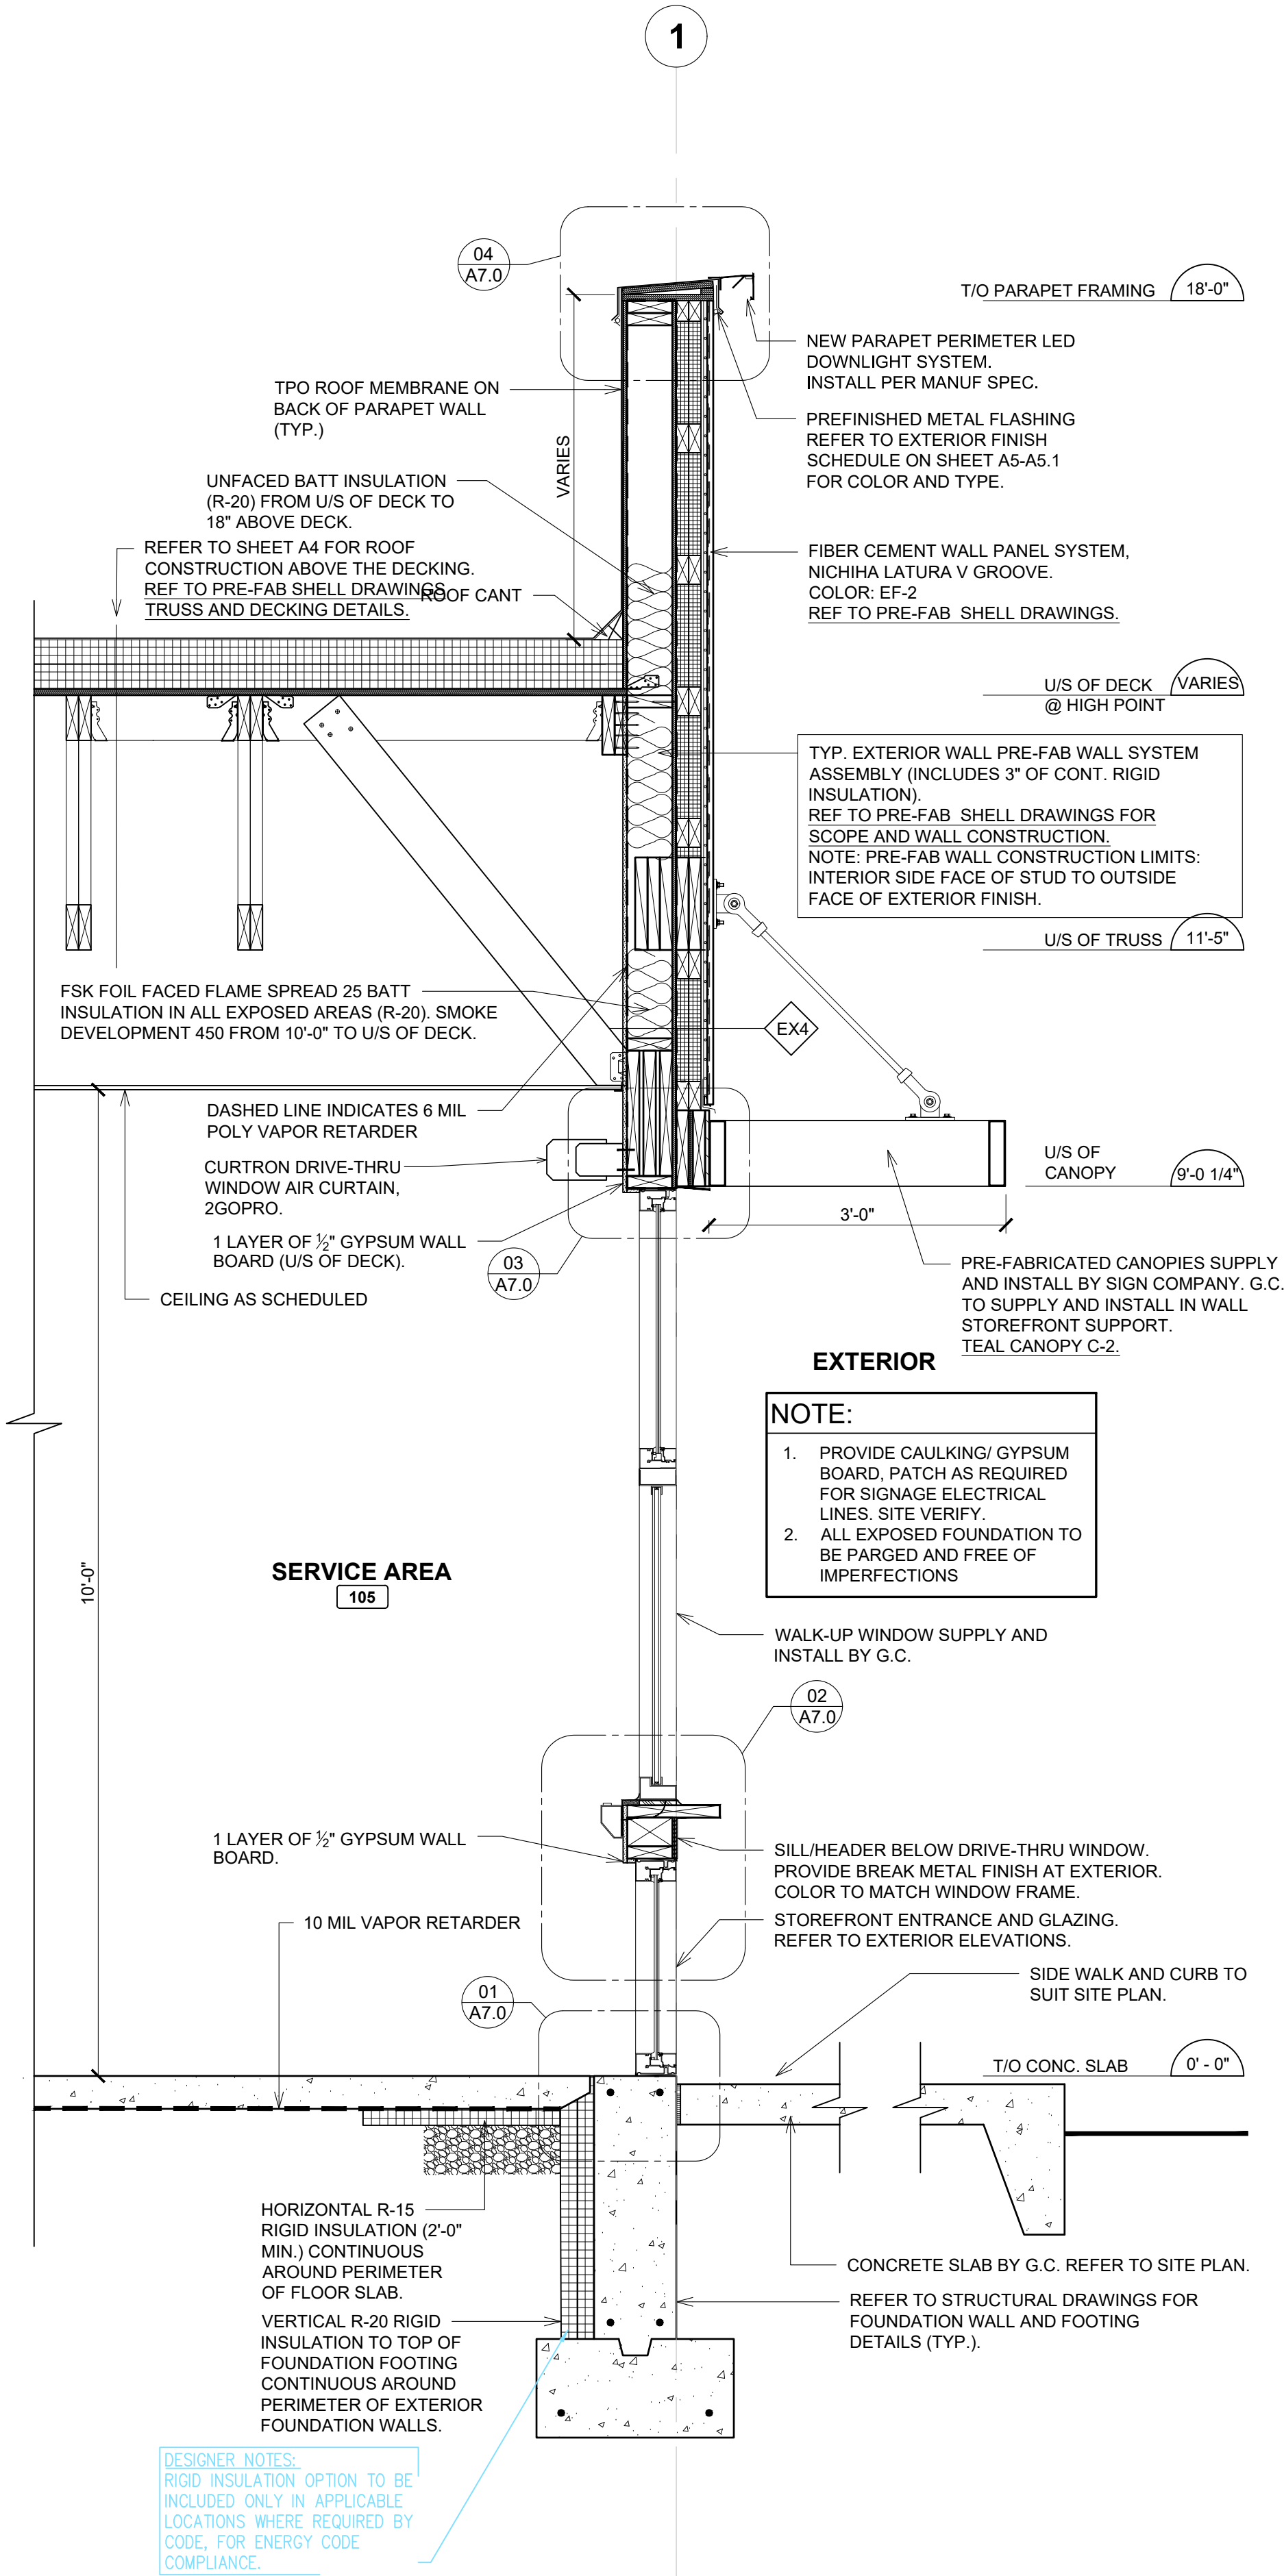

1 WALL SECTION @ WALK-UP WINDOW
SCALE: 3/4" = 1'-0"

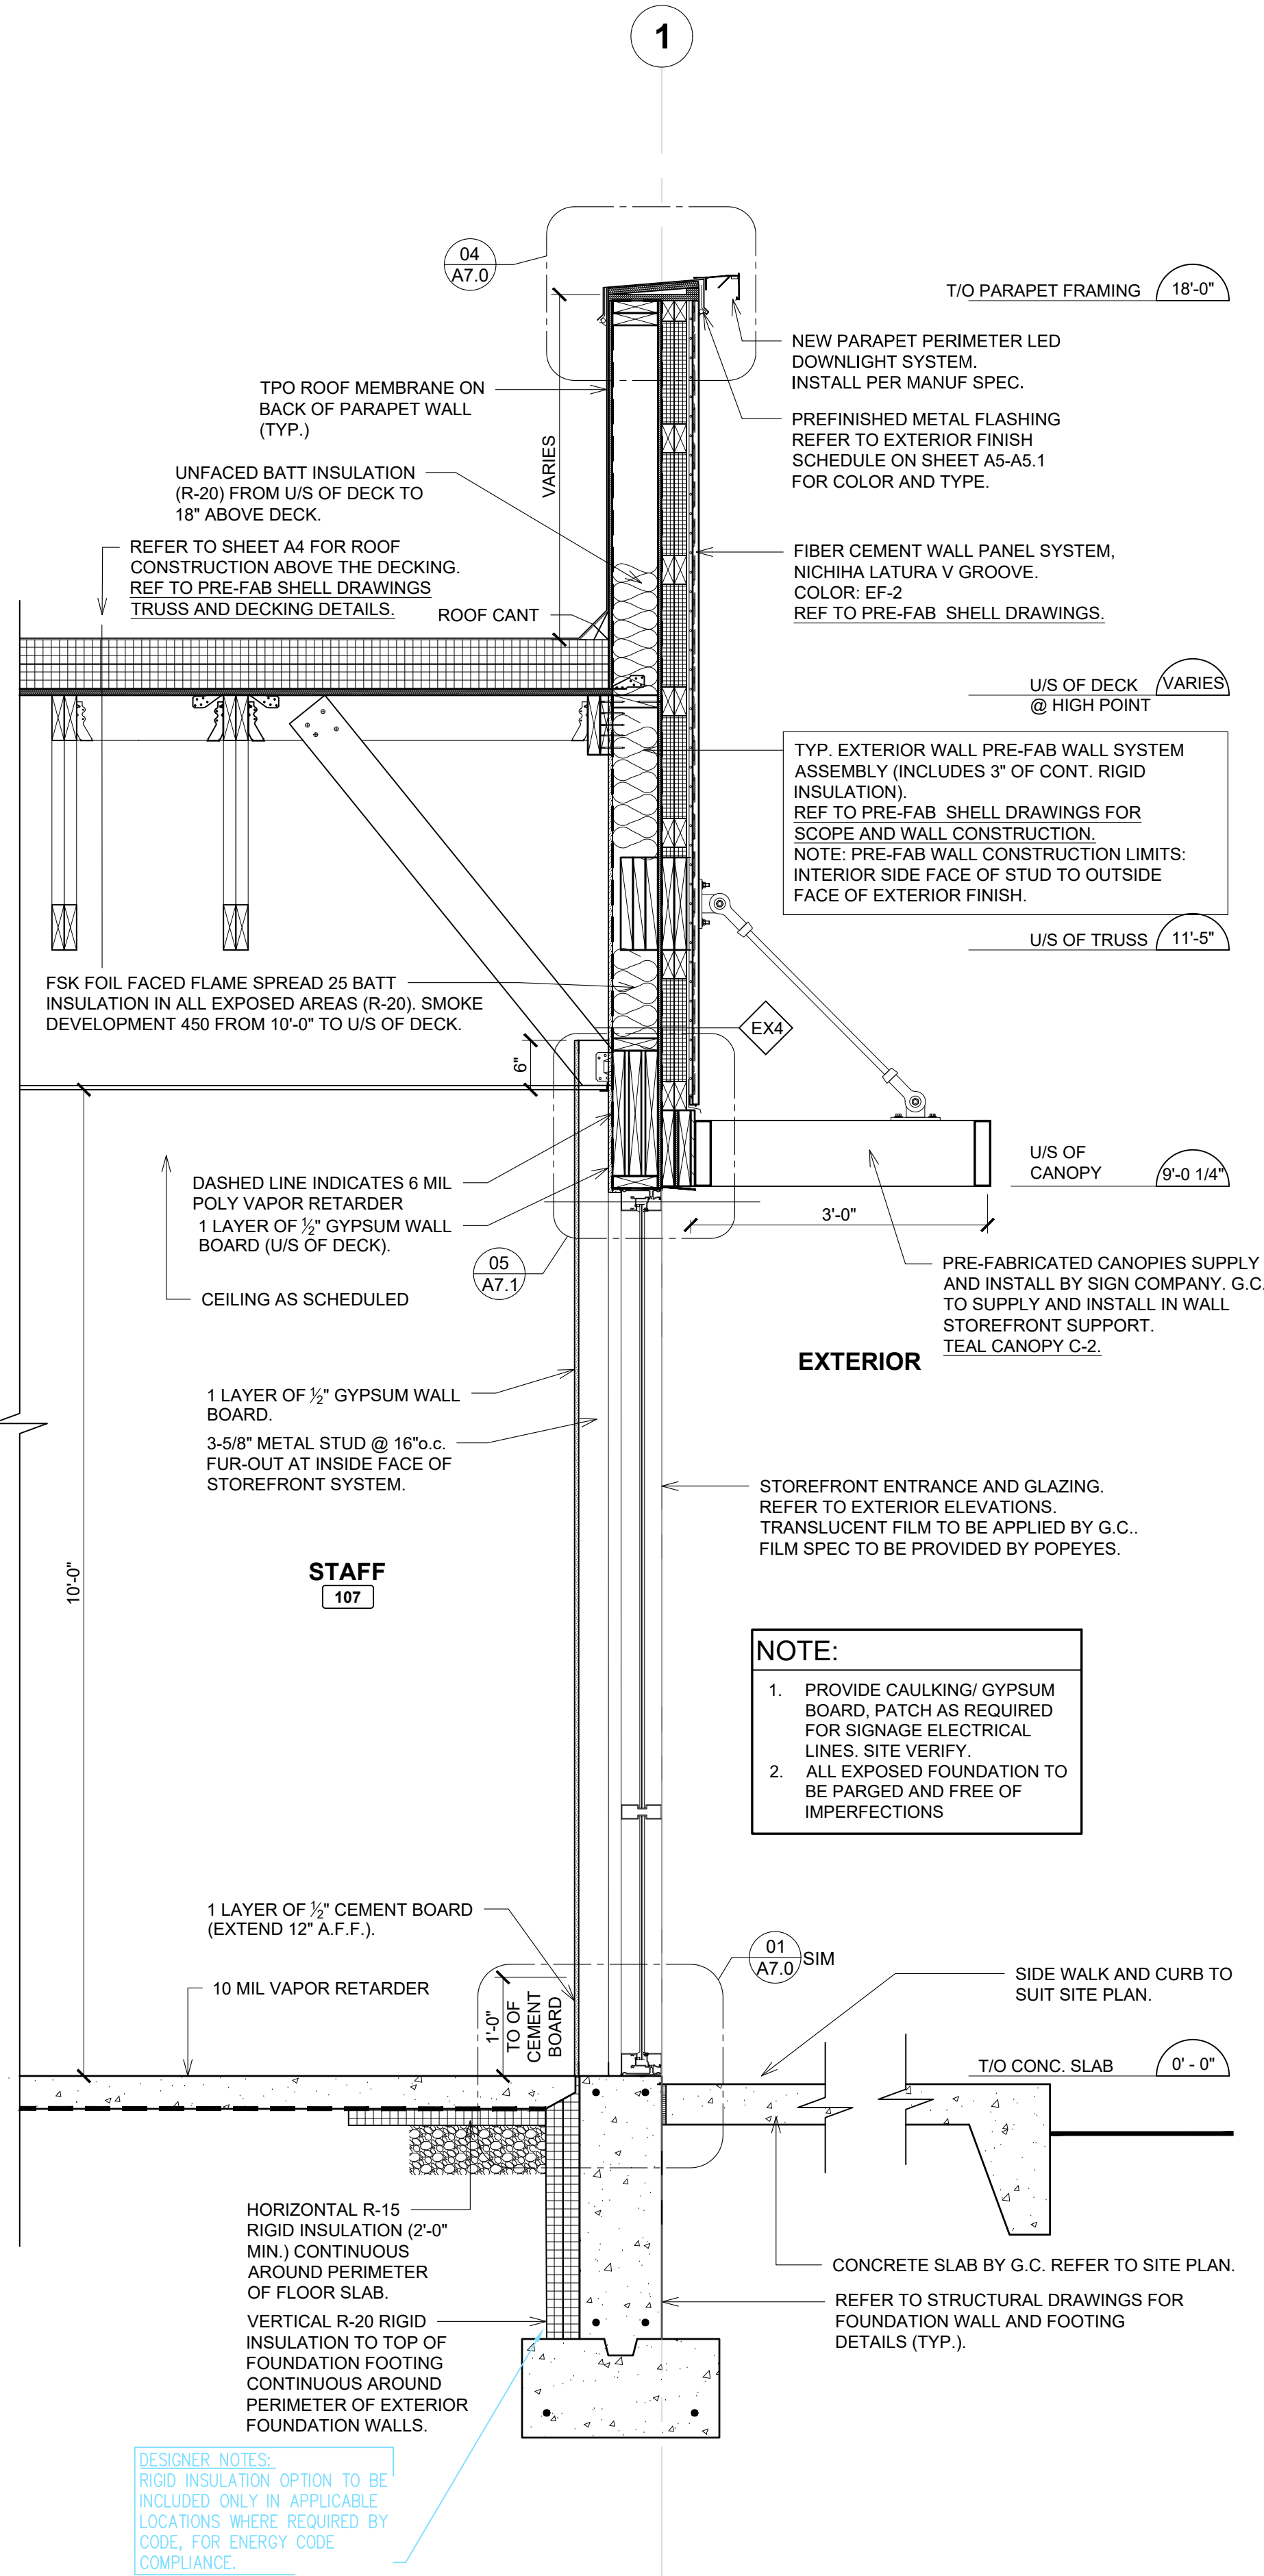


2 WALL SECTION @ FRONT
SCALE: 3/4" = 1'-0"

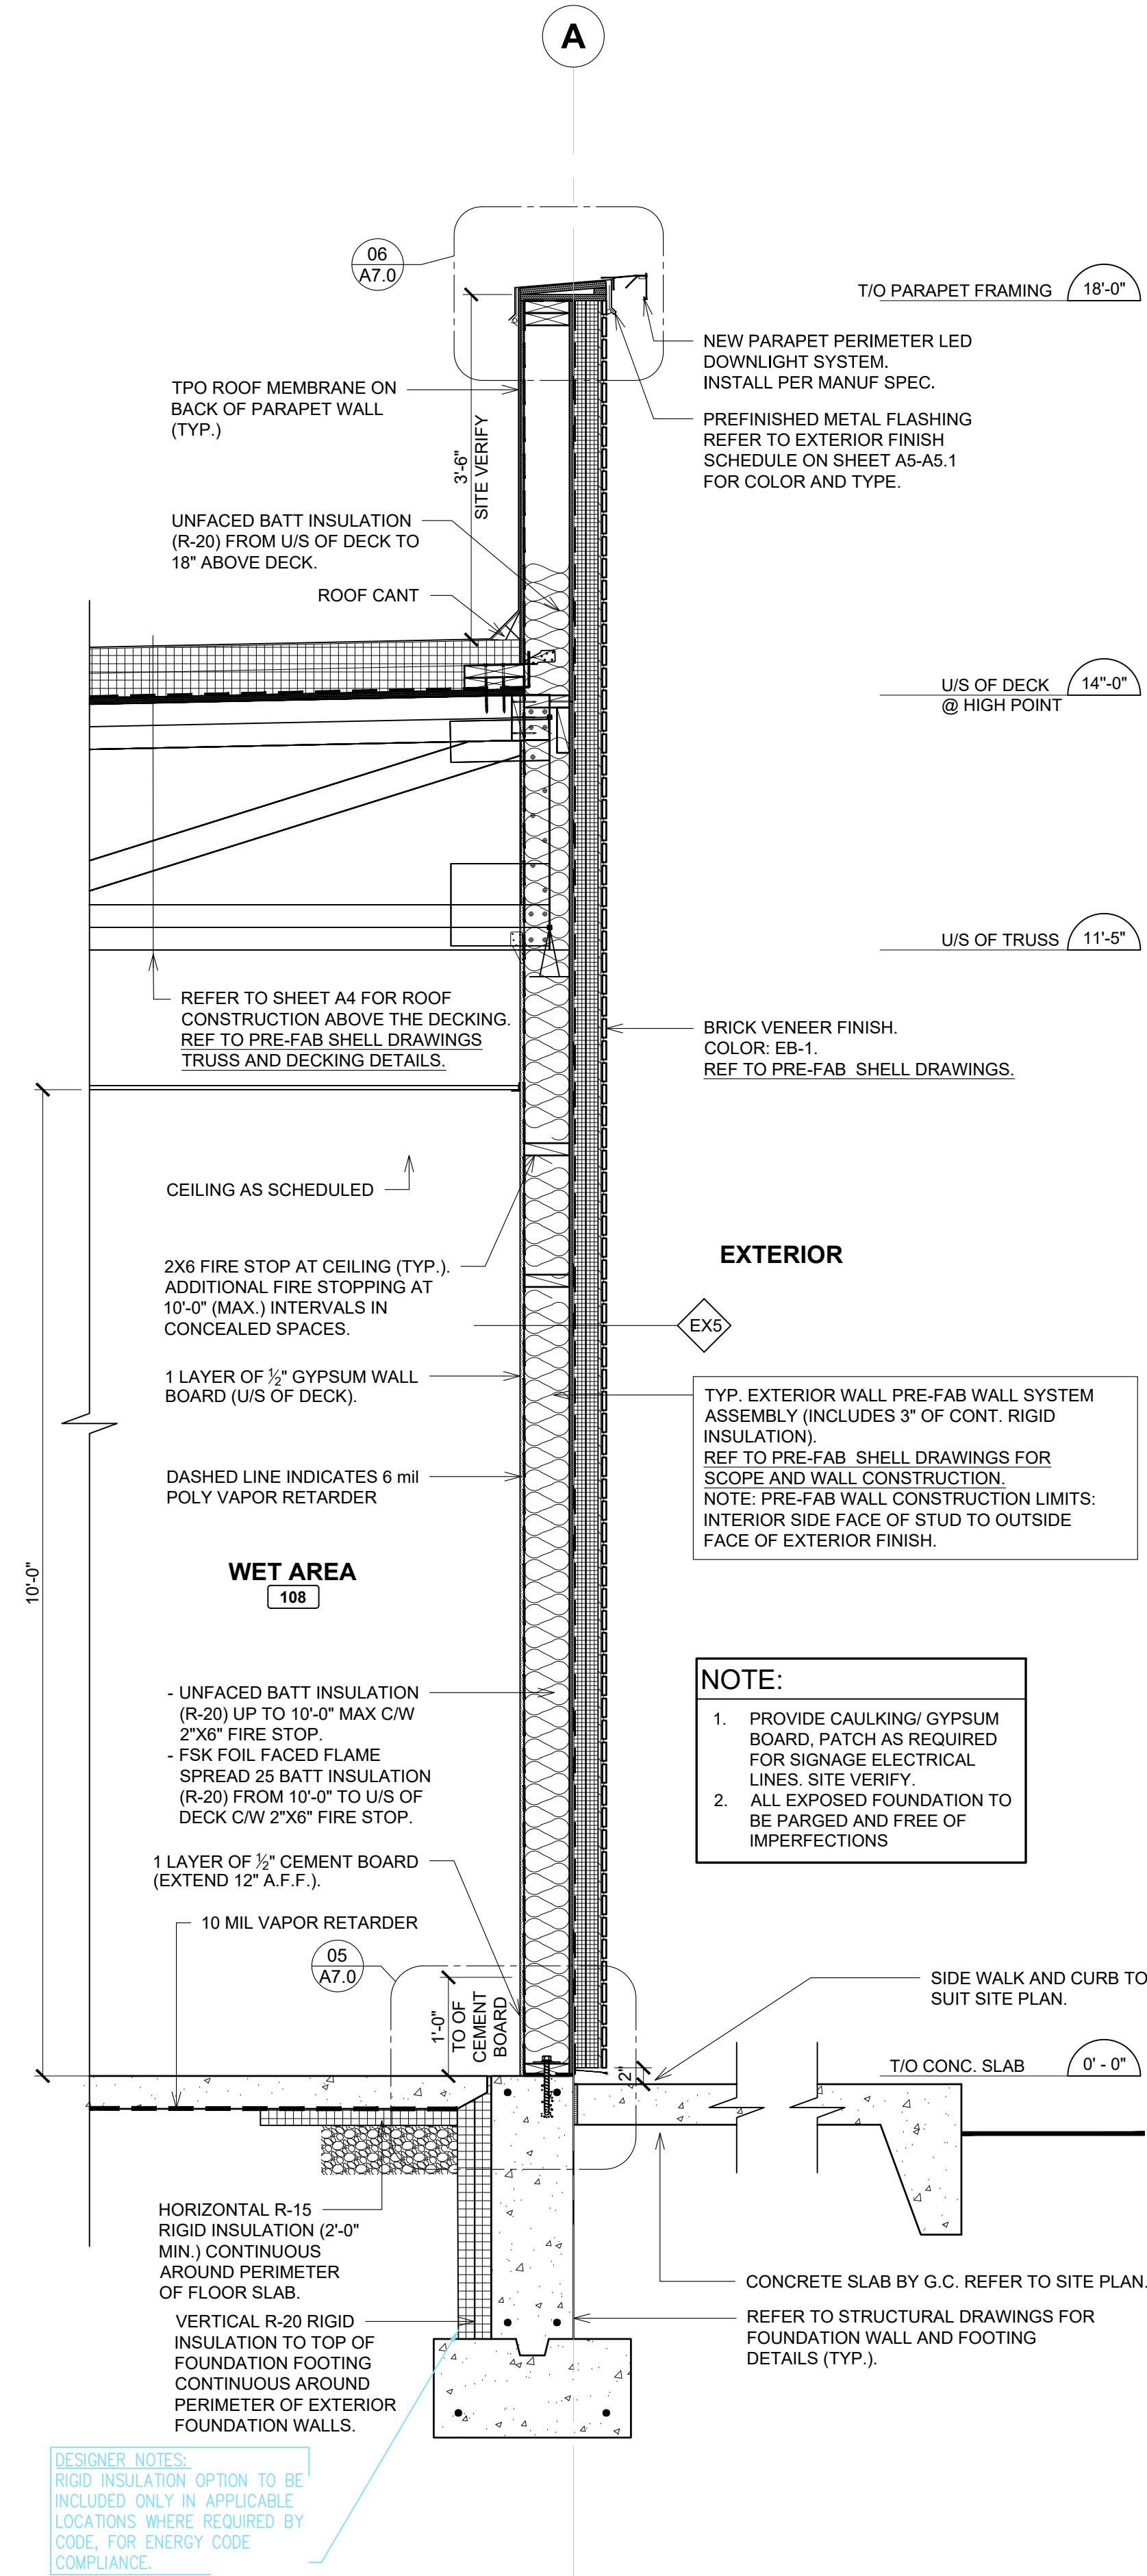


3 WALL SECTION @ SIDE
SCALE: 3/4" = 1'-0"

ISSUE TABLE		
No.	Date (mm/dd/yy)	Description
01	09-26-25	DTGO PROTOTYPE DOCUMENTS
REVISIONS		
No.	Date	Description
DRAWINGS REVISED AS PER DESIGN BULLETIN		
No.	Date	Description
THIS DRAWING IS OWNED BY OR LICENSED FOR USE BY POPEYES LOUISIANA KITCHEN (OR ITS AFFILIATED OR RELATED COMPANIES) AND MAY NOT BE REPRODUCED, USED, DOWNLOADED, DISSEMINATED, PUBLISHED, OR TRANSFERRED IN ANY FORM OR BY ANY MEANS, EXCEPT WITH THE PRIOR WRITTEN CONSENT OF POPEYES LOUISIANA KITCHEN. COPYRIGHT INFRINGEMENT IS A VIOLATION OF FEDERAL LAW SUBJECT TO CRIMINAL AND CIVIL PENALTIES.		
THE CONTRACTOR IS TO VERIFY ALL DIMENSIONS AND CONDITIONS ON THE PROJECT AND TO REPORT ANY DISCREPANCIES TO THE POPEYES LOUISIANA KITCHEN REPRESENTATIVE PRIOR TO COMMENCING WORK. THESE DRAWINGS ARE NOT TO BE USED FOR CONSTRUCTION PURPOSES UNLESS INDICATED BY POPEYES LOUISIANA KITCHEN AS ISSUED FOR CONSTRUCTION.		
Professional Seal		
DESIGNER NOTES: DESIGN GUIDELINE ONLY - NOT FOR PERMIT OR CONSTRUCTION		
THESE DOCUMENTS MUST BE COMPLETED AND / OR MODIFIED BY A LICENSED ARCHITECT AND ENGINEER TO CONFORM TO ALL APPLICABLE CODES, AND SPECIFIC SITE CONDITIONS. THERE IS NO WARRANTY, WHETHER IMPLIED OR EXPRESSED, THAT THESE DOCUMENTS MEET THE APPLICABLE CODE REQUIREMENTS. LIABILITY FOR THE DESIGN AND ANY USE OF THE DOCUMENTS IS THE SOLE RESPONSIBILITY OF THE ARCHITECT AND ENGINEER OF RECORD.		
Company Logo		
Project		
Store Type		
Location		
Drawing Title		
Drawn		
Scale		
Project No.		
Checked		
Date		
Drawing No.		


1 WALL SECTION @ DT ELEVATION
SCALE: 3/4" = 1'-0"

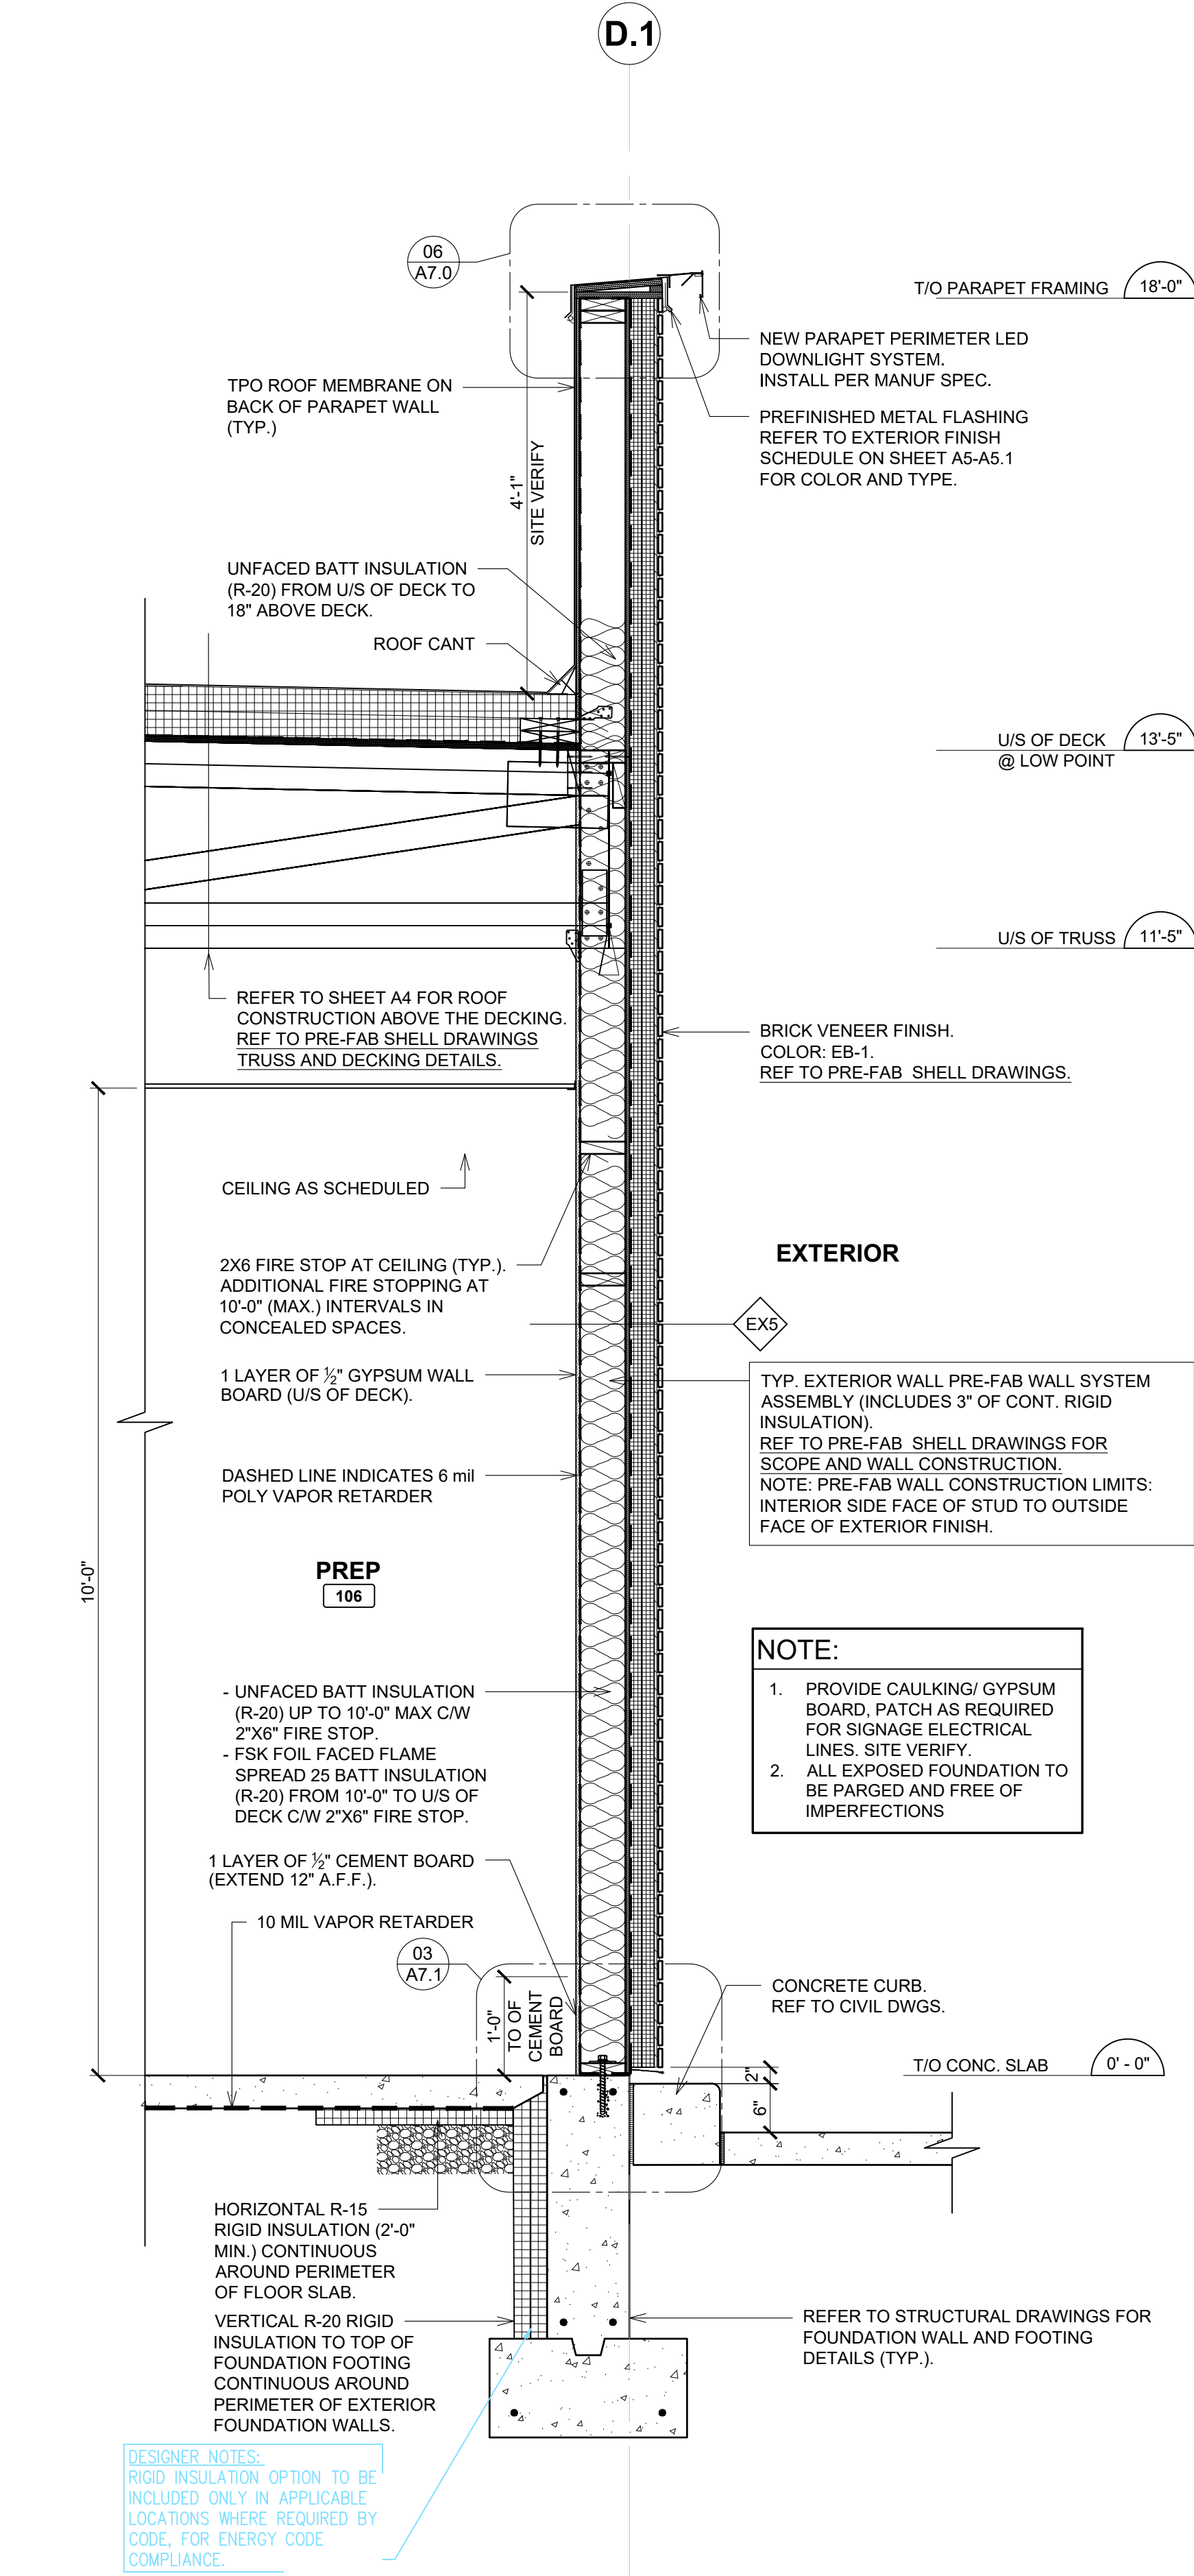


2 WALL SECTION @ DT WINDOW
SCALE: 3/4" = 1'-0"

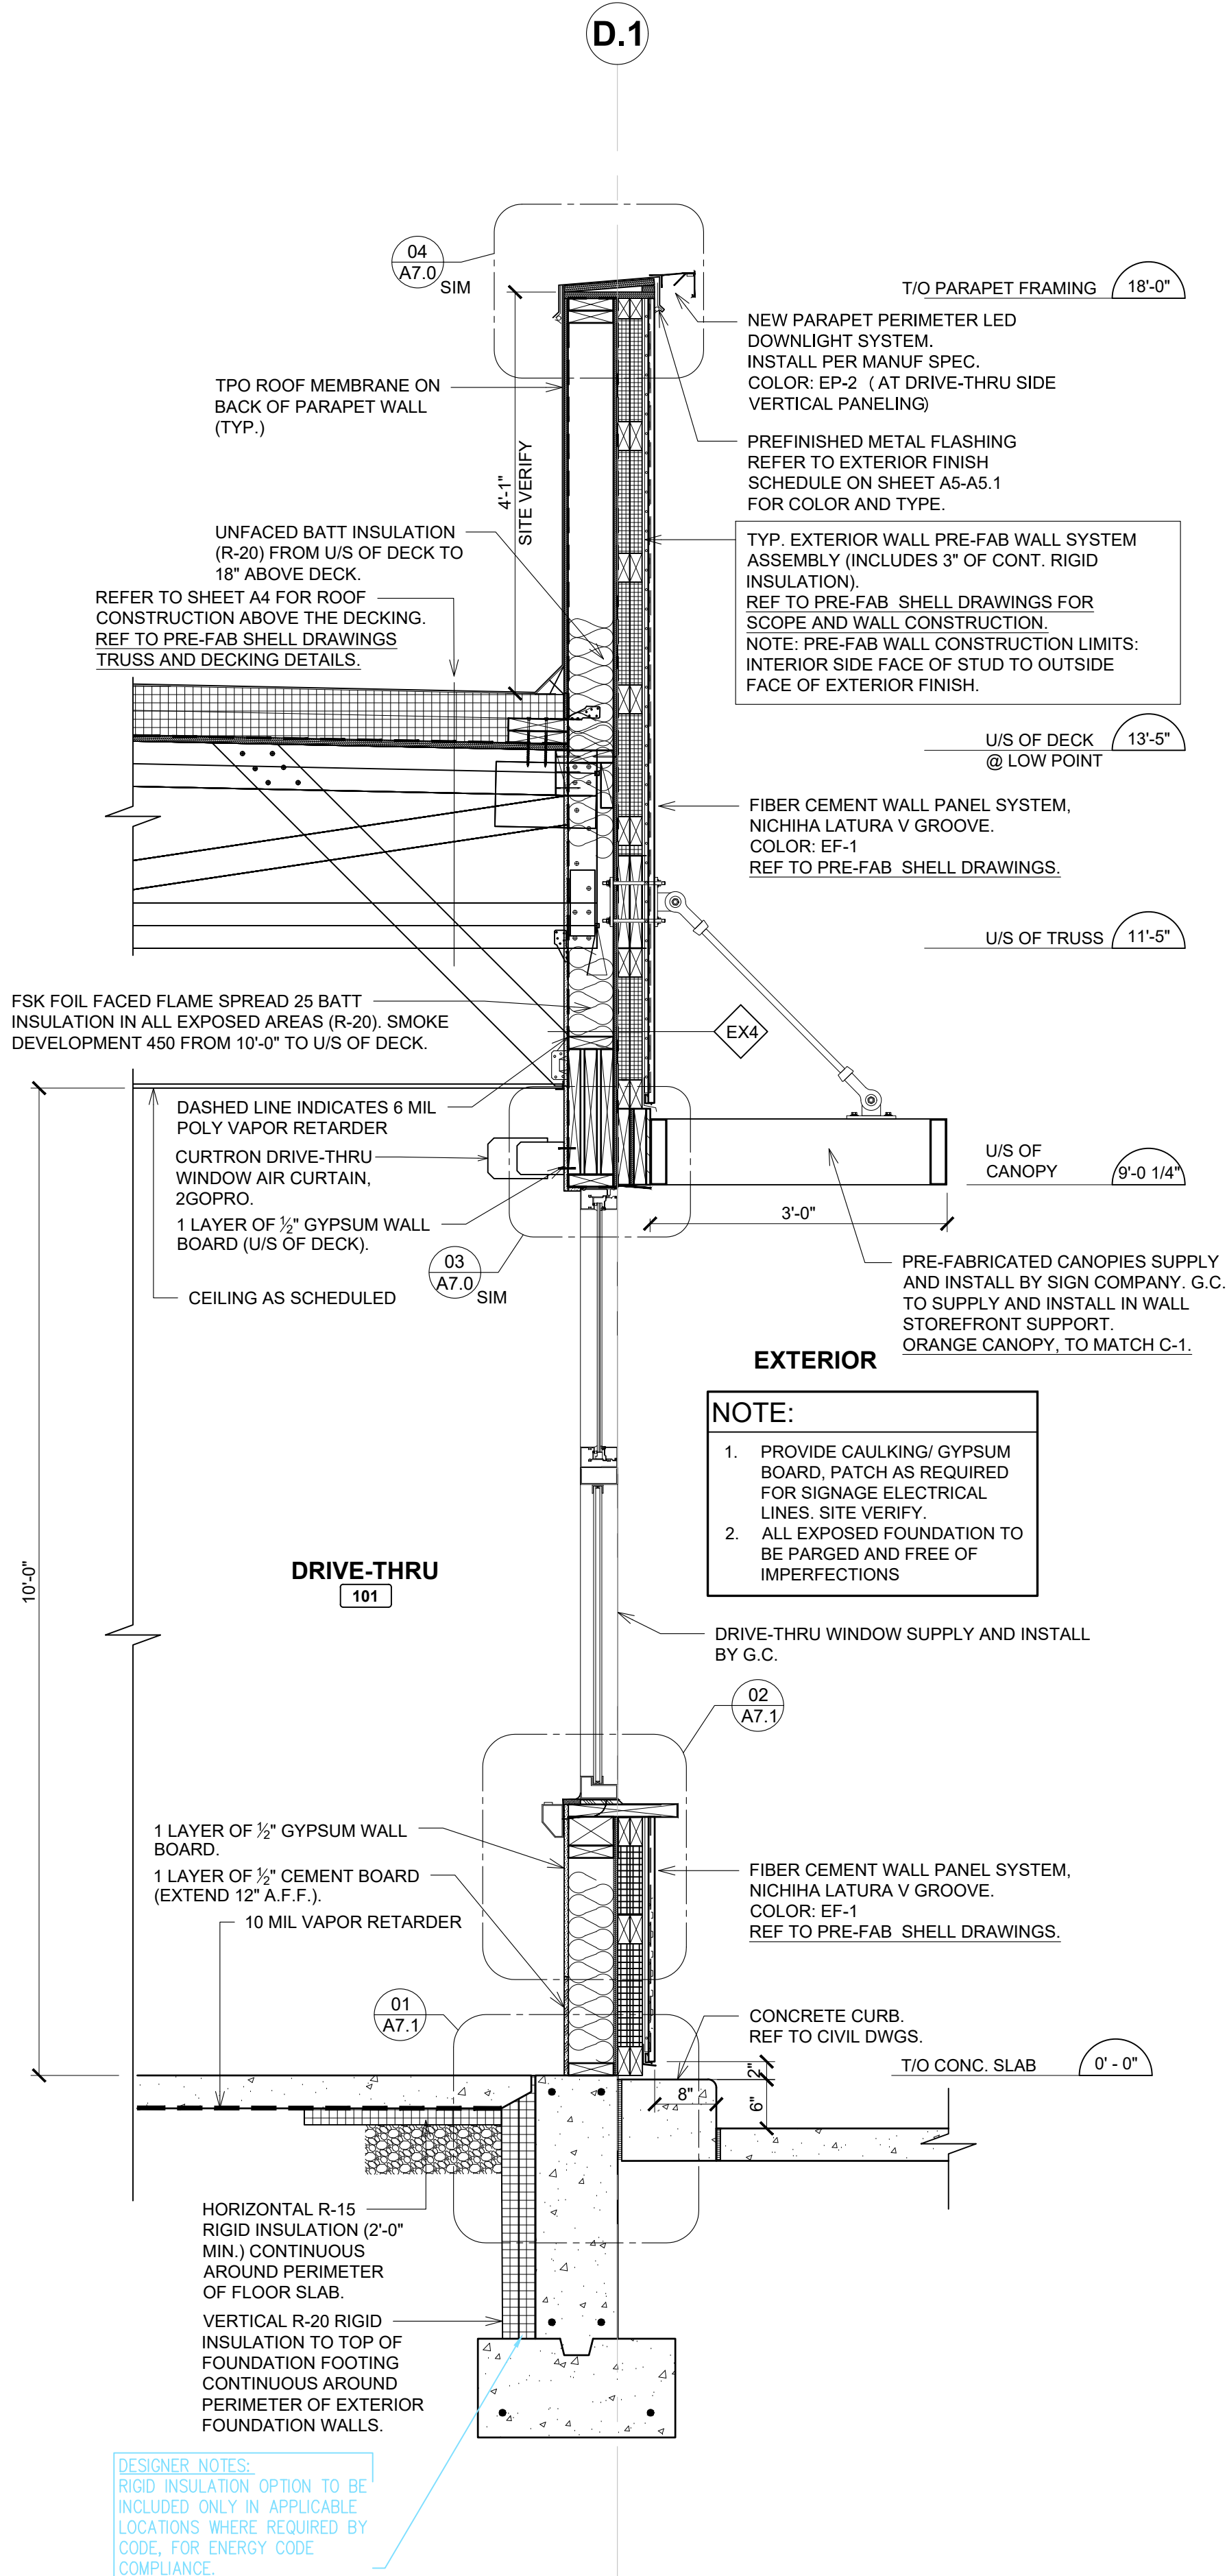


3 WALL SECTION @ REAR
SCALE: 3/4" = 1'-0"

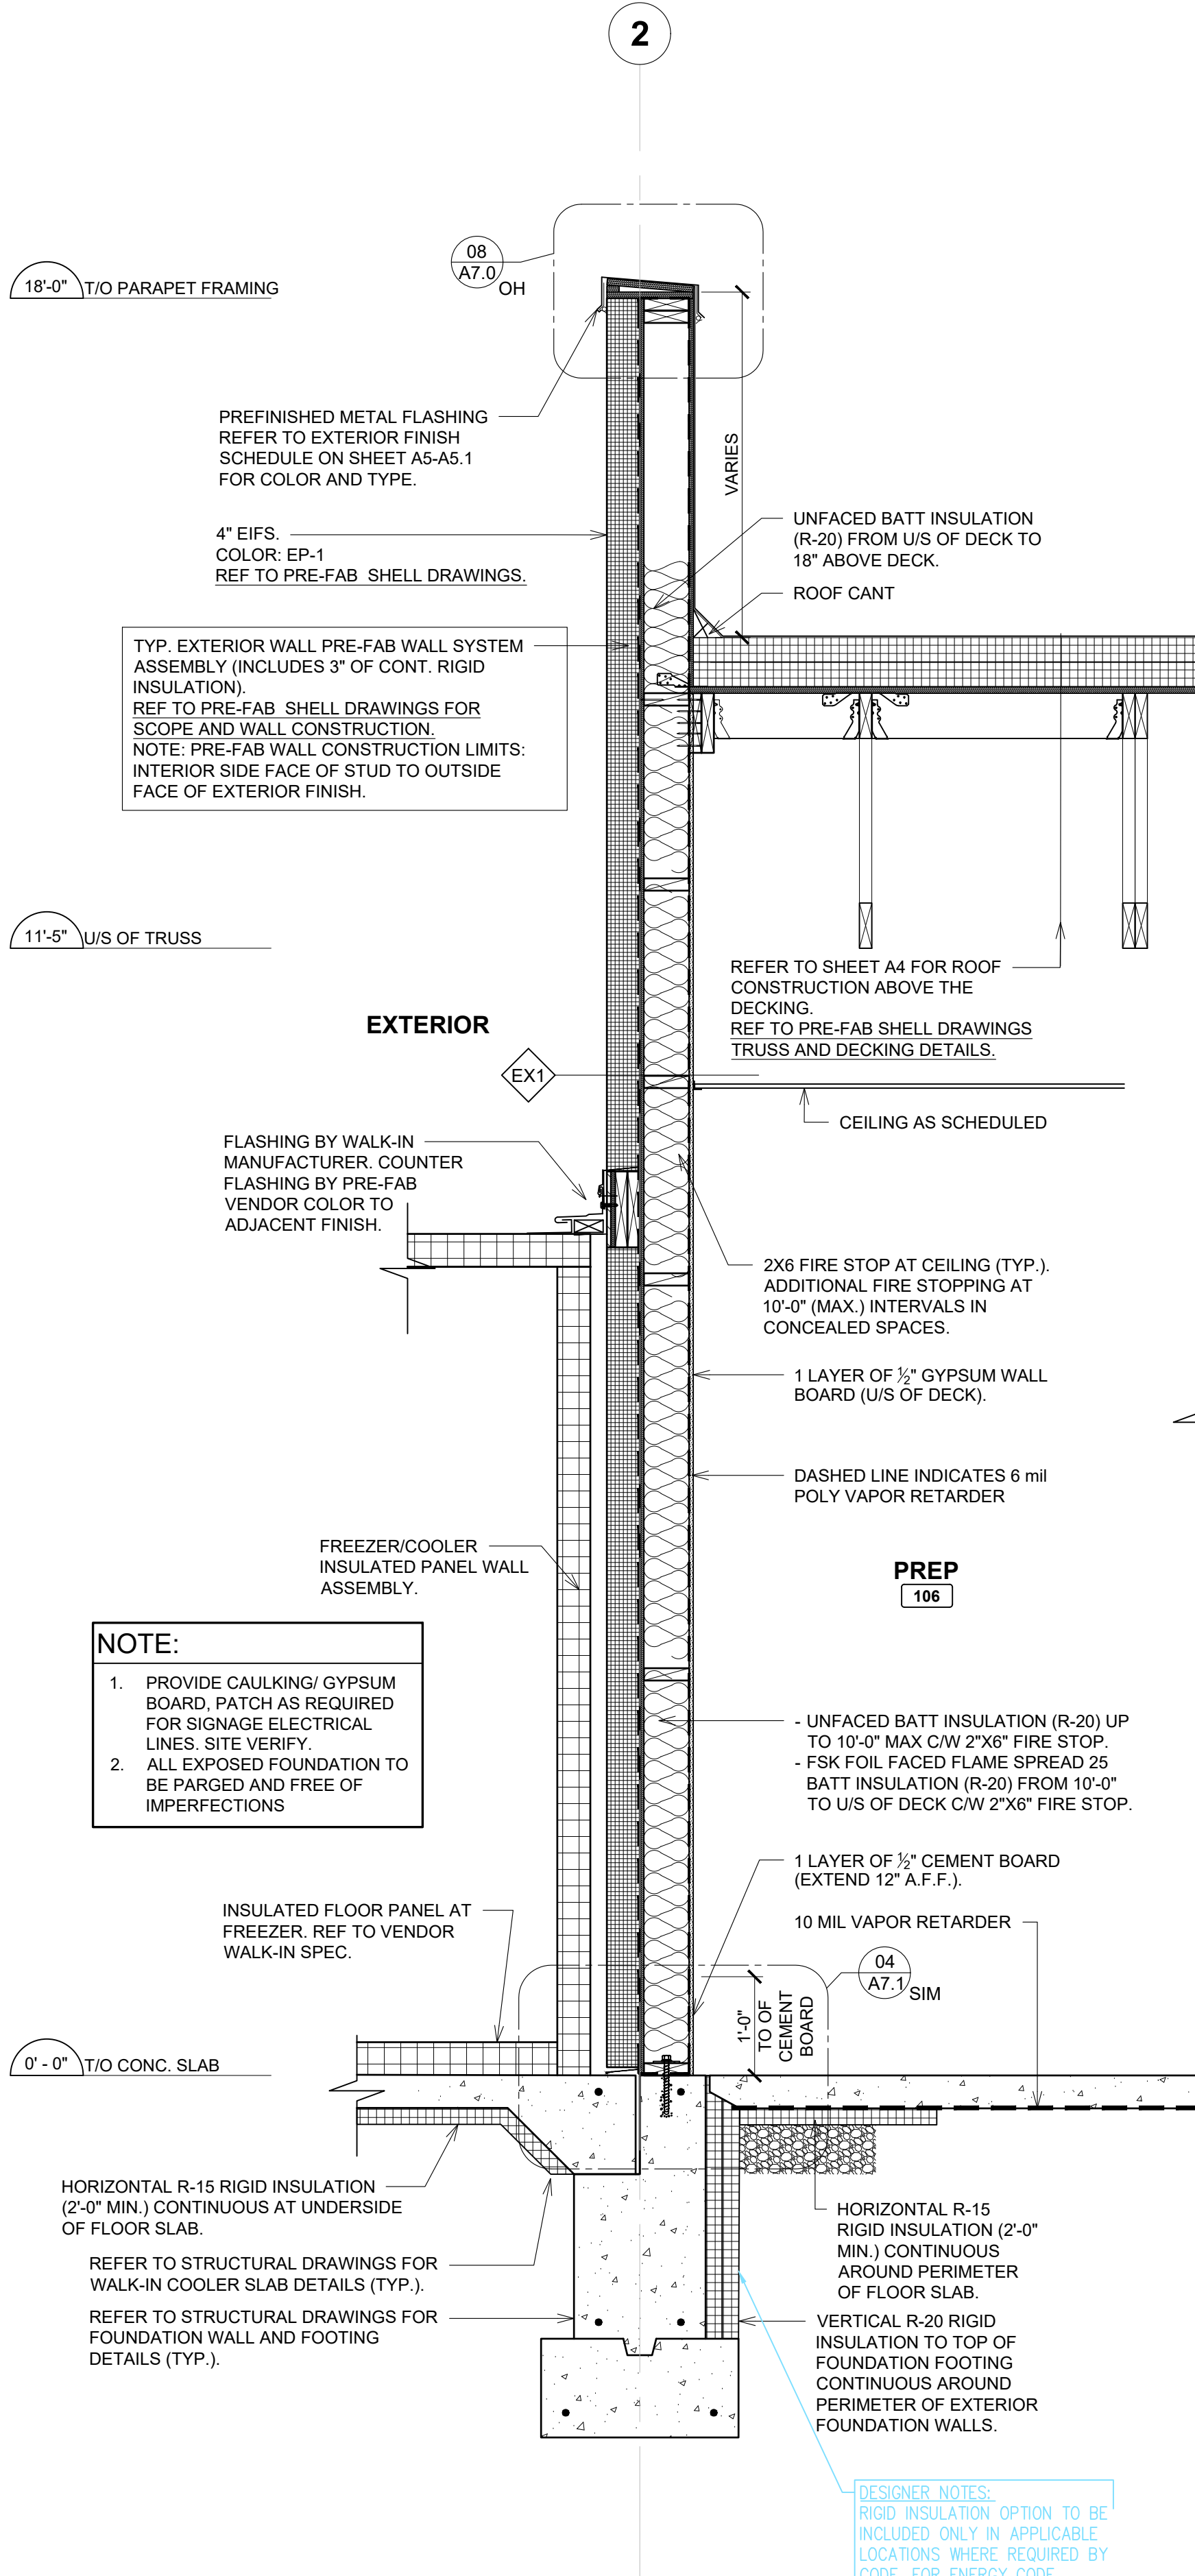


ISSUE TABLE		
No.	Date (mm/dd/yy)	Description
01	09-26-25	DTGO PROTOTYPE DOCUMENTS
REVISIONS		
No.	Date	Description
DRAWINGS REVISED AS PER DESIGN BULLETIN		
No.	Date	Description
THIS DRAWING IS OWNED BY OR LICENSED FOR USE BY POPEYES LOUISIANA KITCHEN (OR ITS AFFILIATED OR RELATED COMPANIES) AND MAY NOT BE REPRODUCED, USED, DOWNLOADED, DISSEMINATED, PUBLISHED, OR TRANSFERRED IN ANY FORM OR BY ANY MEANS, EXCEPT WITH THE PRIOR WRITTEN CONSENT OF POPEYES LOUISIANA KITCHEN. COPYRIGHT INFRINGEMENT IS A VIOLATION OF FEDERAL LAW SUBJECT TO CRIMINAL AND CIVIL PENALTIES.		
THE CONTRACTOR IS TO VERIFY ALL DIMENSIONS AND CONDITIONS ON THE PROJECT AND TO REPORT ANY DISCREPANCIES TO THE POPEYES LOUISIANA KITCHEN REPRESENTATIVE PRIOR TO COMMENCING WORK. THESE DRAWINGS ARE NOT TO BE USED FOR CONSTRUCTION PURPOSES UNLESS INDICATED BY POPEYES LOUISIANA KITCHEN AS "ISSUED FOR CONSTRUCTION".		
Professional Seal		
DESIGNER NOTES: DESIGN GUIDELINE ONLY - NOT FOR PERMIT OR CONSTRUCTION		
THESE DOCUMENTS MUST BE COMPLETED AND / OR MODIFIED BY A LICENSED ARCHITECT AND ENGINEER TO CONFORM TO ALL APPLICABLE CODES, AND SPECIFIC SITE CONDITIONS. THERE IS NO WARRANTY, WHETHER IMPLIED OR EXPRESSED, THAT THESE DOCUMENTS MEET THE APPLICABLE CODE REQUIREMENTS. THE LIABILITY FOR THE DESIGN AND ANY USE OF THE DOCUMENTS IS THE SOLE RESPONSIBILITY OF THE ARCHITECT AND ENGINEER OF RECORD.		
Company Logo		
Project		
Store Type US DTGO PROTOTYPE		
Location CITY, STATE		
Drawing Title WALL SECTIONS		
Drawn XX		Checked XX
Scale AS NOTED		Date ##.##.####
Project No. XX		Drawing No. A6.2

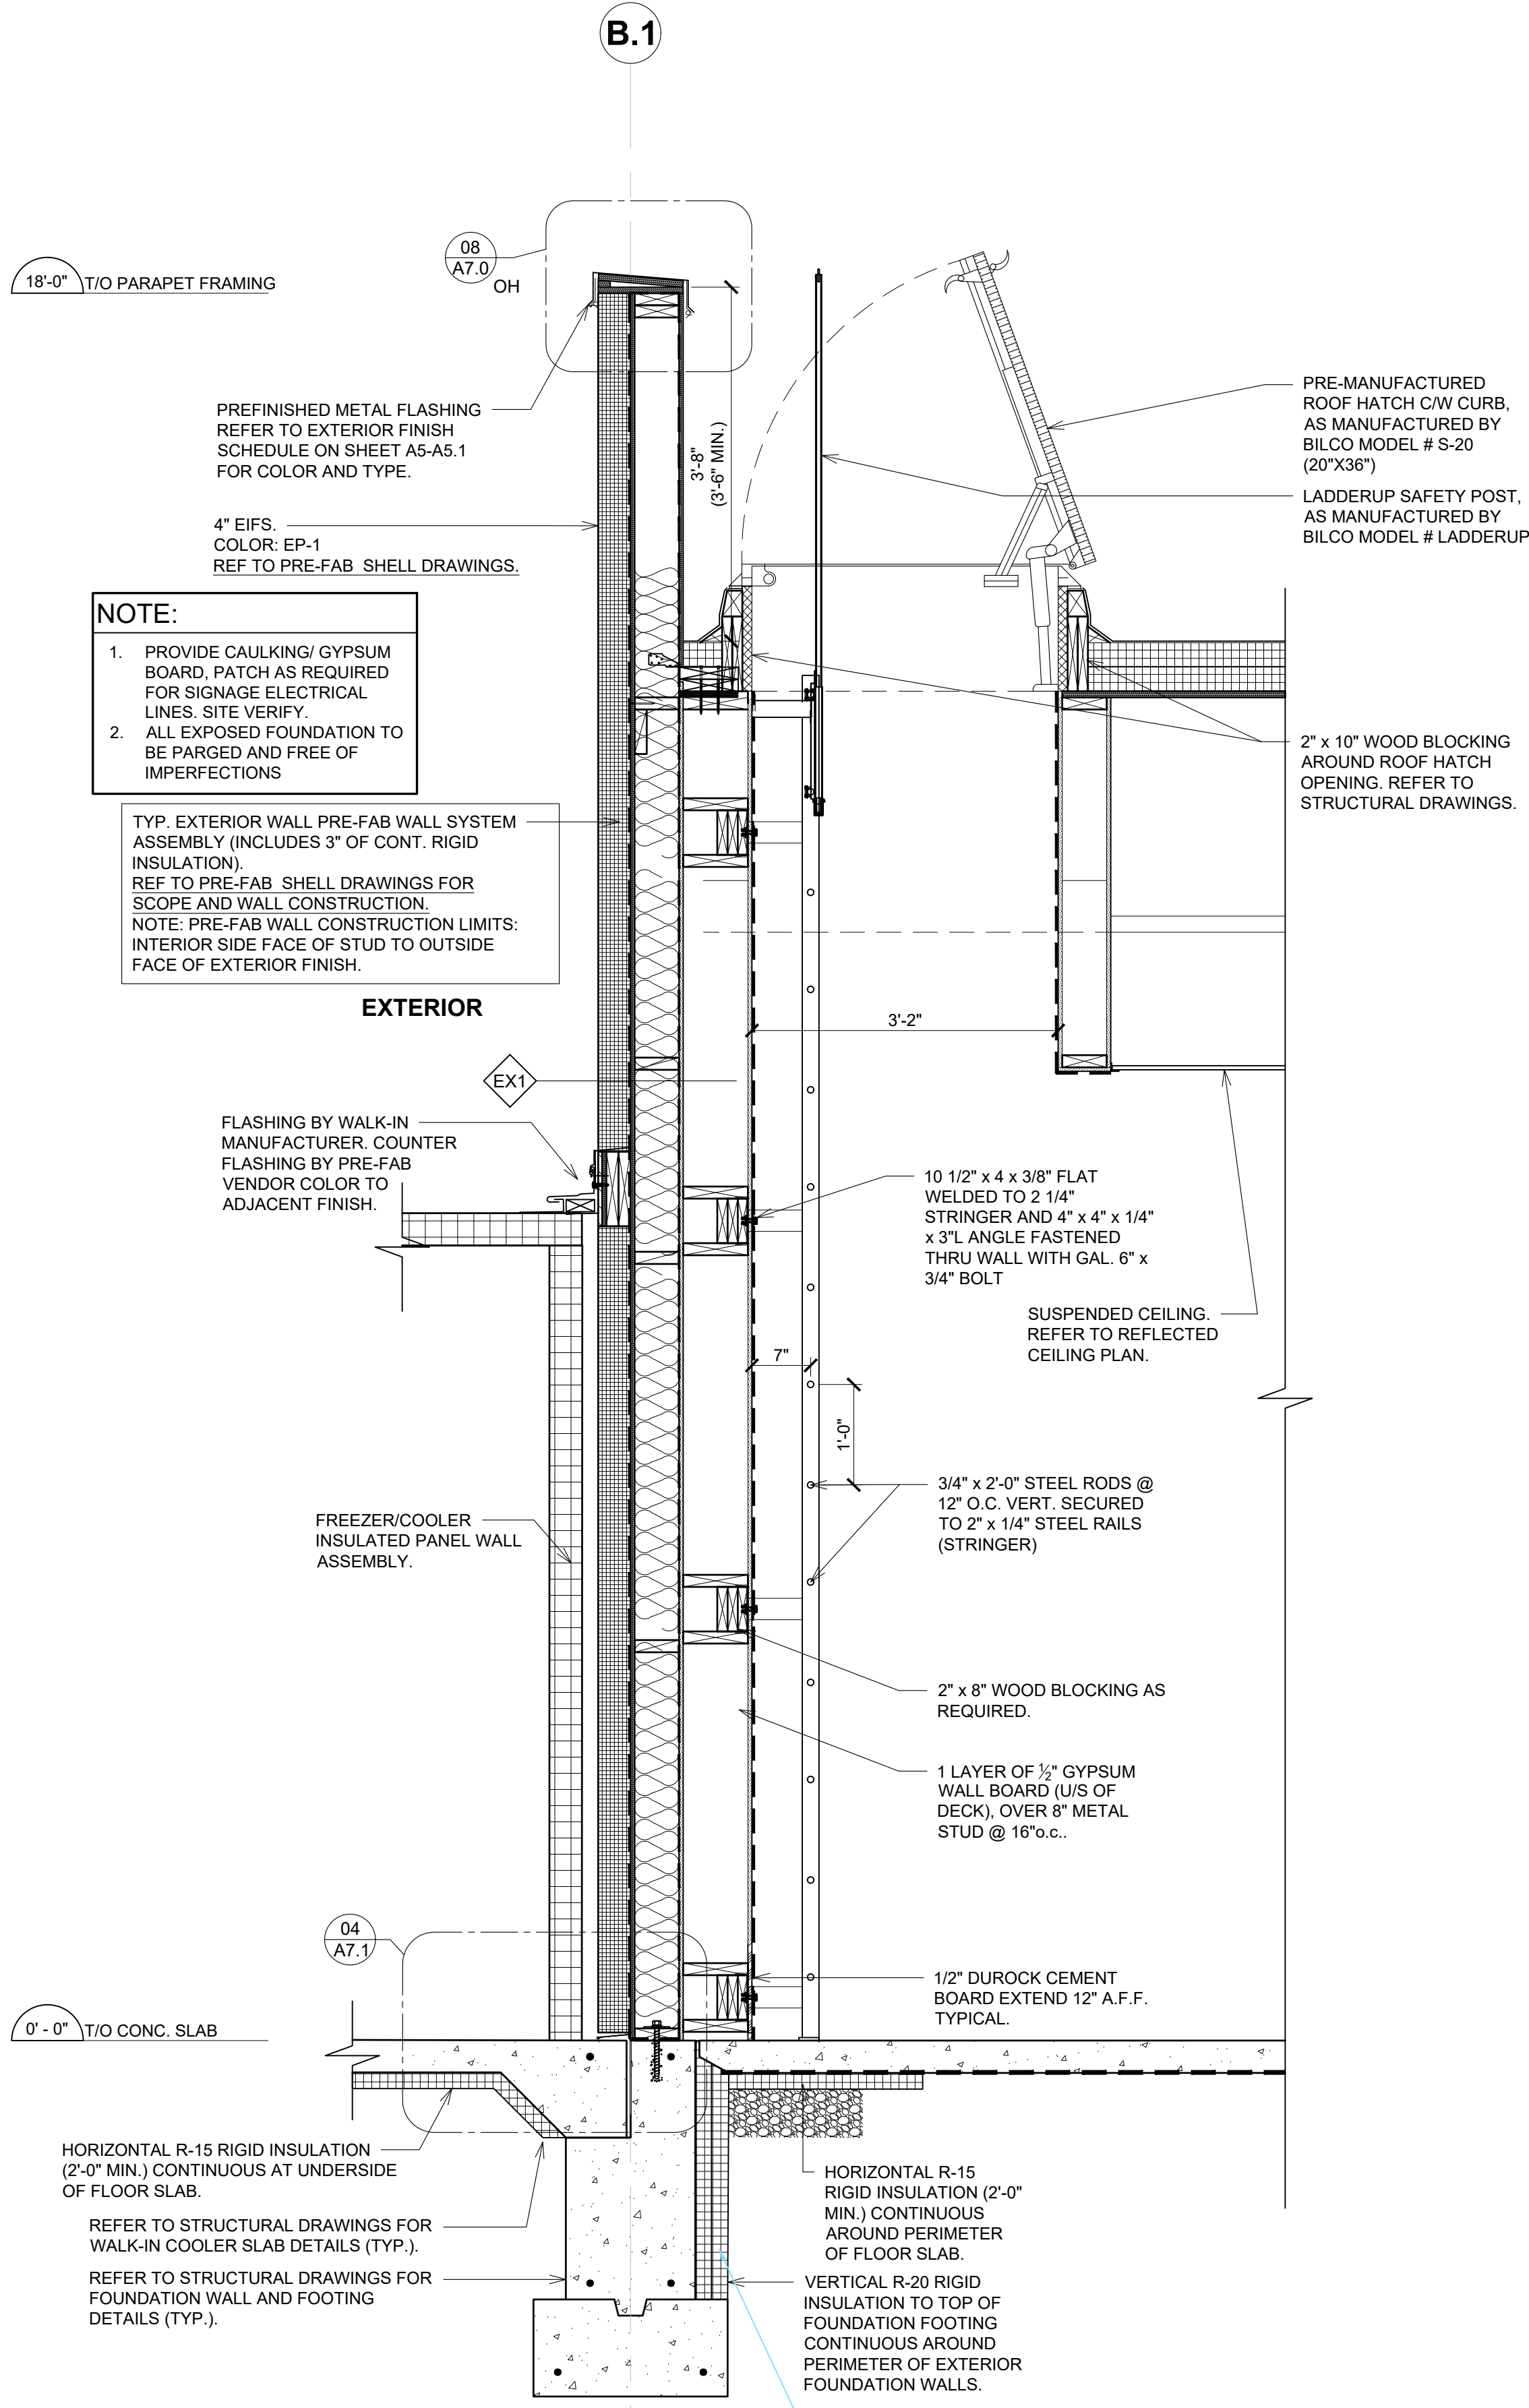

1 WALL SECTION @ ROOF LADDER
A6.3 SCALE: 3/4" = 1'-0"

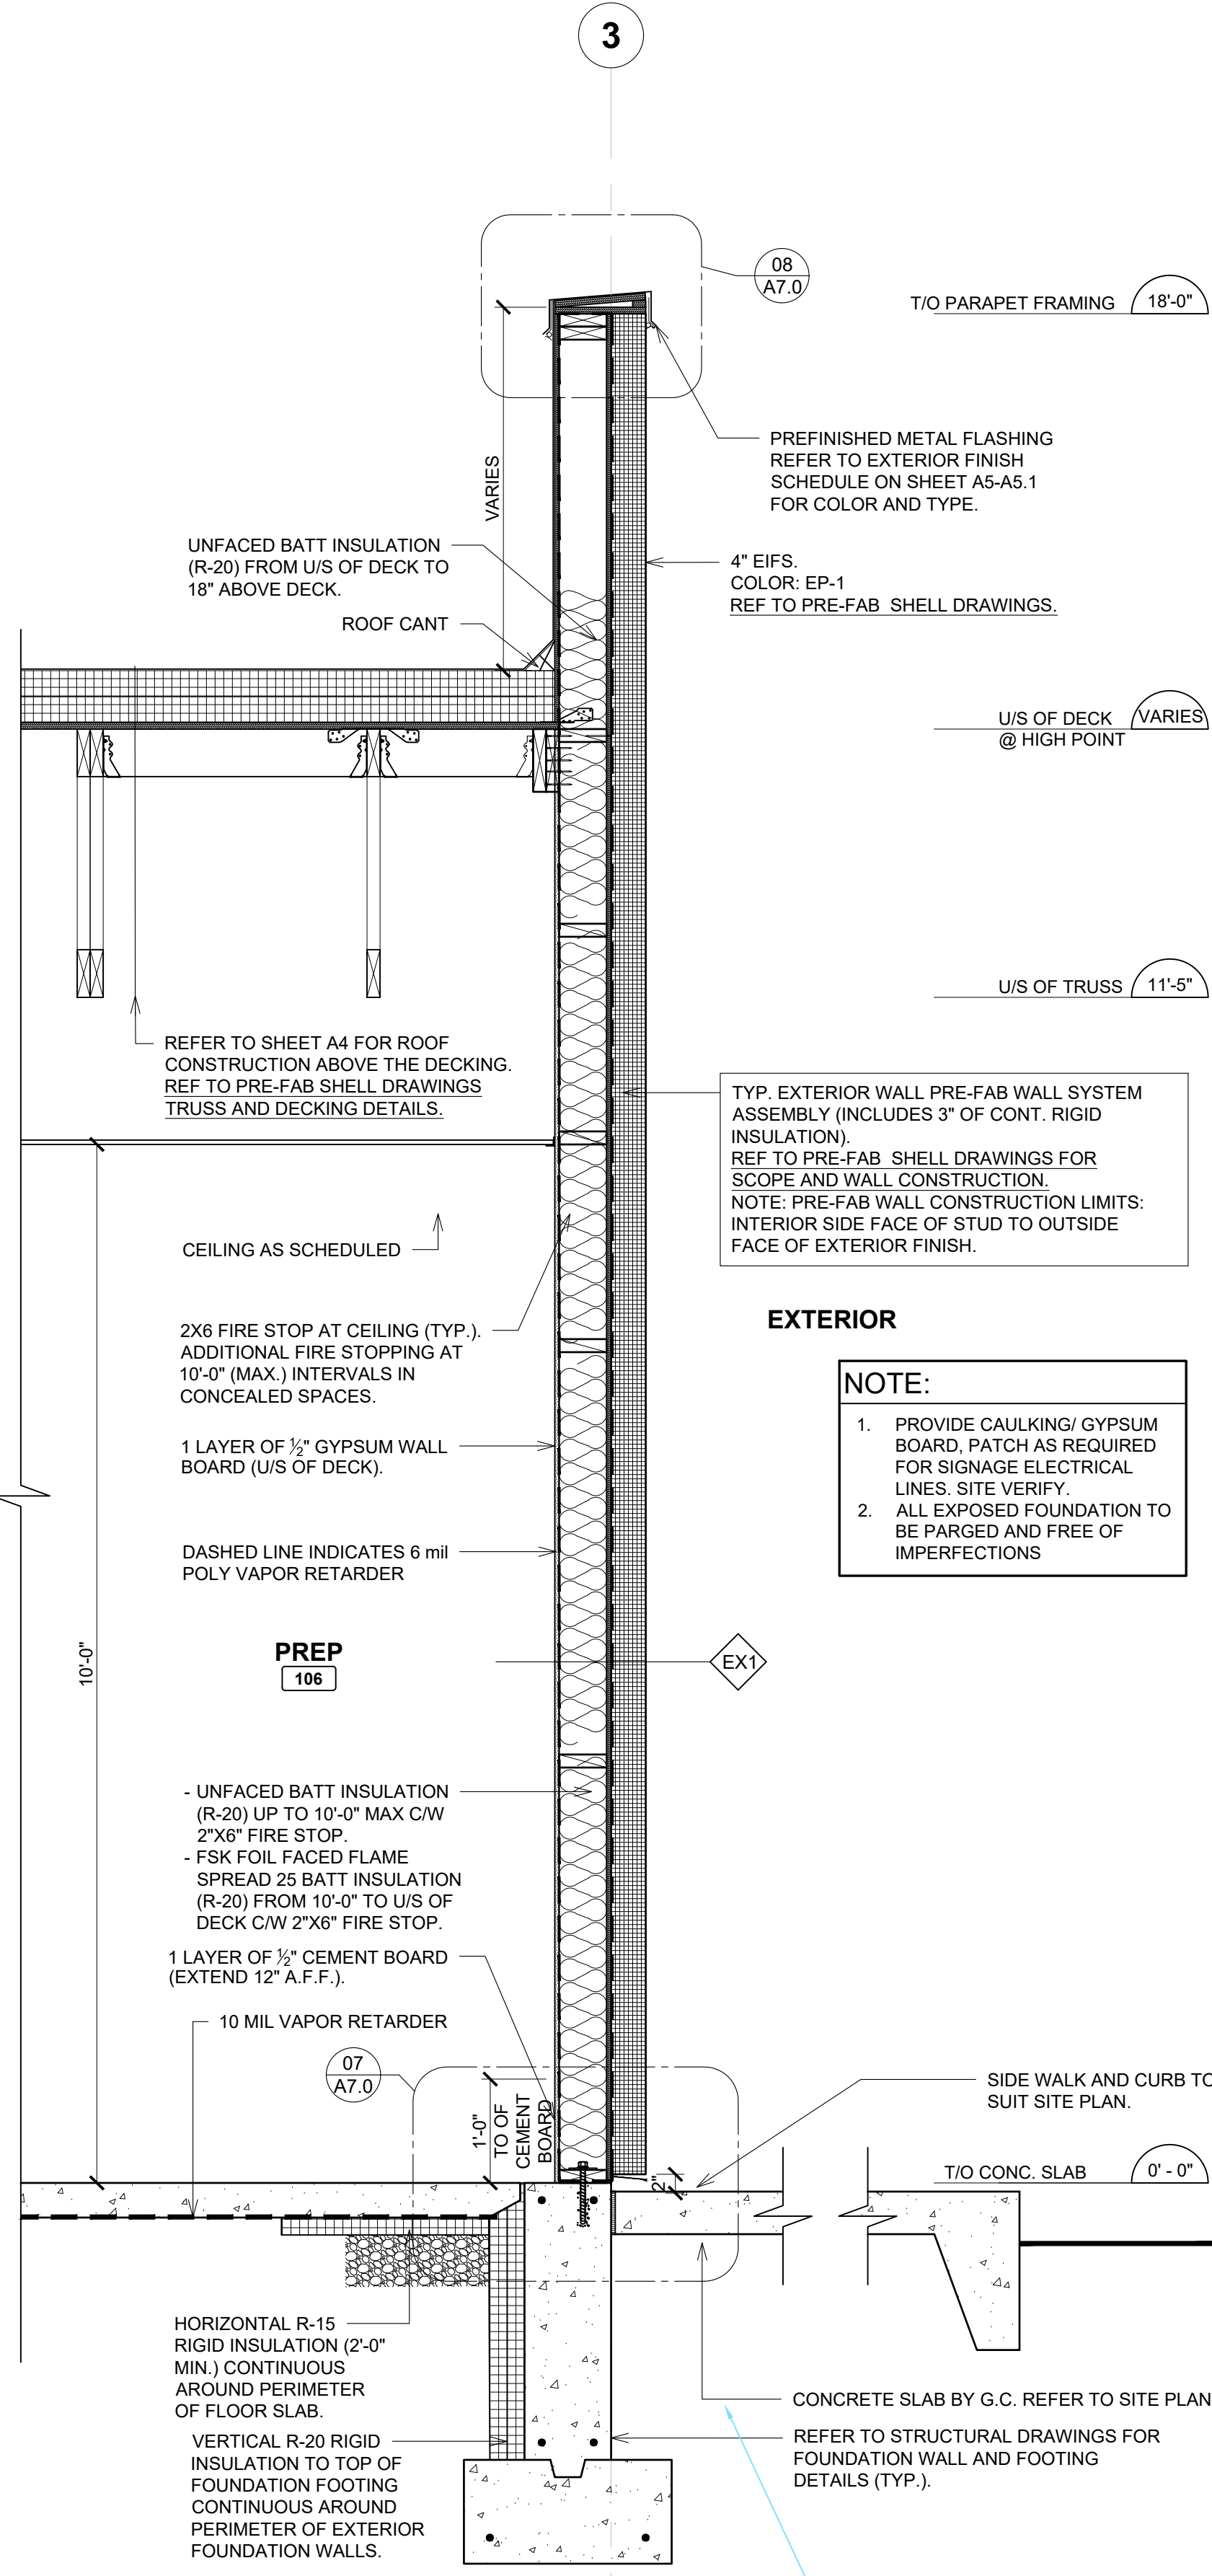


2 WALL SECTION @ REAR
A6.3 SCALE: 3/4" = 1'-0"

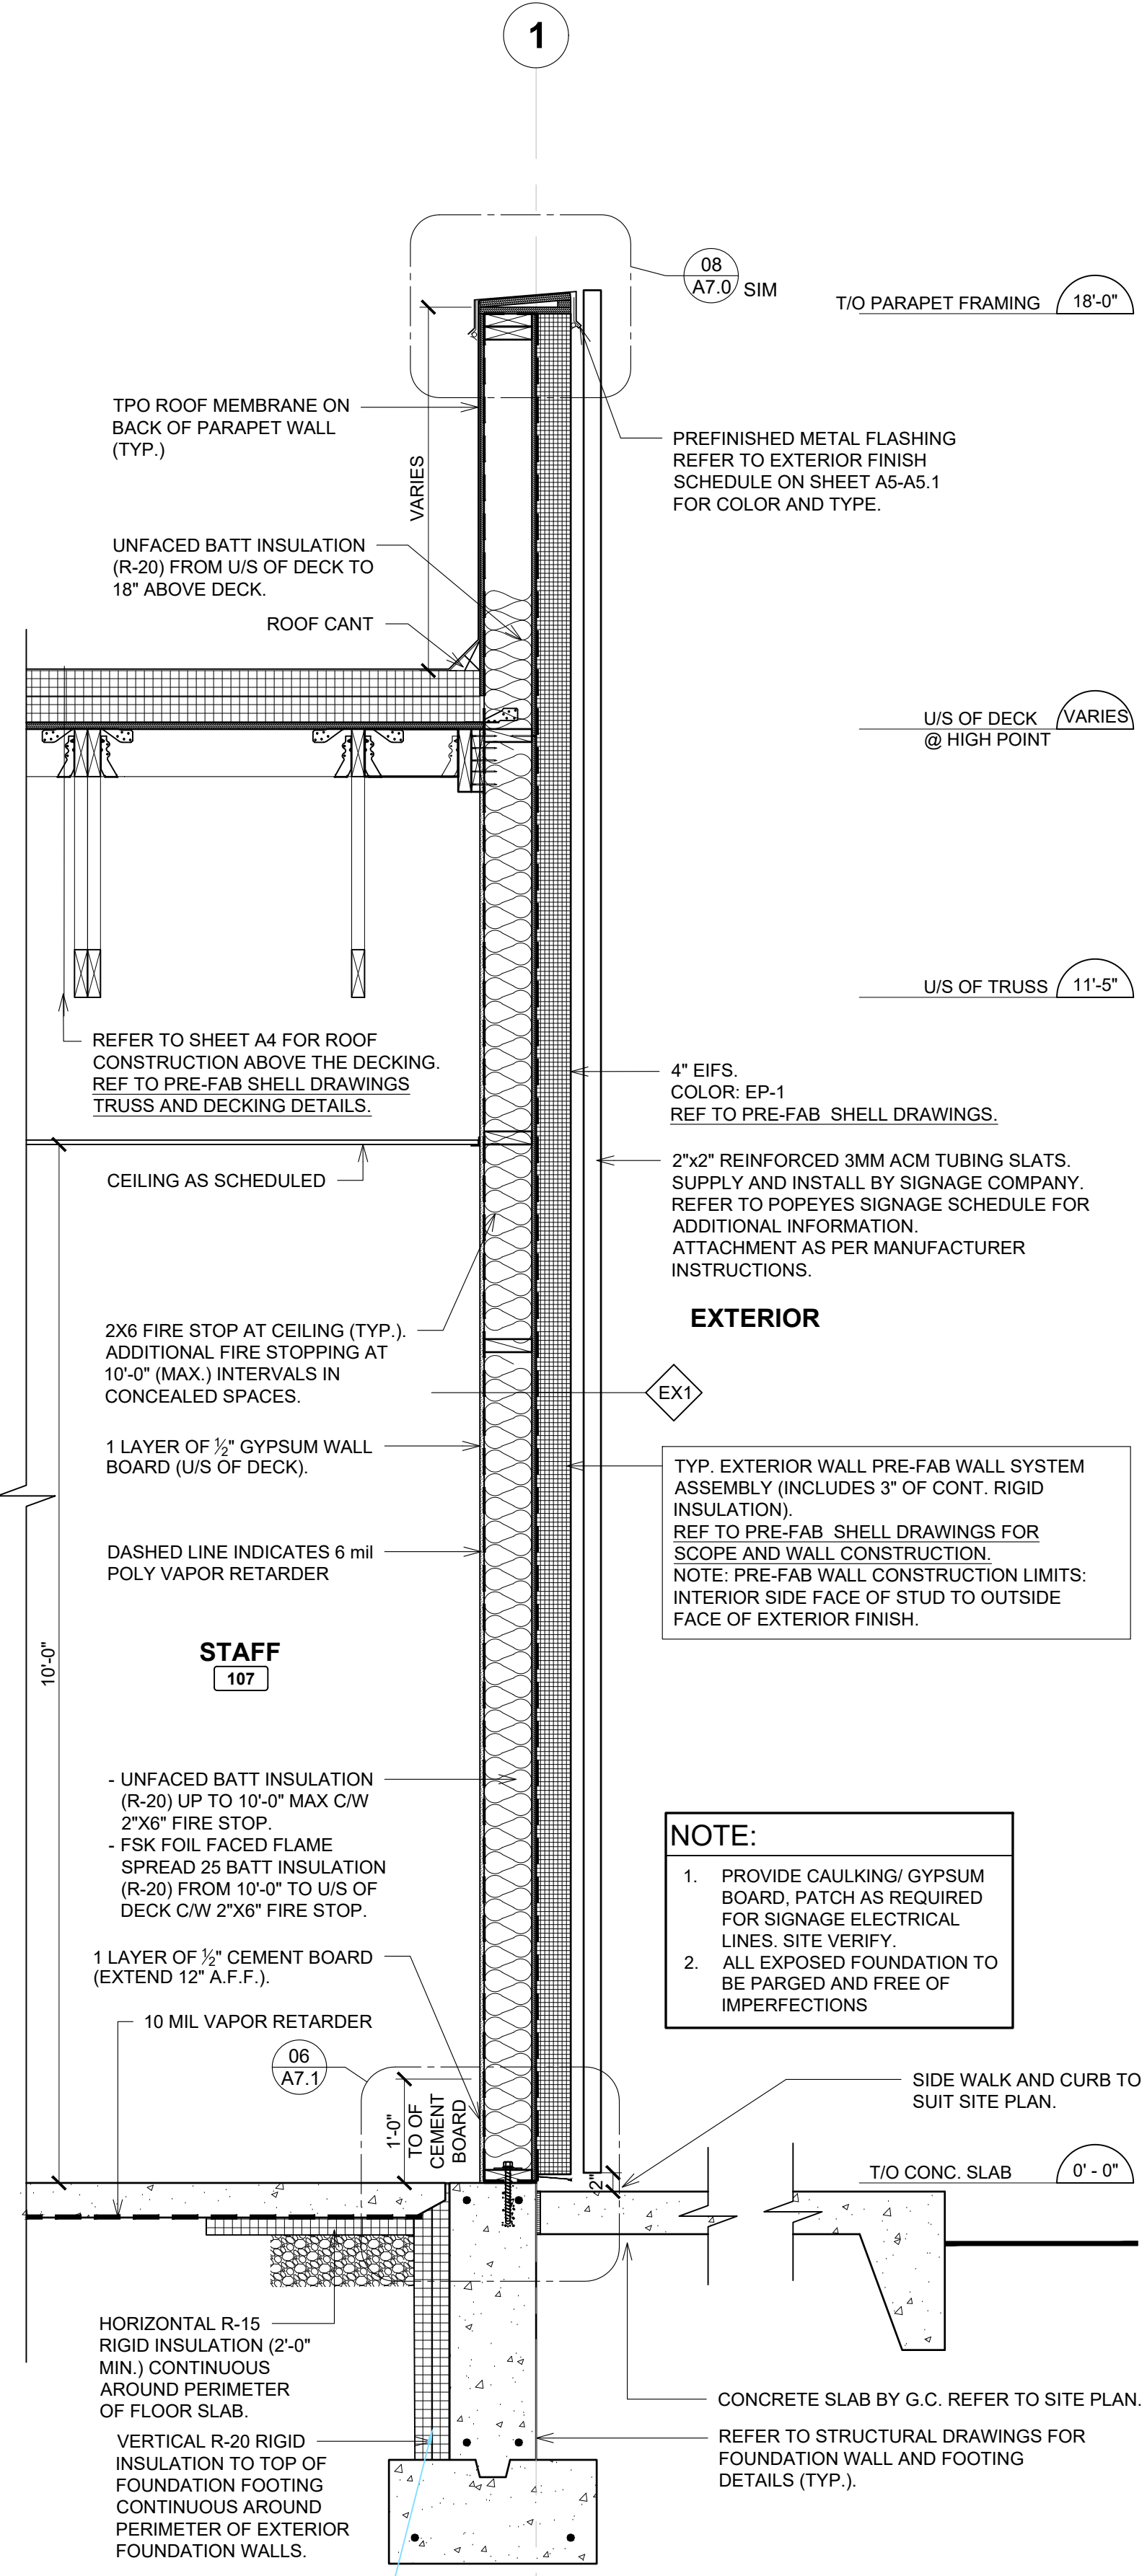


3 WALL SECTION @ FRONT
A6.3 SCALE: 3/4" = 1'-0"


ISSUE TABLE		
No.	Date (mm/dd/yy)	Description
01	09-26-25	DTGO PROTOTYPE DOCUMENTS
REVISIONS		
No.	Date	Description
DRAWINGS REVISED AS PER DESIGN BULLETIN		
No.	Date	Description
THIS DRAWING IS OWNED BY OR LICENSED FOR USE BY POPEYES LOUISIANA KITCHEN (OR ITS AFFILIATED OR RELATED COMPANIES) AND MAY NOT BE REPRODUCED, USED, DOWNLOADED, DISSEMINATED, PUBLISHED, OR TRANSFERRED IN ANY FORM OR BY ANY MEANS, EXCEPT WITH THE PRIOR WRITTEN CONSENT OF POPEYES LOUISIANA KITCHEN. COPYRIGHT INFRINGEMENT IS A VIOLATION OF FEDERAL LAW SUBJECT TO CRIMINAL AND CIVIL PENALTIES.		
THE CONTRACTOR IS TO VERIFY ALL DIMENSIONS AND CONDITIONS ON THE PROJECT AND TO REPORT ANY DISCREPANCIES TO THE POPEYES LOUISIANA KITCHEN REPRESENTATIVE PRIOR TO COMMENCING WORK. THESE DRAWINGS ARE NOT TO BE USED FOR CONSTRUCTION PURPOSES UNLESS INDICATED BY POPEYES LOUISIANA KITCHEN AS "ISSUED FOR CONSTRUCTION".		
Professional Seal		
DESIGNER NOTES: DESIGN GUIDELINE ONLY - NOT FOR PERMIT OR CONSTRUCTION		
THESE DOCUMENTS MUST BE COMPLETED AND / OR MODIFIED BY A LICENSED ARCHITECT AND ENGINEER TO CONFORM TO ALL APPLICABLE CODES, AND SPECIFIC SITE CONDITIONS. THERE IS NO WARRANTY, WHETHER IMPLIED OR EXPRESSED, THAT THESE DOCUMENTS MEET THE APPLICABLE CODE REQUIREMENTS. LIABILITY FOR THE DESIGN AND ANY USE OF THE DOCUMENTS IS THE SOLE RESPONSIBILITY OF THE ARCHITECT AND ENGINEER OF RECORD.		
Company Logo		
Project		
Store Type		
Location		
Drawing Title		
Drawn		
Scale		
Project No.		
Checked		
Date		
Drawing No.		

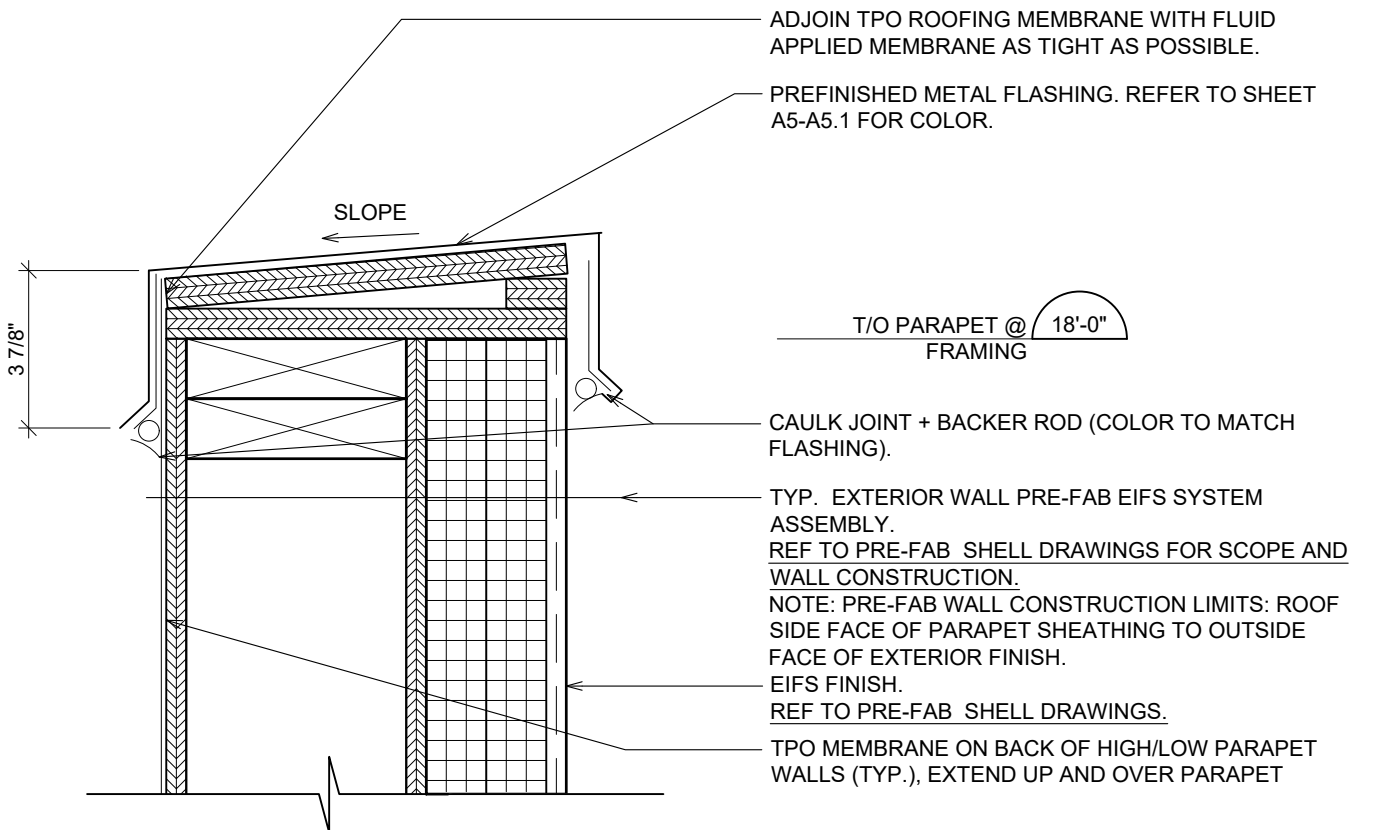


08 SECTION DETAIL @ PARAPET
A7.0 SCALE: 2-1/2" = 1' - 0"

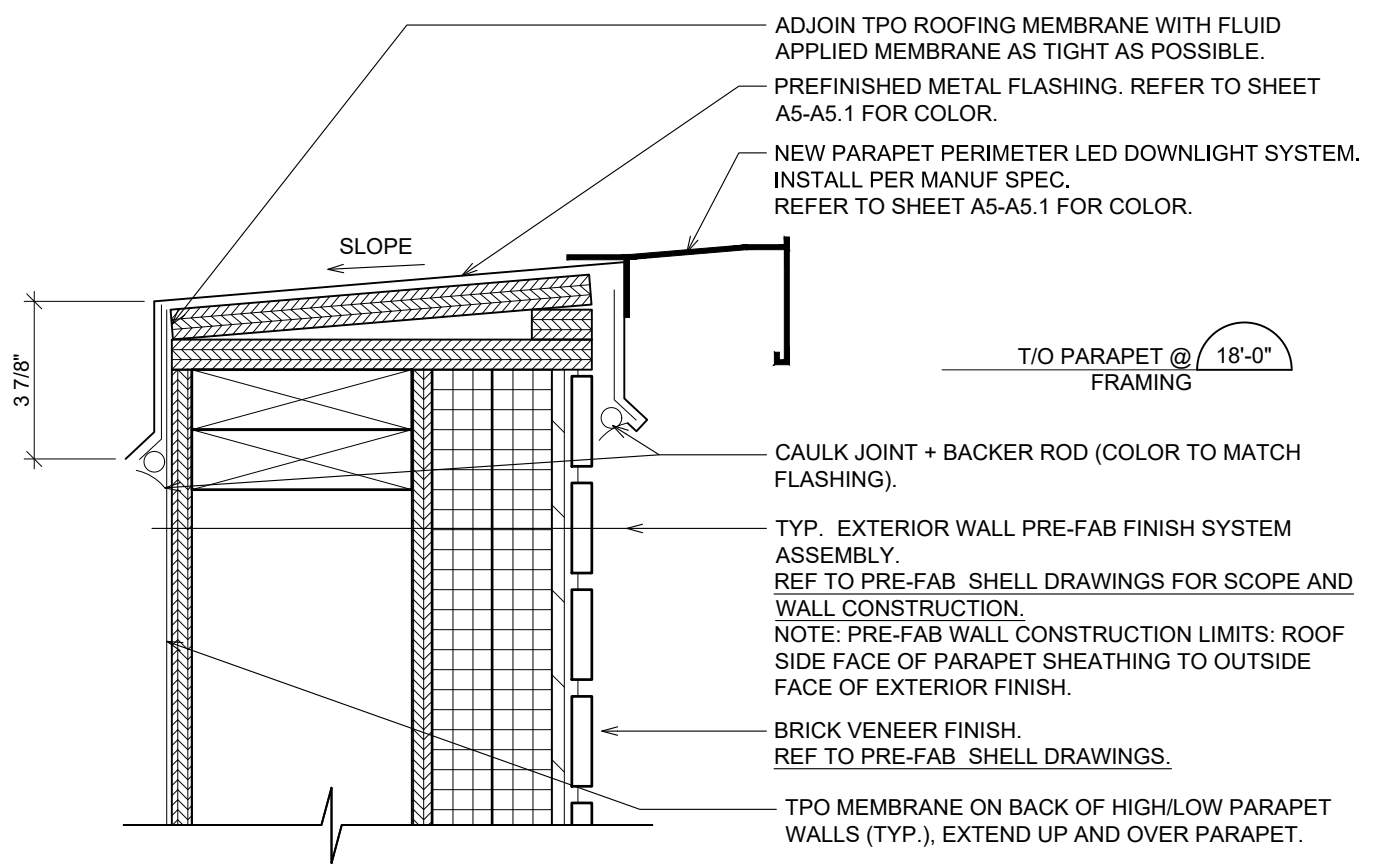


06 SECTION DETAIL @ PARAPET
A7.0 SCALE: 2-1/2" = 1' - 0"

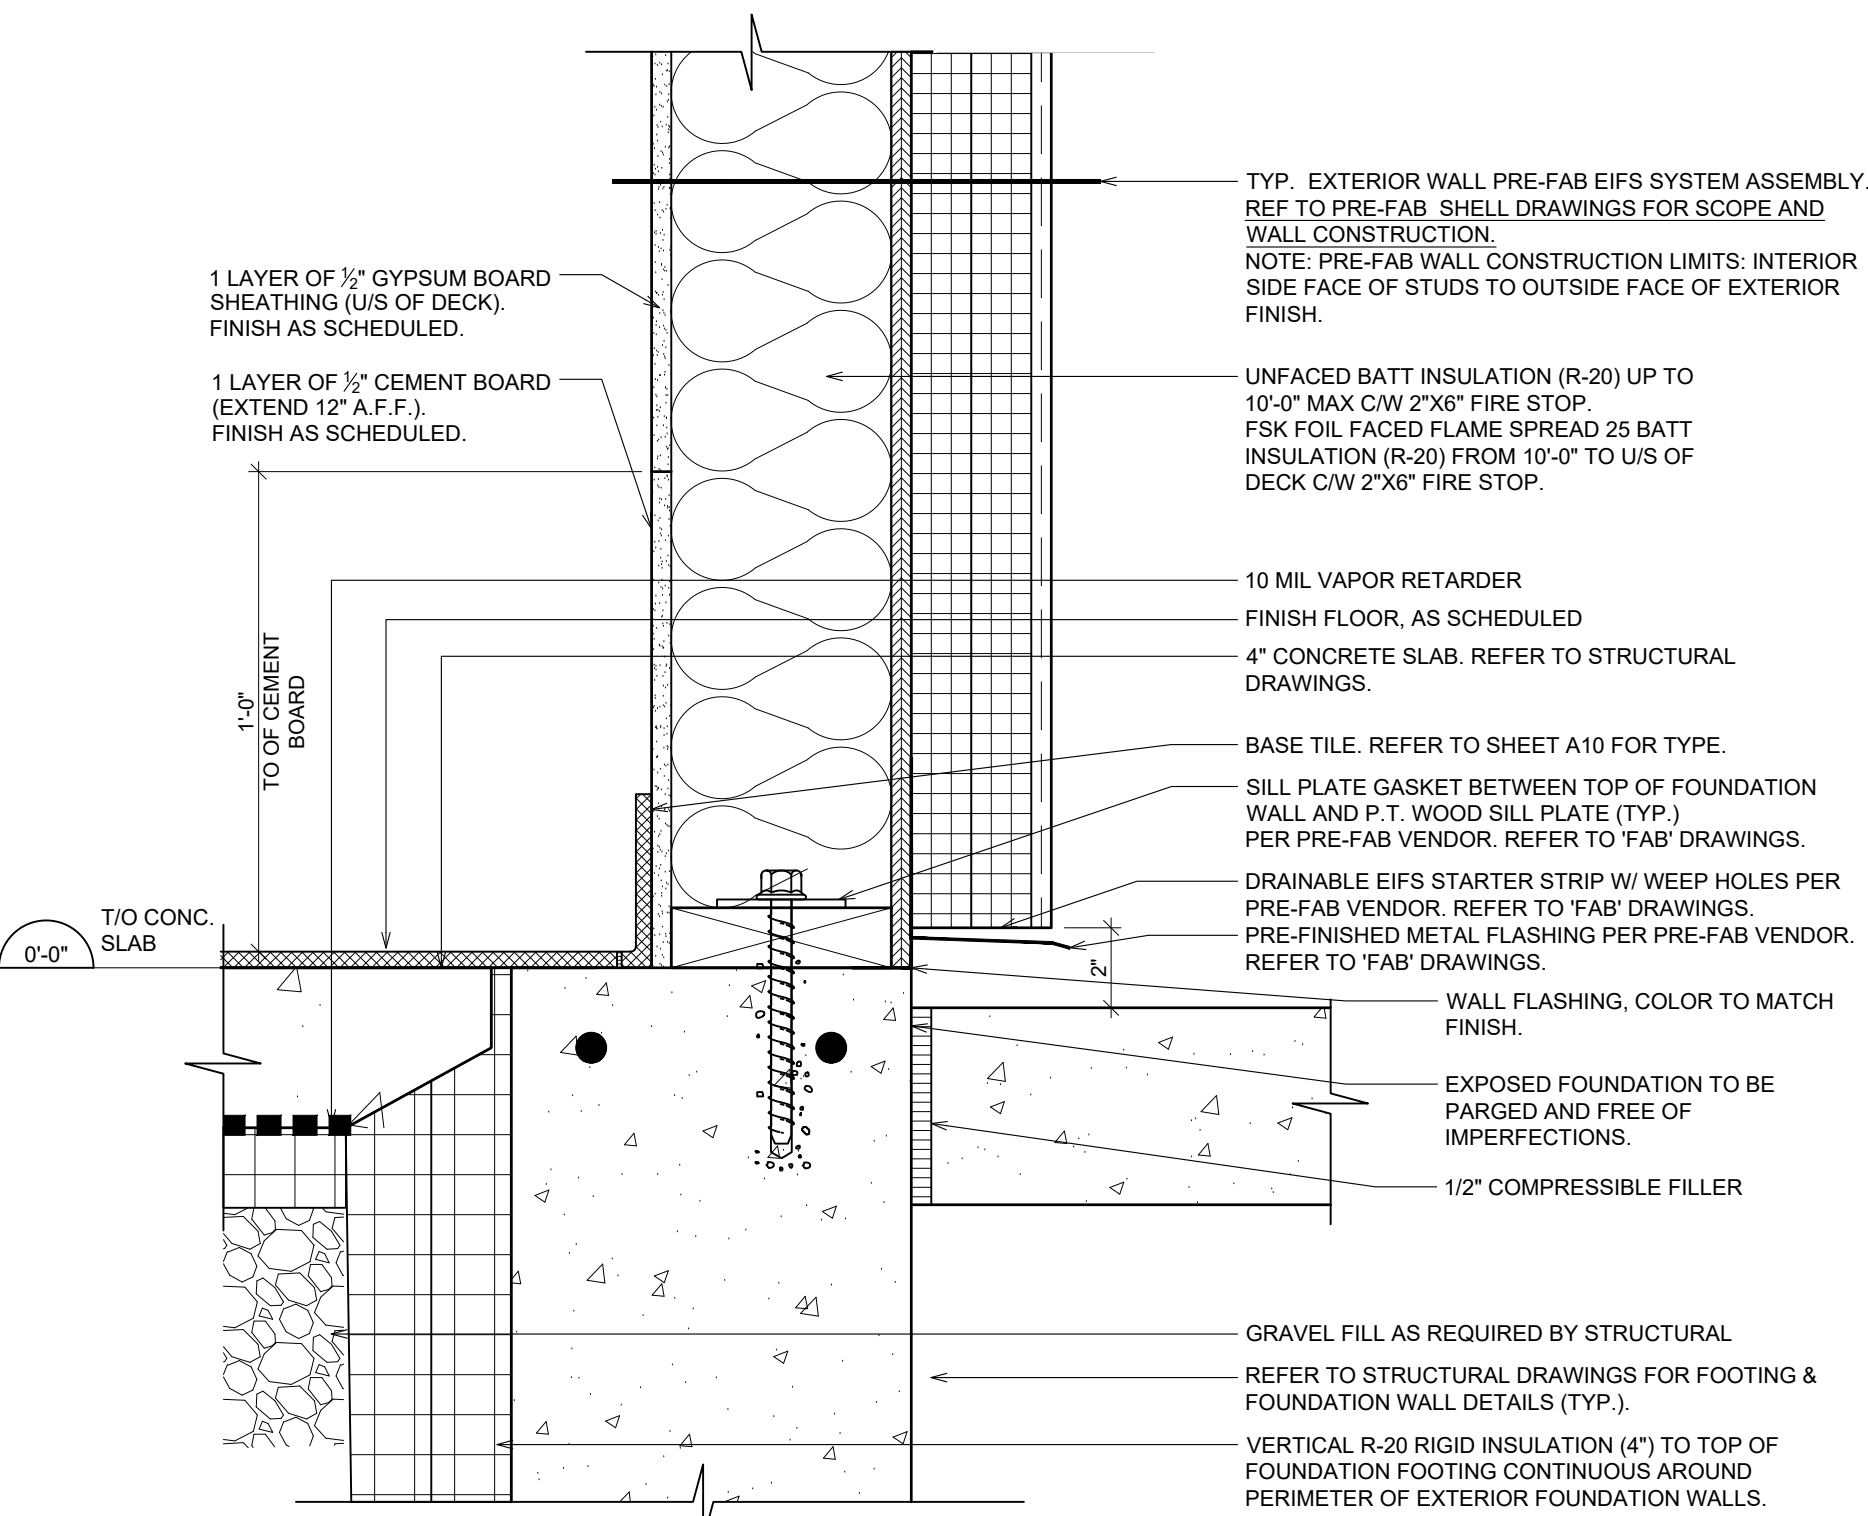


07 SECTION DETAIL @ WALL BASE
A7.0 SCALE: 2-1/2" = 1' - 0"

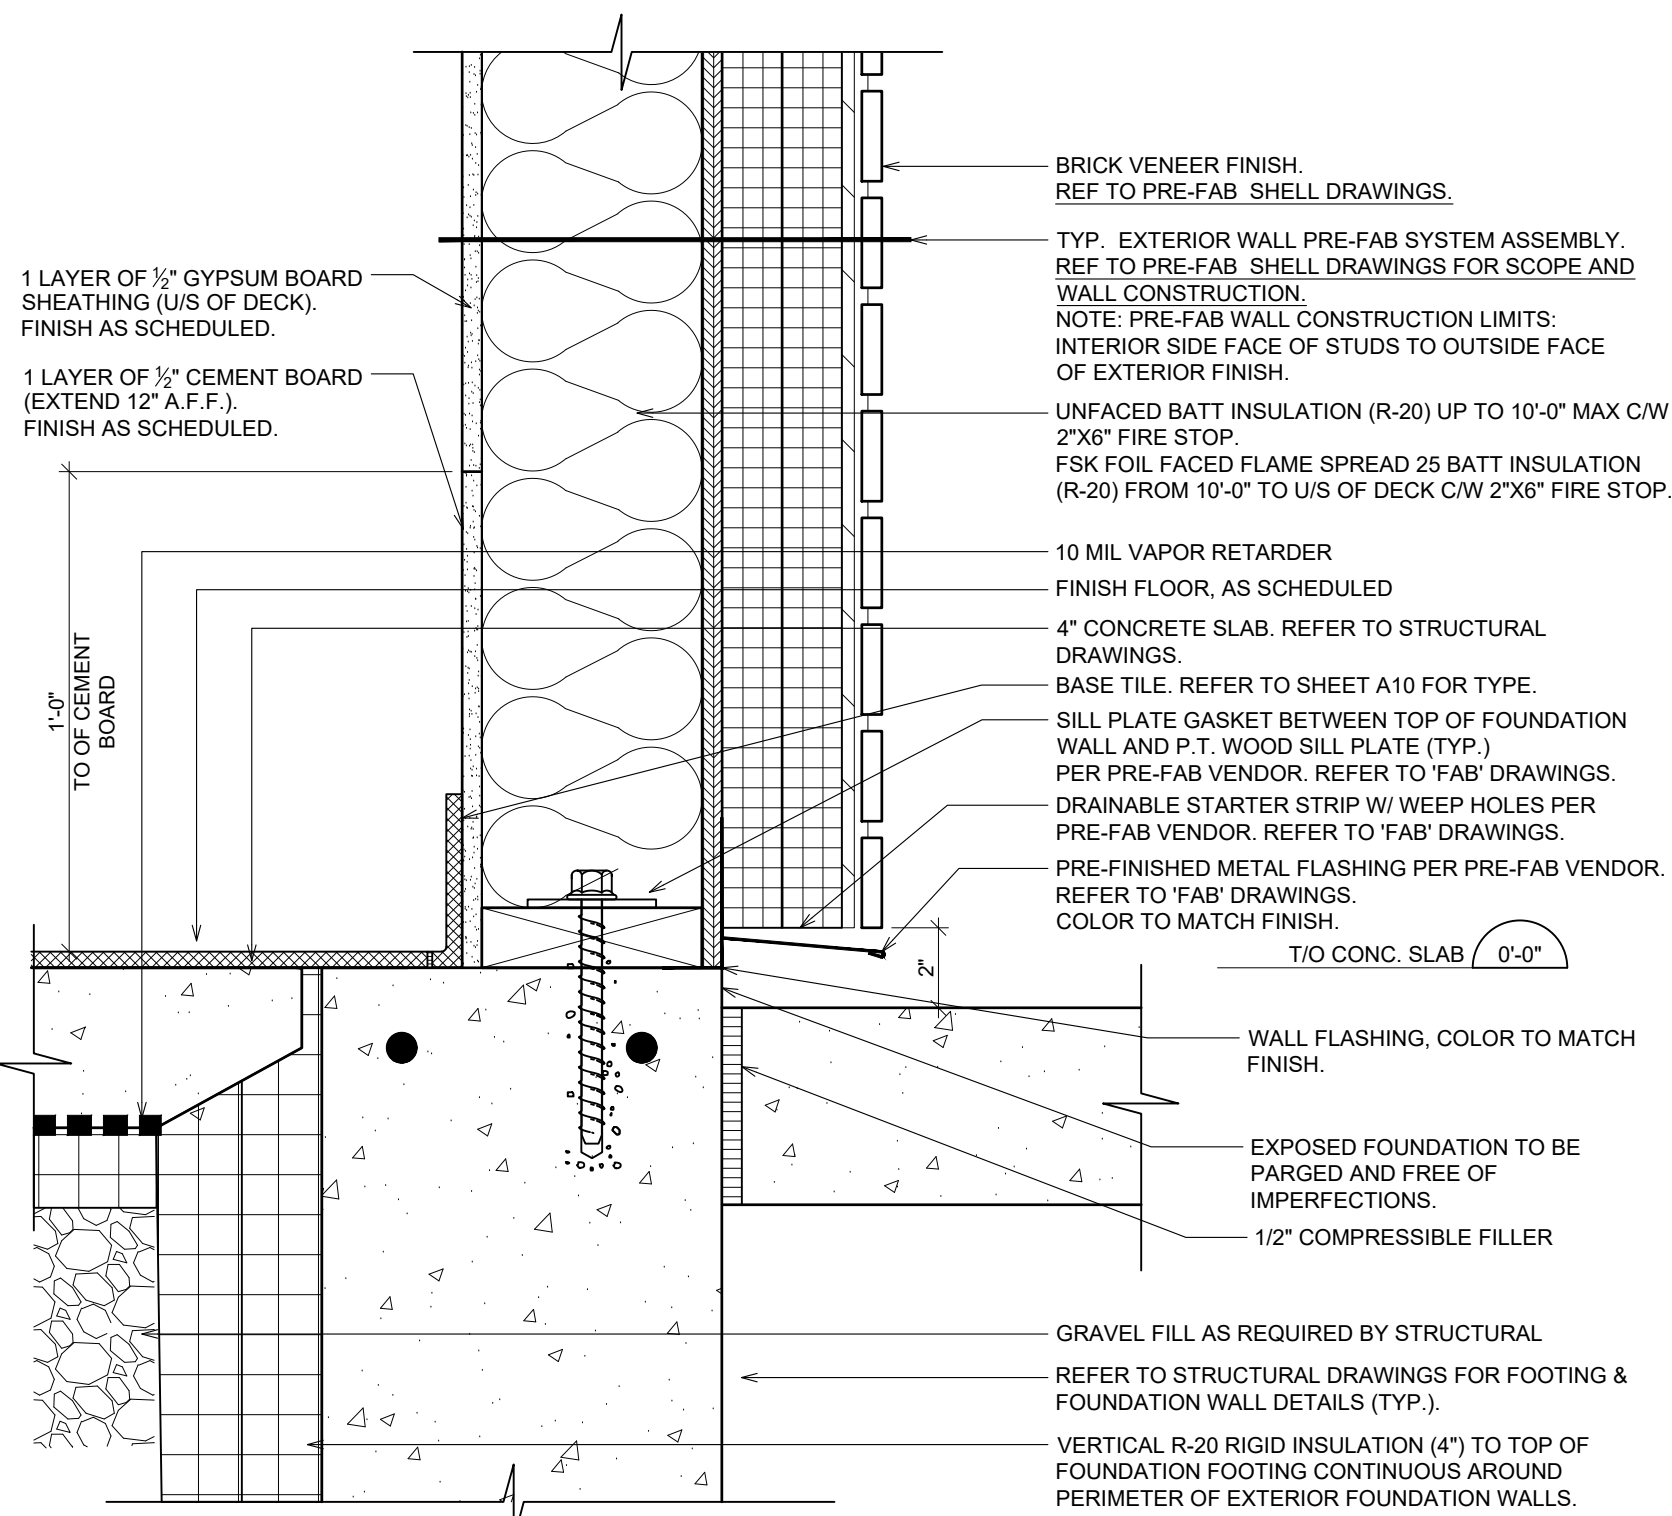


05 SECTION DETAIL @ WALL BASE
A7.0 SCALE: 2-1/2" = 1' - 0"

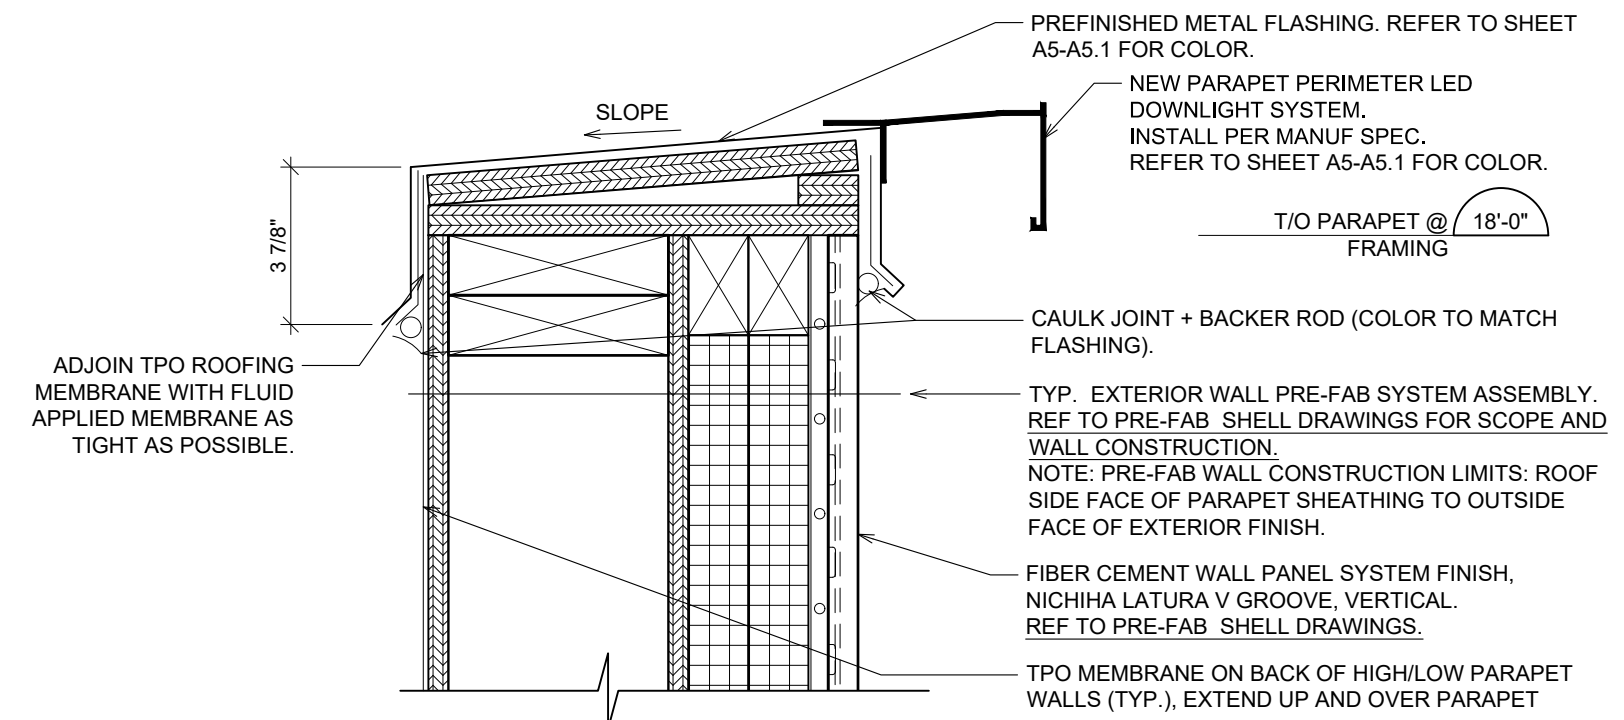


04 SECTION DETAIL @ PARAPET
A7.0 SCALE: 2-1/2" = 1' - 0"

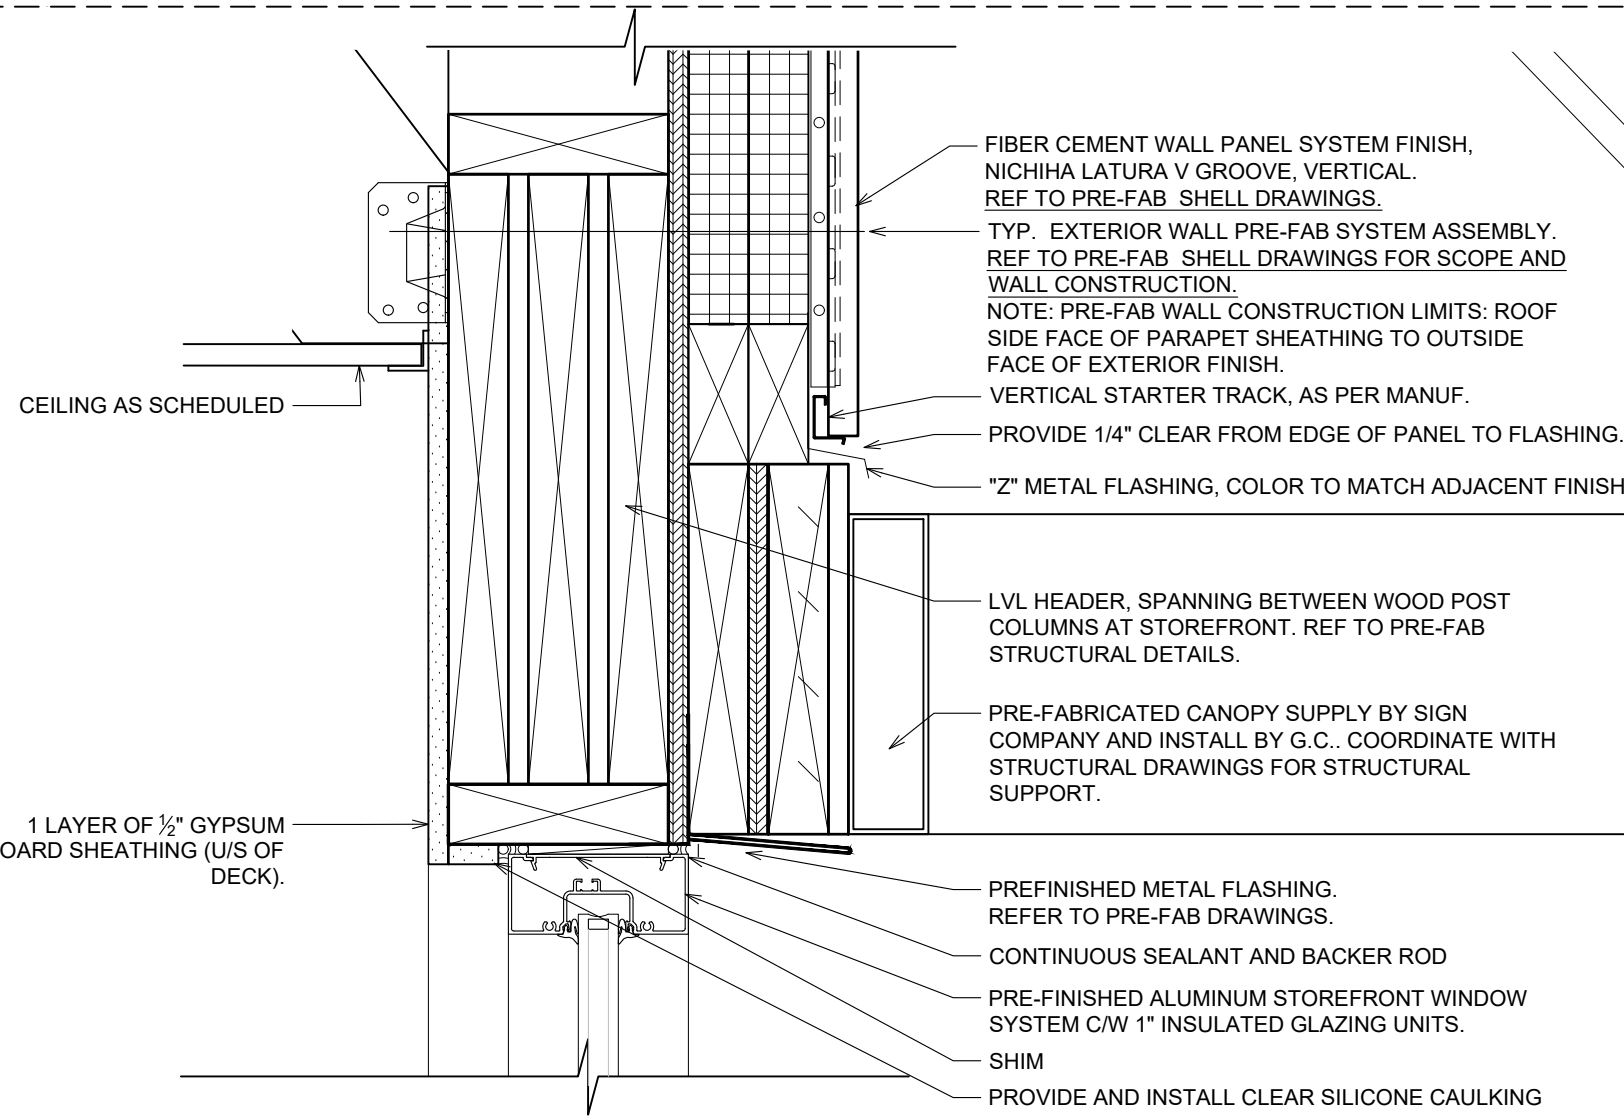

03 SECTION DETAIL @ STOREFRONT HEAD
A7.0 SCALE: 2-1/2" = 1' - 0"



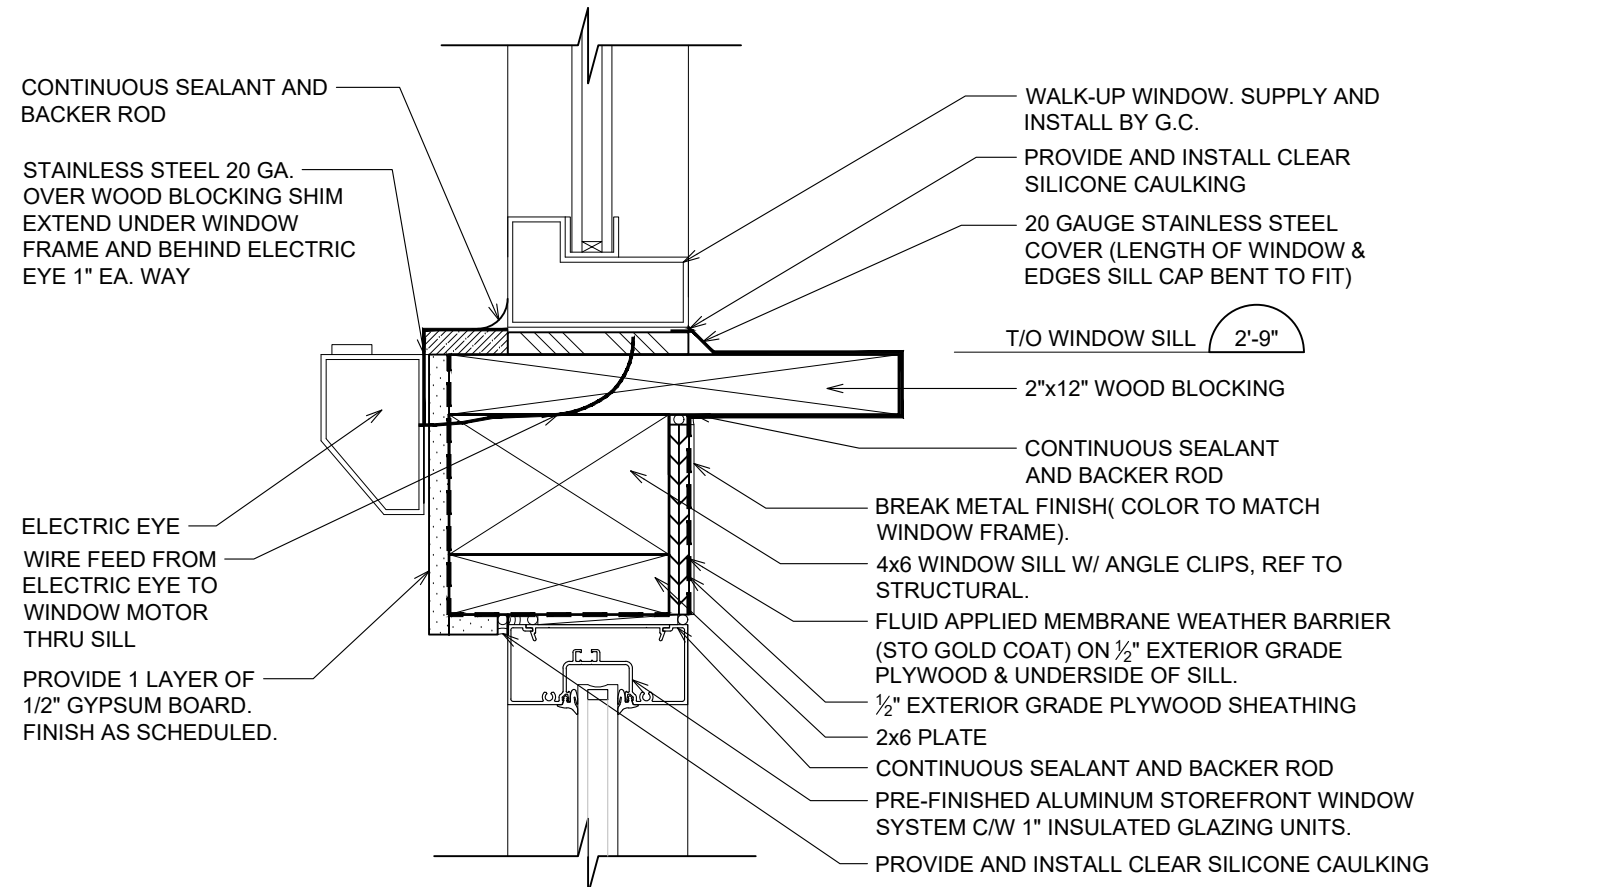



02 SECTION DETAIL @ WALK-UP WINDOW
A7.0 SCALE: 2-1/2" = 1' - 0"

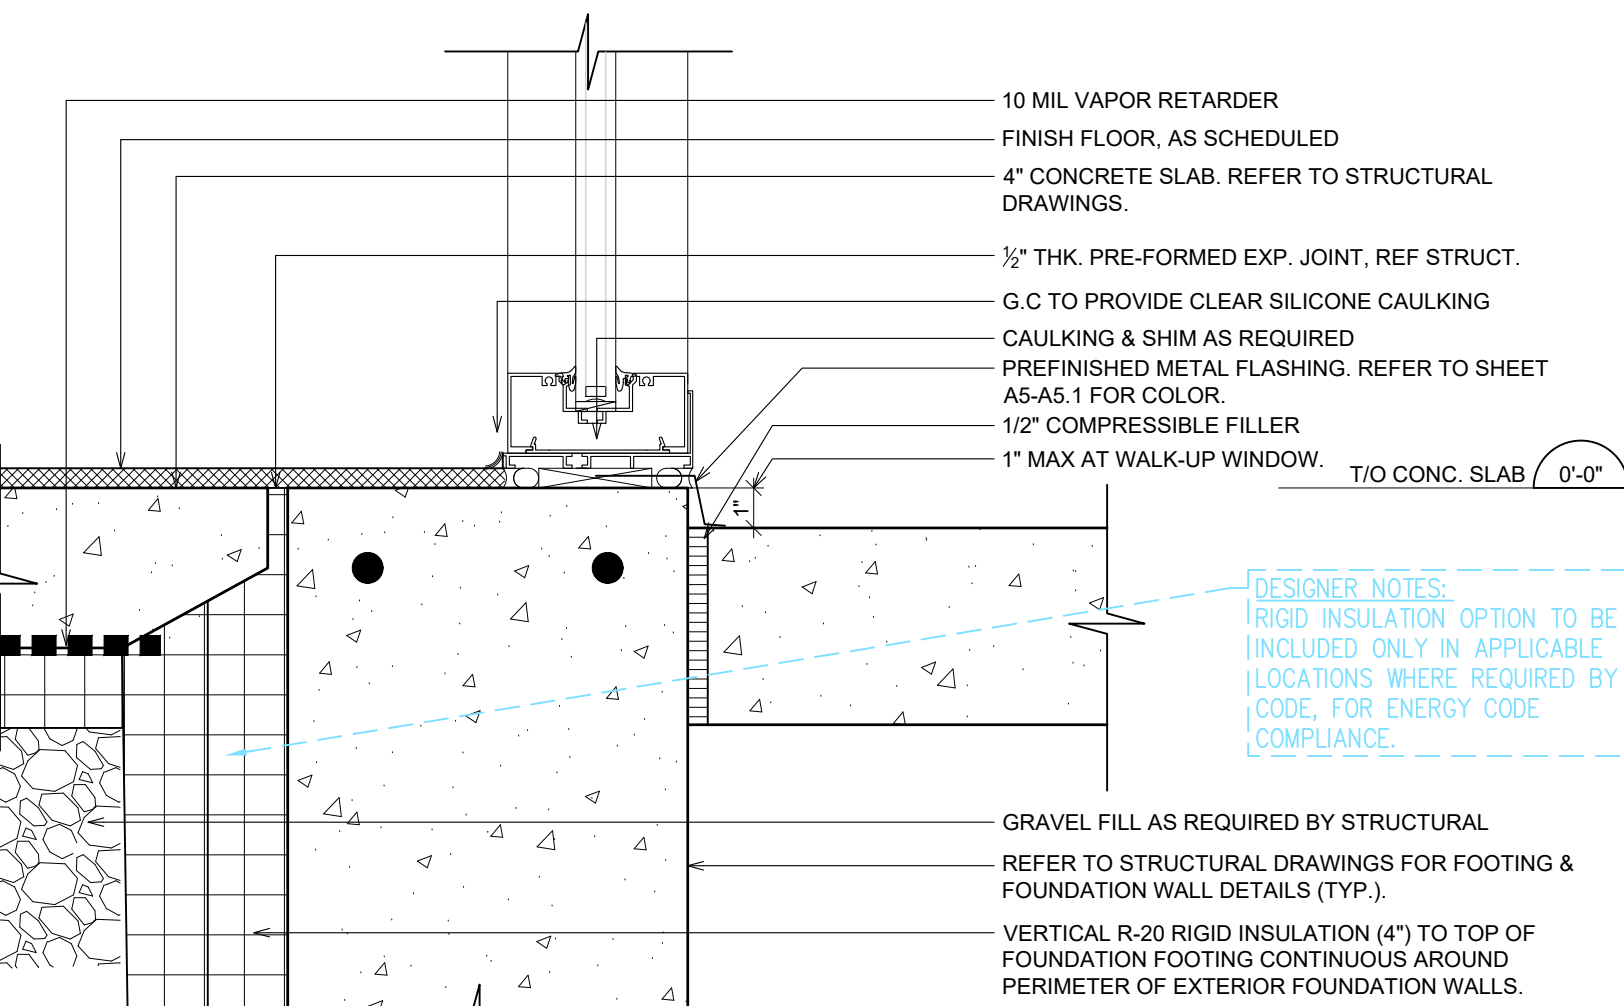


01 SECTION DETAIL @ STOREFRONT BASE
A7.0 SCALE: 2-1/2" = 1' - 0"

ISSUE TABLE		
No.	Date (mm/dd/yy)	Description
01	09-26-25	DTGO PROTOTYPE DOCUMENTS
REVISIONS		
No.	Date	Description
DRAWINGS REVISED AS PER DESIGN BULLETIN		
No.	Date	Description
THIS DRAWING IS OWNED BY OR LICENSED FOR USE BY POPEYES LOUISIANA KITCHEN (OR ITS AFFILIATED OR RELATED COMPANIES) AND MAY NOT BE REPRODUCED, USED, DOWNLOADED, DISSEMINATED, PUBLISHED, OR TRANSFERRED IN ANY FORM OR BY ANY MEANS, EXCEPT WITH THE PRIOR WRITTEN CONSENT OF POPEYES LOUISIANA KITCHEN. COPYRIGHT INFRINGEMENT IS A VIOLATION OF FEDERAL LAW SUBJECT TO CRIMINAL AND CIVIL PENALTIES.		
THE CONTRACTOR IS TO VERIFY ALL DIMENSIONS AND CONDITIONS ON THE PROJECT AND TO REPORT ANY DISCREPANCIES TO THE POPEYES LOUISIANA KITCHEN REPRESENTATIVE PRIOR TO COMMENCING WORK. THESE DRAWINGS ARE NOT TO BE USED FOR CONSTRUCTION PURPOSES UNLESS INDICATED BY POPEYES LOUISIANA KITCHEN AS "ISSUED FOR CONSTRUCTION".		
Professional Seal		
DESIGNER NOTES: DESIGN GUIDELINE ONLY - NOT FOR PERMIT OR CONSTRUCTION		
THESE DOCUMENTS MUST BE COMPLETED AND / OR MODIFIED BY A LICENSED ARCHITECT AND ENGINEER TO CONFORM TO ALL APPLICABLE CODES, AND SPECIFIC SITE CONDITIONS. THERE IS NO WARRANTY, WHETHER IMPLIED OR EXPRESSED THAT THESE DOCUMENTS MEET THE APPLICABLE CODE REQUIREMENTS. LIABILITY FOR THE DESIGN AND ANY USE OF THE DOCUMENTS IS THE SOLE RESPONSIBILITY OF THE ARCHITECT AND ENGINEER OF RECORD.		
Company Logo		
Project		
Store Type		
Location		
Drawing Title		
Drawn		
Checked		
Scale		
Date		
Project No.		
Drawing No.		

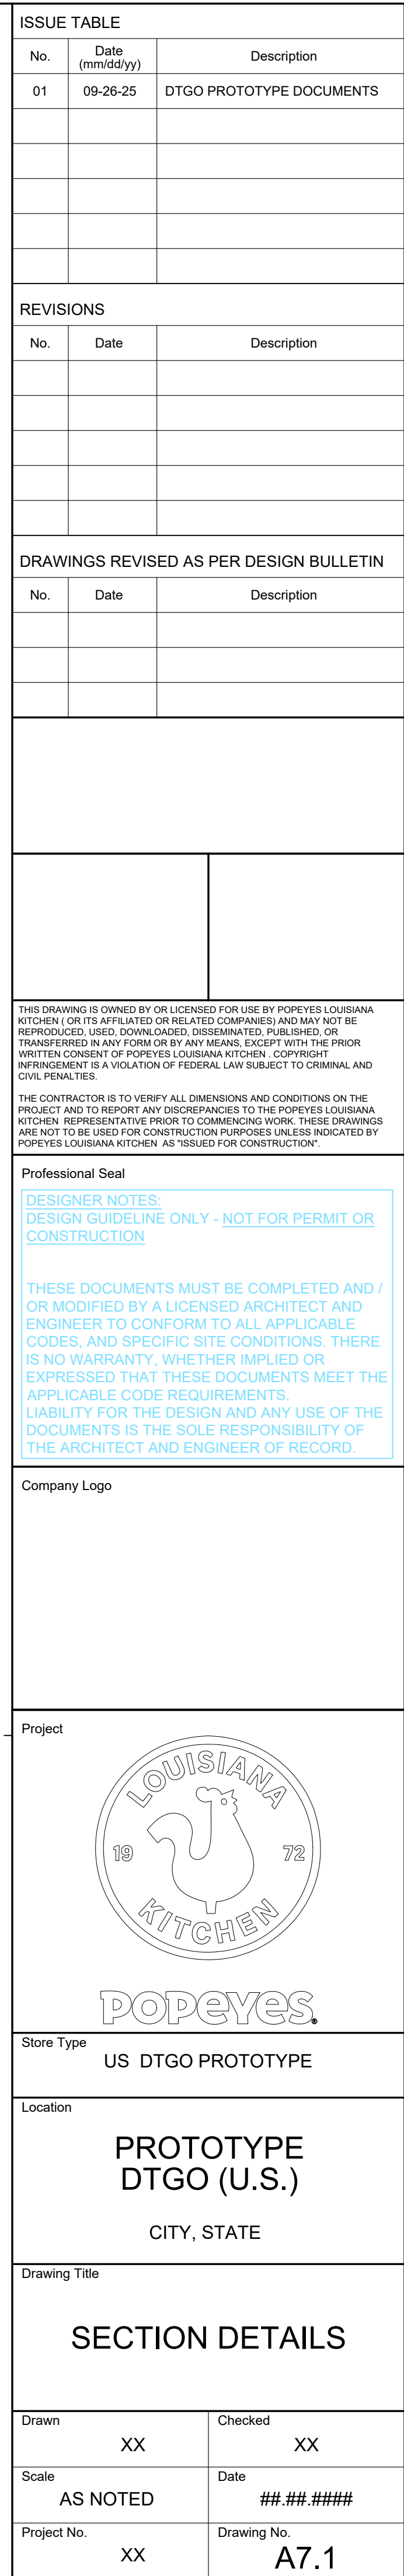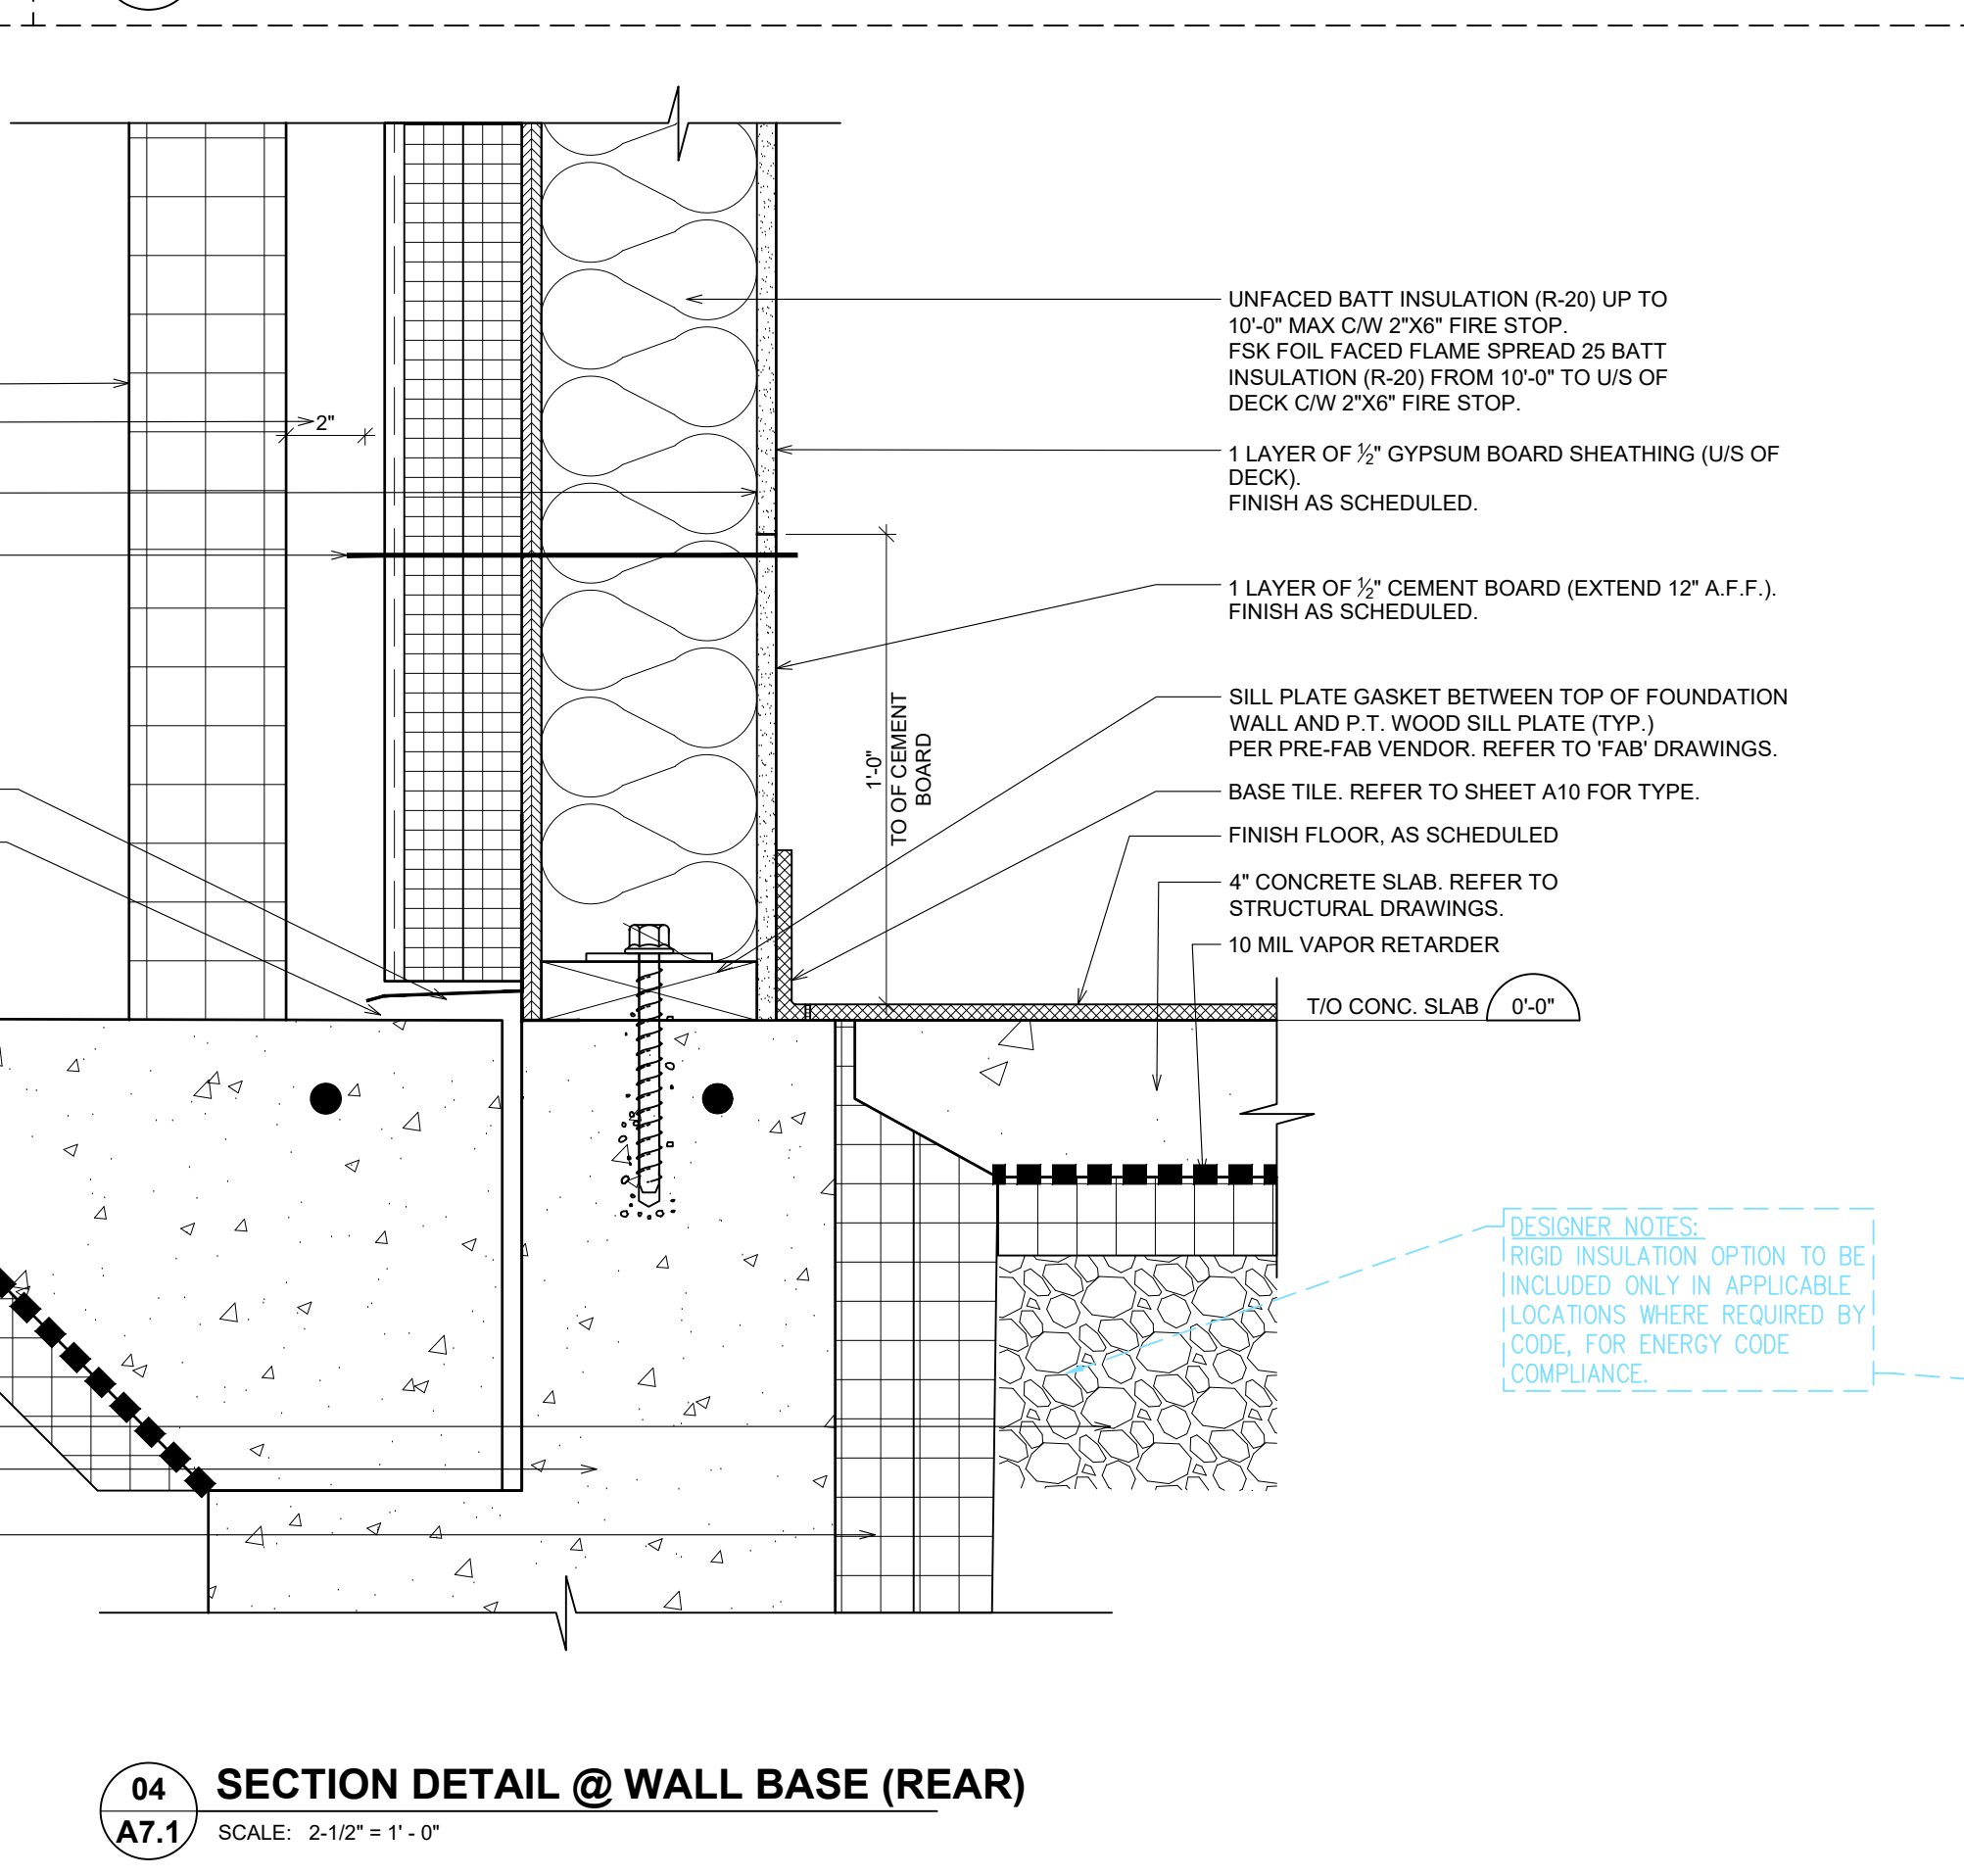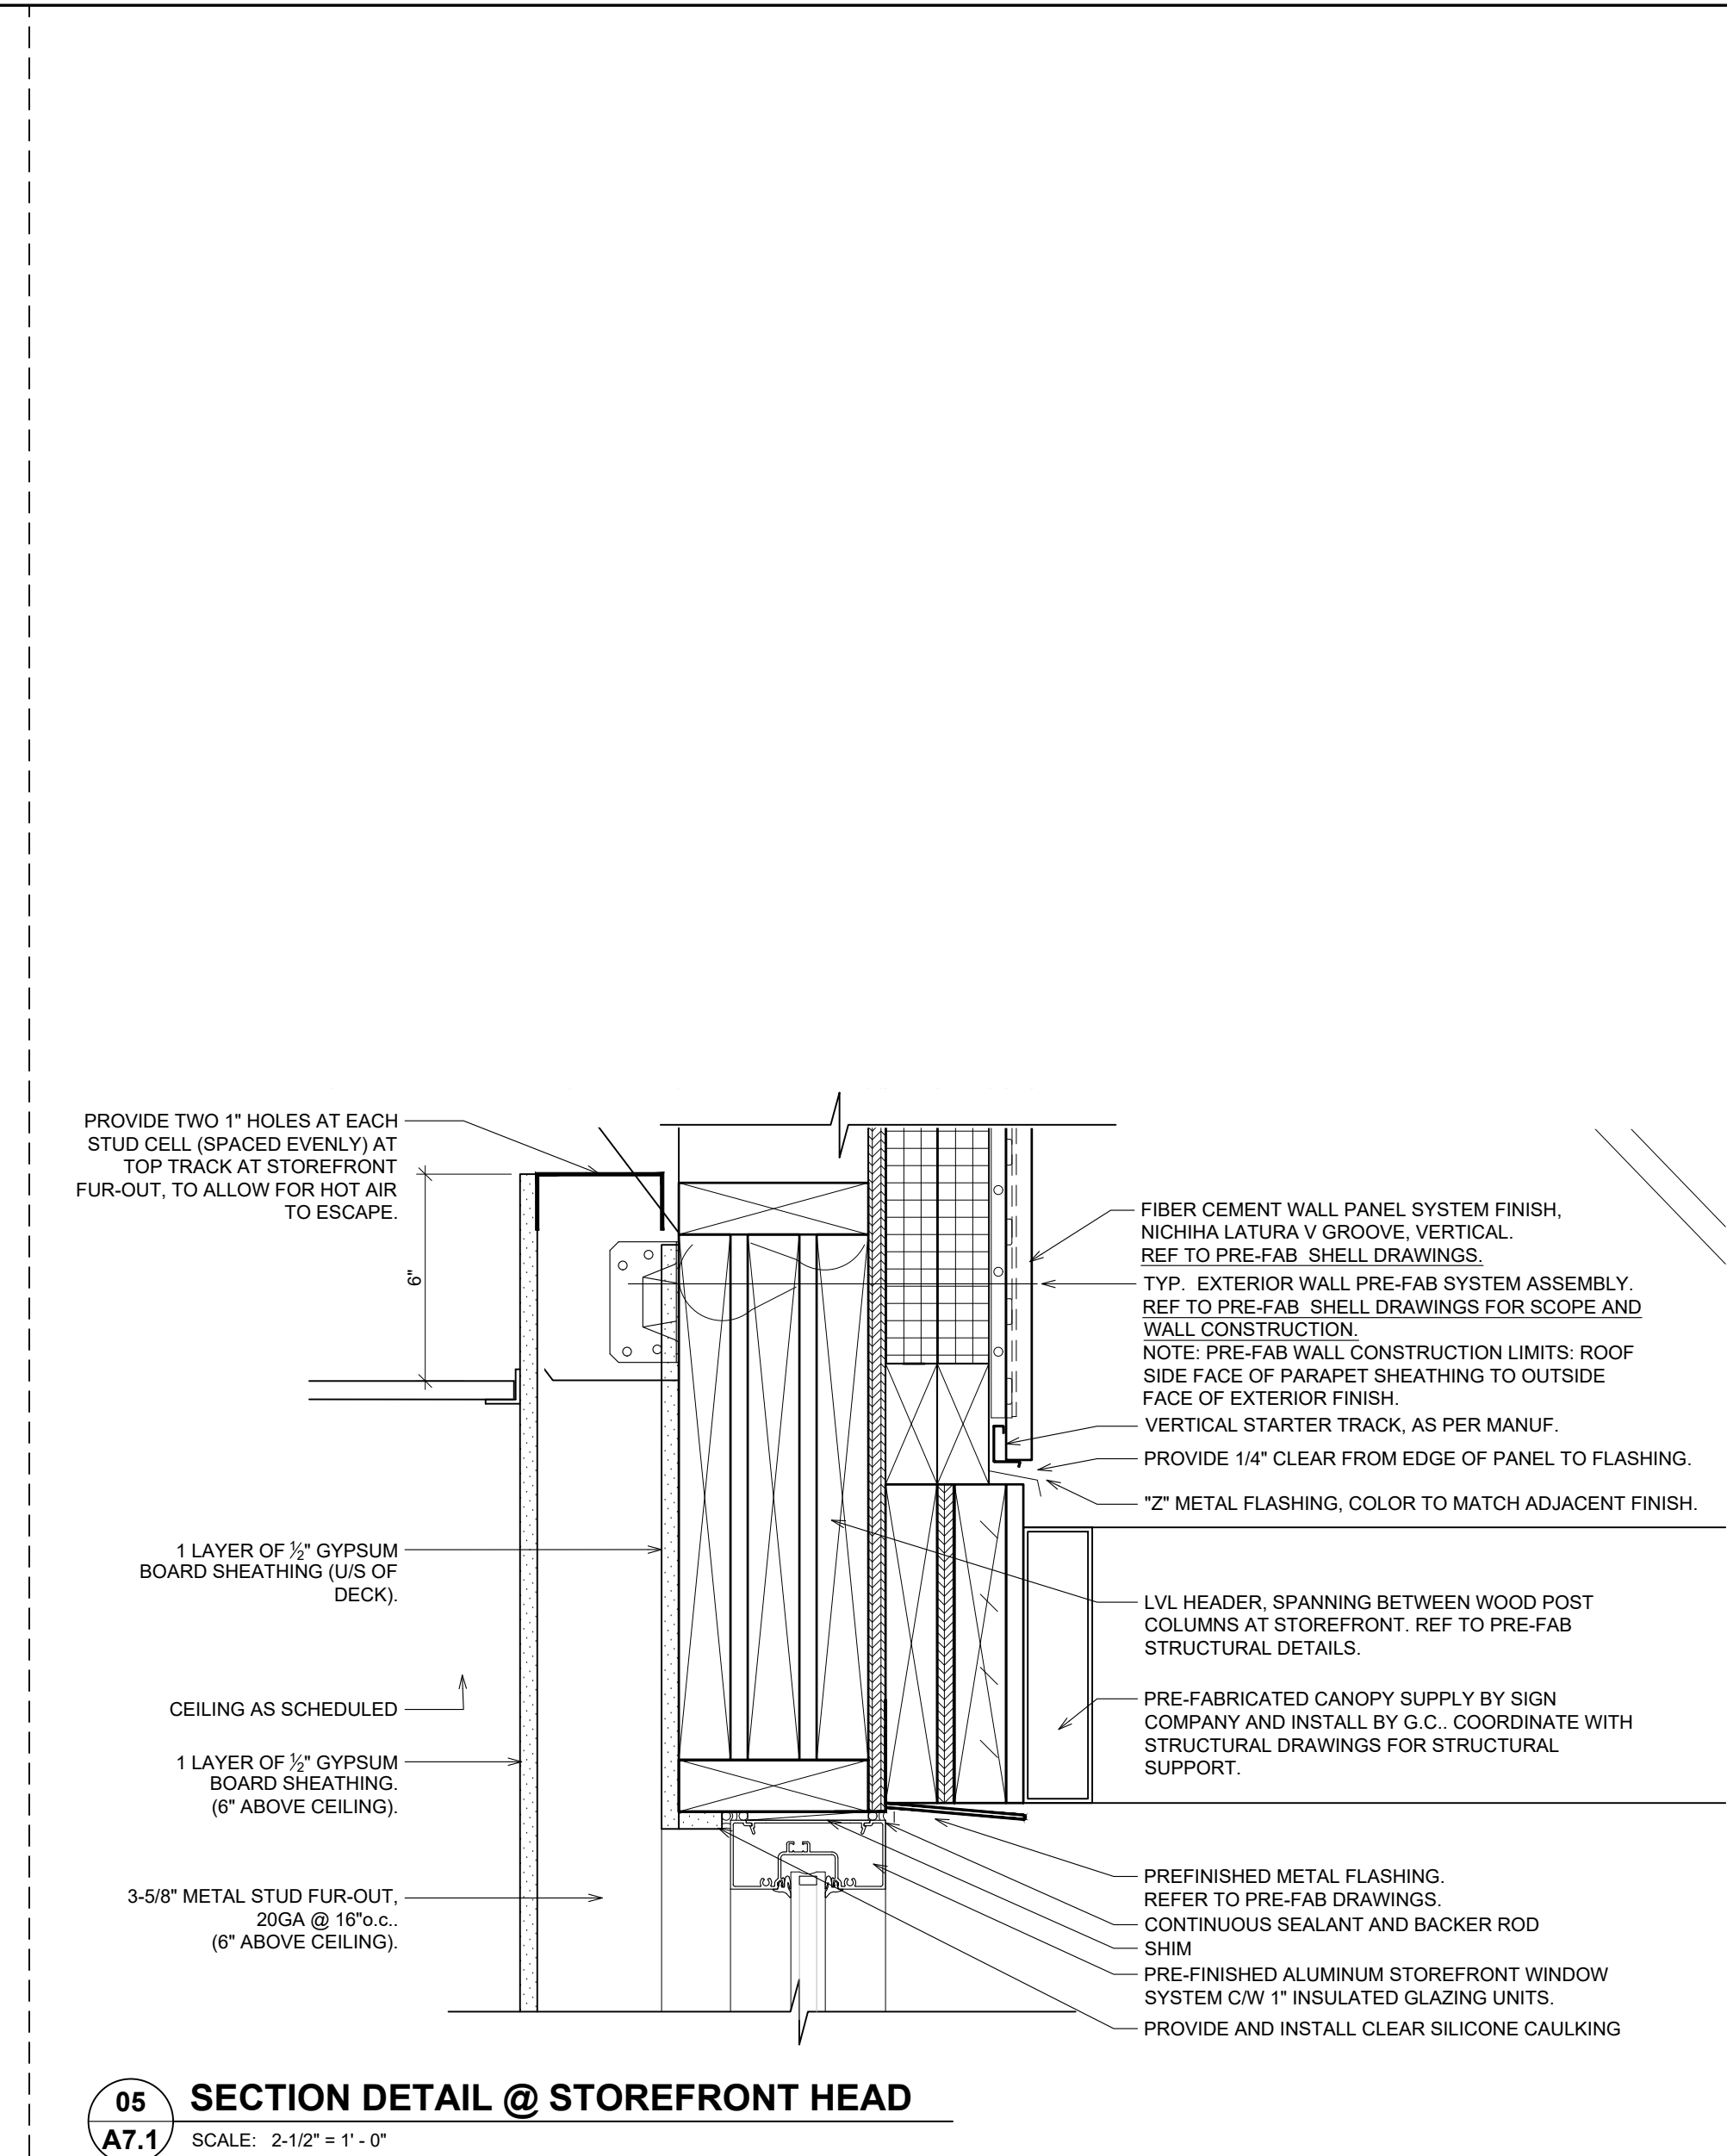


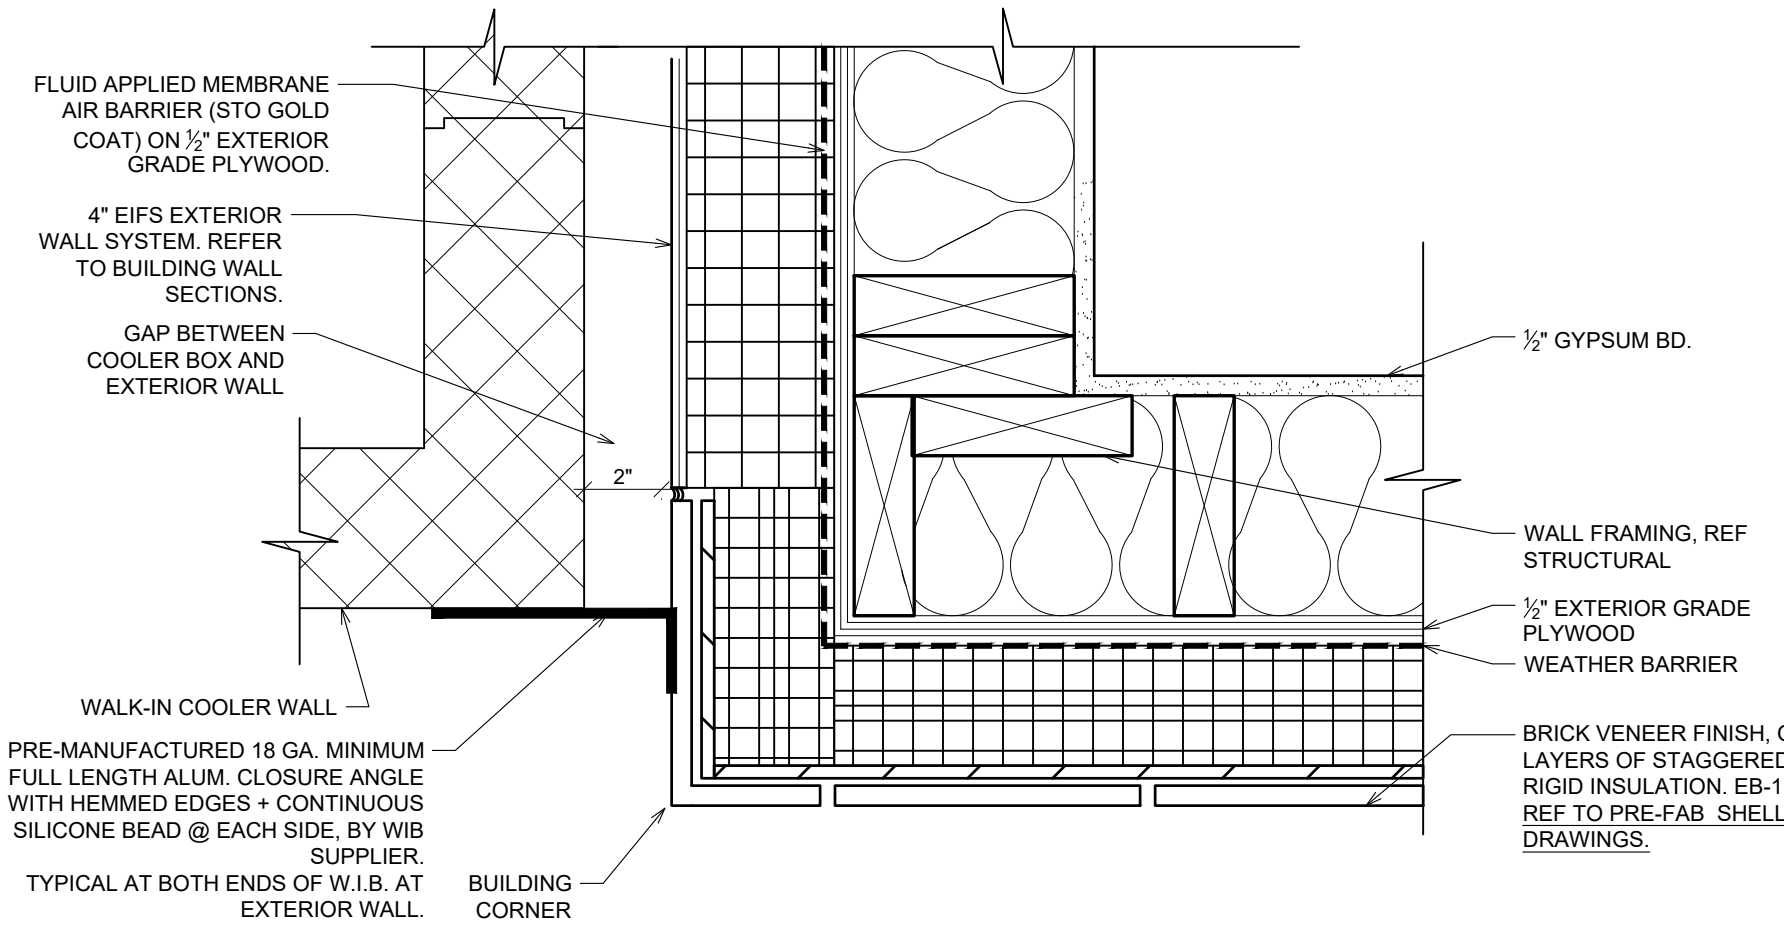


7 FLASHING DETAIL @ W.I.B. CORNER
A7.2 SCALE: 2 1/2"=1'-0"

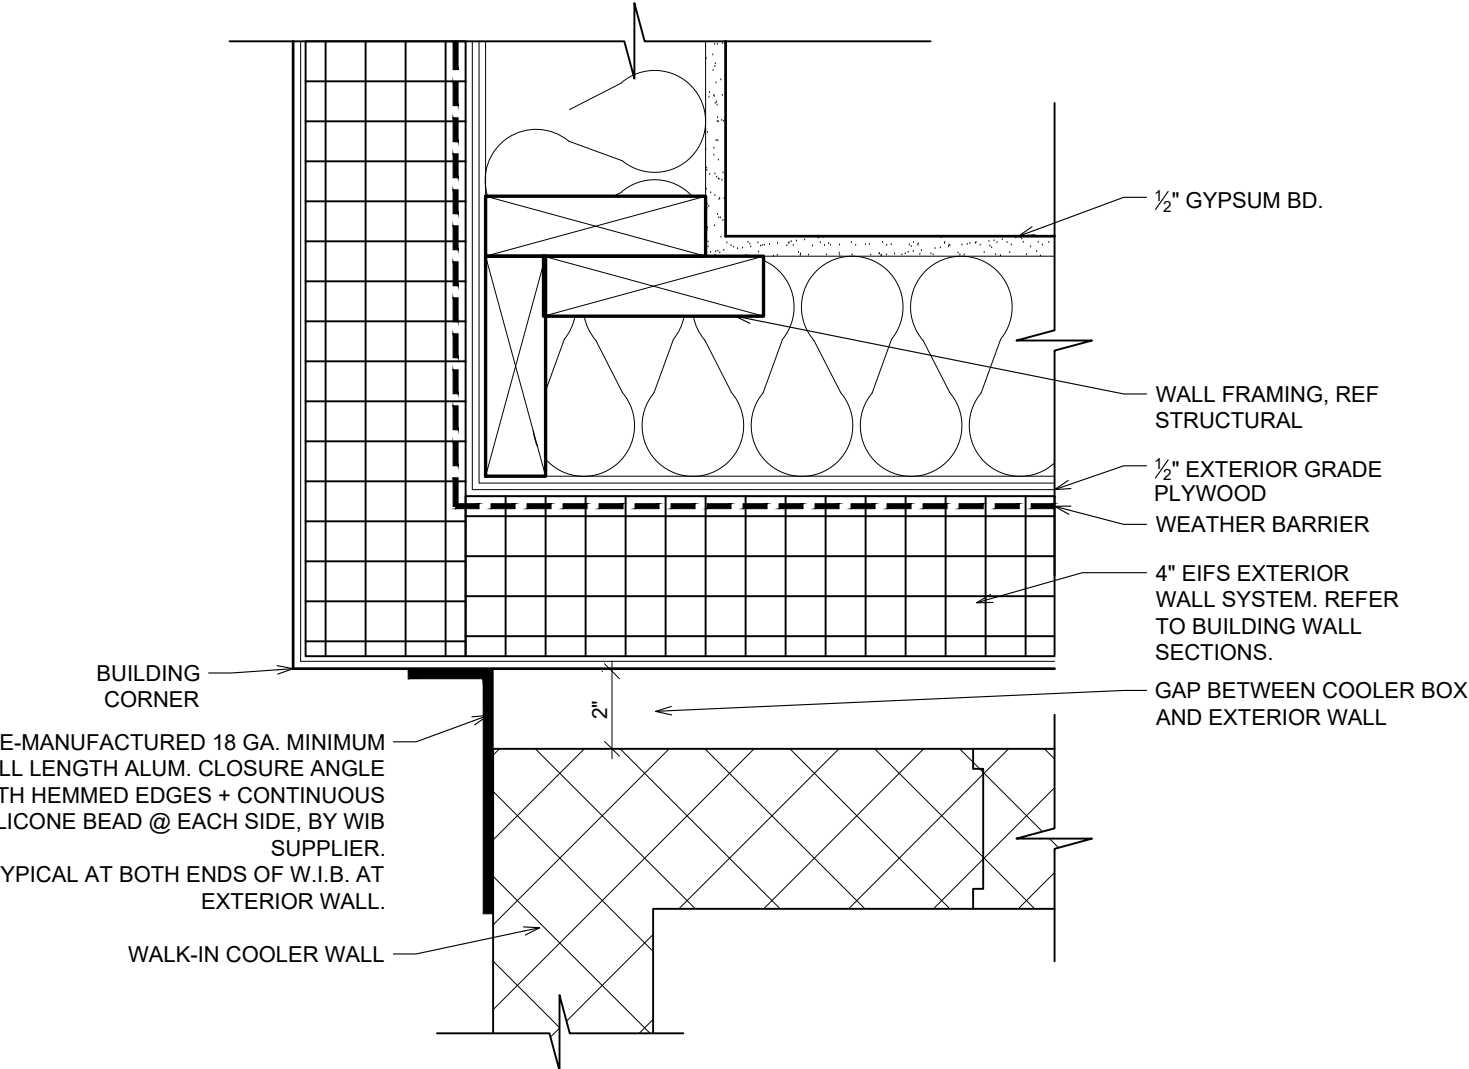


6 FLASHING DETAIL @ W.I.B. CORNER
A7.2 SCALE: 2 1/2"=1'-0"

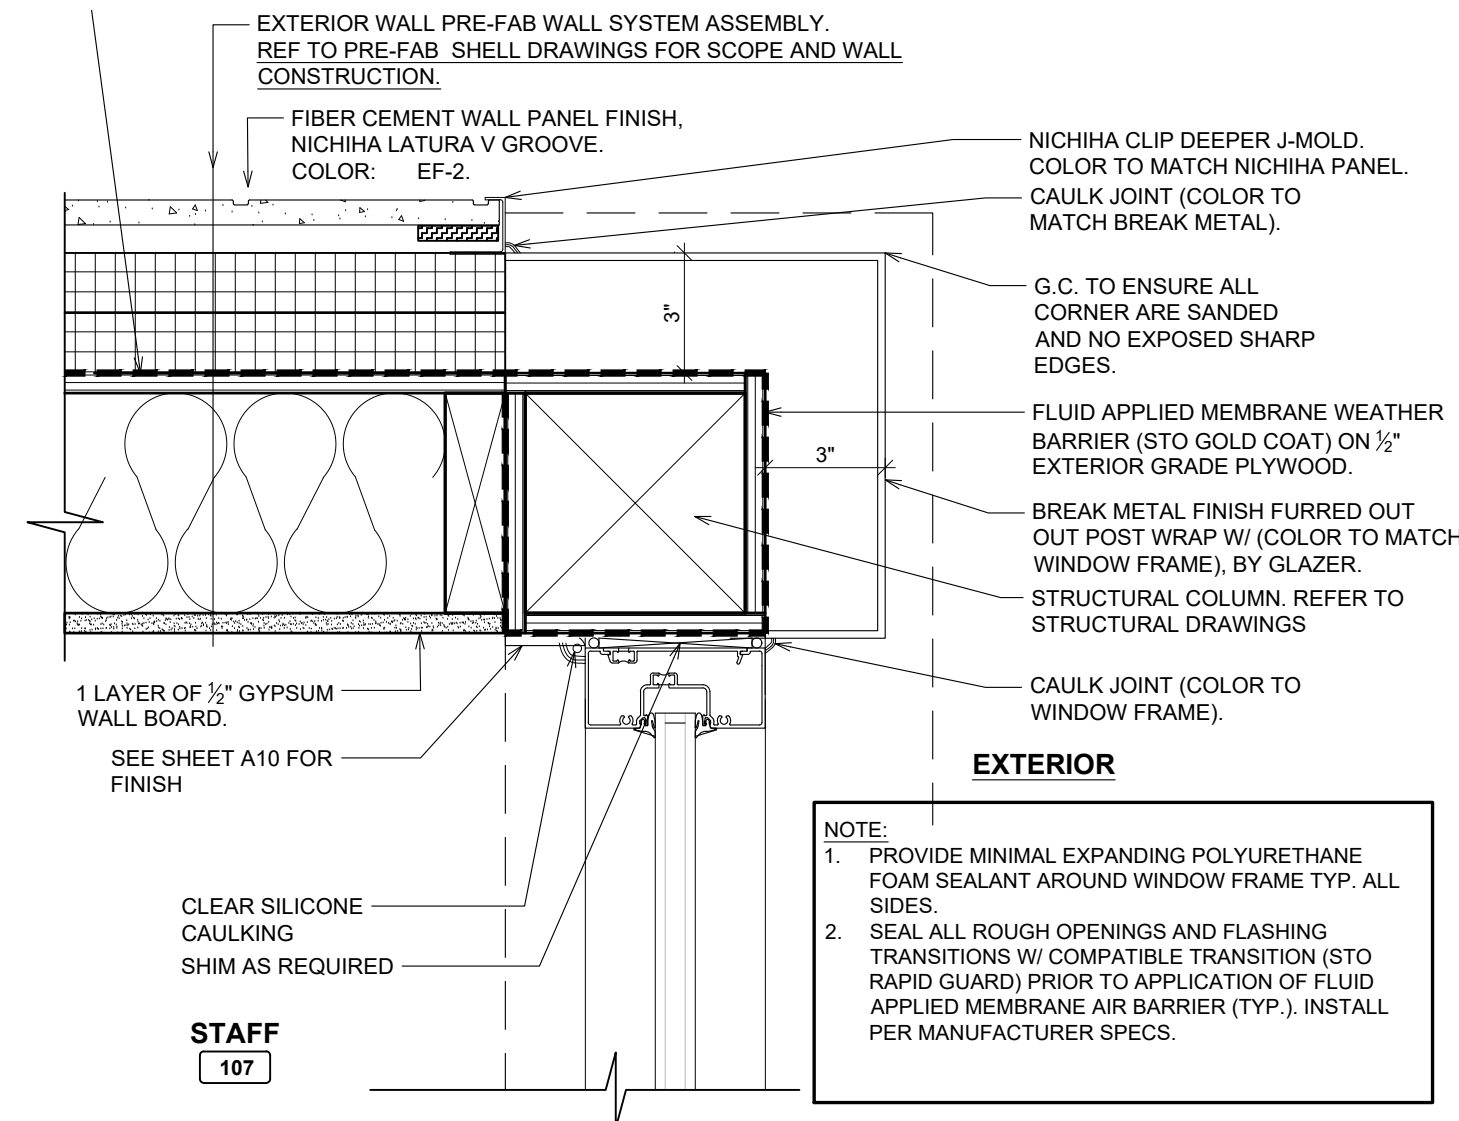


1 PLAN DETAIL @ CORNER
A7.2 SCALE: 2 1/2"=1'-0"

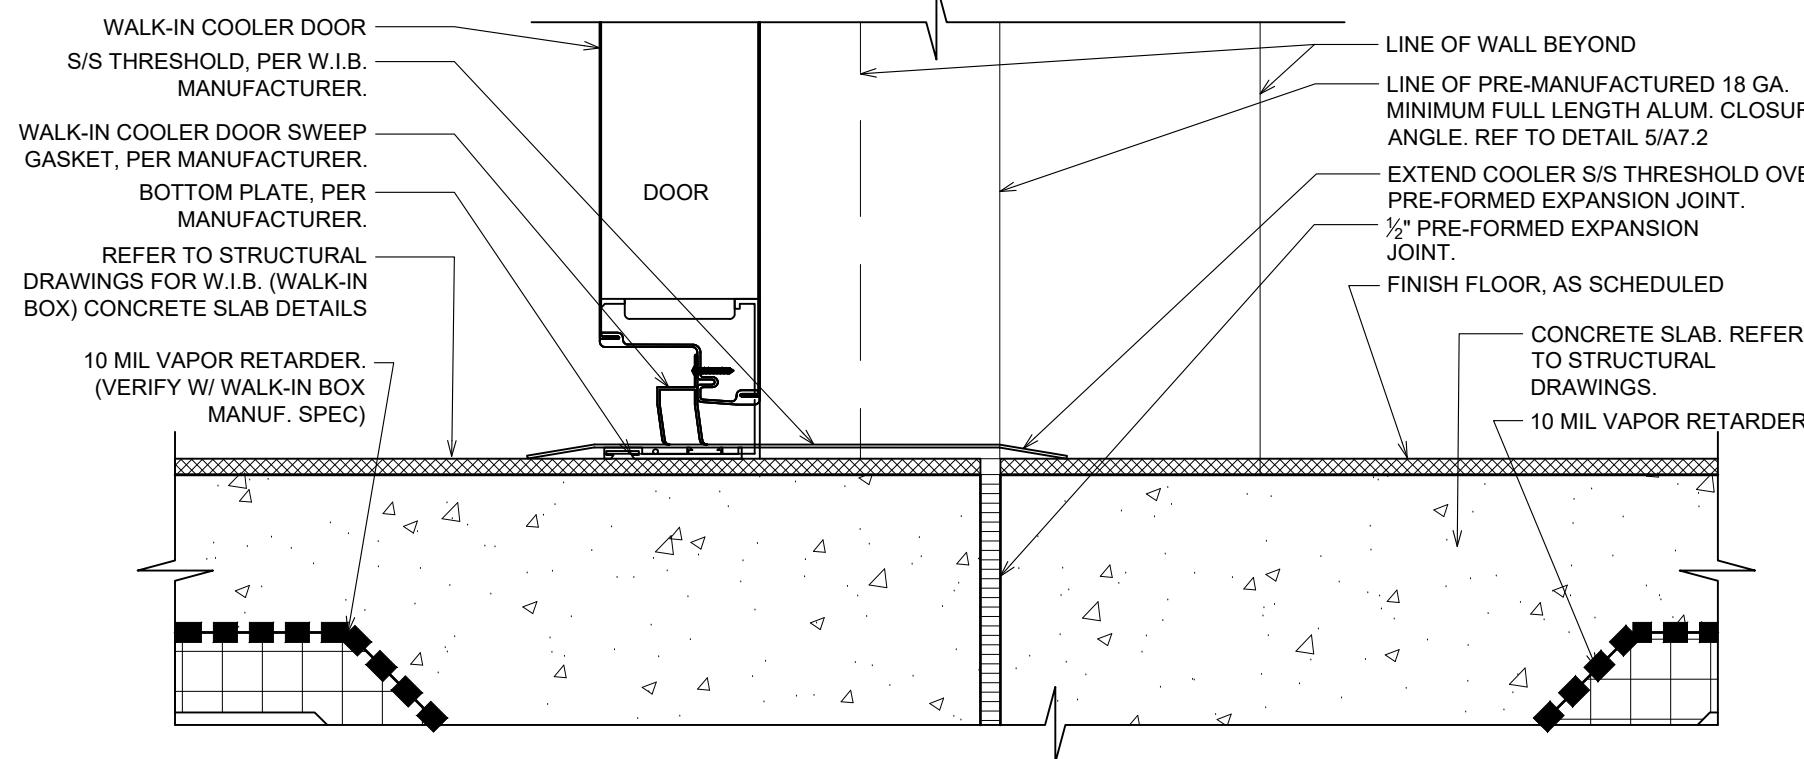


8 THRESHOLD DETAIL @ W.I.B.
A7.2 SCALE: 2 1/2"=1'-0"

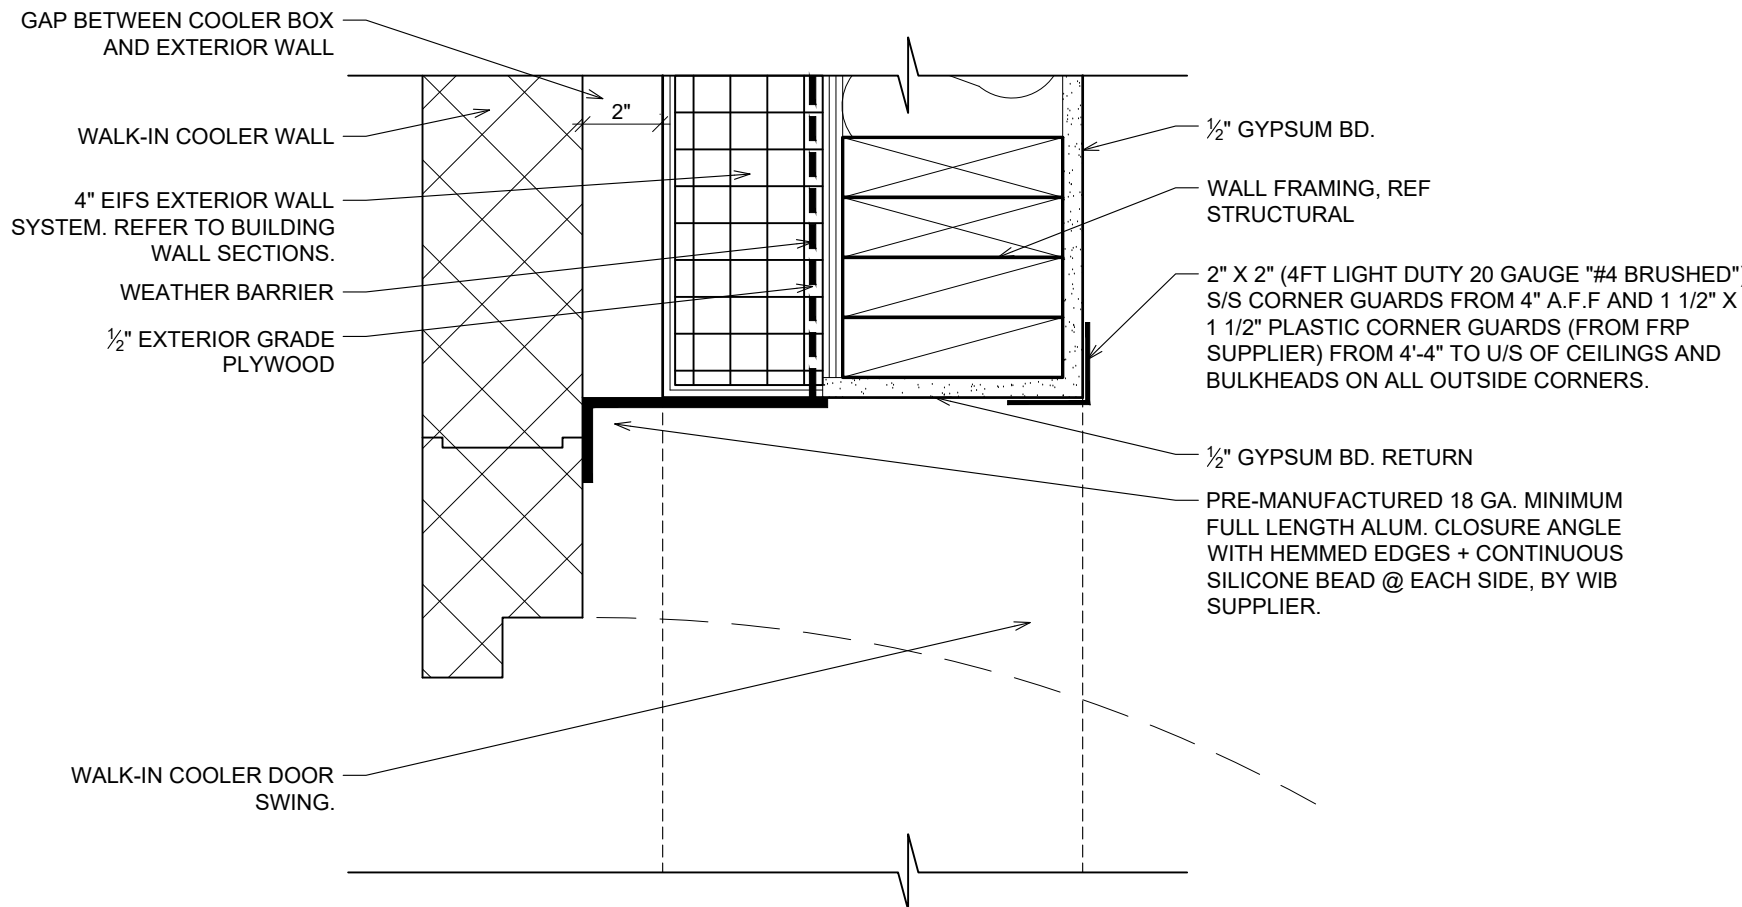


5 FLASHING DETAIL @ W.I.B. DOOR
A7.2 SCALE: 2 1/2"=1'-0"

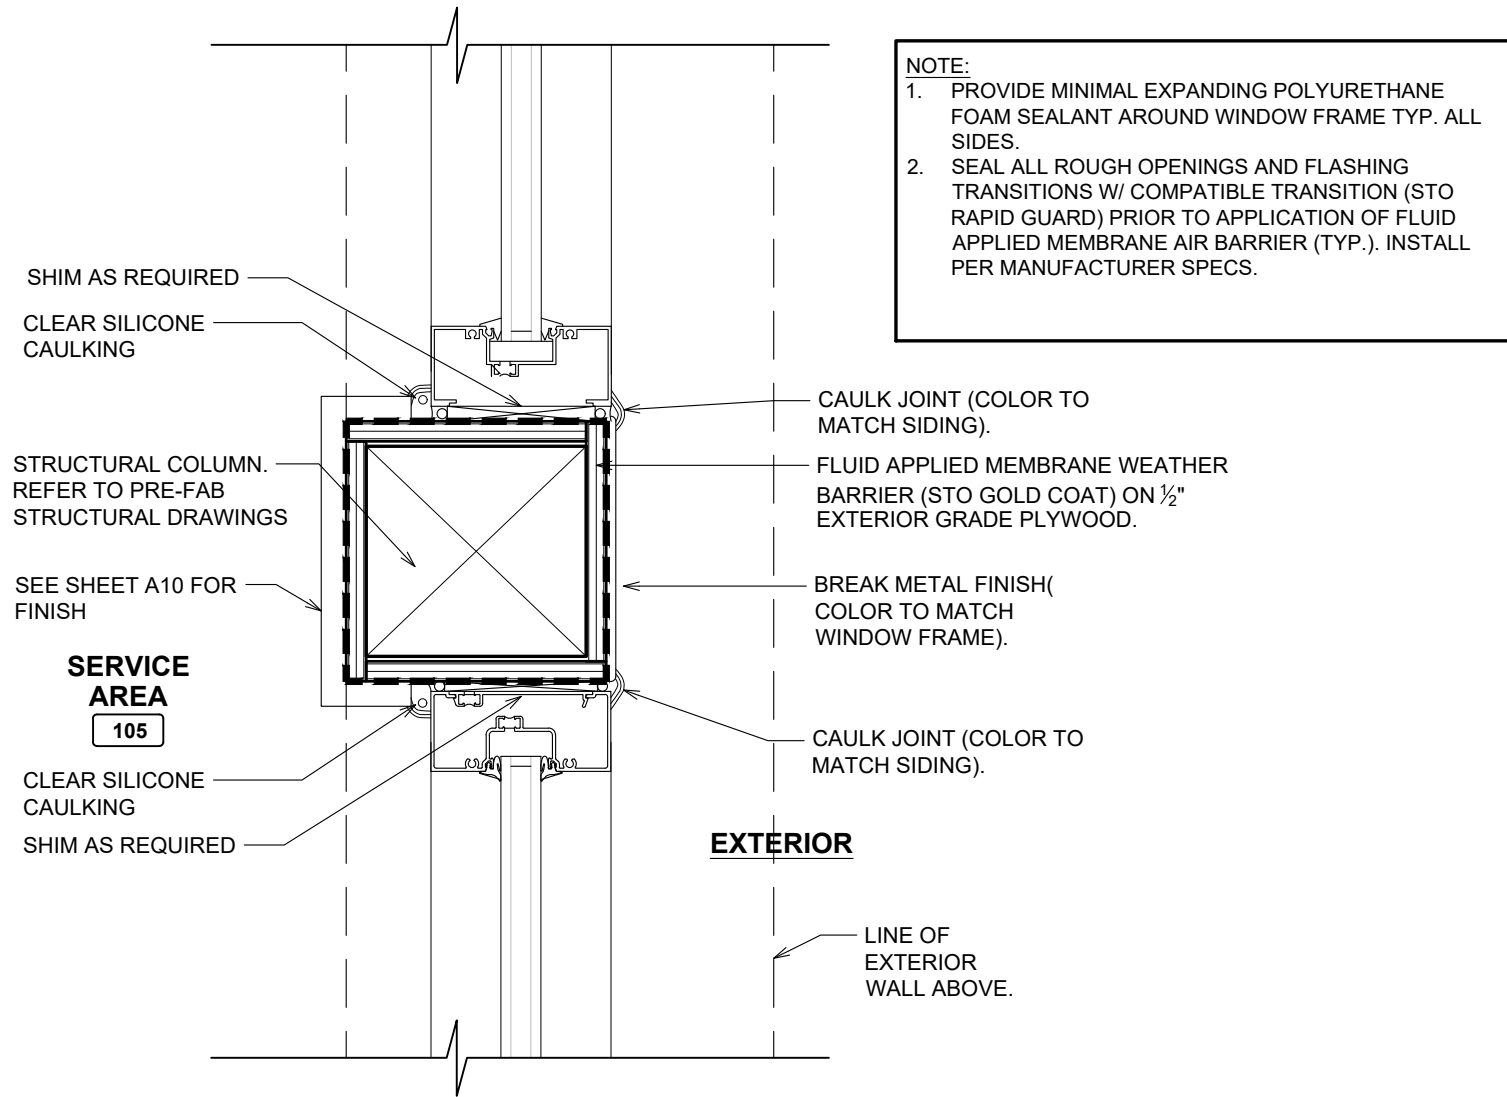

2 PLAN DETAIL @ STOREFRONT POST
A7.2 SCALE: 2 1/2"=1'-0"

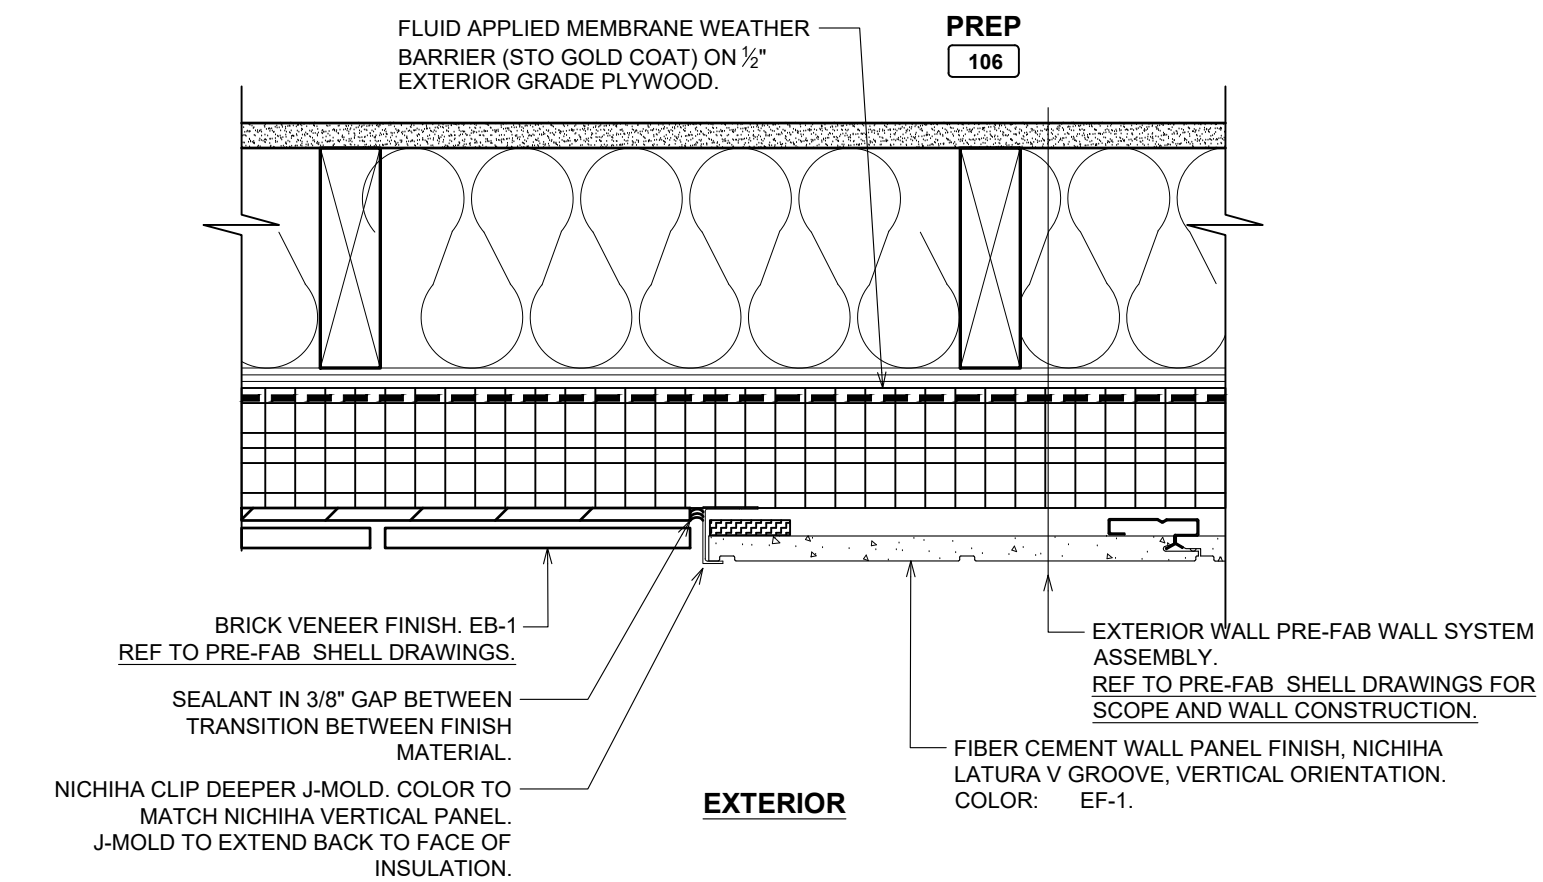

4 PLAN DETAIL @ MATERIAL TRANSITION
A7.2 SCALE: 2 1/2"=1'-0"

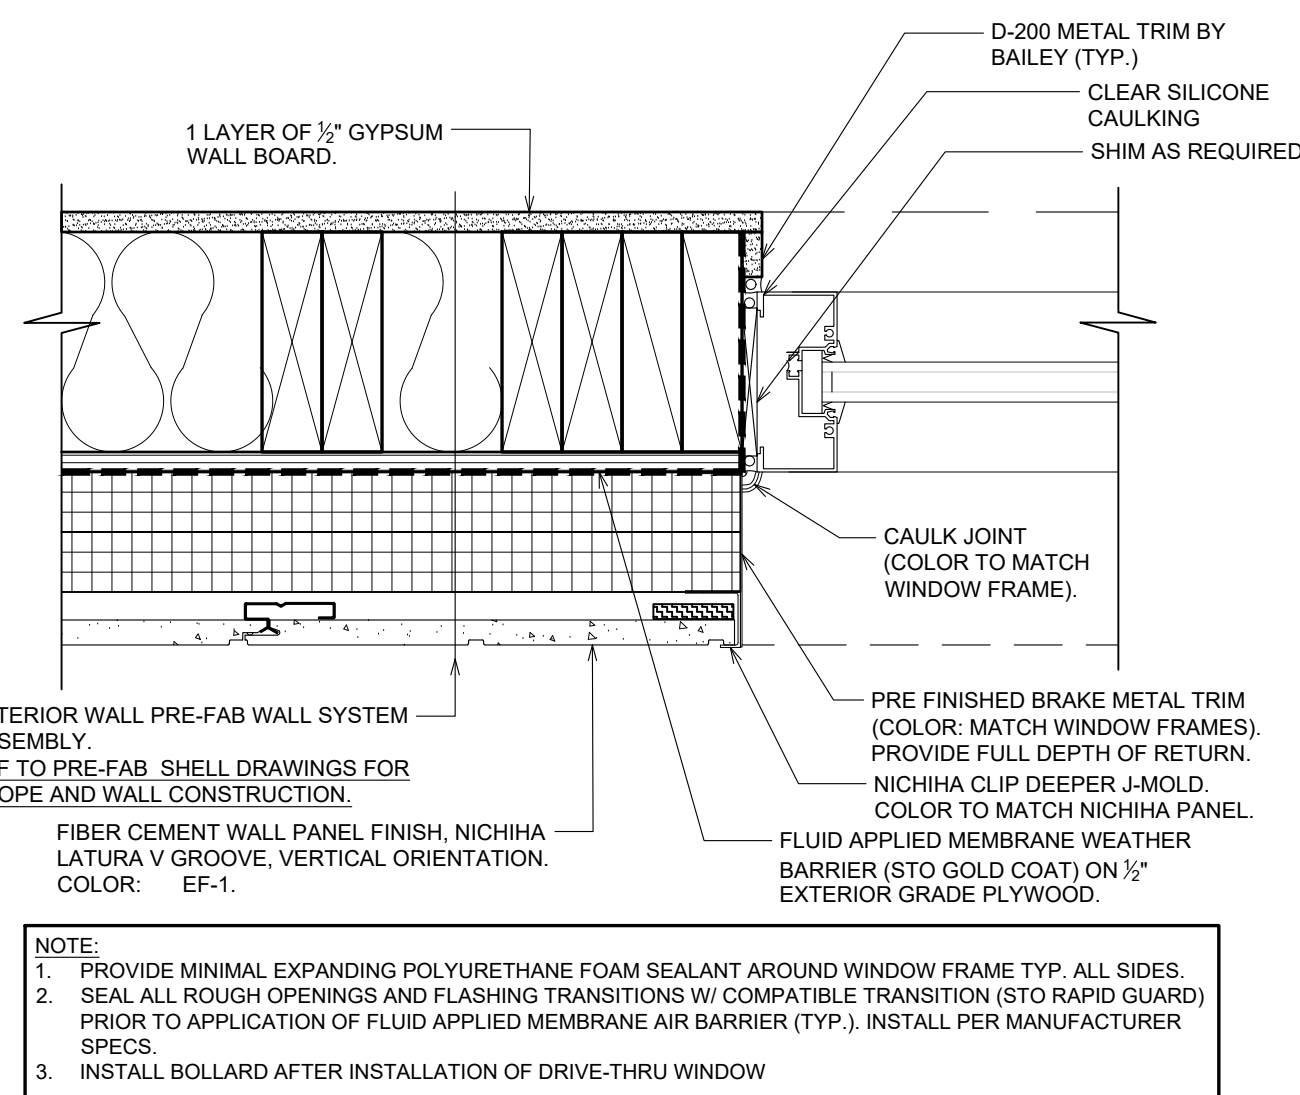

3 PLAN DETAIL @ DRIVE-THRU WINDOW
A7.2 SCALE: 2 1/2"=1'-0"

ISSUE TABLE		
No.	Date (mm/dd/yy)	Description
01	09-26-25	DTGO PROTOTYPE DOCUMENTS
REVISIONS		
No.	Date	Description
DRAWINGS REVISED AS PER DESIGN BULLETIN		
No.	Date	Description

THIS DRAWING IS OWNED BY OR LICENSED FOR USE BY POPEYES LOUISIANA KITCHEN (OR ITS AFFILIATED OR RELATED COMPANIES) AND MAY NOT BE REPRODUCED, USED, DOWNLOADED, DISSEMINATED, PUBLISHED, OR TRANSFERRED IN ANY FORM OR BY ANY MEANS, EXCEPT WITH THE PRIOR WRITTEN CONSENT OF POPEYES LOUISIANA KITCHEN. COPYRIGHT INFRINGEMENT IS A VIOLATION OF FEDERAL LAW SUBJECT TO CRIMINAL AND CIVIL PENALTIES.


THE CONTRACTOR IS TO VERIFY ALL DIMENSIONS AND CONDITIONS ON THE PROJECT AND TO REPORT ANY DISCREPANCIES TO THE POPEYES LOUISIANA KITCHEN REPRESENTATIVE PRIOR TO COMMENCING WORK. THESE DRAWINGS ARE NOT TO BE USED FOR CONSTRUCTION PURPOSES UNLESS INDICATED BY POPEYES LOUISIANA KITCHEN AS "ISSUED FOR CONSTRUCTION".

Professional Seal


DESIGNER NOTES:
DESIGN GUIDELINE ONLY - NOT FOR PERMIT OR CONSTRUCTION

THESE DOCUMENTS MUST BE COMPLETED AND / OR MODIFIED BY A LICENSED ARCHITECT AND ENGINEER TO CONFORM TO ALL APPLICABLE CODES, AND SPECIFIC SITE CONDITIONS. THERE IS NO WARRANTY, WHETHER IMPLIED OR EXPRESSED, THAT THESE DOCUMENTS MEET THE APPLICABLE CODE REQUIREMENTS. LIABILITY FOR THE DESIGN AND ANY USE OF THE DOCUMENTS IS THE SOLE RESPONSIBILITY OF THE ARCHITECT AND ENGINEER OF RECORD.

Company Logo	
Project	
Store Type	US DTGO PROTOTYPE
Location	PROTOTYPE DTGO (U.S.) CITY, STATE
Drawing Title	
PLAN DETAILS	
Drawn	Checked
XX	XX
Scale	Date
AS NOTED	###.###
Project No.	Drawing No.
XX	A7.2

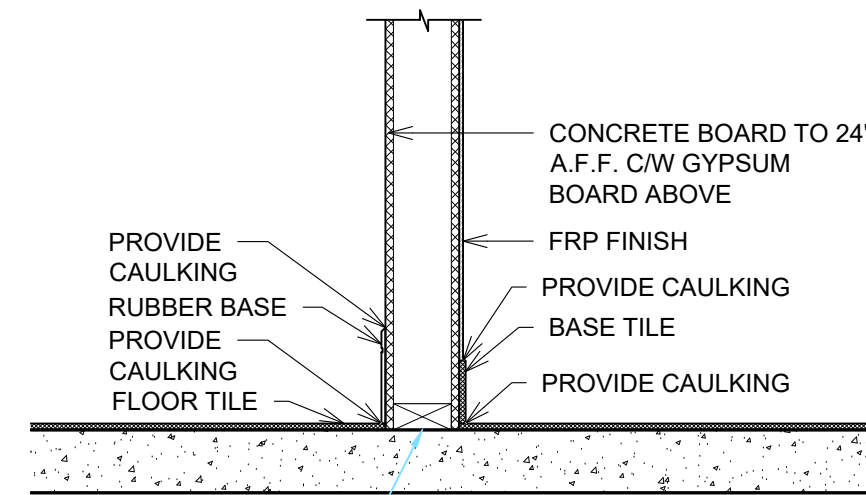


4 BASE @ FRP & GYPSUM BOARD
A8 SCALE: 1" = 1'-0"

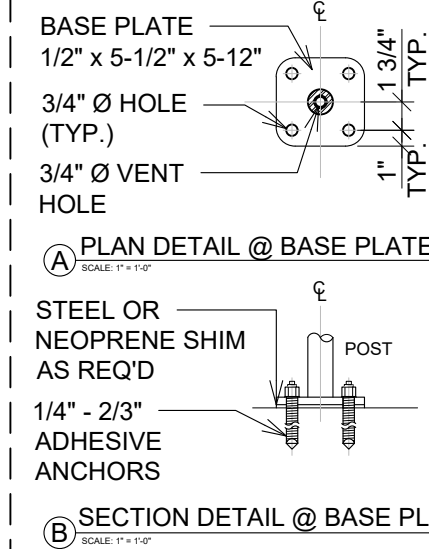


3
A8

NOT USED

SCALE: 1/2" = 1'-0"

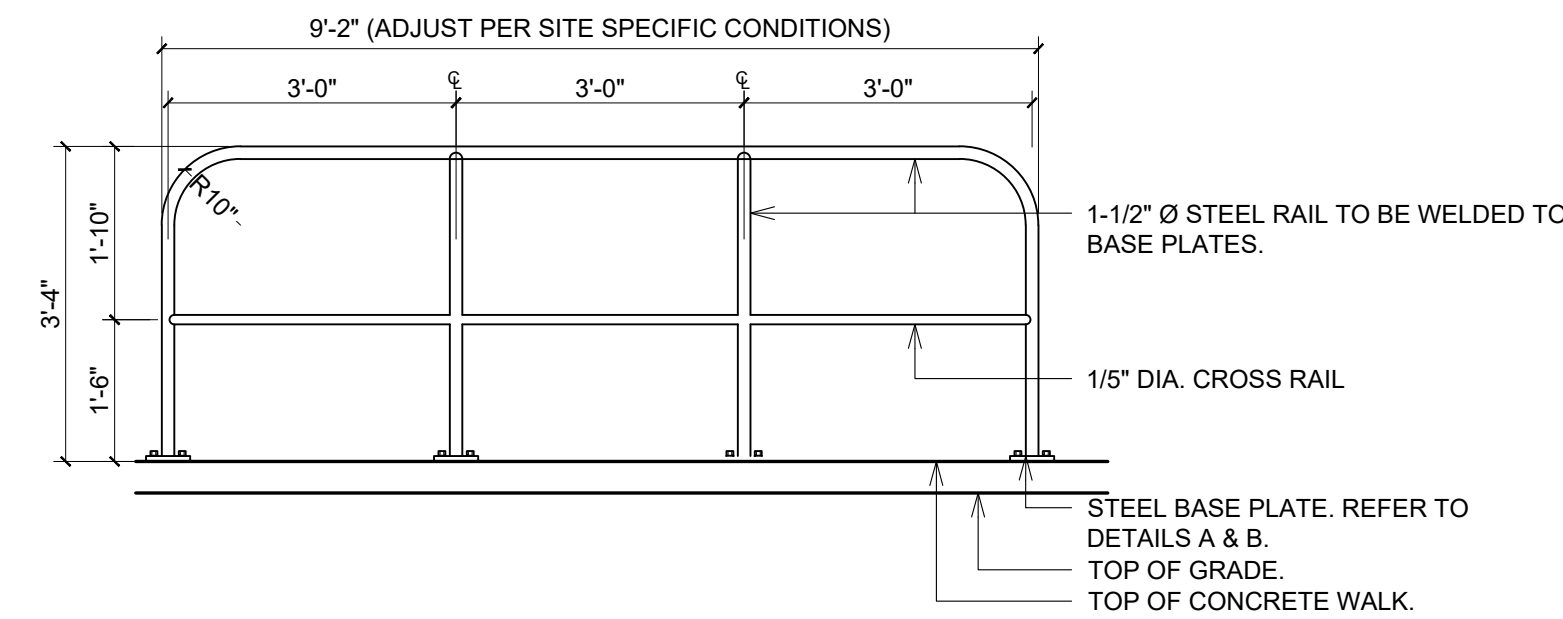

2 **DETAIL @ METAL RAILING**
A8 SCALE: 1/2" = 1'-0"

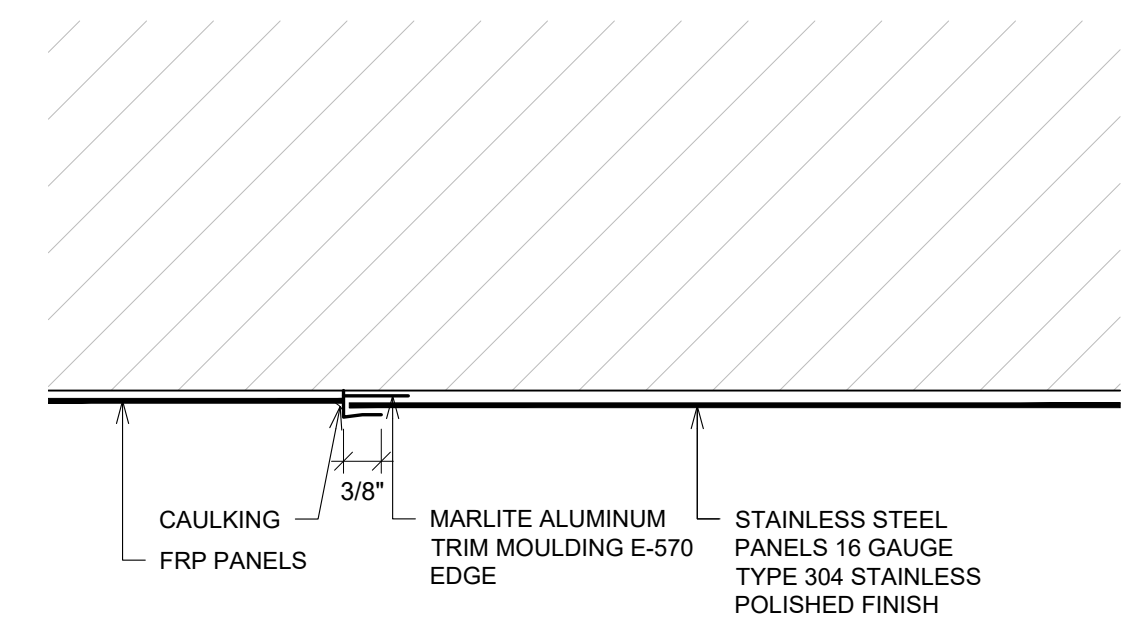

1 FRP-STAINLESS STEEL TRIM DETAIL
A8 SCALE: 6" = 1'-0"

ISSUE TABLE		
No.	Date (mm/dd/yy)	Description
01	09-26-25	DTGO PROTOTYPE DOCUMENTS

REVISIONS

No.	Date	Description

DRAWINGS REVISED AS PER DESIGN BULLETIN

No.	Date	Description

THIS DRAWING IS OWNED BY OR LICENSED FOR USE BY POPEYES LOUISIANA KITCHEN (OR ITS AFFILIATED OR RELATED COMPANIES) AND MAY NOT BE REPRODUCED, USED, DOWNLOADED, DISSEMINATED, PUBLISHED, OR TRANSFERRED IN ANY FORM OR BY ANY MEANS, EXCEPT WITH THE PRIOR WRITTEN CONSENT OF POPEYES LOUISIANA KITCHEN. COPYRIGHT INFRINGEMENT IS A VIOLATION OF FEDERAL LAW SUBJECT TO CRIMINAL AND CIVIL PENALTIES.


THE CONTRACTOR IS TO VERIFY ALL DIMENSIONS AND CONDITIONS ON THE PROJECT AND TO REPORT ANY DISCREPANCIES TO THE POPEYES LOUISIANA KITCHEN REPRESENTATIVE PRIOR TO COMMENCING WORK. THESE DRAWINGS ARE NOT TO BE USED FOR CONSTRUCTION PURPOSES UNLESS INDICATED BY POPEYES LOUISIANA KITCHEN AS "ISSUED FOR CONSTRUCTION".

Professional Seal


DESIGNER NOTES:
DESIGN GUIDELINE ONLY - NOT FOR PERMIT OR CONSTRUCTION

THESE DOCUMENTS MUST BE COMPLETED AND / OR MODIFIED BY A LICENSED ARCHITECT AND ENGINEER TO CONFORM TO ALL APPLICABLE CODES, AND SPECIFIC SITE CONDITIONS. THERE IS NO WARRANTY, WHETHER IMPLIED OR EXPRESSED THAT THESE DOCUMENTS MEET THE APPLICABLE CODE REQUIREMENTS. LIABILITY FOR THE DESIGN AND ANY USE OF THE DOCUMENTS IS THE SOLE RESPONSIBILITY OF THE ARCHITECT AND ENGINEER OF RECORD.

Company Logo

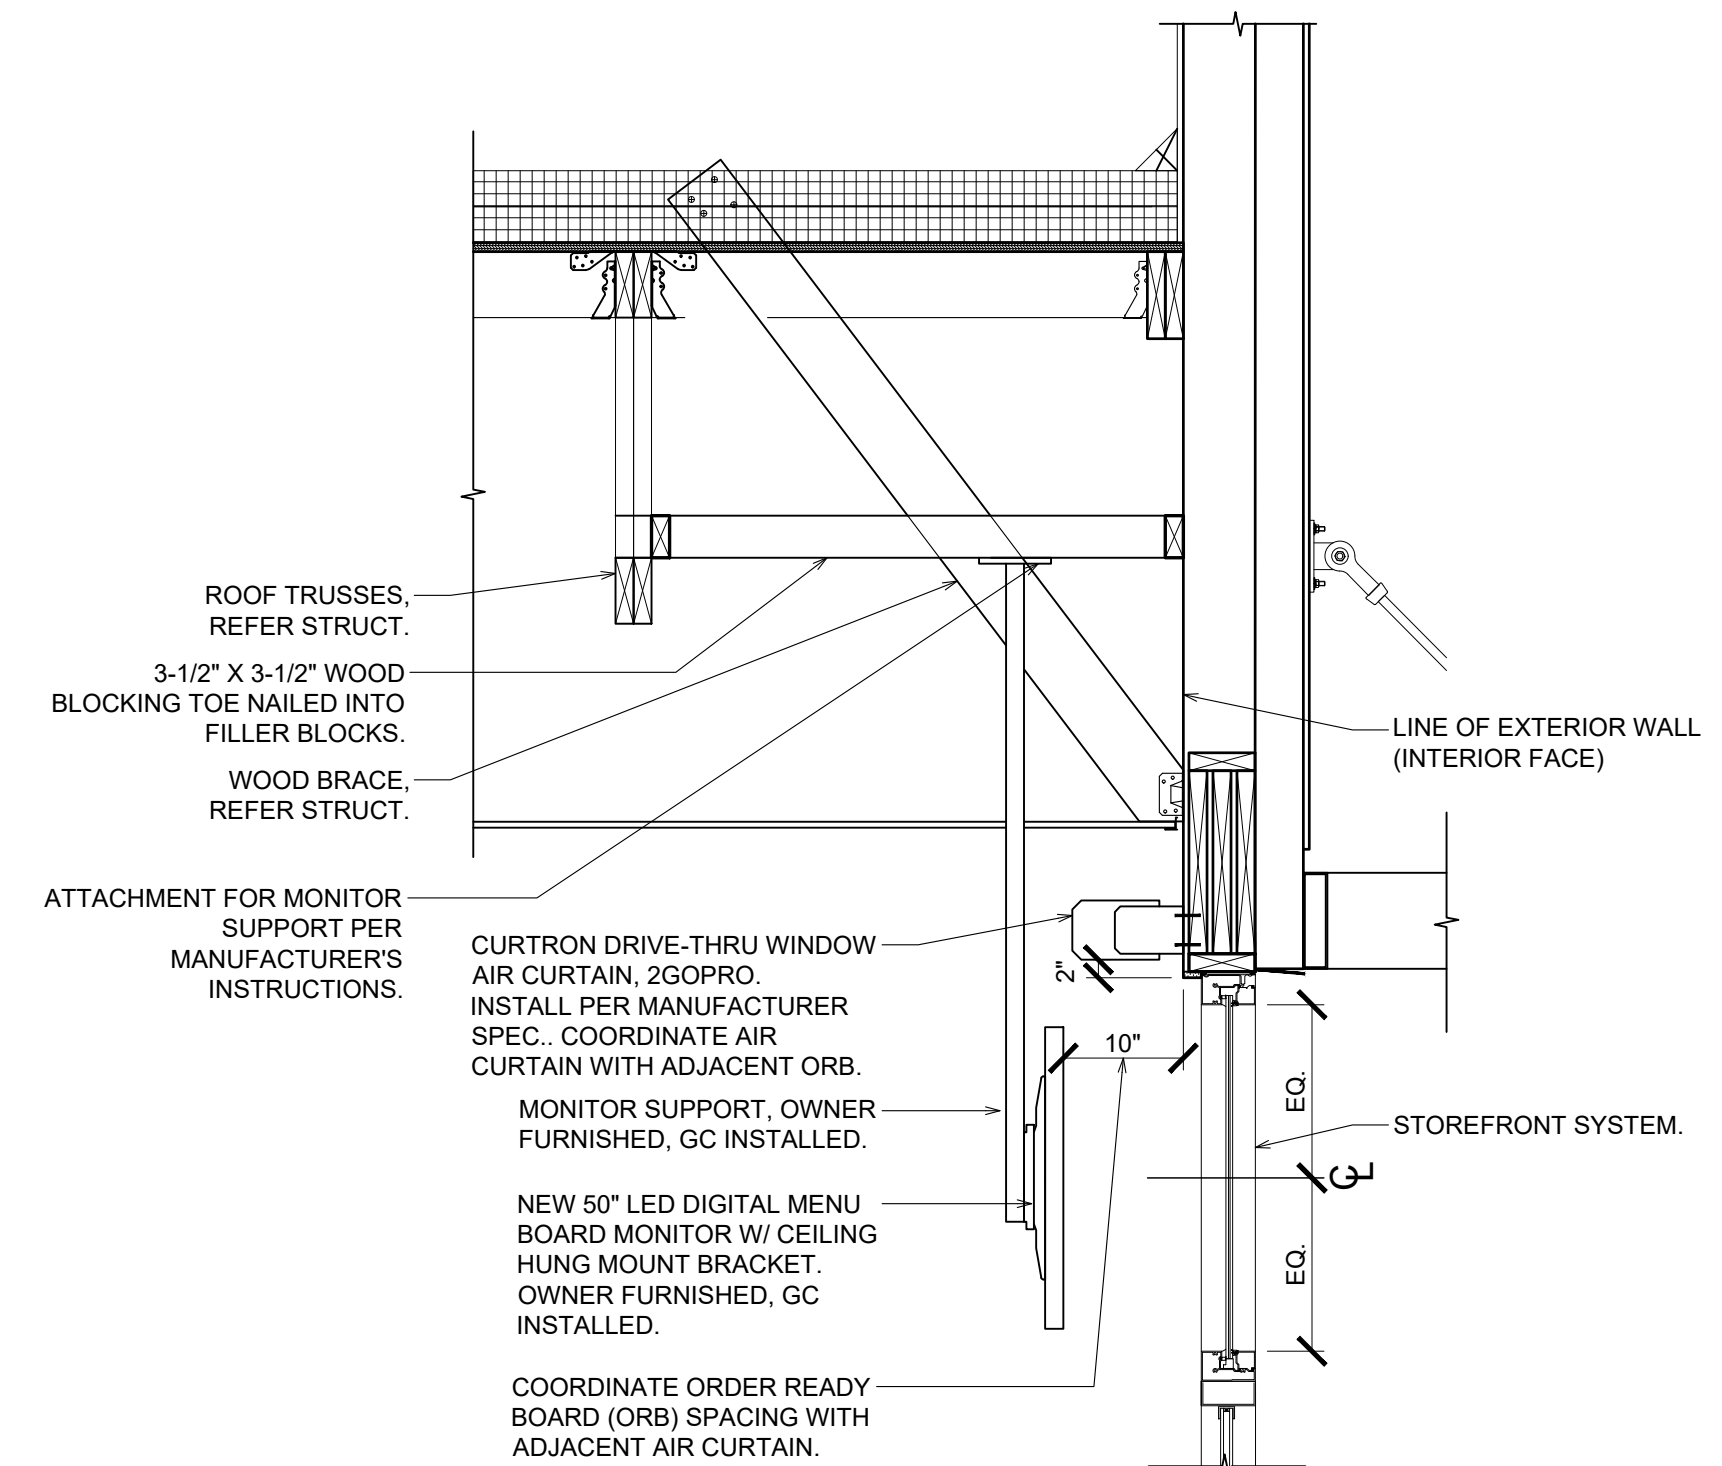


5 **MONITOR SUPPORT BRACKET DETAIL**
A8 SCALE: 3/4" = 1'-0"

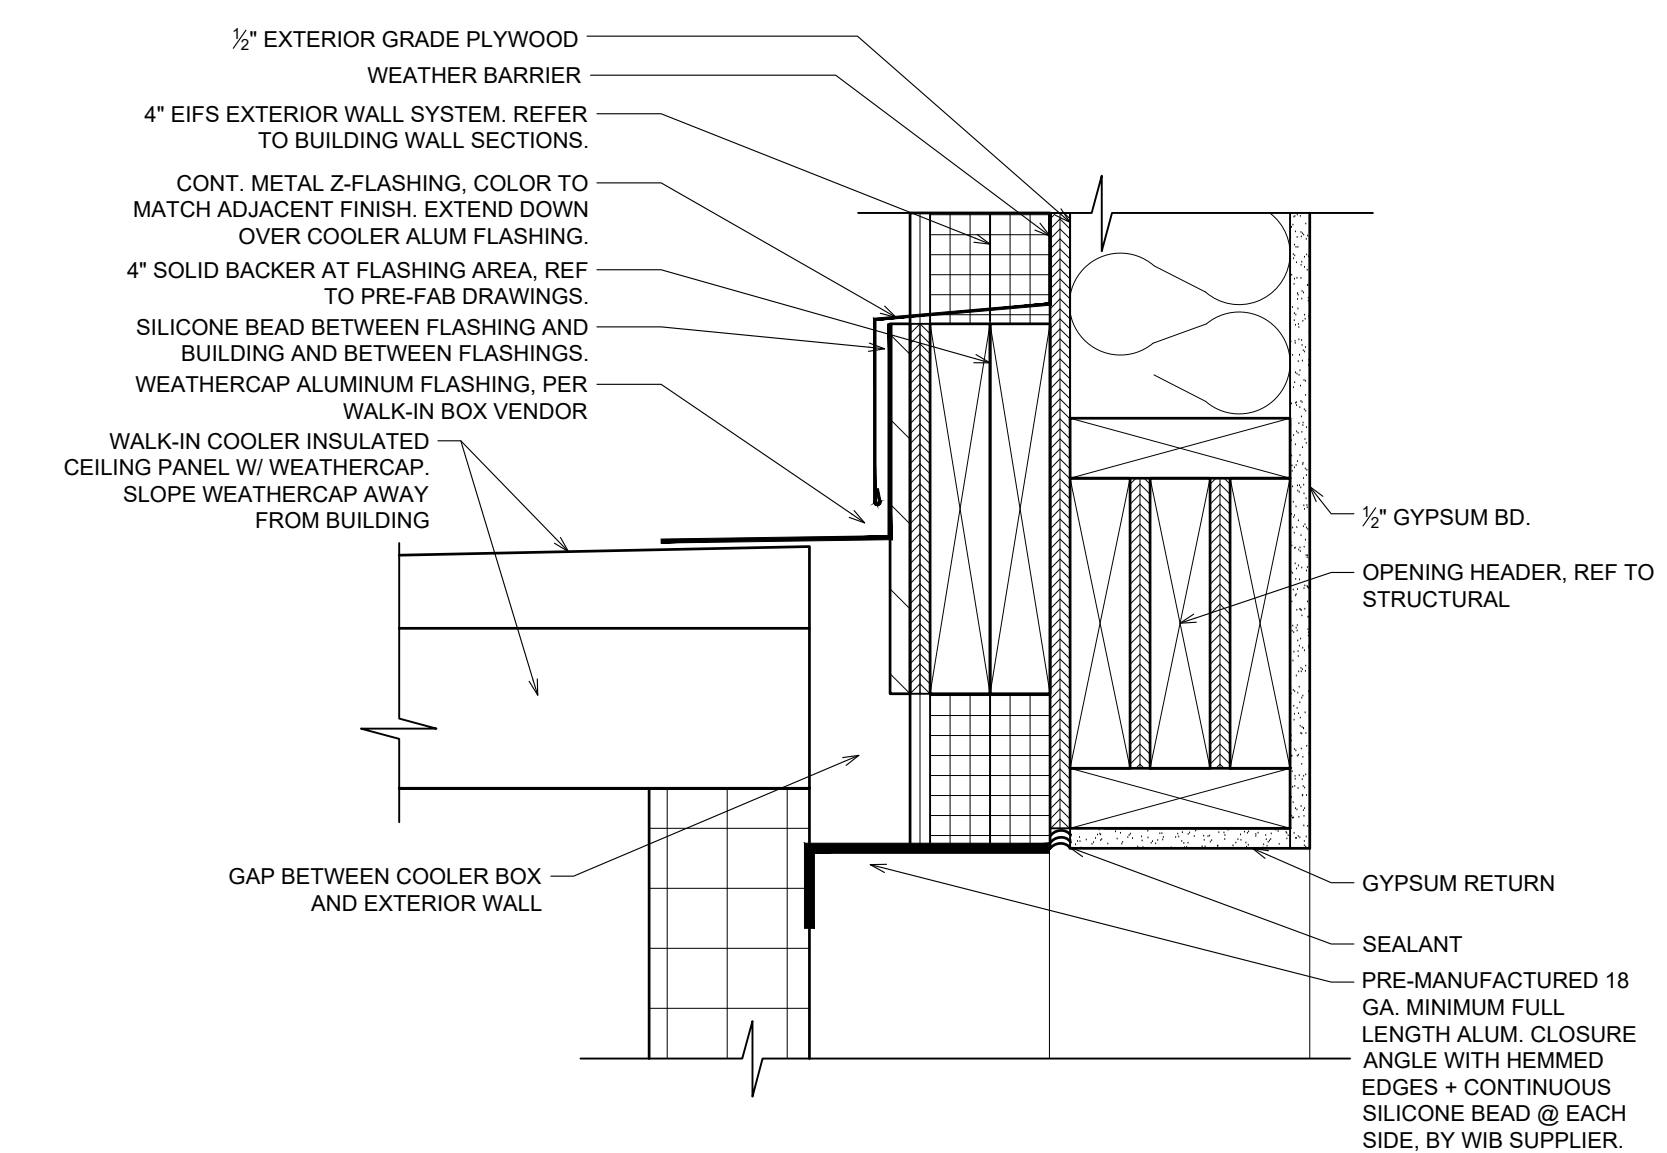


6 HEAD DETAIL @ W.I.B.
A8 SCALE: 2 1/2"=1'-0"


Project	
	
POPEYES.	
Store Type	
US DTGO PROTOTYPE	
Location	
PROTOTYPE DTGO (U.S.)	
City, State	
Drawing Title	
DETAILS	
Drawing	Checked
XX	XX
Scale	Date
AS NOTED	###.###.####
Project No.	Drawing No.
XX	A8

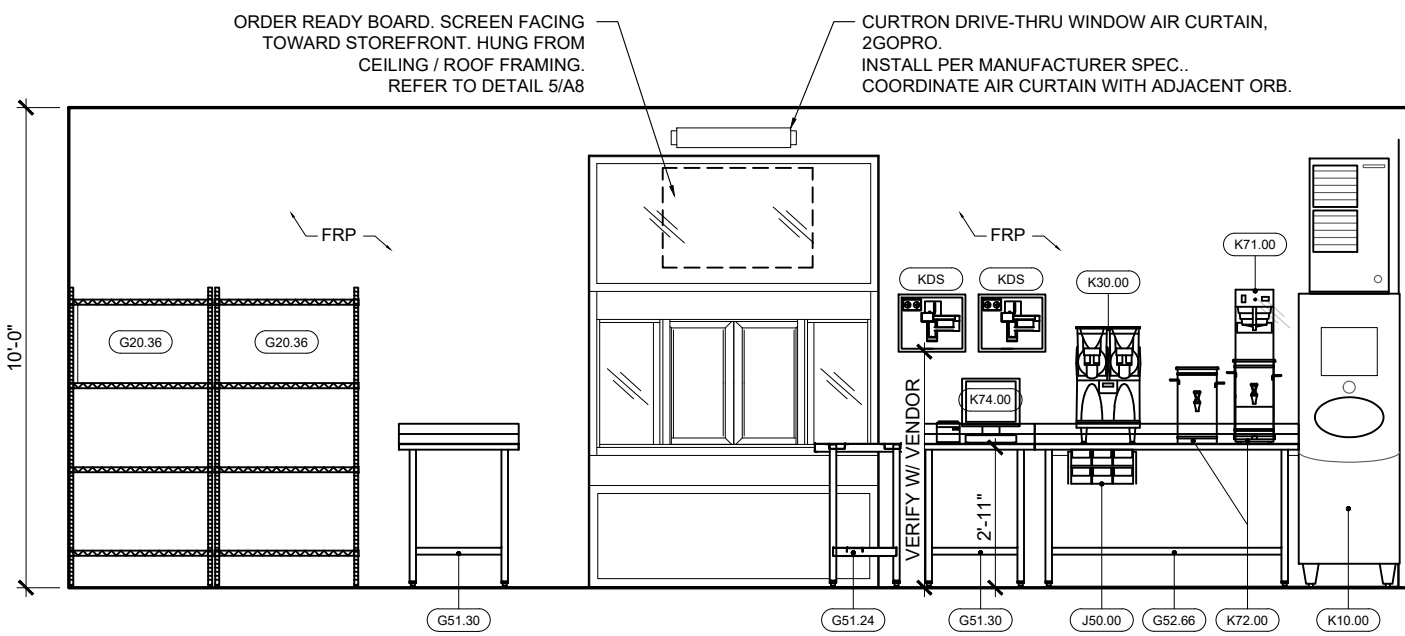


1 SERVICE AREA
A9.1 SCALE: 1/4" = 1'-0"

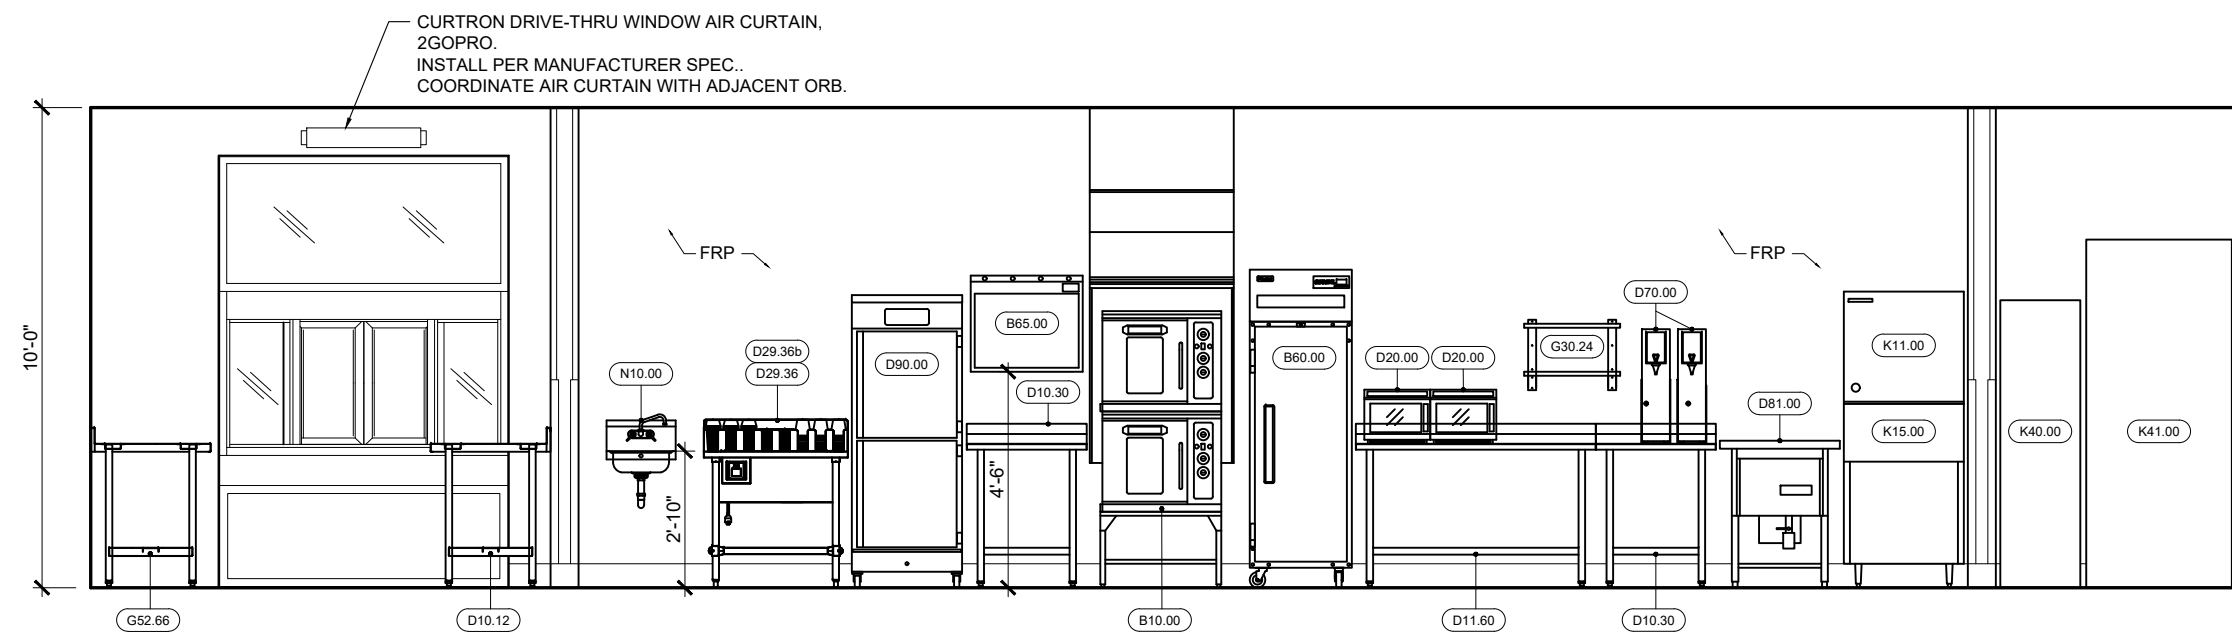


2 SERVICE / PREP AREA
A9.1 SCALE: 1/4" = 1'-0"

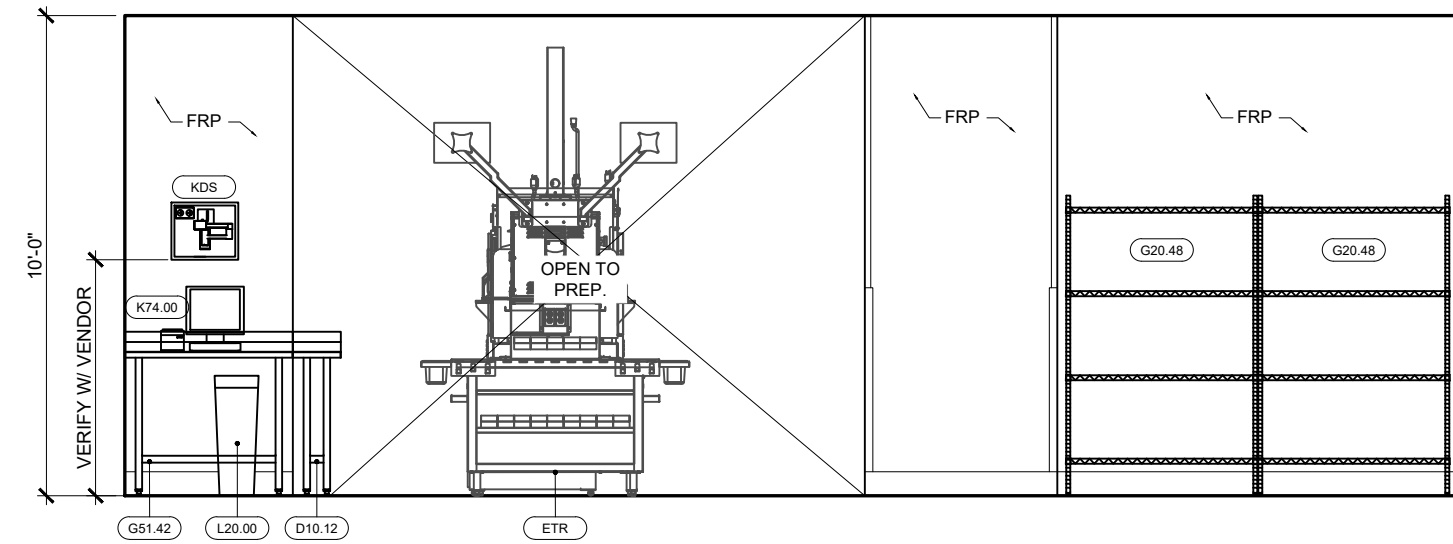


3 PREP / STAFF AREA
A9.1 SCALE: 1/4" = 1'-0"

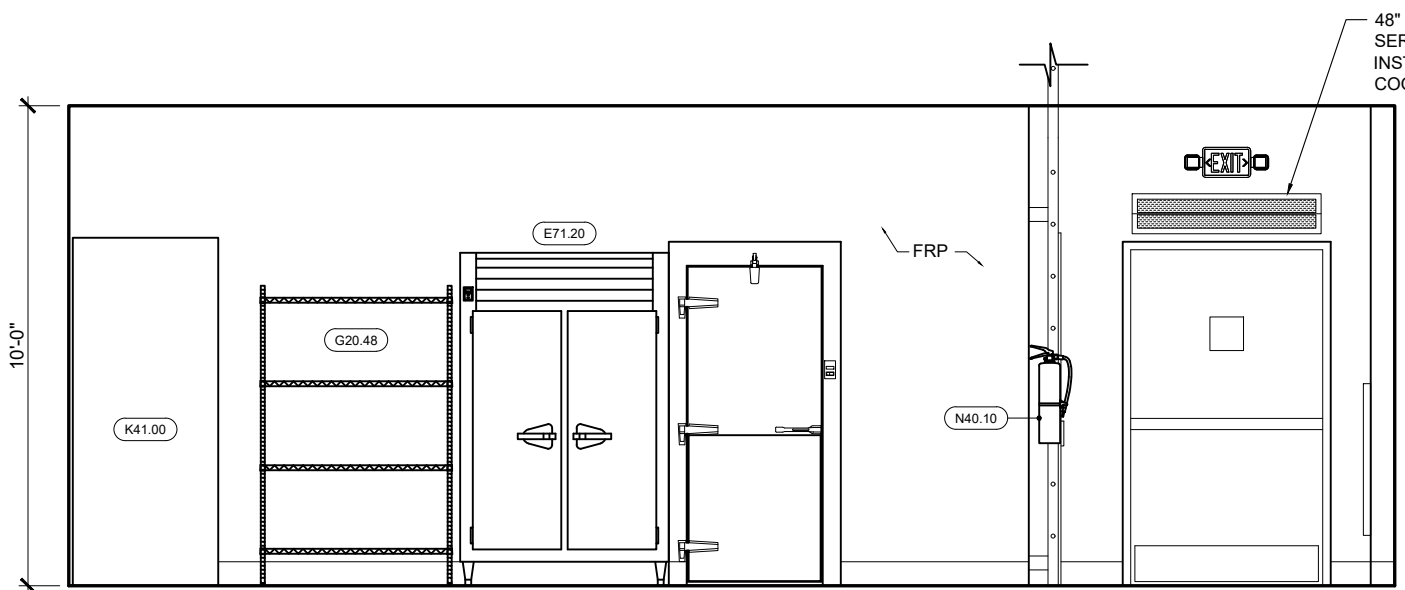


4 PREP AREA
A9.1 SCALE: 1/4" = 1'-0"

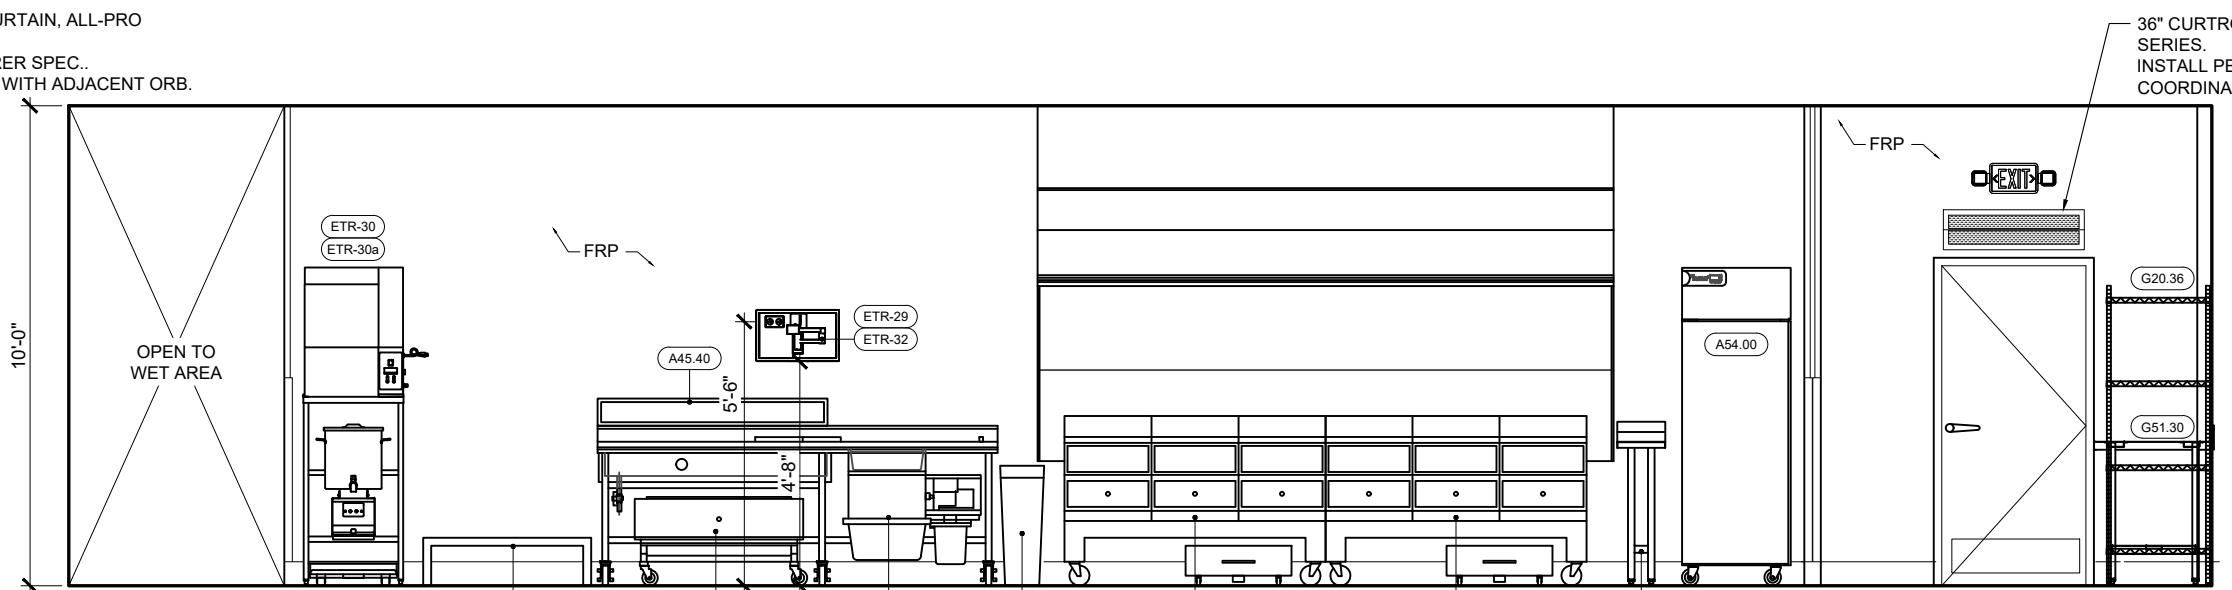


5 PREP AREA
A9.1 SCALE: 1/4" = 1'-0"

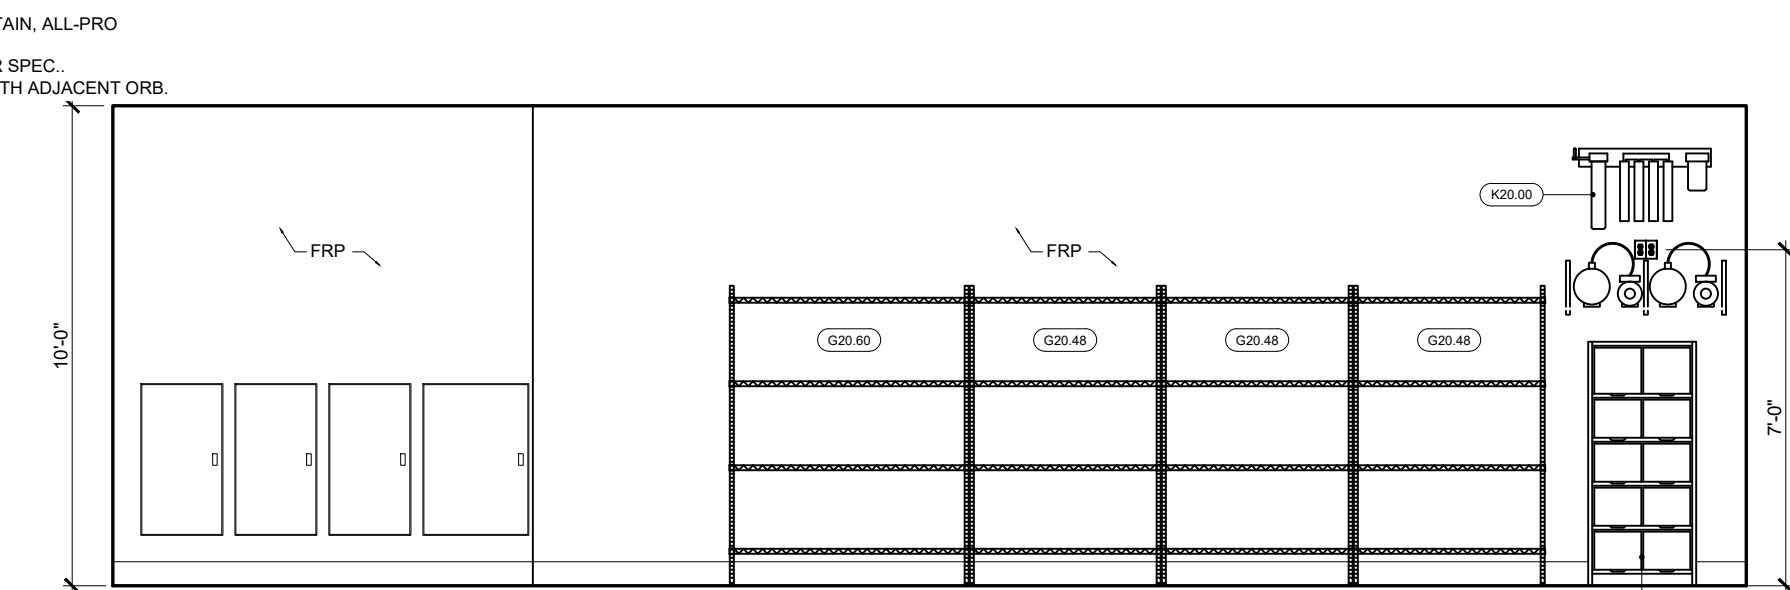


6 WET AREA
A9.1 SCALE: 1/4" = 1'-0"

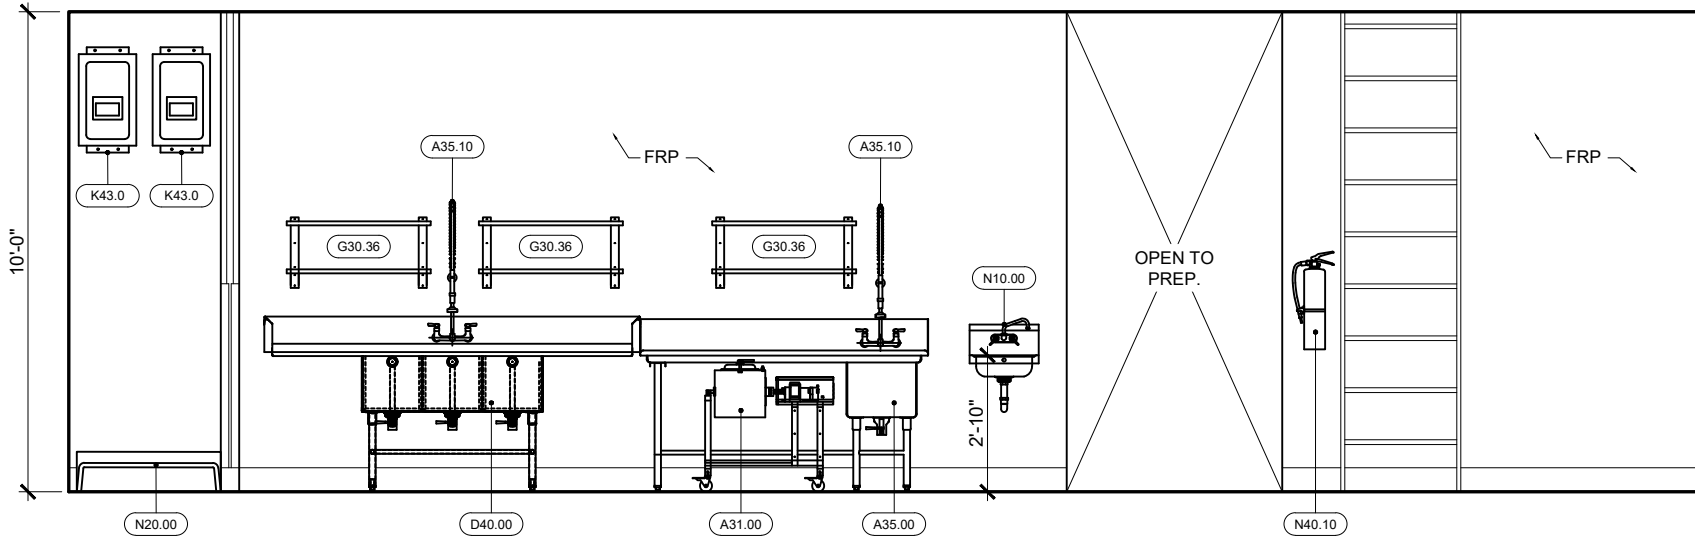



7 WET AREA
A9.1 SCALE: 1/4" = 1'-0"

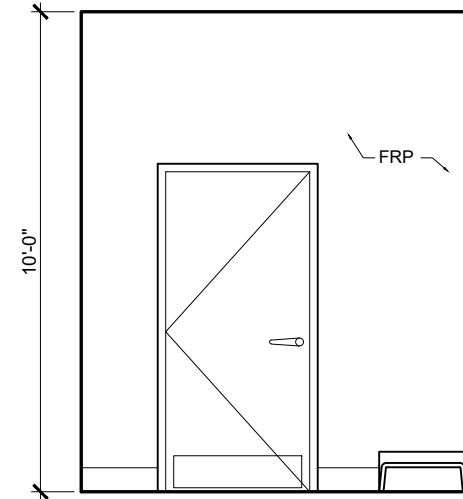

8 WET AREA
A9.1 SCALE: 1/4" = 1'-0"

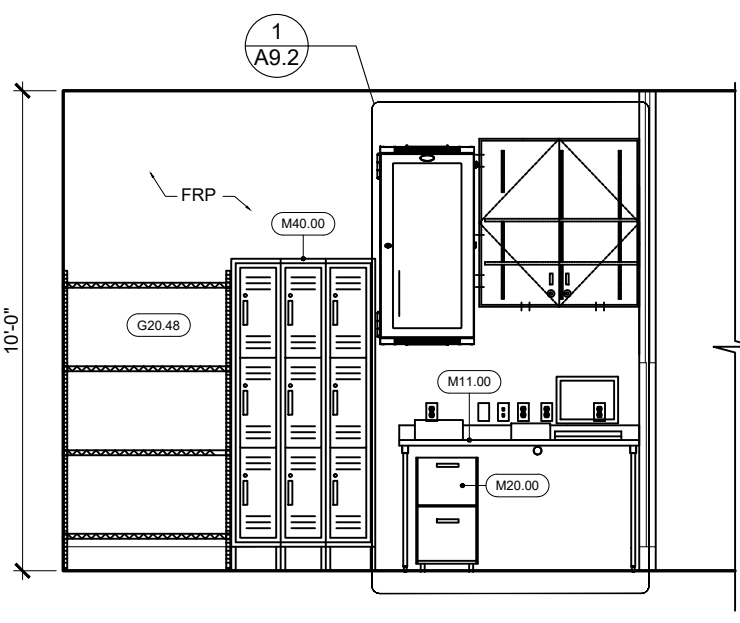


9 PREP AREA
A9.1 SCALE: 1/4" = 1'-0"

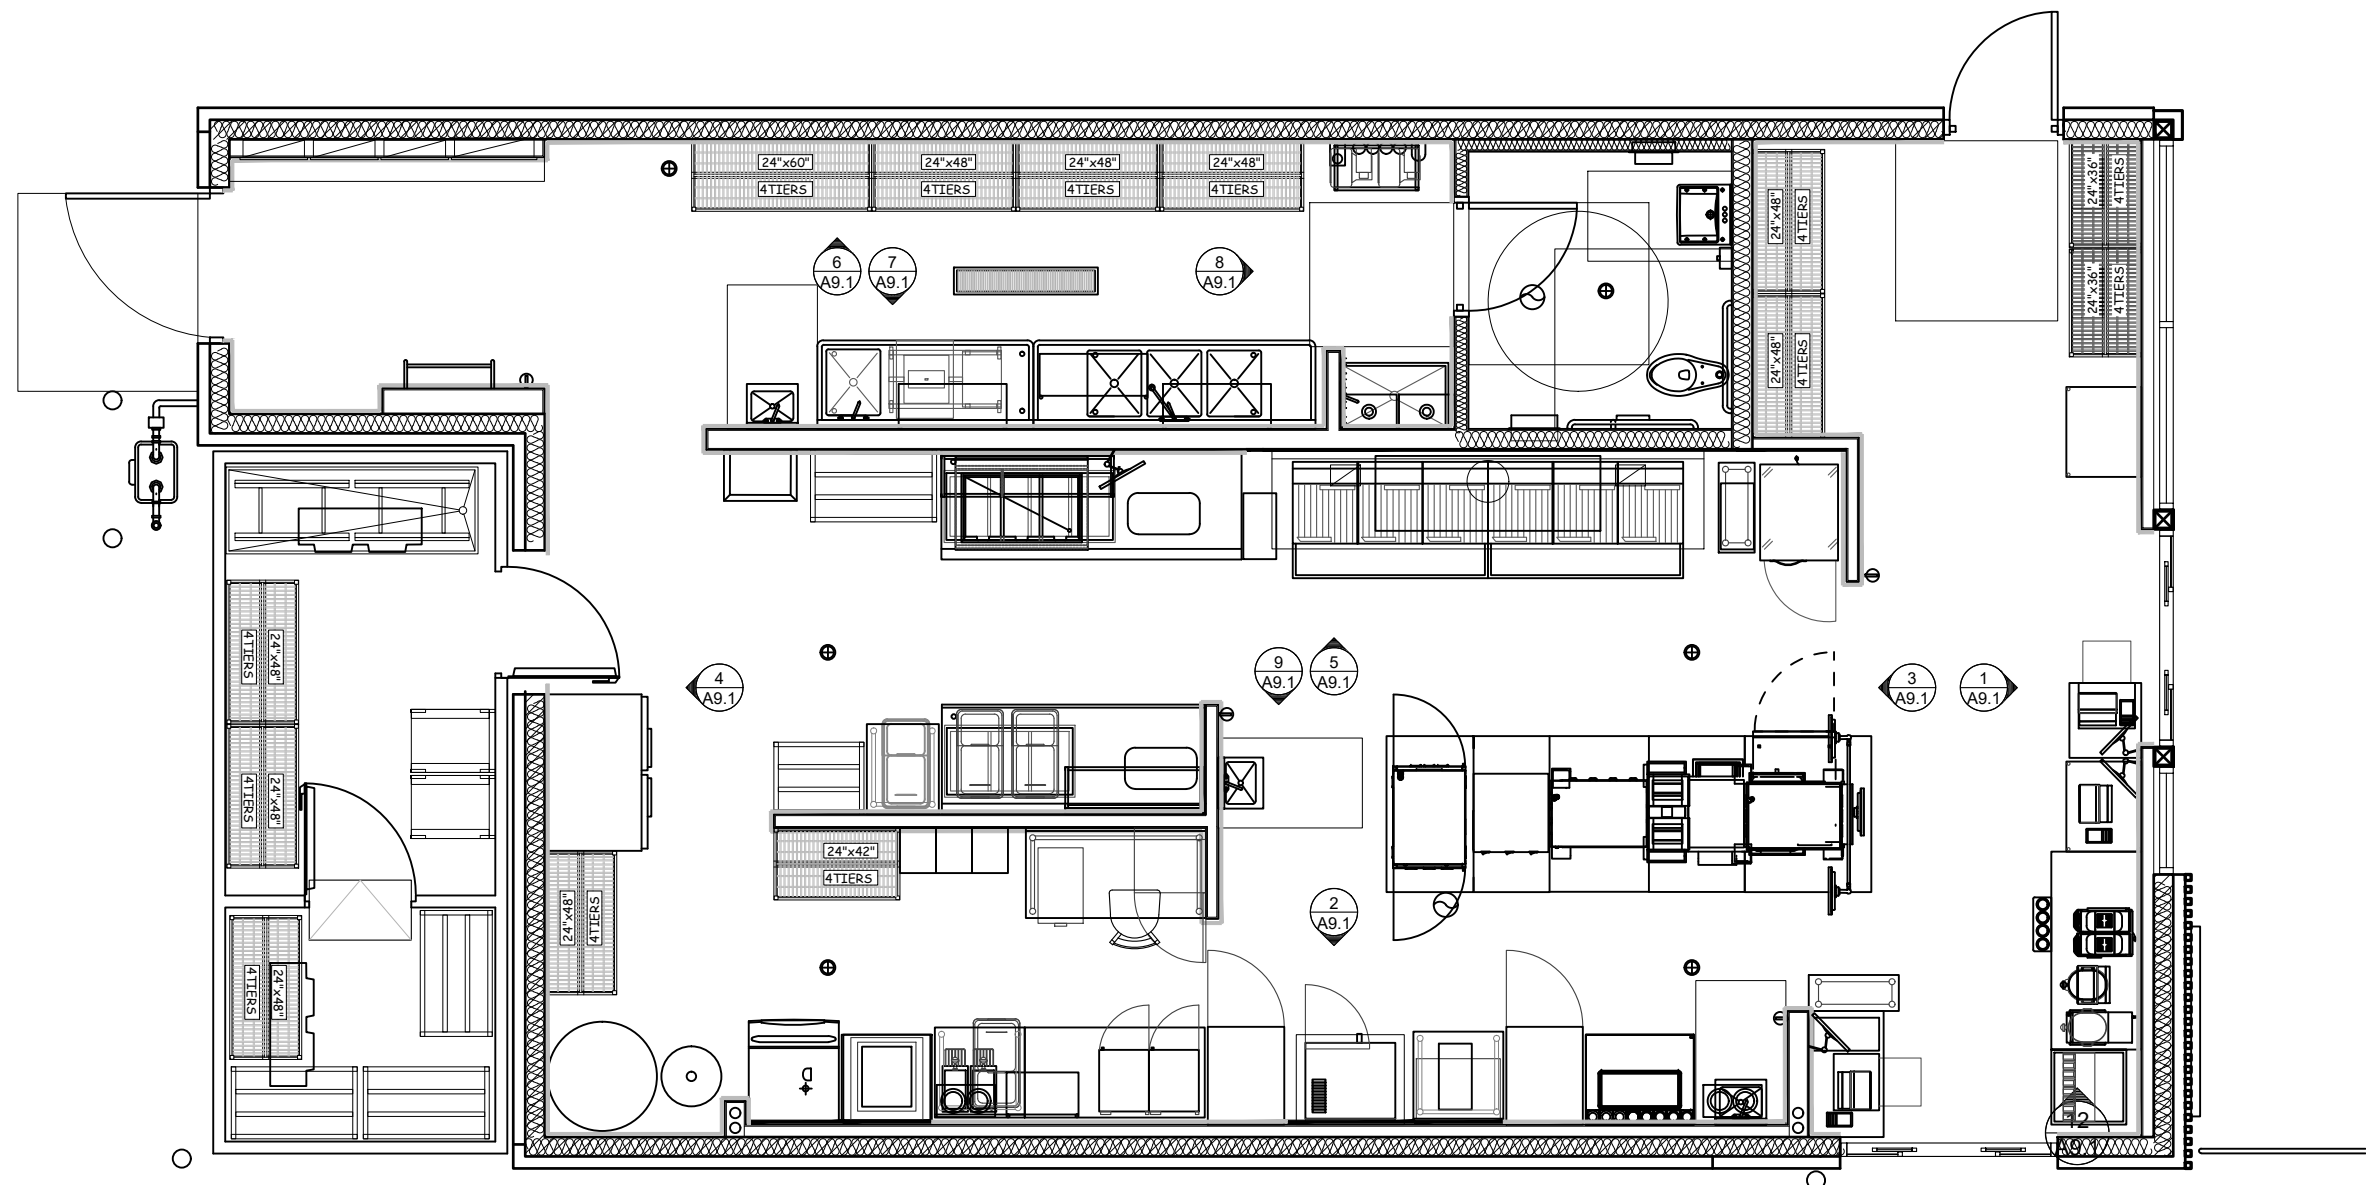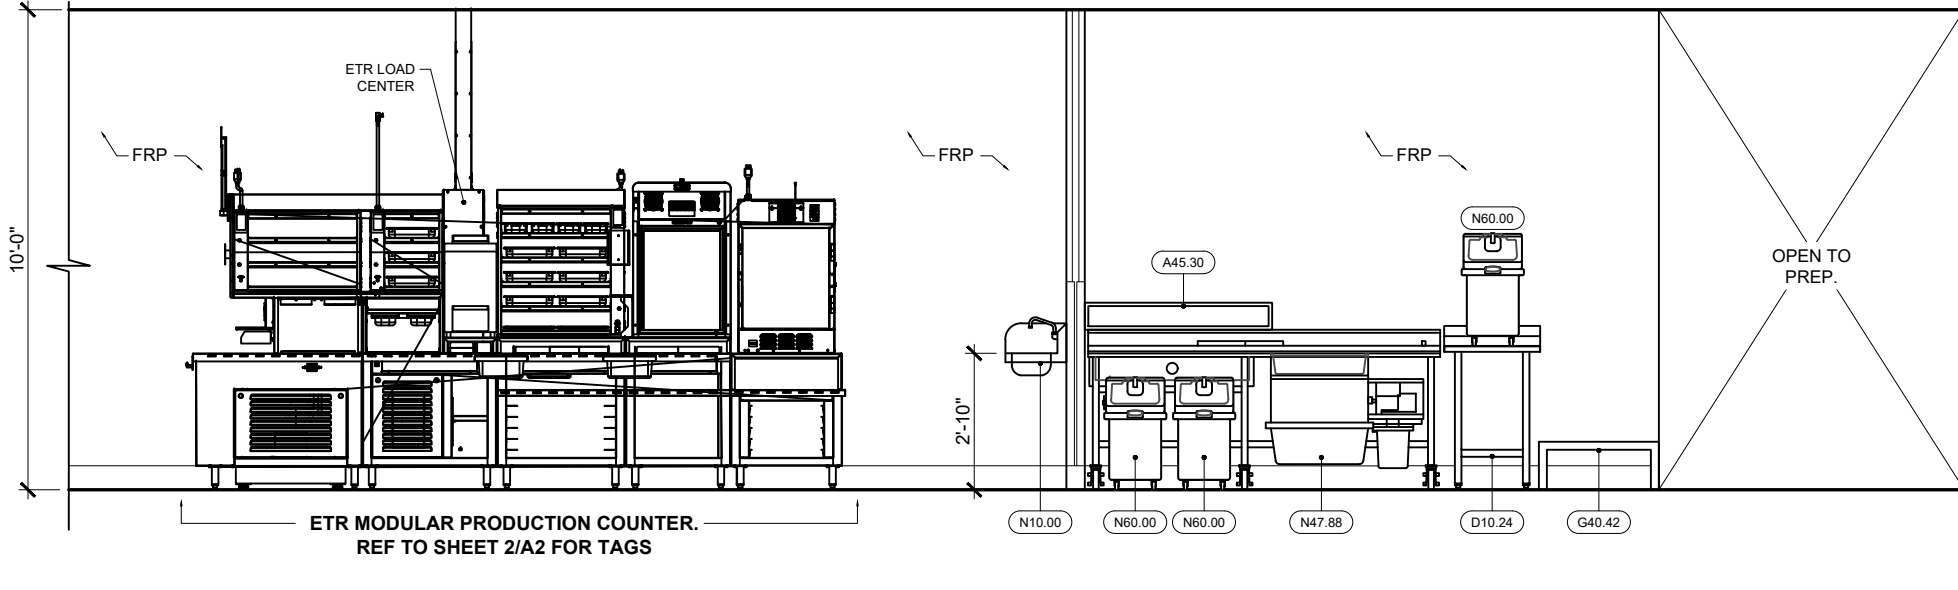


10 LEGEND FLOOR PLAN
A9.1 SCALE: 3/16"=1'-0"

ISSUE TABLE		
No.	Date (mm/dd/yy)	Description
01	09-26-25	DTGO PROTOTYPE DOCUMENTS
REVISIONS		
No.	Date	Description
DRAWINGS REVISED AS PER DESIGN BULLETIN		
No.	Date	Description
THIS DRAWING IS OWNED BY OR LICENSED FOR USE BY POPEYES LOUISIANA KITCHEN (OR ITS AFFILIATED OR RELATED COMPANIES) AND MAY NOT BE REPRODUCED, USED, DOWNLOADED, DISSEMINATED, PUBLISHED, OR TRANSFERRED IN ANY FORM OR BY ANY MEANS, EXCEPT WITH THE PRIOR WRITTEN CONSENT OF POPEYES LOUISIANA KITCHEN. COPYRIGHT INFRINGEMENT IS A VIOLATION OF FEDERAL LAW SUBJECT TO CRIMINAL AND CIVIL PENALTIES.		
THE CONTRACTOR IS TO VERIFY ALL DIMENSIONS AND CONDITIONS ON THE PROJECT AND TO REPORT ANY DISCREPANCIES TO THE POPEYES LOUISIANA KITCHEN REPRESENTATIVE PRIOR TO COMMENCING WORK. THESE DRAWINGS ARE NOT TO BE USED FOR CONSTRUCTION PURPOSES UNLESS INDICATED BY POPEYES LOUISIANA KITCHEN AS "ISSUED FOR CONSTRUCTION".		
Professional Seal		
DESIGNER NOTES: DESIGN GUIDELINE ONLY - NOT FOR PERMIT OR CONSTRUCTION		
THESE DOCUMENTS MUST BE COMPLETED AND / OR MODIFIED BY A LICENSED ARCHITECT AND ENGINEER TO CONFORM TO ALL APPLICABLE CODES, AND SPECIFIC SITE CONDITIONS. THERE IS NO WARRANTY, WHETHER IMPLIED OR EXPRESSED THAT THESE DOCUMENTS MEET THE APPLICABLE CODE REQUIREMENTS. LIABILITY FOR THE DESIGN AND ANY USE OF THE DOCUMENTS IS THE SOLE RESPONSIBILITY OF THE ARCHITECT AND ENGINEER OF RECORD.		
Company Logo		
Project		
Store Type		
Location		
Drawing Title		
Drawn		
Scale		
Project No.		
Checked		
Date		
Drawing No.		

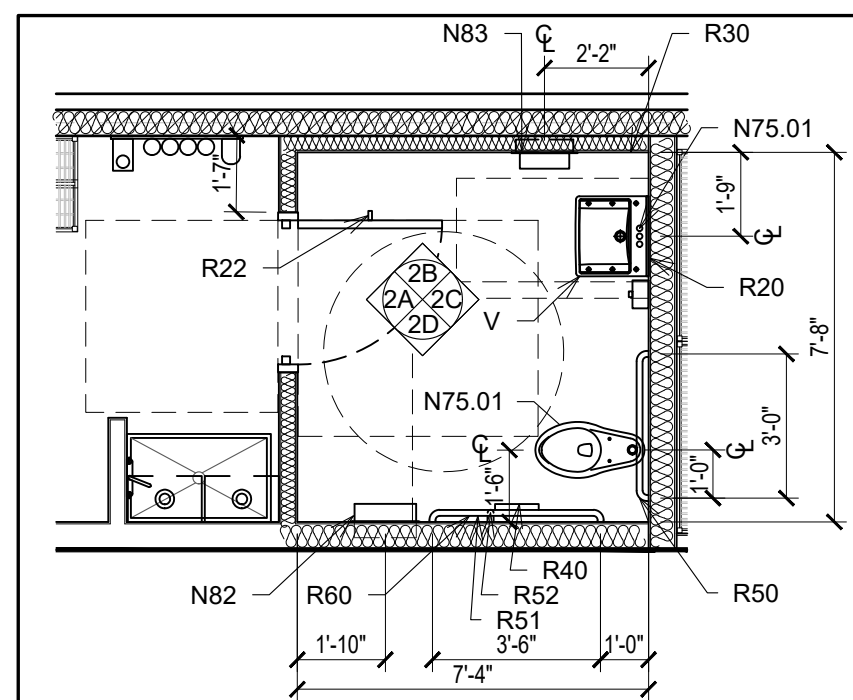


1 **PLAN UNISEX WASHROOM**
A9.3 SCALE: 1/4" = 1'-0"

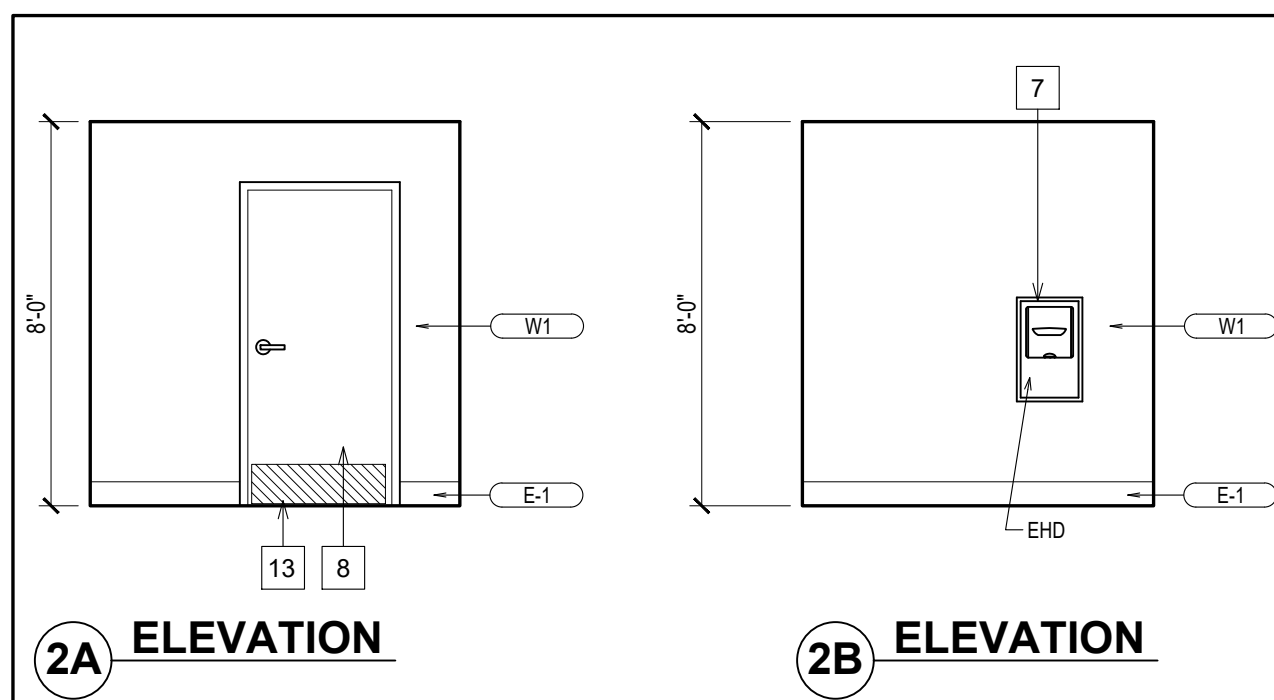


2 ELEVATIONS UNISEX WASHROOM


A9.3 SCALE: 1/4" = 1'-0"

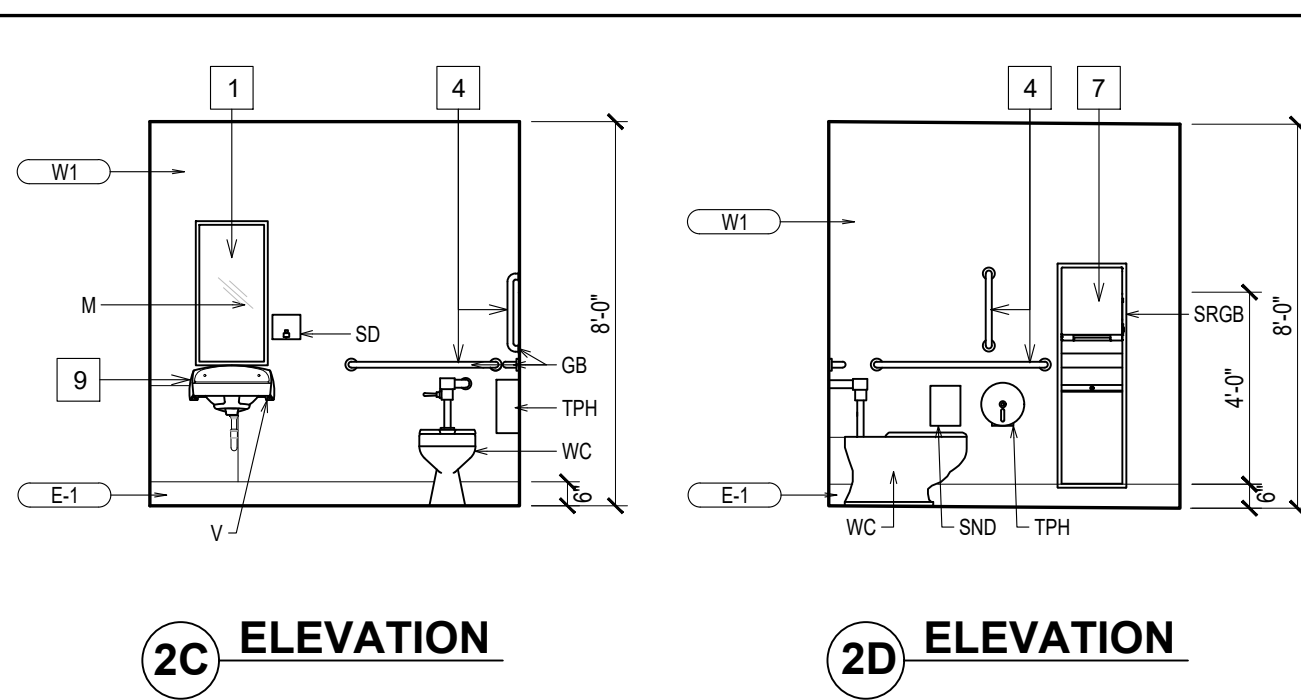


3 N/A
A9.3 SCALE:

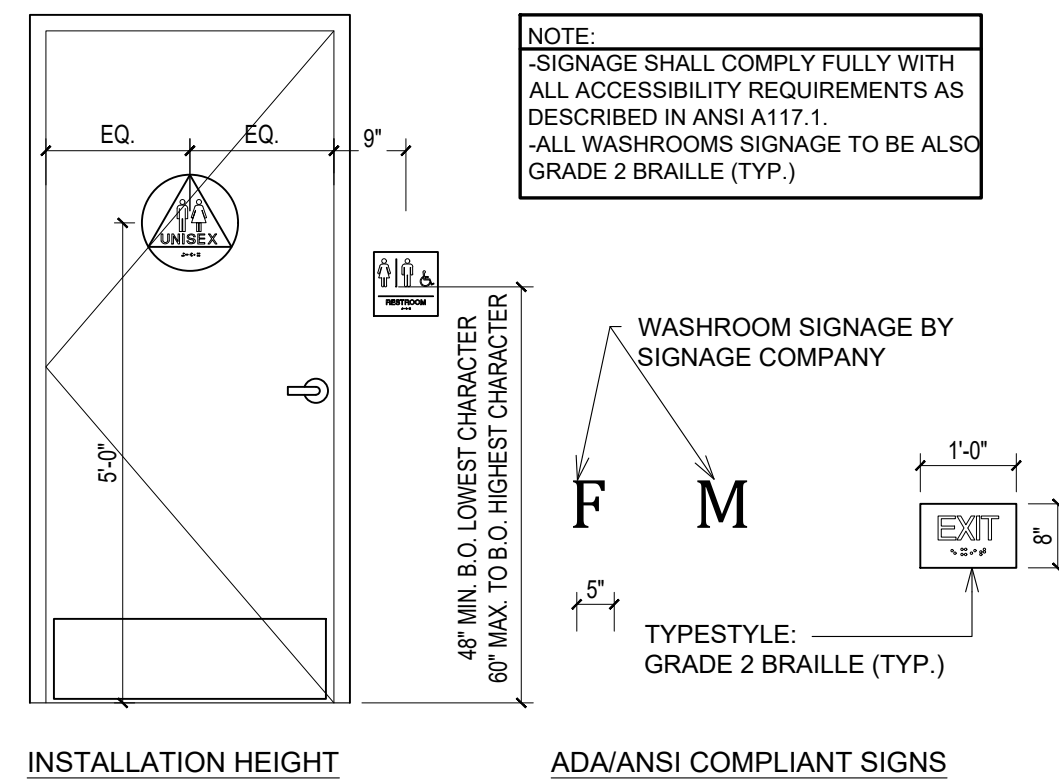




7 ACCESSIBILITY SIGNAGE.

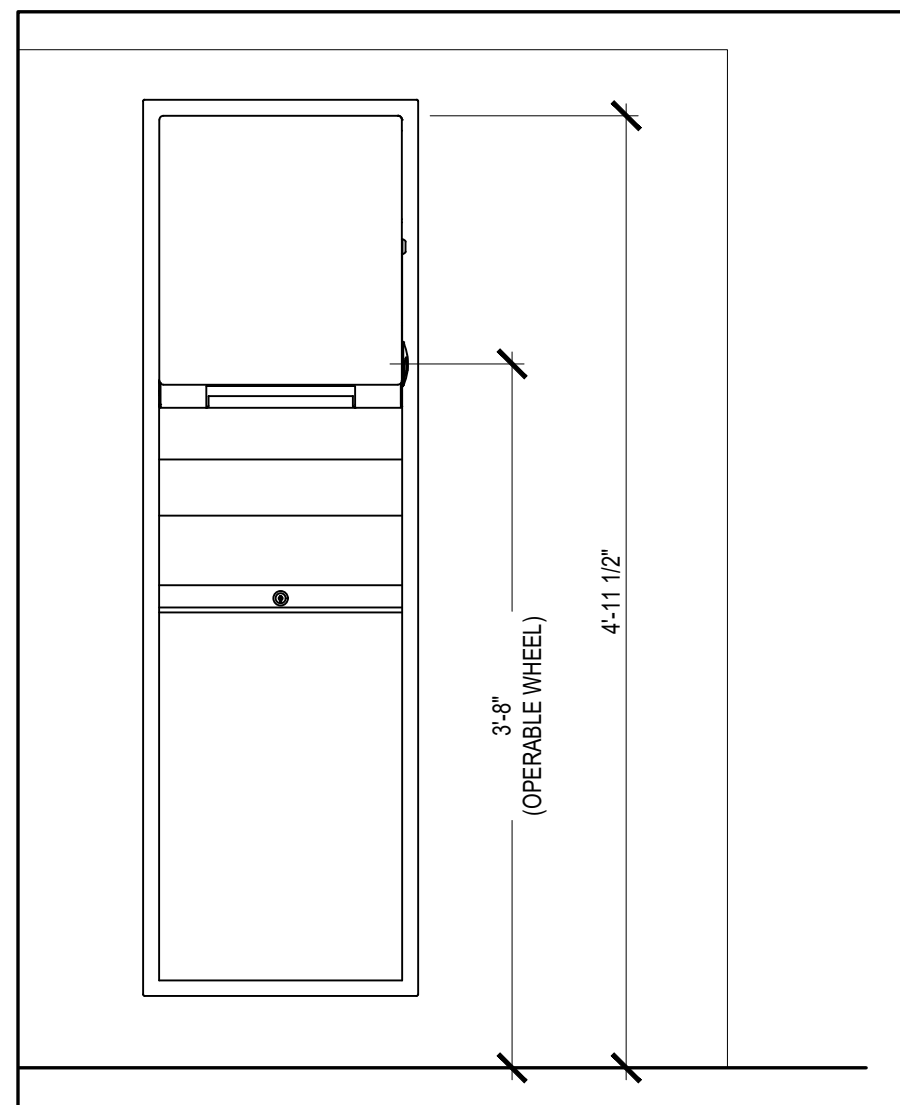


8 **DETAIL @ SEMI-RECESSED**
A9.3 **GARBAGE**
SCALE: 1" = 1'-0"

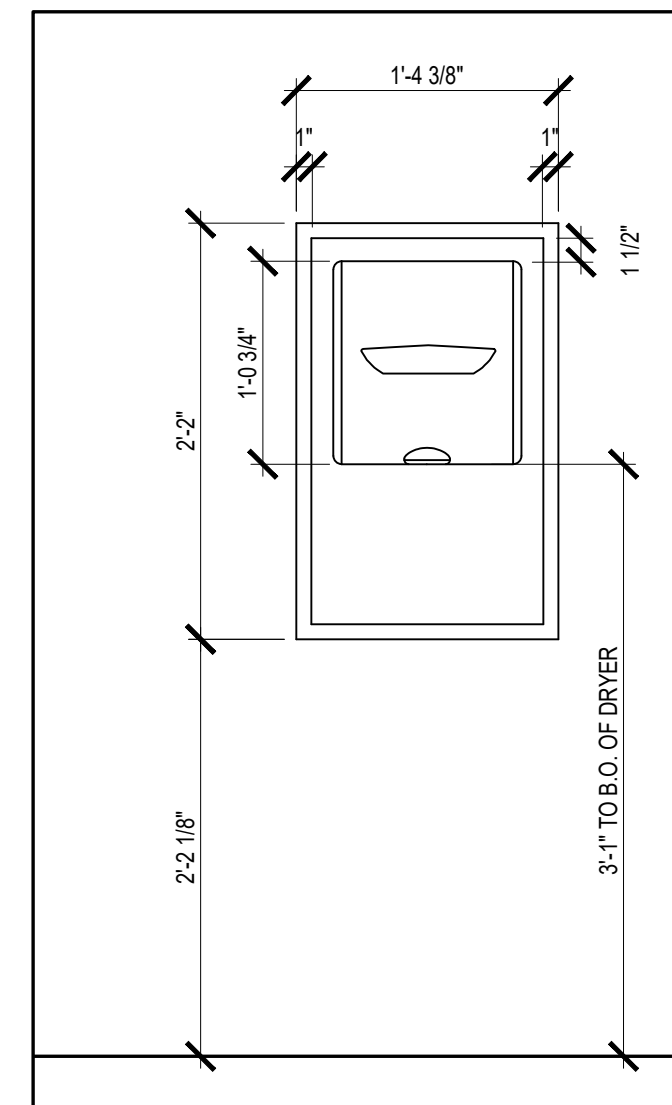


10 **DETAIL @ HAND DRYER**
A9.3 SCALE: 1" = 1'-0"

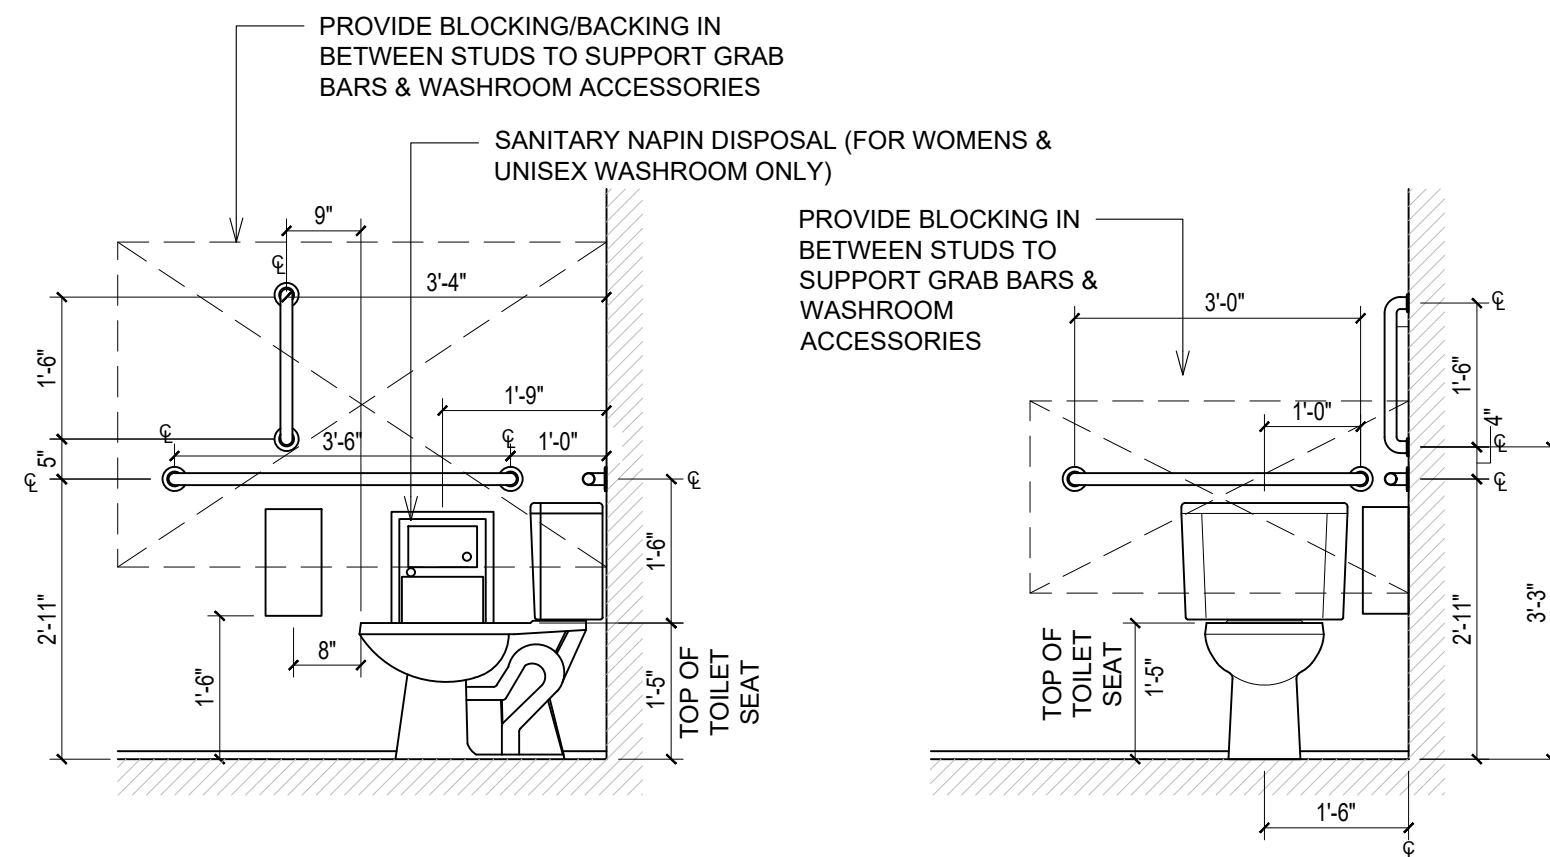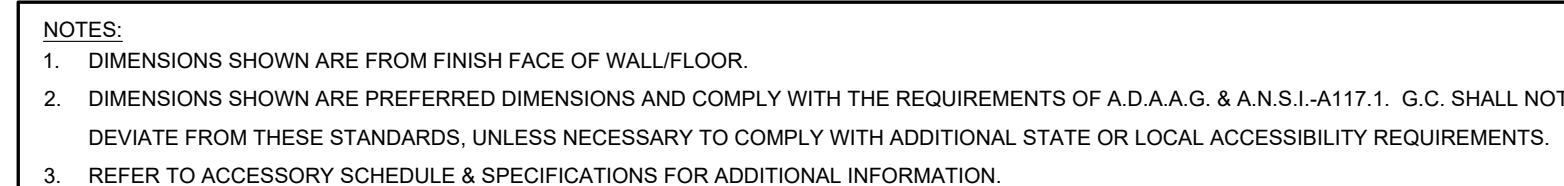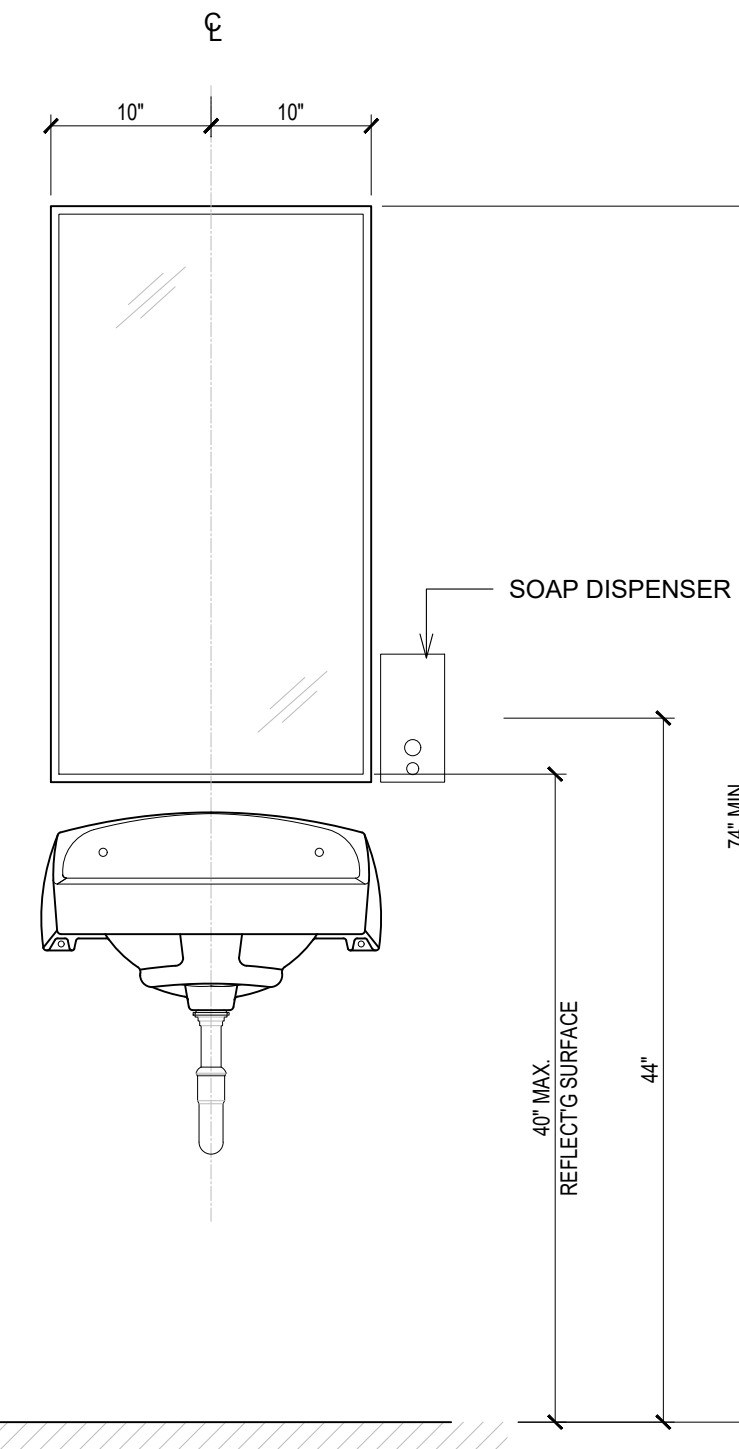


11
A9.3 **DETAIL @ GRAB BARS**
SCALE: 1/2" = 1'-0"

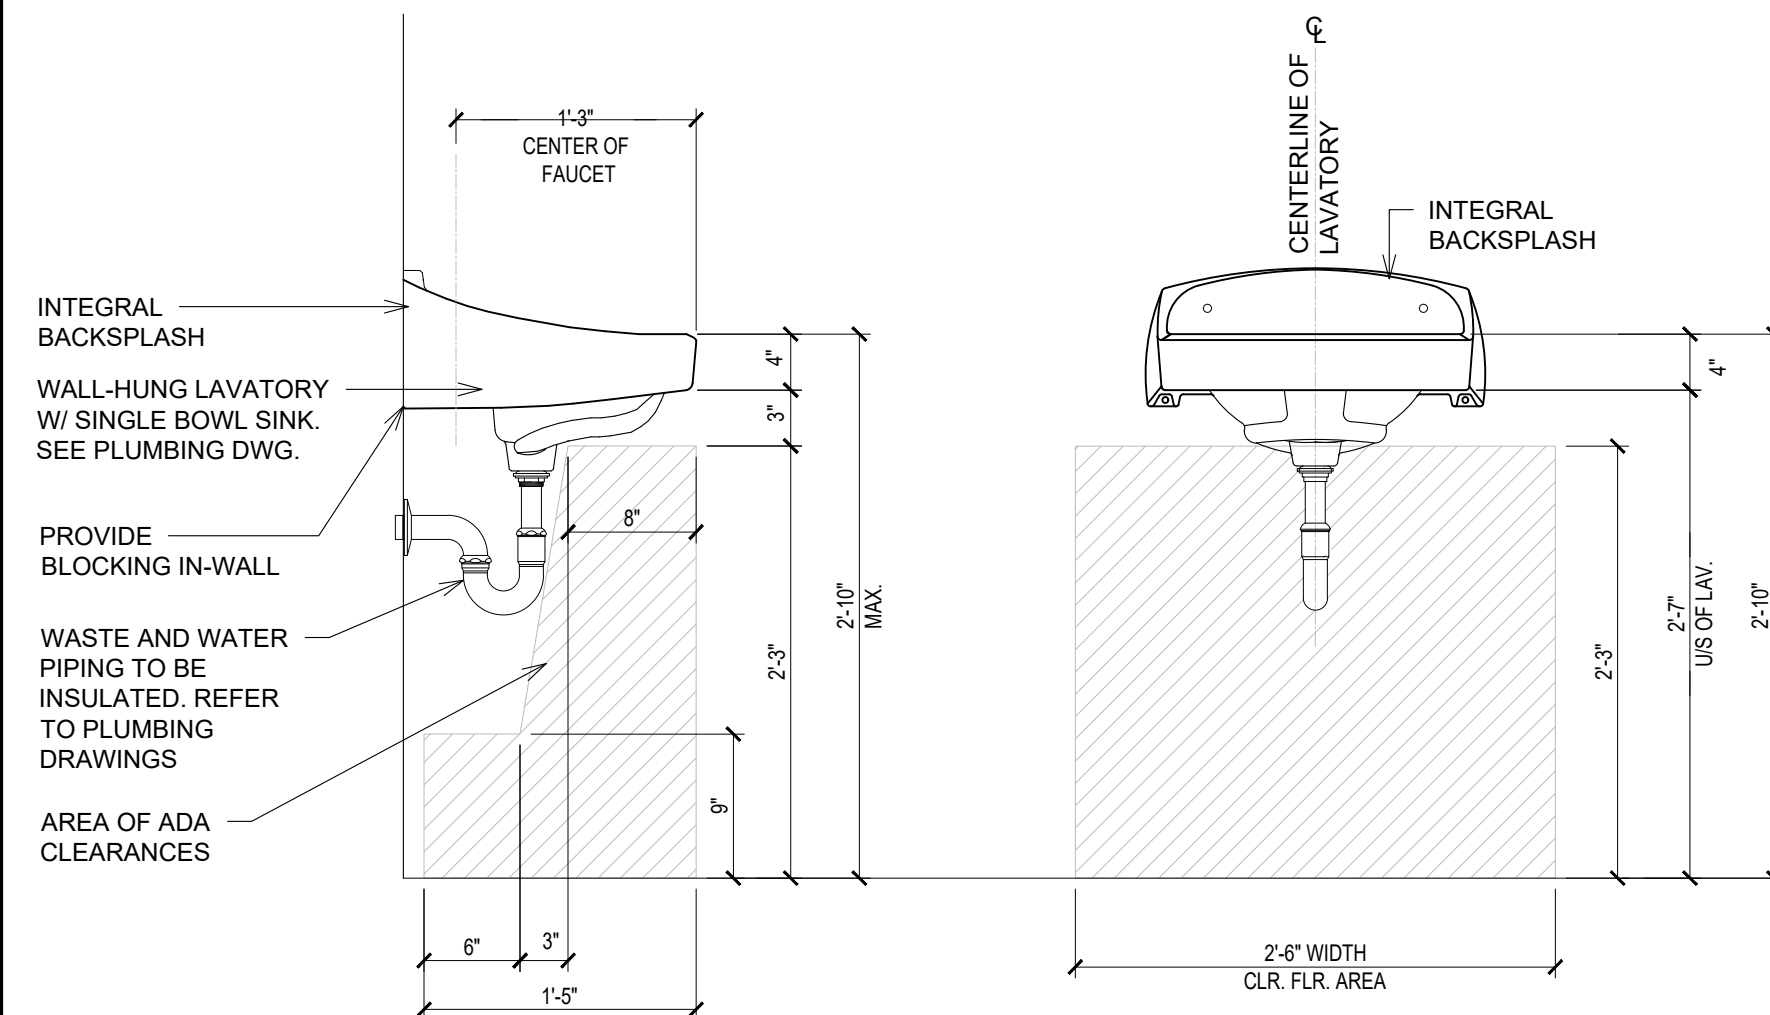

12 **DETAIL @ VANITY**
A9.3 SCALE: 1" = 1'-0"

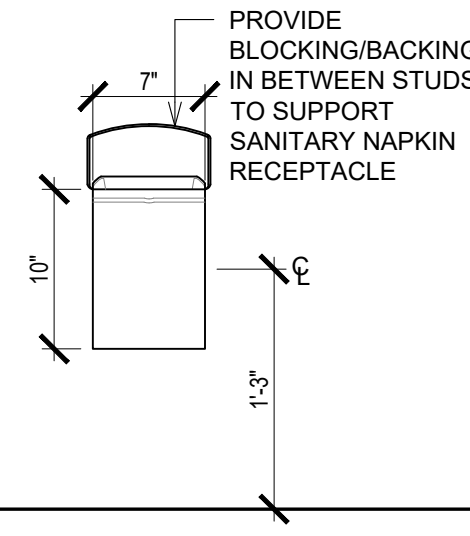

13 **DETAIL @ SANITARY NAPKIN**
A9.3 SCALE: 1" = 1'-0" **RECEPTACLE**

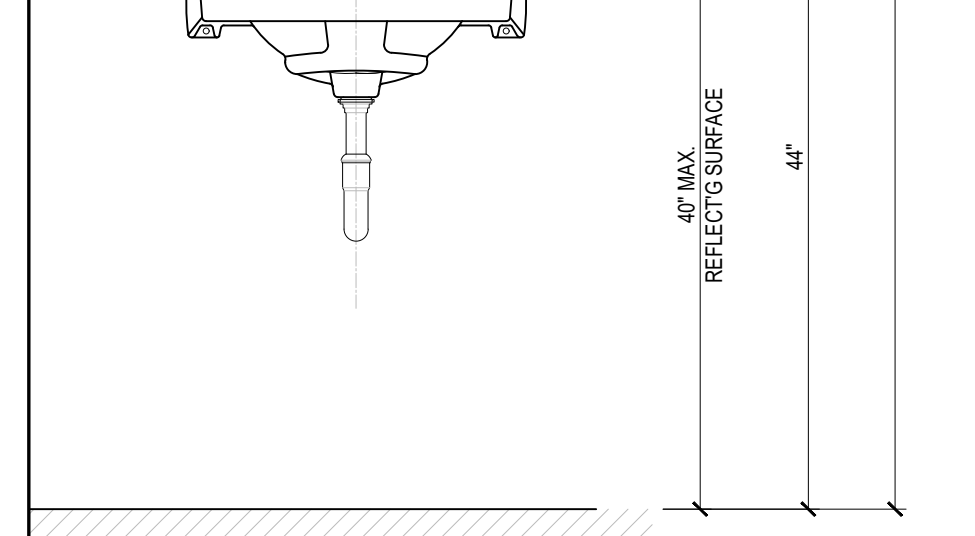

14 **MIRROR AND SOAP DISPENSER DETAIL**
A9.3 SCALE: 1" = 1'-0"

ISSUE TABLE		
No.	Date (mm/dd/yy)	Description
01	09-26-25	DTGO PROTOTYPE DOCUMENTS
REVISIONS		
No.	Date	Description
DRAWINGS REVISED AS PER DESIGN BULLETIN		
No.	Date	Description

THIS DRAWING IS OWNED BY OR LICENSED FOR USE BY POPEYES LOUISIANA KITCHEN (OR ITS AFFILIATED OR RELATED COMPANIES) AND MAY NOT BE REPRODUCED, USED, DOWNLOADED, DISSEMINATED, PUBLISHED, OR TRANSFERRED IN ANY FORM OR BY ANY MEANS, EXCEPT WITH THE PRIOR WRITTEN CONSENT OF POPEYES LOUISIANA KITCHEN. COPYRIGHT INFRINGEMENT IS A VIOLATION OF FEDERAL LAW SUBJECT TO CRIMINAL AND CIVIL PENALTIES.

THE CONTRACTOR IS TO VERIFY ALL DIMENSIONS AND CONDITIONS ON THE PROJECT AND TO REPORT ANY DISCREPANCIES TO THE POPEYES LOUISIANA KITCHEN REPRESENTATIVE PRIOR TO COMMENCING WORK. THESE DRAWINGS ARE NOT TO BE USED FOR ANY OTHER PROJECTS OR PURPOSES INDICATED BY POPEYES LOUISIANA KITCHEN AS "ISSUED FOR CONSTRUCTION".

Professional Seal

DESIGNER NOTES:
DESIGN GUIDELINE ONLY - NOT FOR PERMIT OR CONSTRUCTION

THESE DOCUMENTS MUST BE COMPLETED AND/OR MODIFIED BY A LICENSED ARCHITECT AND ENGINEER TO CONFORM TO ALL APPLICABLE CODES, AND SPECIFIC SITE CONDITIONS. THERE IS NO WARRANTY, WHETHER IMPLIED OR EXPRESSED THAT THESE DOCUMENTS MEET THE APPLICABLE CODE REQUIREMENTS.

LIABILITY FOR THE DESIGN AND ANY USE OF THE DOCUMENTS IS THE SOLE RESPONSIBILITY OF THE ARCHITECT AND ENGINEER OF RECORD.

Company Logo

Project



POPEYES

Store Type	US DTGO PROTOTYPE
------------	-------------------

	Location
--	----------

PROTOTYPE
DTGO (U.S.)

CITY, STATE

	Drawing Title
--	---------------

WASHROOM DETAILS

Drawn	XX XX
-------	-------

Checked	XX
---------	----

Scale
AS NOTED

Date ##.##.####

XX

493

1. GENERAL CONTRACTOR TO PROVIDE MINIMUM 1 CASE OF EACH SET OF FLOOR TILES, WALL TILES & CEILING TILES AND 1 GALLON OF EACH PAINT COLOUR FOR FUTURE USE. THESE MATERIALS ARE TO BE LEFT ON SITE WITH THE RESTAURANT OWNER.
2. IF APPLICABLE, PROVIDE & INSTALL SCHLUTER STRIP (SHL-3) AT ALL FLOOR TILE TRANSITION THROUGHOUT THE ENTIRE STORE. REFER TO FINISHING SCHEDULE.
3. PROVIDE & INSTALL SCHLUTER-DILEX-KSN AT LOCATION OF FLOOR TILE AT DELIVERY DOOR. REFER TO FINISHING SCHEDULE.
4. G.C. TO SEAL ALL GWB / MILLWORK JOINTS WITH CLEAR SILICONE CAULKING AFTER COMPLETION OF PAINTING, FINAL CLEANING.

[illegible]

ISSUE TABLE		
No.	Date (mm/dd/yy)	Description
01	09-26-25	DTGO PROTOTYPE DOCUMENTS
REVISIONS		
No.	Date	Description
DRAWINGS REVISED AS PER DESIGN BULLETIN		
No.	Date	Description
THIS DRAWING IS OWNED BY OR LICENSED FOR USE BY POPEYES LOUISIANA KITCHEN (OR ITS AFFILIATED OR RELATED COMPANIES) AND MAY NOT BE REPRODUCED, USED, DOWNLOADED, DISSEMINATED, PUBLISHED, OR TRANSFERRED IN ANY FORM OR BY ANY MEANS, EXCEPT WITH THE PRIOR WRITTEN CONSENT OF POPEYES LOUISIANA KITCHEN. COPYRIGHT INFRINGEMENT IS A VIOLATION OF FEDERAL LAW SUBJECT TO CRIMINAL AND CIVIL PENALTIES. THE CONTRACTOR IS TO VERIFY ALL DIMENSIONS AND CONDITIONS ON THE PROJECT AND TO REPORT ANY DISCREPANCIES TO THE POPEYES LOUISIANA KITCHEN REPRESENTATIVE PRIOR TO COMMENCING WORK. THESE DRAWINGS ARE NOT TO BE USED FOR CONSTRUCTION PURPOSES UNLESS INDICATED BY POPEYES LOUISIANA KITCHEN AS "ISSUED FOR CONSTRUCTION".		
Professional Seal		
DESIGNER NOTES: DESIGN GUIDELINE ONLY - NOT FOR PERMIT OR CONSTRUCTION THESE DOCUMENTS MUST BE COMPLETED AND / OR MODIFIED BY A LICENSED ARCHITECT AND ENGINEER TO CONFORM TO ALL APPLICABLE CODES, AND SPECIFIC SITE CONDITIONS. THERE IS NO WARRANTY, WHETHER IMPLIED OR EXPRESSED THAT THESE DOCUMENTS MEET THE APPLICABLE CODE REQUIREMENTS. LIABILITY FOR THE DESIGN AND ANY USE OF THE DOCUMENTS IS THE SOLE RESPONSIBILITY OF THE ARCHITECT AND ENGINEER OF RECORD.		
Company Logo		
Project		
The Project section contains two logos. The first is the Louisiana Kitchen logo, which consists of a circular emblem. Inside the circle is a stylized chicken silhouette facing right. Above the chicken is the word 'LOUISIANA' in an arc, and below it is 'KITCHEN' in an arc. To the left of the chicken is the year '19' and to the right is '72'. Below the circular emblem is the 'POPEYES' logo in its characteristic bold, italicized font.		
Store Type	US DTGO PROTOTYPE	
Location	PROTOTYPE DTGO (U.S.) CITY, STATE	
Drawing Title	TILE PLAN AND FINISHING SCHEDULE	
Drawn	XX	Checked XX
Scale	1/4"=1'-0"	Date ###.##.####
Project No.	XX	Drawing No. A10

DOOR AND FRAME SCHEDULE											
DOORS						FRAMES			HARDWARE	REMARKS	
NO.	SIZE	R.O SIZE	TYPE	MAT.	FIN.	TYPE	MAT.	FIN.	SET NO.		
(103)	3'-0" x 6'-8" x 1-3/4"	DOOR WIDTH + 1-1/4" x DOOR HEIGHT + 5/8"	E	HM	--	F2	HM KNOCKDOWN	--	03	UNDERCUT DOOR 5/8". DOORS / FRAMES TO BE PAINTED AS PER POPEYES DECOR PACKAGE. TRANSITION TO OCCUR AT DOOR JAMB.	
(106)	4'-0" x 7'-0" x 1-3/4"	DOOR WIDTH + 1-1/4" x DOOR HEIGHT + 5/8"	B	HM/N	--	F2	HM/N	--	01	16 GA. GALVANIZED LOCKNET SECURITY DOOR.	
(107)	3'-0" x 7'-0" x 1-3/4"	DOOR WIDTH + 1-1/4" x DOOR HEIGHT + 5/8"	B	HM/N	--	F2	HM/N	--	06	16 GA. GALVANIZED LOCKNET SECURITY DOOR.	
ABBREVIATIONS											
AL	ALUMINUM	HM	HOLLOW METAL			PLY	PLYWOOD	P.LAM	PLASTIC LAMINATE	WD	WOOD
GL	GLASS	HMIN	HOLLOW METAL INSULATED			PM	PREFINISHED METAL	MILLWK	MILLWORK		PROVIDED BY DOOR MANUFACTURER

EXTERIOR WINDOW SCHEDULE

Diagram W0: Single window. Rough opening: 6'-0 5/8" (height) x 9'-0" (width). Frame dimensions: 2'-5 3/8" (height) x 2" (width). Glazing dimensions: 2'-7 1/2" (height) x 3'-0" (width). Glazing provided with reflective privacy glazing film.

Diagram W1: Double window. Rough opening: 6'-0 5/8" (height) x 10'-3 1/2" (width). Frame dimensions: 2'-5 3/8" (height) x 2" (width). Glazing dimensions: 4'-10 1/2" (height) x 4'-10 1/2" (width). Glazing provided with reflective privacy glazing film.

Diagram W2: Double window. Rough opening: 6'-0 1/2" (height) x 9'-0" (width). Frame dimensions: 2'-5 3/8" (height) x 2" (width). Glazing dimensions: 4'-10 1/2" (height) x 4'-10 1/2" (width). Glazing provided with reflective privacy glazing film. Transaction window dimensions: 6'-0 1/2" (height) x 3'-5 1/2" (width). No privacy film to be applied at upper glazing.

DOOR HARDWARE SCHEDULE					
HARDWARE SET NO. 1:(LOCKNET SERIES DOOR PACKAGE) DOOR FRAME & HARDWARE INCLUDING ONE- WAY VISION PANEL W/ FLAP, CONTINUOUS HINGE, HEAVY DUTY CLOSER AND PANIC HARDWARE ORDERED THROUGH LOCKNET (800) 887-4307 1 EA. 3'-6" X 7'-0" X 1.75" X 16 GA. X G60 GALVANIZED LOCKNET SECURITY DOOR 1 EA. 3'-6" X 7'-0" X (5'-7/8" OR 6-3/4") JAMB DEPTH X 14 GA. X G60 GALVANIZED X WELDED IN PLACE EOA X 1/4" X 2-1/2" HR PLATE SPREADER BAR X 4-SIDED WELDED DOOR FRAME X FACTORY FINISH PAINTED 8 EA. 3/4"Ø COVER PLUGS (BLACK) 1 EA. AIR LOUVER VLF-IG-PVC-1/2" LEXAN - 9" X 9" GALVANIZED SECURITY VISION 1 EA. PEMKO CDHFM82SLF-HD FULL MORTISE CONT. GEARED ALUM. HINGE X 628 1 EA. SECURITY LATCH GUARD X FULL LENGTH X TORX SD/ST SMS X FACTORY FINISH 1 EA. ARROW 1250S X EO X AL EXIT DEVICE 1 EA. DORMA 8616 X DS X FCOV S SN1 X AL CLOSER 1 EA. ROCKWOOD 24" X 40" X .050 X US32D X SECURITY TORX SD/ST SMS ARMOR PLATE ON PUSH SIDE 1 EA. PEMKO 171A X 42" X DOUBLE NOTCH CUT ENDS X THRESHOLD 1 EA. PEMKO 346C X 46" AL OVERHEAD RAIN DRIP X SECURITY TORX SD/ST SMS 1 EA. PEMKO 221APK X 42" AL COMBINATION KICK PLAT & DOOR SHOE X TORX 1 SET. P8512 X CONT. PERIMETER WEATHER SEAL (BLACK) 1 EA. INSTALLATION KIT (PER LOCKNET) 1 EA. CARDBOARD PACKAGING (2 PIECE BOX) 1 EA. DELIVERED ON FULL LENGTH WOODEN PALLET		HARDWARE SET NO. 3: 1-1/2 PR. HINGES 1 EA. LATCHSET W/LOCK 1 EA. FLOOR STOP 1 EA. KICKPLATE 1 EA. COAT HOOK 1 EA. CLOSER McKINNEY SCHLAGE BALDWIN BURNS JACKNOB LCN BEARING HINGES,4-1/2" X 4-1/2" US26D SATURN X US26D #4000 FLOOR MOUNT 8" X 30" X 8" 16GA. US628 #400 WITH RUBBER BUMPER 1460 ALUMINUM CLOSER FOLLOWING ITEMS PROVIDED & INSTALLED BY G.C.: 1 EA. SIGN 1 EA. SIGN HANDICAP ACCESSIBILITY (ADA) AS REQD: DOOR #103 HARDWARE SET NO. 4: NOT USED			
HARDWARE SET NO. 2: (BY YKK AP AMERICA INC.) NOT USED		HARDWARE SET NO. 5: NOT USED			
		HARDWARE SET NO. 6:(LOCKNET SERIES DOOR PACKAGE) DOOR FRAME & HARDWARE INCLUDING ONE- WAY VISION PANEL W/ FLAP, CONTINUOUS HINGE, HEAVY DUTY CLOSER AND PANIC HARDWARE ORDERED THROUGH LOCKNET (800) 887-4307 1 EA. 3'-0" X 7'-0" X 1.75" X 16 GA. X G60 GALVANIZED LOCKNET SECURITY DOOR 1 EA. 3'-0" X 7'-0" X (5'-7/8" OR 6-3/4") JAMB DEPTH X 14 GA. X G60 GALVANIZED X WELDED IN PLACE EOA X 1/4" X 2-1/2" HR PLATE SPREADER BAR X 4-SIDED WELDED DOOR FRAME X FACTORY FINISH PAINTED 8 EA. 3/4"Ø COVER PLUGS (BLACK) 1 EA. AIR LOUVER VLF-IG-PVC-1/2" LEXAN - 9" X 9" GALVANIZED SECURITY VISION 1 EA. PEMKO CDHFM82SLF-HD FULL MORTISE CONT. GEARED ALUM. HINGE X 628 1 EA. SECURITY LATCH GUARD X FULL LENGTH X TORX SD/ST SMS X FACTORY FINISH 1 EA. ARROW 1250S X EO X AL EXIT DEVICE 1 EA. DORMA 8616 X DS X FCOV S SN1 X AL CLOSER 1 EA. ROCKWOOD 24" X 40" X .050 X US32D X SECURITY TORX SD/ST SMS ARMOR PLATE ON PUSH SIDE 1 EA. PEMKO 171A X 36" X DOUBLE NOTCH CUT ENDS X THRESHOLD 1 EA. PEMKO 346C X 40" AL OVERHEAD RAIN DRIP X SECURITY TORX SD/ST SMS 1 EA. PEMKO 221APK X 36" AL COMBINATION KICK PLAT & DOOR SHOE X TORX 1 SET. P8512 X CONT. PERIMETER WEATHER SEAL (BLACK) 1 EA. INSTALLATION KIT (PER LOCKNET) 1 EA. CARDBOARD PACKAGING (2 PIECE BOX) 1 EA. DELIVERED ON FULL LENGTH WOODEN PALLET			
HARDWARE SCHEDULE NOTES: 1. ALL HARDWARE IS NEW. 2. ALL DOOR LOCKSETS / LATCHES SHALL BE "LEVER TYPE" IN COMPLIANCE WITH A.D.A.A.G. SECTION 4.1.3.9). 3. ALL DOOR HANDLES, PULLS, LATCHES, LOCKS, AND/OR OTHER OPERATING DEVICES SHALL BE INSTALLED BETWEEN 34" MINIMUM AND 48" MAXIMUM ABOVE FINISHED FLOOR. 4. ALL DOOR THRESHOLDS SHALL BE 1/2" HIGH MAXIMUM. 5. ALL DOOR CLOSERS SHALL BE ADJUSTED SO THAT FROM THE OPEN POSITION OF 70 DEGREES, THE DOOR WILL TAKE AT LEAST 3 SECONDS TO MOVE TO A POINT 3 INCHES FROM THE LATCH, MEASURED TO THE LEAD EDGE (A.D.A.A.G. 4.13.10).					

[illegible]

DRIVE-THRU AND WALK-UP WINDOW SCHEDULE

The image contains two main architectural drawings of a window unit, labeled 'W5', which is a 'DRIVE-THRU WINDOW'.

VIEW FROM EXTERIOR: This drawing shows the window from the outside. It is a double-hung style window with two sashes. The overall width is 6'-0 1/2" and the overall height is 9'-0". The centerlines of the windows are indicated. The window is flanked by two panels labeled 'GL-2'. The window unit is labeled 'W5' with arrows pointing outwards. Below the window, there are two panels labeled 'SLIDE'. The window is set into a wall. Dimensions include 2'-10 1/2" for the top section, 3'-5 1/2" for the middle section, and 2'-8" for the bottom section. A note below the drawing says 'SEE ELEVATIONS (A5 & A5.1) FOR SILL CONDITION AT WINDOWS, IE SOLID OR GLAZING.' and '2'-10" ADA'.

ELEVATION: This drawing shows the side profile of the window. It shows the window frame and the glass. The overall height is 9'-0". The window is set into a wall. Dimensions include 6'-6" for the top section, 3'-5 1/2" for the middle section, and 2'-8" for the bottom section. The window is labeled 'W5' with arrows pointing outwards. The window unit is labeled 'SLIDE'. The window is set into a wall. A note below the drawing says 'SEE ELEVATIONS (A5 & A5.1) FOR SILL CONDITION AT WINDOWS, IE SOLID OR GLAZING.' and '2'-8" CRI'.

NOTES:

1. REFER TO SECTION 08 56 19 FOR SPECIFICATIONS FOR ADDITIONAL INFORMATION.
2. REFER TO ELECTRICAL DRAWINGS FOR DRIVE-THRU WINDOW AUDIO & POWER REQUIREMENTS

W5 - DRIVE-THRU WINDOW:

QUICKSERV DT WINDOW
MODEL BP-7241E
ORANGE ANODIZED KYNAR
FACTORY FINISH (CLASS 1, .7 MILS MINIMUM) ALUMINUM

ELEVATION

SCALE: 1/2" = 1'-0"


WINDOW TYPE PRIMARY MANUFACTURER - KAWNEER - KAWNEER TRIFAB VERSAGLASS 451T THERMALLY BROKEN 2"x$\frac{1}{2}$" COLOUR: BLACK ANODIZED - CLASS 2, 000A ANODIZING LOW E TINT ALL GLAZING IN DOORS TO BE SAFETY HEAT TREATED. REFER TO SP4 FOR APPROVED ALTERNATE MANUFACTURERS ALL CALCULK TO MATCH FRAMES (TREMCO DYWIDAG) MAXIMUM U-FACTOR OF FIXED GLAZING ASSEMBLY (GLASS UNIT & ALUMINUM FRAMING): -0.36	GLAZING TYPE: -(GL-1) 1" INSULATED GLAZING PANEL, CLEAR GLASS -(GL-2) 1" INSULATED GLAZING PANEL, CLEAR TINTED / SAFETY GLASS REFER TO SPECIFICATION SECTION 08 8000 MAX. SHGC (GLASS ONLY) = 0.38
---	---

DOOR TYPES		
NOT USED TYPE 'A' STOREFRONT (NARROW FRAME)		NOT USED TYPE 'C' (SOLID CORE) 1 3/4\" WOOD DOOR, BIRCH
NOT USED TYPE 'D' (SOLID CORE) 1 3/4\" WOOD DOOR, BIRCH		

GENERAL NOTE

ALL DOORS TO BE SUPPLIED BY G.C. UNLESS OTHERWISE NOTED.

DOOR FRAME TYPES

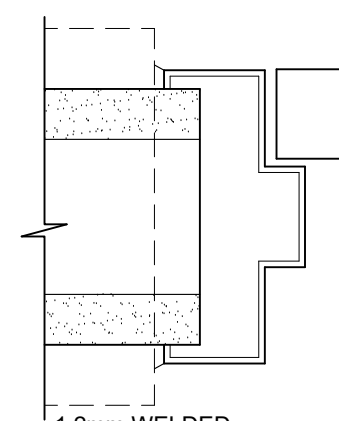

1.2mm WELDED

TYPE 'F2'

(HOLLOW METAL)

ISSUE TABLE		
No.	Date (mm/dd/yy)	Description
01	09-26-25	DTGO PROTOTYPE DOCUMENTS
REVISIONS		
No.	Date	Description
DRAWINGS REVISED AS PER DESIGN BULLETIN		
No.	Date	Description
THIS DRAWING IS OWNED BY OR LICENSED FOR USE BY POPEYES LOUISIANA KITCHEN (OR ITS AFFILIATED OR RELATED COMPANIES) AND MAY NOT BE REPRODUCED, USED, DOWNLOADED, DISSEMINATED, PUBLISHED, OR TRANSFERRED IN ANY FORM OR BY ANY MEANS, EXCEPT WITH THE PRIOR WRITTEN CONSENT OF POPEYES LOUISIANA KITCHEN . COPYRIGHT INFRINGEMENT IS A VIOLATION OF FEDERAL LAW SUBJECT TO CRIMINAL AND CIVIL PENALTIES.		
THE CONTRACTOR IS TO VERIFY ALL DIMENSIONS AND CONDITIONS ON THE PROJECT AND TO REPORT ANY DISCREPANCIES TO THE POPEYES LOUISIANA KITCHEN REPRESENTATIVE PRIOR TO COMMENCING WORK. THESE DRAWINGS ARE NOT TO BE USED FOR CONSTRUCTION PURPOSES UNLESS INDICATED BY POPEYES LOUISIANA KITCHEN. AS "ISSUED FOR CONSTRUCTION".		
Professional Seal		
DESIGNER NOTES: DESIGN GUIDELINE ONLY - NOT FOR PERMIT OR CONSTRUCTION THESE DOCUMENTS MUST BE COMPLETED AND / OR MODIFIED BY A LICENSED ARCHITECT AND ENGINEER TO CONFORM TO ALL APPLICABLE CODES, AND SPECIFIC SITE CONDITIONS. THERE IS NO WARRANTY, WHETHER IMPLIED OR EXPRESSED THAT THESE DOCUMENTS MEET THE APPLICABLE CODE REQUIREMENTS. LIABILITY FOR THE DESIGN AND ANY USE OF THE DOCUMENTS IS THE SOLE RESPONSIBILITY OF THE ARCHITECT AND ENGINEER OF RECORD.		
Company Logo		
Project		
Store Type		
US DTGO PROTOTYPE		
Location		
PROTOTYPE DTGO (U.S.) CITY, STATE		
Drawing Title		
DOOR AND WINDOW SCHEDULES		
Drawn		Checked
XX		XX
Scale		Date
AS NOTED		##.##.####
Project No.		Drawing No.
XX		A11

[illegible]

DIVISION 10 - SPECIALTIES			DIVISION 12 - WINDOW TREATMENTS		
SIGNAGE	SECTION 10 14 23		ROLL-DOWN BLINDS	SECTION 12 21 23	
PART 1 - GENERAL			(AS APPLICABLE - CONFIRM W/ POPEYES DESIGN MANAGER)		
1. SUMMARY			PART 1 - GENERAL		
A. SECTION INCLUDES:			1. SUMMARY		
1. ILLUMINATED PANEL SIGNS			A. MANUAL ROLLER SHADES AND HARDWARE		
2. RECOGNIFICATION SIGNS			1. SYSTEM DESCRIPTION		
12. ACTION SUBMITTALS			1.3. SUBMITTALS		
A. PRODUCT DATA FOR EACH TYPE OF PRODUCT			A. PRODUCT DATA: SUBMIT AN ELECTRONIC PDF COPY OF MANUFACTURERS TECHNICAL DATA AND INSTALLATION INSTRUCTIONS		
B. SHOP DRAWINGS FOR PANEL SIGNS			B. SAMPLES: SUBMIT THREE SAMPLES OF EACH SHADE CLOTH WITH COMPLETE COLOR SWATCH		
C. SHOW SIGN MOUNTING HEIGHTS, LOCATIONS OF SUPPLEMENTARY SUPPORTS TO BE PROVIDED BY OTHERS, AND ACCESSORIES			C. SHOP DRAWINGS: SUBMIT DRAWINGS OF MECHANICAL PRODUCTS WITH APPROPRIATE DIMENSIONS		
D. SHOW MESSAGE LIST, TYPE STYLES, GRAPHIC ELEMENTS, INCLUDING RAISED CHARACTERS AND BRAILLE, AND LAYOUT FOR EACH SIGN AT LEAST 1/4" SIZE 12"			1.4. QUALITY ASSURANCE		
E. SHOW LOCATIONS OF ELECTRICAL SERVICE CONNECTIONS			A. THE MANUFACTURER OF THESE PRODUCTS SHALL SHOW A MINIMUM OF 20 YEARS DOCUMENTED EXPERIENCE		
F. INCLUDE DIAGRAMS FOR POWER, SIGNAL, AND CONTROL WIRING			B. THE INSTALLER SHALL SHOW A MINIMUM OF 3 YEARS EXPERIENCE WITH THESE SYSTEMS		
G. SAMPLES FOR EACH EXPOSED PRODUCT AND FOR EACH COLOR AND TEXTURE SPECIFIED			2.1. MANUFACTURER		
H. SIGN SCHEDULE: USE SAME DESIGNATIONS SPECIFIED OR INDICATED ON DRAWINGS OR IN SIGN SCHEDULE			A. S05 "SUN OR SHADE" A DIVISION OF INSIDE OUTFITTERS, INC. 8331 GREEN MEADOWS DRIVE N., STE. B, LEWIS CENTER, OH. 43085 P. 614.743.3372, F. 617.888.3846, E. INFO@S05SHADES.COM		
1.3. INFORMATIONAL SUBMITTALS			2.2. MATERIALS		
A. SAMPLE WARRANTY			A. SHADE FABRICS: TRANSLUCENT FABRICS HAVE AN OPACITY FACTOR OF 10%; THE FABRIC SHALL HAVE A HIGH DEGREE OF OPACITY FOR EFFECTIVE CONTROL OF LIGHT. THE FABRIC MUST HAVE SUFFICIENT RIGIDITY TO INSURE STRAIGHT HANGING, RESIST CURL, TWIST, BOWING AND DISTORTION. IT MUST BE DIMENSIONALLY STABLE AND WILL NOT SHRINK OR STRETCH. THE FABRIC SHALL BE COLORFAST AND SHALL NOT BE AFFECTED BY MOISTURE OR HEAT. THE COLOR SHALL BE SELECTED FROM STANDARD COLORS. ALL SEAMS ARE TO BE HAND SEWED. SEWING IS NOT ACCEPTED. THE FABRIC COLOR SHALL BE SELECTED FROM THE MANUFACTURERS STANDARD COLOR LINE. SKEERWEAVE 4100 - COLOR REBELSTONE FABRIC STYLE (10% OPACITY)		
1.4. CLOSEOUT SUBMITTALS			B. TUBE: THE FABRIC SHADES SHALL BE MOUNTED ON TO A 1-1/4", 1-1/2", 2", OR 2-1/2" OR 3-1/4 DIAMETER ALUMINUM TUBE DEPENDING ON THE WIDTH OF THE SHADE AND FABRIC CHOSEN FOR THE SHADE		
A. MAINTENANCE DATA			C. BEAD CHAIN CLUTCH: THE CLUTCH INCORPORATES AN ADJUSTABLE SLIP CLUTCH TO CONTROL THE RATE OF FALL FROM FREE RUNNING ZERO FRICTION FACTOR TO A FACTOR OF 100%. THE SHADE MAY BE ADJUSTED TO STOP AND HOLD AT ANY POSITION. THE BEAD CHAIN SHALL CONTAIN AUTOMATIC STOPS TO PREVENT THE SHADE FROM OVER WINDING OR UNWINDING. THE BEAD CHAIN WILL BE SECURED BY A HOLD DOWN CLIP		
1.5. WARRANTY			D. EASY LIFT: THIS OPTION IS ADDED TO ALL SHADES THAT ARE OVER 30 POUNDS		
A. SPECIAL WARRANTY: MANUFACTURER AGREES TO REPAIR OR REPLACE COMPONENTS OF SIGNS THAT FAIL IN MATERIALS OR WORKMANSHIP WITHIN SPECIFIED WARRANTY PERIOD			E. HEMBAR: SHALL BE A CONTINUOUS ALUMINUM BAR 1" X 3/8" WITH SUFFICIENT WEIGHT TO ALLOW THE SHADE TO CLOSE WITHOUT BACKING OR SAGGING. STANDARD HEMBAR IS WRAPPED IN FABRIC AND SEALED AROUND ALL EDGES		
1. WARRANTY PERIOD: FIVE YEARS FROM DATE OF SUBSTANTIAL COMPLETION			F. SHADE MOUNTING BRACKETS: SHADE MOUNTING BRACKETS SHALL BE MANUFACTURED FROM 304 GALVANIZED STEEL, REVERSIBLE FOR RIGHT AND LEFT HAND MOUNTING. THE BRACKETS MAY BE FIELD MOUNTED INSIDE, OUTSIDE OR CEILING MOUNTED. FABRIC BRACKETS SHALL MATCH FABRIC COLOR		
PART 2 - PRODUCTS			G. FASCIA SYSTEM: ALL FASCIA SYSTEMS SHALL BE PRIME PAINTED WITH BAKED ENAMEL. UTILIZING THE POWDER PAINT METHOD TO ENSURE AN ENVIRONMENTAL, FRIENDLY APPLICATION. NET PAINT METHOD SHALL NOT BE ACCEPTED		
2.1. SIGNS			1. LANGLE FASCIA: FASCIA PANELS SHALL BE MADE FROM EXTRUDED ALUMINUM. FASCIA SHALL BE 3" OR 4" TO ACCOMMODATE SHADE ROLL. FASCIA SHALL CLIP TO BRACKETS AND SNAP EASILY INTO PLACE. IT SHALL BE EASILY REMOVED FOR ANY NECESSARY MAINTENANCE		
A. MANUFACTURER: APPROVED POPEYES SIGNAGE MANUFACTURER			a. FASCIA COLOR: VANILLA		
B. PANEL SIGN: SIGN WITH SMOOTH, UNIFORM SURFACES WITH MESSAGE AND CHARACTERS HAVING UNIFORM FACES, SHARP CORNERS, AND PRECISELY FORMED LINES AND PROFILES, AND AS FOLLOWS			PART 3 - EXECUTION		
1. ILLUMINATED PANEL SIGN: BACKLIT CONSTRUCTION INCLUDING TRANSFORMERS, INSULATORS, AND/OR OTHER ACCESSORIES FOR OPERABILITY, WIRING, AND CONCEALING CONNECTIONS TO BUILDING ELECTRICAL SYSTEM. USE TIGHT OR SEALED JOINT CONSTRUCTION TO PREVENT UNINTENTIONAL LIGHT LEAKAGE. SPACE LAMPS AWAY FROM EACH OTHER AND AWAY FROM SIGN SURFACES AS NEEDED TO ILLUMINATE EVENLY			1. INSTALLATION		
a. POWER: AS INDICATED ON ELECTRICAL DRAWINGS			A. INSTALL THE SHADES WHERE SHOWN ON THE CONTRACT DRAWINGS IN ACCORDANCE WITH PRINTED INSTRUCTIONS PROVIDED BY THE MANUFACTURER. S05 SHADE SYSTEMS, OR A MODIFICATION AS APPROVED BY THE MANUFACTURER		
2. MOUNTING: MANUFACTURERS STANDARD METHOD FOR SUBSTRATES INDICATED ON EXTERIOR ELEVATIONS			B. THE SHADE FABRIC SHALL HANG FLAT WITHOUT BUCKLING OR DISTORTION. THE EDGE WHEN TRIMMED SHALL HANG STRAIGHT WITHOUT CURVING OR BOWLING. UNJOINED ROLLER FABRICS SHALL ROLL WITHOUT SHIFTING SIDEWAYS MORE THAN 1/4" IN EITHER DIRECTION. TOLERANCE FOR BRACKETS SHALL BE 0.0025 IN/4" ON EITHER SIDE		
C. RESTROOM IDENTIFICATION SIGN: SIGN WITH SMOOTH, UNIFORM SURFACES, WITH MESSAGE AND CHARACTERS HAVING UNIFORM FACES, SHARP CORNERS, AND PRECISELY FORMED LINES AND PROFILES, AND AS FOLLOWS			C. VERIFY THAT ALL SURFACES AND OPENINGS ARE READY TO RECEIVE THE WORK. DO NOT COMMENCE THE WORK UNTIL THE INSTALLER VERIFIES FIELD MEASUREMENTS		
1. LAMINATED SHEET SIGN: FACE SHEET WITH RAISED GRAPHICS LAMINATED TO BACKING SHEET TO PRODUCE COMPOSITE SHEET			D. BEGINNING THE INSTALLATION INDICATES THE INSTALLER ACCEPTS THE SUBSTRATE		
a. COLOR AS PER AUTHORITIES HAVING JURISDICTION			3.2. ADJUSTING		
2. MOUNTING: SURFACE MOUNTED WITH ADHESIVE			A. THE SYSTEM SHALL BE ADJUSTED BY THE INSTALLER FOR SMOOTH OPERATION. ALL COMPLETED SHADES WILL BE OPERATED BY THE INSTALLER TO ENSURE THAT THEY FUNCTION CORRECTLY		
PART 3 - EXECUTION			B. INSTRUCT THE OWNERS OR REPRESENTATIVE, AS TO THE PROPER OPERATING PROCEDURES AND MAINTENANCE OF THE SYSTEM		
1. INSTALLATION			END OF SECTION 12 21 23		
A. GENERAL: INSTALL SIGNS USING MOUNTING METHODS INDICATED ACCORDING TO MANUFACTURERS WRITTEN INSTRUCTIONS			PART 3 - EXECUTION		
1. INSTALL SIGNS LEVEL, PLUMB, TRUE TO LINE, AND AT LOCATIONS AND HEIGHTS INDICATED, WITH SIGN SURFACES FREE OF DISTORTION AND OTHER DEFECTS IN APPEARANCE			1. INSTALLATION		
2. INSTALL SIGNS SO THEY DO NOT PROTRUDE OR OBSTRUCT ACCORDING TO THE ACCESSIBILITY STANDARDS			A. INSTALL THE SHADES WHERE SHOWN ON THE CONTRACT DRAWINGS IN ACCORDANCE WITH PRINTED INSTRUCTIONS PROVIDED BY THE MANUFACTURER. S05 SHADE SYSTEMS, OR A MODIFICATION AS APPROVED BY THE MANUFACTURER		
3. BEFORE INSTALLATION, VERIFY THAT SIGN SURFACES ARE CLEAN AND ARE FREE OF MATERIALS OR DEBRIS THAT WOULD IMPAIR INSTALLATION			B. THE SHADE FABRIC SHALL HANG FLAT WITHOUT BUCKLING OR DISTORTION. THE EDGE WHEN TRIMMED SHALL HANG STRAIGHT WITHOUT CURVING OR BOWLING. UNJOINED ROLLER FABRICS SHALL ROLL WITHOUT SHIFTING SIDEWAYS MORE THAN 1/4" IN EITHER DIRECTION. TOLERANCE FOR BRACKETS SHALL BE 0.0025 IN/4" ON EITHER SIDE		
4. CORROSION PROTECTION: COAT CONCEALED SURFACES OF ALUMINUM IN CONTACT WITH GROUT, CONCRETE, MASONRY, WOOD, OR DISSIMILAR METALS, WITH A HEAVY COAT OF BITUMINOUS PAINT			C. VERIFY THAT ALL SURFACES AND OPENINGS ARE READY TO RECEIVE THE WORK. DO NOT COMMENCE THE WORK UNTIL THE INSTALLER VERIFIES FIELD MEASUREMENTS		
B. MOUNTING METHODS			D. BEGINNING THE INSTALLATION INDICATES THE INSTALLER ACCEPTS THE SUBSTRATE		
1. EXTERIOR LUMINATED BUILDING SIGNS: MOUNTING METHOD TO BE PROVIDED BY MANUFACTURER			3.2. ADJUSTING		
2. RESTROOM IDENTIFICATION SIGN			A. THE SYSTEM SHALL BE ADJUSTED BY THE INSTALLER FOR SMOOTH OPERATION. ALL COMPLETED SHADES WILL BE OPERATED BY THE INSTALLER TO ENSURE THAT THEY FUNCTION CORRECTLY		
a. ADHESIVE: CLEAN BOND-BREAKING MATERIALS FROM SUBSTRATE SURFACE AND REMOVE LOOSE DEBRIS. APPLY LINEAR BEADS OR SPOTS OF ADHESIVE SYMMETRICALLY TO BACK OF SIGN AND CURE WITHOUT SURFAP. KEEP ADHESIVE AWAY FROM EDGES TO PREVENT ADHESIVE EXTRUSION AS SIGN IS APPLIED AND TO PREVENT VISIBILITY OF CURED ADHESIVE AT SIGN EDGES. PLACE SIGN IN POSITION, AND PUSH TO ENGAGE ADHESIVE. TEMPORARILY SUPPORT SIGN IN POSITION UNTIL ADHESIVE FULLY SETS			B. INSTRUCT THE OWNERS OR REPRESENTATIVE, AS TO THE PROPER OPERATING PROCEDURES AND MAINTENANCE OF THE SYSTEM		
b. TWO-FACE TAPE: CLEAN BOND-BREAKING MATERIALS FROM SUBSTRATE SURFACE AND REMOVE LOOSE DEBRIS. APPLY TAPE STRIPS SYMMETRICALLY TO BACK OF SIGN AND OF SUITABLE QUANTITY TO SUPPORT WEIGHT OF SIGN WITHOUT SURFAP. KEEP STRIPS AWAY FROM EDGES TO PREVENT VISIBILITY AT SIGN EDGES. PLACE SIGN IN POSITION, AND PUSH TO ENGAGE TAPE ADHESIVE			END OF SECTION 12 21 23		
C. REMOVE TEMPORARY PROTECTIVE COVERINGS AND STRIPPEABLE FILMS AS SIGNS ARE INSTALLED			PART 3 - EXECUTION		
END OF SECTION 10 14 23			1. EXAMINATION		
WALL PROTECTION			A. EXAMINE WALLS ROUGH-IN FOR HOSE VALVES, HOSE RACKS, AND CABINETS TO VERIFY ACTUAL LOCATIONS OF PIPING CONNECTIONS BEFORE CABINET INSTALLATION		
SECTION 10 20 00			B. EXAMINE WALLS AND PARTITIONS FOR SUITABLE FRAMING DEPTH AND BLOCKING WHERE RECESSED AND SEMI-RECESSED CABINETS ARE TO BE INSTALLED		
PART 1 - GENERAL			C. EXAMINE FIRE EXTINGUISHERS FOR PROPER CHARGING AND TAGGING		
1. SUMMARY			1. REMOVE AND REPLACE DAMAGE, DEFECTIVE, OR UNDERCHARGED		
A. SECTION INCLUDES:			2. PROCEED WITH INSTALLATION ONLY AFTER UNSATISFACTORY CONDITIONS HAVE BEEN CORRECTED		
1. CORNER GUARDS			3.2. INSTALLATION		
12. ACTION SUBMITTALS			A. COMPLY WITH		

PROJECT SPECIFICATIONS

DIVISION 01 - GENERAL REQUIREMENTS

GENERAL REQUIREMENTS SECTION 01 01 00

DIVISION 02 - EXISTING CONDITIONS (NOT INCLUDED)

DIVISION 03 - CONCRETE

REINFORCED CONCRETE SECTION 03 00 30

DIVISION 04 - MASONRY

UNIT MASONRY SECTION 04 00 20

DIVISION 05 - METALS

DECORATIVE METAL FINISH SECTION 05 73 00

DIVISION 06 - WOOD, PLASTICS AND COMPOSITES

ROUGH CARPENTRY SECTION 06 10 00

SHEATHING SECTION 06 10 00

SHOP FABRICATED WOOD SECTION 06 17 03

TRUSSES SECTION 06 20 00

FINISH CARPENTRY SECTION 06 20 00

DIVISION 07 - THERMAL AND MOISTURE PROTECTION

THERMAL INSULATION SECTION 07 21 00

EXTERIOR INSULATION SECTION 07 21 00

FISH SYSTEMS SECTION 07 22 26

ADHESIVE SECTION 07 22 26

EXTRUDED JUNCTION SANDING SECTION 07 24 16

MEMBRANE ROOFING SECTION 07 24 16

SHEET METAL FLASHING SECTION 07 24 00

AND TRIM SECTION 07 21 23

GUTTERS AND DOWNSPOUTS SECTION 07 24 00

JOINT SEALANTS SECTION 07 24 00

DIVISION 08 - OPENINGS

METAL DOORS AND FRAMES SECTION 08 11 00

ALUMINUM ENTRANCES AND STOREFRONT WINDOWS SECTION 08 14 13

PASS-THRU WINDOWS SECTION 08 56 19

DOOR HARDWARE SECTION 08 56 00

GLAZING SECTION 08 56 00

DIVISION 09 - FINISHES

GYPSUM BOARD ASSEMBLIES SECTION 09 21 00

CERAMIC TILING SECTION 09 30 13

CEILING TILES SECTION 09 31 23

FIBERGLASS REINFORCED PANELS SECTION 09 31 00

DIVISION 10 - SPECIALTIES

SGNAGE SECTION 10 11 23

WALL PROTECTION SECTION 10 20 00

TOILET ACCESSORIES SECTION 10 20 00

PIPE PROTECTION SECTION 10 24 00

SPECIALTIES SECTION 10 24 00

DIVISION 12 - WINDOW TREATMENTS

ROLL-UP/DOWN BLINDS SECTION 12 21 23

DIVISION 22 - PLUMBING

SEE MECHANICAL DRAWINGS

DIVISION 23 - HEATING, VENTILATING AND AIR CONDITIONING (HVAC)

SEE MECHANICAL DRAWINGS

DIVISION 26 - ELECTRICAL

SEE ELECTRICAL DRAWINGS

APPROVED SUPPLIERS LIST

BIDDING REQUIREMENTS; INSTRUCTIONS TO BIDDERS

EXAMINATION OF SITE: ALL BIDDERS SUBMITTING PROPOSALS FOR THIS WORK SHALL FIRST EXAMINE THE SITE (PREMISES) AND ALL SUCH CONDITIONS AS MAY AFFECT THE WORK UNDER THIS CONTRACT. FAILURE TO EXAMINE THE SITE WILL NOT RELIEVE THE SUCCESSFUL BIDDER FROM THE NECESSITY TO PROVIDE WORK THAT MAY BE REQUIRED TO COMPLETE THE WORK WITHOUT ADDITIONAL COST TO THE OWNER.

EXPLANATION TO BIDDERS: A. NO ORAL EXPLANATION IN REGARD TO THE MEANING OF THE DRAWINGS AND SPECIFICATIONS WILL BE MADE AND NO ORAL INSTRUCTIONS WILL BE GIVEN BEFORE THE AWARD OF THE CONTRACT. DISCREPANCIES, OMISSIONS, OR DOUBTS AS TO MEANINGS OF THE DRAWINGS AND SPECIFICATIONS SHALL BE COMMUNICATED IN WRITING TO THE OWNER FOR INTERPRETATION.

IN THE EVENT OF UNRESOLVED DISCREPANCIES OR AMBIGUITY, ARCHITECT OF RECORD WILL BE THE FINAL JUDGE ON PLAN INTERPRETATION. BIDDERS SHOULD ACT PROMPTLY AND ALLOW SUFFICIENT TIME FOR A REPLY TO REACH THEM BEFORE THE SUBMISSION OF THEIR BIDS. ANY REVISION MADE WILL BE IN THE FORM OF AN ADDENDUM TO THE SPECIFICATIONS BEARING THE APPROVAL OF THE OWNER AND WILL BE FORWARDED TO ALL BIDDERS AND ITS RECEIPT BY THE BIDDER SHOULD BE ACKNOWLEDGED BY THE BIDDER BY HIS SIGNATURE AFFIXED THERETO AT THE TIME OF RECEIPT AND VERIFIED BY HIS ACKNOWLEDGMENT ON THE BID FORM.

B. EACH PROPOSITIVE BIDDER WILL BE FURNISHED BIDDER DOCUMENTS TO COMPLETE THEIR BID.

PREPARATION & SUBMISSION OF BIDS: A. THE BIDDER IS REQUIRED TO BID ON ALL ALTERNATES AND/OR ALLOWANCES OR ON ALL ITEMS CALLED FOR IN THE BID FORM, EXCEPT WHEN ALTERNATES ARE CALLED FOR ON A TYPE OR METHOD OF CONSTRUCTION AS TO WHICH BIDDER DOES NOT DESIRE TO BID. HE MUST INSERT THE WORDS "NO BID" IN THE SPACE PROVIDED FOR PRICES ON SUCH ALTERNATE TYPE OR METHOD OF CONSTRUCTION.

B. BIDS SHALL BE SUBMITTED ON THE FORMS FURNISHED AND SHALL BE SIGNED IN INK. ERASURES OR OTHER CHANGES IN A BID MUST BE INITIALED BY THE BIDDER. THE SIGNATURE OF THE BIDDER, BIDS CONTAINING ANY CONDITIONS, OMISSIONS, UNEXPLAINED ERASURES OR ALTERNATES, OR ITEMS NOT CALLED FOR IN THE PROPOSAL, OR IRREGULARITIES OF ANY KIND, MAY BE REJECTED BY THE OWNER AS BEING INCOMPLETE.

BID AND BIDS: BIDS SHALL BE ACCOMPANIED BY ONE (1) SIGNED COPY OF POPEYES STANDARD BID ANALYSIS FORM, AS INDICATED ON THE BIDDING INDIVIDUAL LINE ITEMS ARE TO BE SHOWN AT THE GENERAL CONTRACTORS COST WITH NO MARKUP FOR OVERHEAD AND PROFIT BY THE GENERAL CONTRACTOR. HOWEVER, EACH LINE ITEM SHALL INDICATE THE FULL VALUE OF SUBCONTRACTOR INCLUDING SUBCONTRACTORS OVERHEAD AND PROFIT. SUPERVISION, OVERHEAD AND PROFIT FOR THE CONTRACTOR AND FOR EACH SUBCONTRACTOR SHALL BE SHOWN ON THE APPROPRIATE LINES.

AWARD OF CONTRACT: THE OWNER RESERVES THE RIGHT TO DETERMINE WHAT ARE INFORMALITIES IN THE MAKING, RECEIVING, AND OPENING OF BIDS AND THE AWARDING OF CONTRACTS THEREON, AND THE FURTHER RIGHT TO WAIVE ANY SUCH INFORMALITY WHEN SUCH WAIVER IS, IN THE DISCRETION OF THE OWNER, TO THE BEST INTEREST. ALSO, TO ACCEPT ANY ITEM IN THE BID UNLESS OTHERWISE SPECIFIED.

REJECTION: THE OWNER RESERVES THE RIGHT TO REJECT ANY AND ALL BIDS.

STANDARD FORMS: 1. AIA DOCUMENT A305 - CONTRACTOR QUALIFICATIONS STATEMENT.

2. AIA DOCUMENT C701 - CHANGE ORDER.

3. AIA DOCUMENT G702 - APPLICATION AND CERTIFICATE OF PAYMENT. THIS DOCUMENT SUMMARIZES THE CONTRACT AMOUNT, WORK COMPLETED, STORED MATERIALS, RETAINAGE, PREVIOUS CERTIFICATES OF PAYMENT, AND THE CURRENT AMOUNT DUE.

4. AIA DOCUMENT G703 - CONTINUATION SHEET (ONE (1) OR MORE SHEETS AS REQUIRED) TO BE SUBMITTED WITH THE BIDDING INDIVIDUAL LINE ITEMS ARE TO BE SHOWN AT THE GENERAL CONTRACTORS COST WITH NO MARKUP FOR OVERHEAD AND PROFIT BY THE GENERAL CONTRACTOR. HOWEVER, EACH LINE ITEM SHALL INDICATE THE FULL VALUE OF SUBCONTRACTOR INCLUDING SUBCONTRACTORS OVERHEAD AND PROFIT. SUPERVISION, OVERHEAD AND PROFIT FOR THE CONTRACTOR AND FOR EACH SUBCONTRACTOR SHALL BE SHOWN ON THE APPROPRIATE LINES.

5. AIA DOCUMENT G704 - CONTRACTORS AFFIDAVIT OF PAYMENT OF DEBTS AND CLAIMS. IN THIS DOCUMENT, THE CONTRACTOR SWEARS THAT ALL SUBCONTRACTORS AND MATERIALMEN HAVE BEEN PAID AND THAT WARRERS OF LIENS, HIS OWN INCLUDED, ARE ATTACHED.

6. AIA DOCUMENT G705 - LIST OF SUBCONTRACTORS AND MATERIALMEN. IN THIS FORM, THE CONTRACTOR, SUBCONTRACTORS AND MATERIALMEN WAIVE THEIR RIGHT TO FILE A LIEN FOR WORK PERFORMED TO DATE. THIS DOCUMENT IS ACCEPTABLE FOR INTERIM CERTIFICATES OF PAYMENT.

7. AIA DOCUMENT G706 - CONTRACTORS AFFIDAVIT OF RELEASE OF LIENS. IN THIS DOCUMENT, THE CONTRACTOR SWEARS THAT ALL SUBCONTRACTORS AND MATERIALMEN HAVE BEEN PAID AND THAT WARRERS OF LIENS, HIS OWN INCLUDED, ARE ATTACHED.

8. AIA DOCUMENT G707 - CHANGE ORDER AUTHORIZATIONS. CONSENT OR SUPERVISORY COMPANY APPROVAL IS REQUIRED FOR ALL CHANGES AND MATERIALMEN WAIVE THEIR RIGHT TO FILE A LIEN FOR WORK PERFORMED TO DATE. THIS DOCUMENT IS ACCEPTABLE FOR INTERIM CERTIFICATES OF PAYMENT.

9. AIA DOCUMENT G708 - CONTRACTORS AFFIDAVIT OF RELEASE OF LIENS. IN THIS DOCUMENT, THE CONTRACTOR SWEARS THAT ALL SUBCONTRACTORS AND MATERIALMEN HAVE BEEN PAID AND THAT WARRERS OF LIENS, HIS OWN INCLUDED, ARE ATTACHED.

10. AIA DOCUMENT G709 - CONTRACTORS AFFIDAVIT OF PAYMENT OF DEBTS AND CLAIMS. IN THIS DOCUMENT, THE CONTRACTOR SWEARS THAT ALL SUBCONTRACTORS AND MATERIALMEN HAVE BEEN PAID AND THAT WARRERS OF LIENS, HIS OWN INCLUDED, ARE ATTACHED.

11. AIA DOCUMENT G710 - CONTRACTORS AFFIDAVIT OF RELEASE OF LIENS. IN THIS DOCUMENT, THE CONTRACTOR SWEARS THAT ALL SUBCONTRACTORS AND MATERIALMEN HAVE BEEN PAID AND THAT WARRERS OF LIENS, HIS OWN INCLUDED, ARE ATTACHED.

12. AIA DOCUMENT G711 - CONTRACTORS AFFIDAVIT OF RELEASE OF LIENS. IN THIS DOCUMENT, THE CONTRACTOR SWEARS THAT ALL SUBCONTRACTORS AND MATERIALMEN HAVE BEEN PAID AND THAT WARRERS OF LIENS, HIS OWN INCLUDED, ARE ATTACHED.

93. AIA DOCUMENT G792 - CONTRACTORS AFFIDAVIT OF RELEASE OF LIENS. IN THIS DOCUMENT, THE CONTRACTOR SWEARS THAT ALL SUBCONTRACTORS AND MATERIALMEN HAVE BEEN PAID AND THAT WARRERS OF LIENS, HIS OWN INCLUDED, ARE ATTACHED.

94. AIA DOCUMENT G793 - CONTRACTORS AFFIDAVIT OF RELEASE OF LIENS. IN THIS DOCUMENT, THE CONTRACTOR SWEARS THAT ALL SUB