


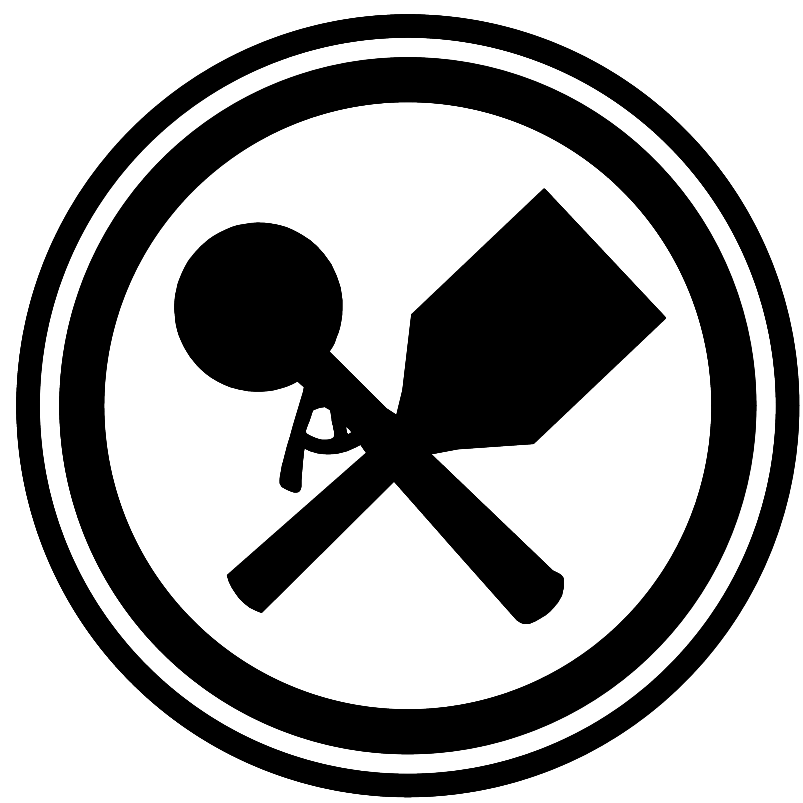

CULVER FRANCHISING SYSTEM, LLC

CULVER'S OF SHAKOPEE, MN #0131

4058 12TH AVENUE EAST, SHAKOPEE, MN, 55379

REIMAGE PLANS

GENERAL NOTES:

- THESE DRAWINGS ARE MEANT TO CONVEY DESIGN INTENT AND ARE NOT INTENDED TO BE FINAL CONSTRUCTION DRAWINGS. IT IS THE RESPONSIBILITY OF THE GENERAL CONTRACTOR (GC) TO COMPLY WITH ALL FEDERAL, STATE AND LOCAL LAWS, CODES AND ORDINANCES AND TO FIELD VERIFY ALL ITEMS RELATING TO THE SCOPE OF WORK. GC SHOULD REVIEW SCOPE OF DESIGN AND SCOPE OF SERVICES WITH FRANCHISEE PRIOR TO SUBMITTING ANY PRICING.
- FRANCHISEE TO VERIFY WITH LOCAL AUTHORITIES IF ARCHITECT/ ENGINEER SEALS ARE REQUIRED. IF ARCHITECT/ ENGINEER IS REQUIRED CULVER FRANCHISING SYSTEM, LLC (CFS) WILL PROVIDE THESE PLANS IN ELECTRONIC FORMAT AND ASSIST TO INTERPRET THE INTENT OF THE DRAWINGS. THE LOCAL ARCHITECT/ ENGINEER SHALL PROVIDE CODE COMPLIANT CONTRACT DOCUMENTS FOR CONTRACTOR USE.
- GC TO VERIFY ALL DIMENSIONS IN FIELD. COORDINATE ALL EXISTING CONDITIONS WITH PROPOSED NEW CONSTRUCTION, DEMO AND MEP CLEARANCES AND REQUIREMENTS.
- VERIFY THAT LOCATIONS OF NEW WALLS OR WALL MOUNTED ITEMS DO NOT INTERFERE WITH EXISTING UTILITIES (EXAMPLE: SMOKE DETECTORS, AED, THERMOSTATS, ETC.).
- MEP TO BE REWORKED, DESIGN-BUILD. GC TO COORDINATE ALL EXISTING AND NEW FIXTURE LOCATIONS IN FIELD AND TO PROVIDE DESIGN-BUILD MECHANICAL, ELECTRICAL, AND PLUMBING DESIGN TO FRANCHISEE AND REVIEW DESIGNS PRIOR TO BID.
- SHOULD ADDITIONAL DRAWINGS OR CHANGES BE DEVELOPED BY FRANCHISEE TEAM, FRANCHISEE WILL COPY CFS FOR CFS REVIEW AND APPROVAL.

BEST PRACTICES FOR AFTER-HOURS SAFETY AND SECURITY:

- KEEP EXTERIOR DOORS CLOSED AND LOCKED AT ALL TIMES AND LIMIT THE AMOUNT OF TIMES ENTERING AND EXITING THE BUILDING.
- KEEP ALL EXTERIOR LIGHTS ON.
- ENSURE THE VIDEO SURVEILLANCE SYSTEM IS RECORDING AND CAMERAS ARE NOT COVERED OR BLOCKED DURING CONSTRUCTION.
- KNOW HOW TO GET IN TOUCH WITH THE EMERGENCY CONTACT PERSON(S) FOR THE RESTAURANT AND LEARN HOW TO USE THE RESTAURANT PHONE SYSTEM SHOULD YOU NEED TO MAKE AN EMERGENCY CALL.

AMERICANS WITH DISABILITIES ACT (ADA) GENERAL NOTES:

- IT IS THE RESPONSIBILITY OF THE GC TO ENSURE ALL CONSTRUCTION AND IMPROVEMENTS COMPLY WITH FEDERAL, STATE AND LOCAL ADA LAWS AND CODES, INCLUDING BUT NOT LIMITED TO: WALL ACCESSORIES, VANITIES AND PLUMBING FIXTURES AND ACCESSORIES.

ELECTRICAL CONTRACTOR NOTES:

- VERIFY LOCATION AND SIZE OF ALL EXISTING LIGHTING FIXTURES.
- COORDINATE THE RELOCATION OF EXISTING LIGHTING FIXTURES (RECESSED CANS AND LAY-IN FIXTURES) AND OUTLETS WITH THE NEW FLOOR AND CEILING PLANS. REFER TO SHEET A-2 FOR NEW WALL AND FURNITURE LOCATIONS. REFER TO SHEET A-5 FOR NEW CEILING DESIGN ELEMENTS. REFER TO SHEET D-1 FOR DEMO'D WALLS. VERIFY THE LOCATION OF EXISTING LIGHTING FIXTURES DO NOT INTERFERE WITH NEW WALL OR PENDANT LOCATIONS. REMOVE OR RELOCATE AS NEEDED.
- PATCH AND REPAIR LOCATIONS OF EXISTING PENDANTS OR REPLACE EXISTING PENDANTS WITH RECESSED CAN FIXTURES OR REPLACE EXISTING PENDANT WITH NEW PENDANT FIXTURE SELECTION. REFER TO SHEET A-5 FOR NEW PENDANT LOCATIONS. VERIFY W/ OWNER WHERE TO PATCH AND REPAIR OR REPLACE WITH RECESSED FIXTURES.
- COORDINATE AND VERIFY EQUIPMENT ELECTRICAL REQUIREMENTS WITH FOODSERVICE EQUIPMENT DEALER AND FRANCHISEE.
- ENSURE A MINIMUM OF 15 FOOT-CANDLES AT ALL TABLE SURFACES.
- IN RESTROOMS, WHEN REPLACING LAY-IN FIXTURES WITH RECESSED CANS, VERIFY NUMBER OF FIXTURES REQUIRED WITH FRANCHISEE.

PLUMBING CONTRACTOR NOTES:

- SEE SHEET A-2 FOR PLUMBING FIXTURE SPECIFICATIONS. VERIFY WATER SUPPLY BEFORE SELECTING TOILET OPTION.

DRAWING INDEX	
SHEET NO.	SHEET TITLE
T-1	TITLE, GENERAL NOTES, & SHEET INDEX
ADA-1	TYPICAL ACCESSIBILITY DETAILS
D-1	DEMOLITION PLAN
A-2	DIMENSIONED FLOOR PLAN
A-3.0	EXTERIOR ELEVATIONS
A-3.1	EXTERIOR ELEVATIONS
A-5	REFLECTED CEILING PLAN
A-6	FINISH PLAN
A-7	INTERIOR DECOR PLAN
A-8	INTERIOR ELEVATIONS & DETAILS
FS-1	FOODSERVICE PLAN
FS-2	FOODSERVICE PLUMBING OR ROUGH-INS PLAN
FS-3	FOODSERVICE ELECTRICAL PLAN

CONTRACTORS ARE RESPONSIBLE FOR ALL PLAN SHEETS. DO NOT ISSUE PARTIAL PLANS!

NATIONAL ACCOUNT SUPPLIER CONTACT (GC PROVIDED)			
ITEM	SUPPLIER	REP CONTACT INFO	NOTES
CARPET	TARGET	STEPHANIE SCHIPPER REGIONAL BUSINESS MANAGER STEPHANIE.SCHIPPER@TARGET.COM 608-400-7260	CONTACT REP FOR APPROVED INSTALLERS AND ORDER FORM
TILE	DAL-TILE	DAL-TILE SYSTEM 360 CULVERS@DAL-TILE.COM 877-556-5728	CONTACT FOR CULVER'S ORDER FORM
PLUMBING FIXTURES	TOTO	RICHARD LUESSER MANAGER OF BUSINESS DEVELOPMENT RLUESSER@TOTO.COM 773-706-3949	
WAINSCOTING, FRP, INTERIOR LAMINATE DOORS/ HARDWARE	MARLITE	KAREN KRANE SALES MANAGER KRANE@MARLITE.COM 390-260-7617	CONTACT REP FOR CULVER'S ORDER FORM
VINYL WALLCOVERING	MOMENTUM TEXTILES	JAMIE COOPER SALES REPRESENTATIVE JCOOPER@MOMENTEX.COM 262-606-9241	CONTACT REP FOR ORDER FORM
PAINT	SHERWIN WILLIAMS	KEVIN SYKES ACCOUNT MANAGER KEVIN.L.SYKES@SHERWIN.COM 773-241-0793	
ELECTRICAL - SITE LIGHTING AND PHOTOMETRICS	CRESCENT	GARY MANDERS DEPARTMENT MANAGER CULVERS@CESCO.COM	CONTACT CULVERS@CESCO.COM FOR PHOTOMETRICS
ELECTRICAL - LIGHTING, SWITCHGEAR, AND DEVICES	CRESCENT	DANA MCCOOK ACCOUNT MANAGER CULVERS@CESCO.COM	CONTACT CULVERS@CESCO.COM FOR BID REQUESTS
CEILING DIFFUSERS	HUNZICKER LLC	MARIE WILSON OWNER/ SALES MARIE@HUNZICKERLLC.COM 608-849-9951	
STONE VENEER	ENVIRONMENTAL STONENETWORKS	ANDY HOFFMAN SALES REPRESENTATIVE ANDREW.HOFFMAN@CORNERSTONE-PB.COM 612-380-1676	
STONE VENEER	WESTLAKE ROYAL STONE	JOE MARKKORS NATIONAL COMMERCIAL ACCOUNT MANAGER JMARKKORS@WESTLAKE.NET 314-780-4162	
BACK OF HOUSE FLOORING	RES-TEK	JOE LASKO ACCOUNT MANAGER JOE.LASKO@RES-TEK.NET 678-959-3299	CONTACT REP FOR APPROVED INSTALLERS
SOLID SURFACE	WILSONART	BRYNN BISHOP NATIONAL ACCOUNT MANAGER BRYNN.BISHOP@WILSONART.COM 720-346-4538	CONTACT REP FOR PRICING AND PREFERRED LOCAL DISTRIBUTOR
ACOUSTICAL CEILING	USG	JOHN FJINES CORPORATE ACCOUNTS MANAGER JFJINES@USG.COM 312-401-6579	
DIGITAL MENU BOARDS	CRI	NATALIE MINDS DIRECTOR/ ACCOUNT MANAGEMENT NATALIE.MINDS@CRI.COM CLIENTEXPERIENCE@CRI.COM	

FE #	PROJECT RESPONSIBILITY MATRIX			
	NOTES: MATRIX IS FOR INFORMATION PURPOSES, NOT ALL ITEMS LISTED ARE APPLICABLE. ANY ITEMS NOT INCLUDED IN RESPONSIBILITY MATRIX OR FOODSERVICE EQUIPMENT SCHEDULE ARE ASSUMED TO BE PROVIDED AND INSTALLED BY THE GC. SCOPE OF WORK WILL VARY.			
	KEY: FEC = FOODSERVICE EQUIPMENT CONTRACTOR GC = GENERAL CONTRACTOR		V = VENDOR O = OWNER	
	SITE ITEMS	SUPPLIED	INSTALLED	NOTES
	SITE WORK	GC	GC	
	DUMPSTER CORRAL	GC	GC	
	CONCRETE / ASPHALT/ STRIPING	GC	GC	
	ENTRY AND DRIVE-THRU CANOPY	GC	GC	
	LANDSCAPING	GC	GC	
	SITE LIGHTING AND POLES	GC	GC	NATIONAL ACCOUNT
	ADA BOLLARD POSTS	GC	GC	
	PATIO UMBRELLAS	O	V	NATIONAL ACCOUNT
	PYLON/ MONUMENT SIGNAGE	O	V	GC TO COORD. ROUGH-INS W/ VENDOR
	SITE SIGNAGE	O	V	GC TO COORD. ROUGH-INS W/ VENDOR
	PATIO TABLES/ CHAIRS	O	GC	NATIONAL ACCOUNT
	DRIVE-THRU MENU BOARD	O	V	GC TO COORD. ROUGH-INS W/ VENDOR
	DRIVE-THRU SPEAKER POST	O	V	BASE BY GC VERIFY SCOPE
	DRIVE-THRU CANOPY POST	O	V	BASE BY V W/ SIGN VENDOR
	DRIVE-THRU SENSOR LOOP	O	GC	NATIONAL ACCOUNT
	PATIO FENCING/ WALLS	GC	GC	
	BUILDING EXTERIOR			
	STOREFRONT WINDOWS & DOORS	GC	GC	
	BUILDING SIGNAGE	O	V	GC TO COORD. ROUGH-INS W/ VENDOR
	EXTERIOR BLUE STRIP LIGHTING	O	V	GC TO COORD. ROUGH-INS W/ VENDOR
	AWNINGS	O	V	NATIONAL ACCOUNT
	BUILDING LIGHTING	GC	GC	NATIONAL ACCOUNT
	BUILDING SHELL AND FINISHES	GC	GC	
	INTERIOR			
66	MENU BOARD AND SIGNAGE	O	V	GC TO COORD. ROUGH-INS W/ VENDOR
	INTERIOR WALLS	GC	GC	
	FLOOR AND WALL TILE	GC	GC	NATIONAL ACCOUNT
	PAINT	GC	GC	
	WALLCOVERING	GC	GC	NATIONAL ACCOUNT
	FRP	GC	GC	NATIONAL ACCOUNT
	S/S WALL PANELS	GC	GC	
	CARPET	GC	GC	NATIONAL ACCOUNT
	INT. DOORS/ FRAMES/ HARDWARE	GC	GC	NATIONAL ACCOUNT
	ACOUSTICAL CEILING	GC	GC	
	ARTWORK	O	GC	
	S/S COUNTER BASES	FEC	GC	GC TO TILE BASES
	ACRYLIC FLOORING SYSTEM	GC	GC	NATIONAL ACCOUNT
	WAINSCOTING	GC	GC	NATIONAL ACCOUNT
	RESTROOM MIRRORS	O	GC	
	RESTROOM ACCESSORIES	GC / O/ FEC	GC	SEE RESTROOM ACCESSORY SCHEDULE
	OPTIONAL AED/ SHARPS CONTAINER	O	GC	
	MILLWORK ITEMS			
	SOLID SURFACE WINDOW SILLS	GC	GC	
	RESTROOM VANITIES & SUPPORTS	GC	GC	
	SOLID SURFACE TO-GO COUNTER	GC	GC	
	SOLID SURFACE ANGLED WALL CAP	GC	GC	
800	WOOD TRIM PACKAGE	FEC	GC	GC TO ORDER THROUGH FEC
	ELECTRICAL	SUPPLIED	INSTALLED	NOTES
	LIGHTING AND SWITCHGEAR	GC	GC	NATIONAL ACCOUNT
	DEVICES	GC	GC	NATIONAL ACCOUNT
	POS SYSTEM	O	V	EC TO SET BOXES AND PULL WIRE
	DIG. FEATURE BOARDS/ BRACKETS	O	GC	
	PLUMBING			
19	HAND SINKS	FEC	GC	
12	GREASE CONTAINMENT SYSTEM	O	V	PIPING/ ELECTRICAL BY GC PER PLANS
	RESTROOM FIXTURES	GC	GC	NATIONAL ACCOUNT
	SODA SYSTEM	O	V/ GC	NATIONAL ACCOUNT - COORD W/ VENDOR
28	DISHWASHER	O	GC/ FEC	GC TO COORD W/ FEC
30	EYE WASH STATION	FEC	GC	GC TO INSTALL MIXING VALVE
	PIPING FOR WATER, GAS, WASTE OIL	GC	GC	
	HVAC			
52	FRYER HOOD	GC	GC	NATIONAL ACCOUNT
49	GRILL HOOD	GC	GC	NATIONAL ACCOUNT
	ANUL SYSTEM	GC	GC/ V	NATIONAL ACCOUNT
	GRILLS/ DIFFUSERS	GC	GC	NATIONAL ACCOUNT
	CLUSTARD CONDENSING UNITS (x3)	O	GC/ FEC	GC TO COORDINATE W/ FEC
	WALK-IN CONDENSING UNITS (x2)	FEC	GC/ FEC	GC TO COORDINATE W/ FEC
	HVAC TEST AND BALANCE	V	N/ A	GC TO COORDINATE W/ VENDOR
	FOODSERVICE EQUIPMENT - (ITEMS W/ GC SCOPE)			
63	CLUSTARD MACHINE	O	FEC/ GC	
70	SHAKE MACHINE	O	V/ GC	
1	WALK-IN COOLER	FEC	GC/ FEC	
2	WALK-IN FREEZER	FEC	GC/ FEC	
509	REFRIGERATION LINE SETS	FEC	FEC	GC TO COORDINATE W/ FEC
	**GC REQUIRED TO MAKE FINAL HOOK UPS OF ALL EQUIPMENT. REFER TO FOODSERVICE EQUIPMENT SCHEDULE FOR FULL LIST OF FEC SUPPLIED/ INSTALLED EQUIPMENT			

WARNING: These plans are for the exclusive use of Culver Franchising System, LLC and authorized franchise holders only. No part of these plans or the design they represent may be duplicated or reproduced without permission of Culver Franchising System, LLC


By				
Revision				
Date				

Culver Franchising System, LLC
1240 Water Street
Prairie du Sac, WI 53578
608-643-7980


CULVER FRANCHISING SYSTEM, LLC
REIMAGE 2027
CULVER'S OF SHAKOPEE, MN #0131

Sheet Contents	
TITLE & INDEX	
Project No.	Shakopee, MN #0131
Drawn By:	E. ROCKWEILER
Date:	06/12/26

Sheet
T-1

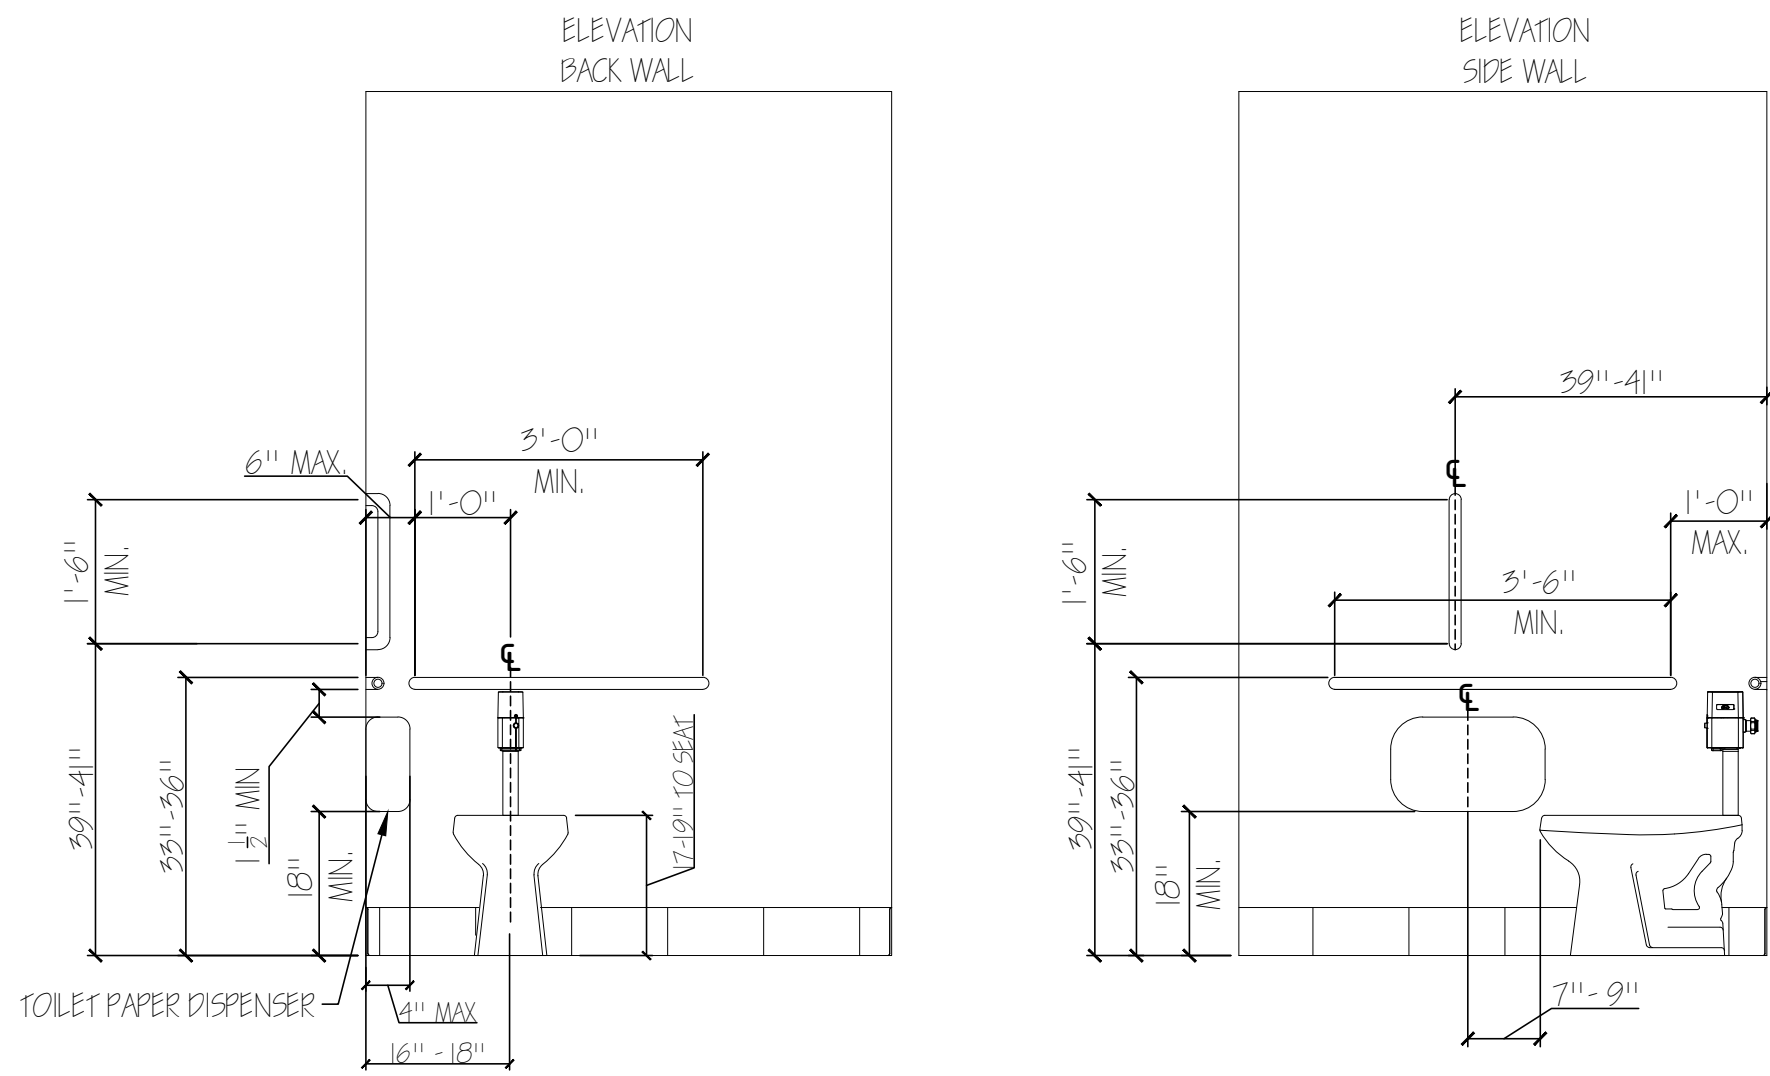


1 ADA TOILET STALL CLEARANCES TYP.
A-9 SCALE: 1/2" = 1'-0"


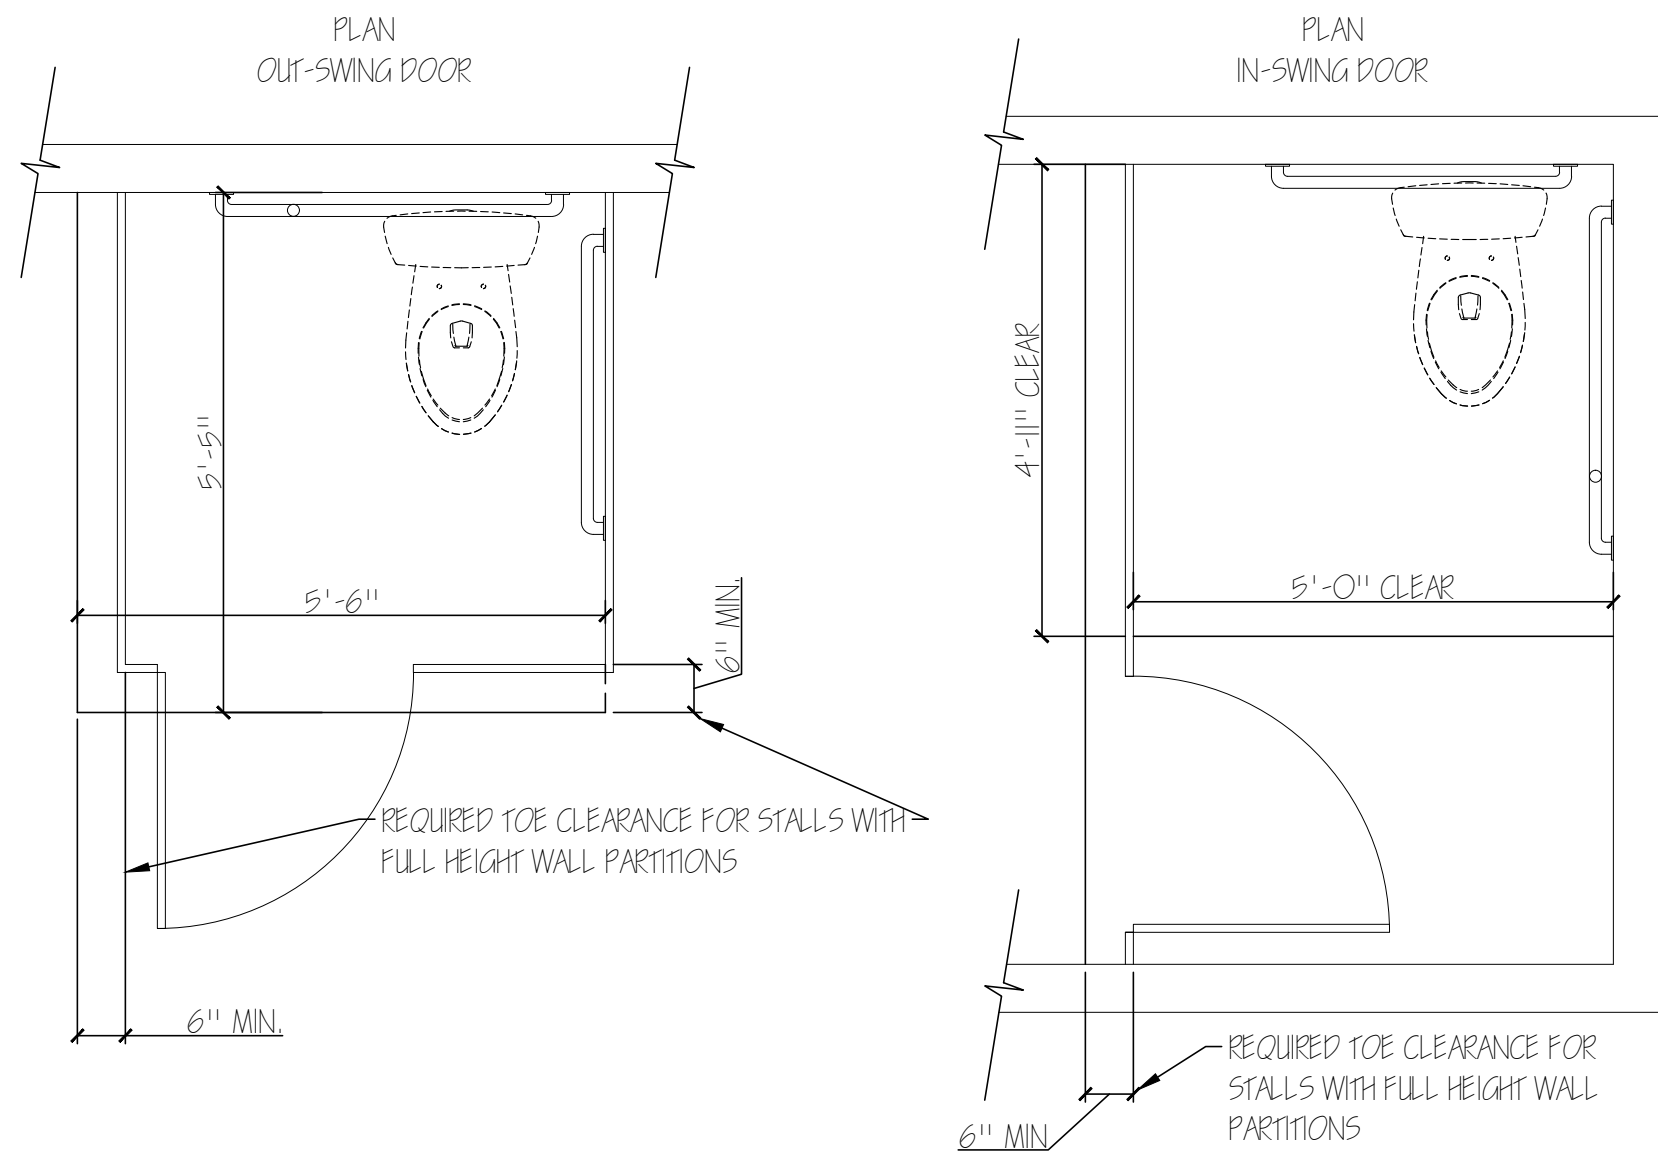


GENERAL NOTES:


- IT IS THE GC'S RESPONSIBILITY TO ENSURE ALL WALL ACCESSORIES, VANITIES AND PLUMBING FIXTURES AND ACCESSORIES COMPLY WITH FEDERAL, STATE AND LOCAL ACCESSIBILITY LAWS AND CODES.
- THESE DETAILS ONLY REPRESENT A PORTION OF THE FEDERAL ADA CODE. FULL COMPLIANCE WITH OTHER ADA DETAILS AND STATE SPECIFIC CODES IS THE RESPONSIBILITY OF THE GC.

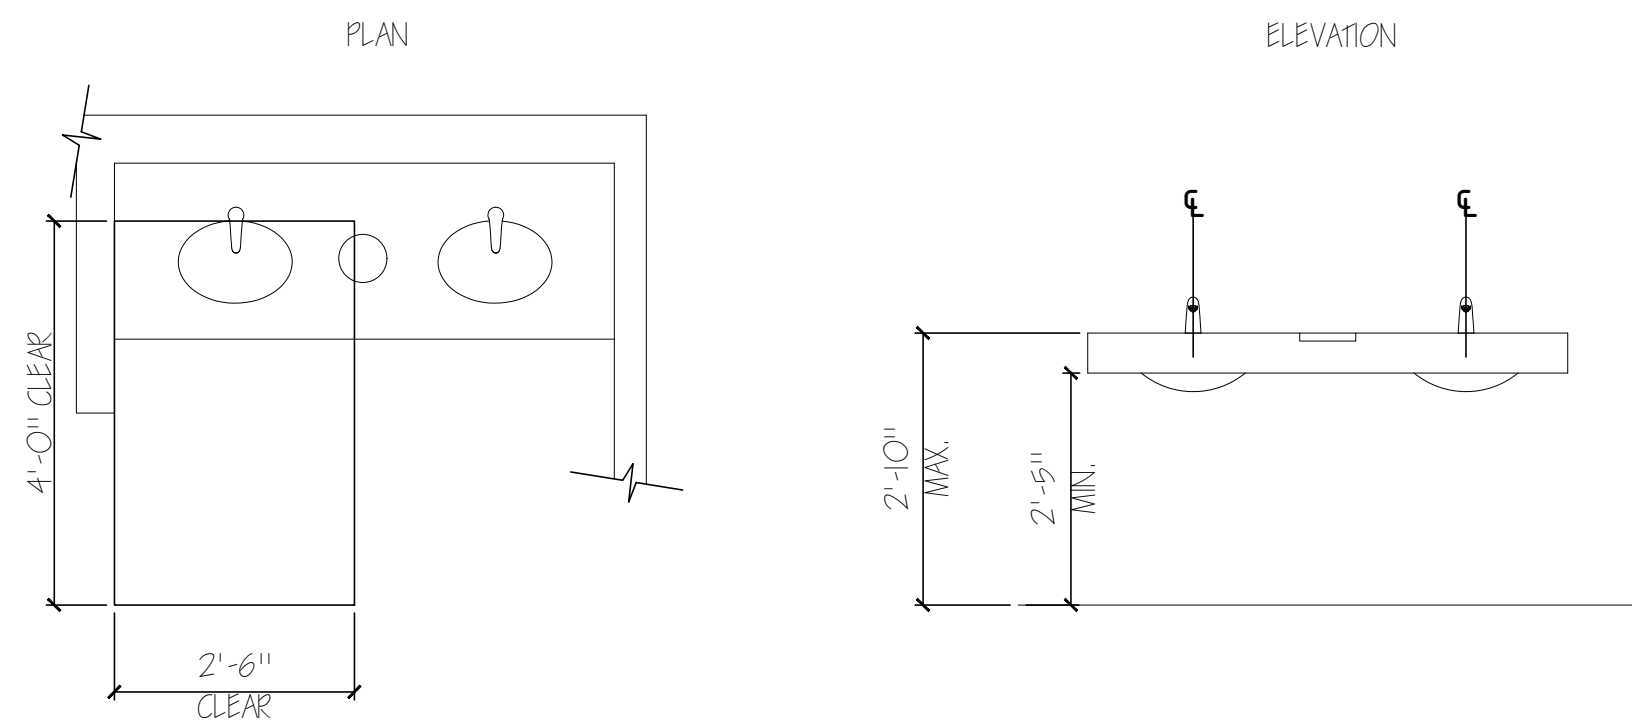


2 ADA LAVATORY CLEARANCES TYP.
A-9 SCALE: 1/2" = 1'-0"

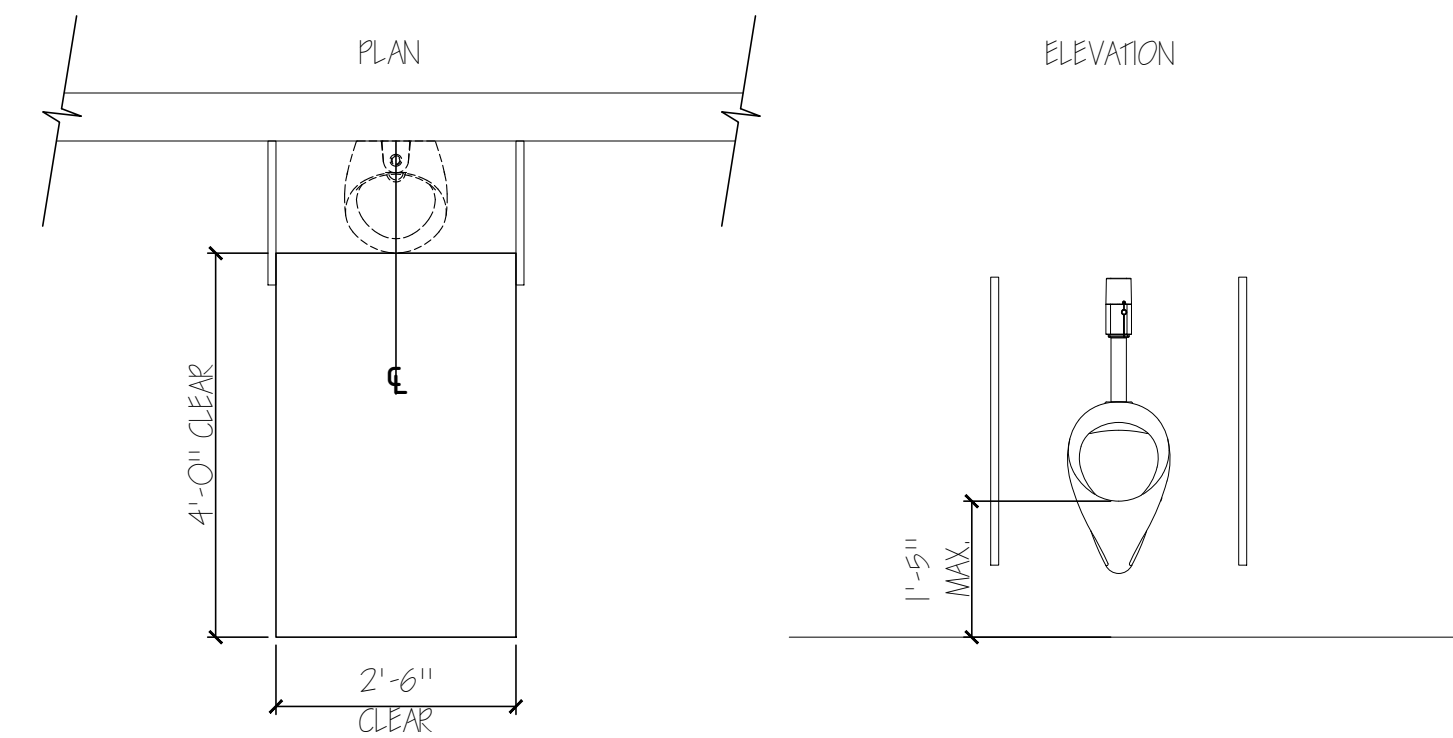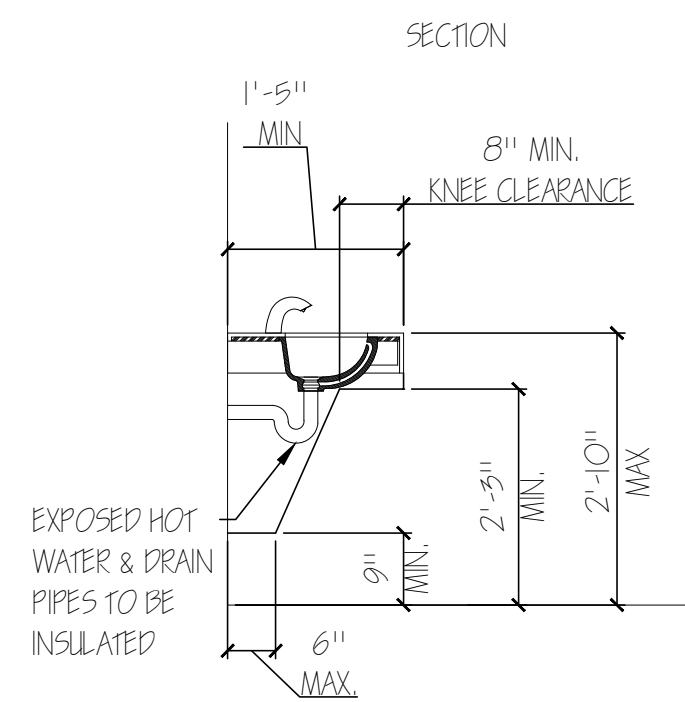

3 ADA URINAL CLEARANCES TYP.
A-9 SCALE: 1/2" = 1'-0"

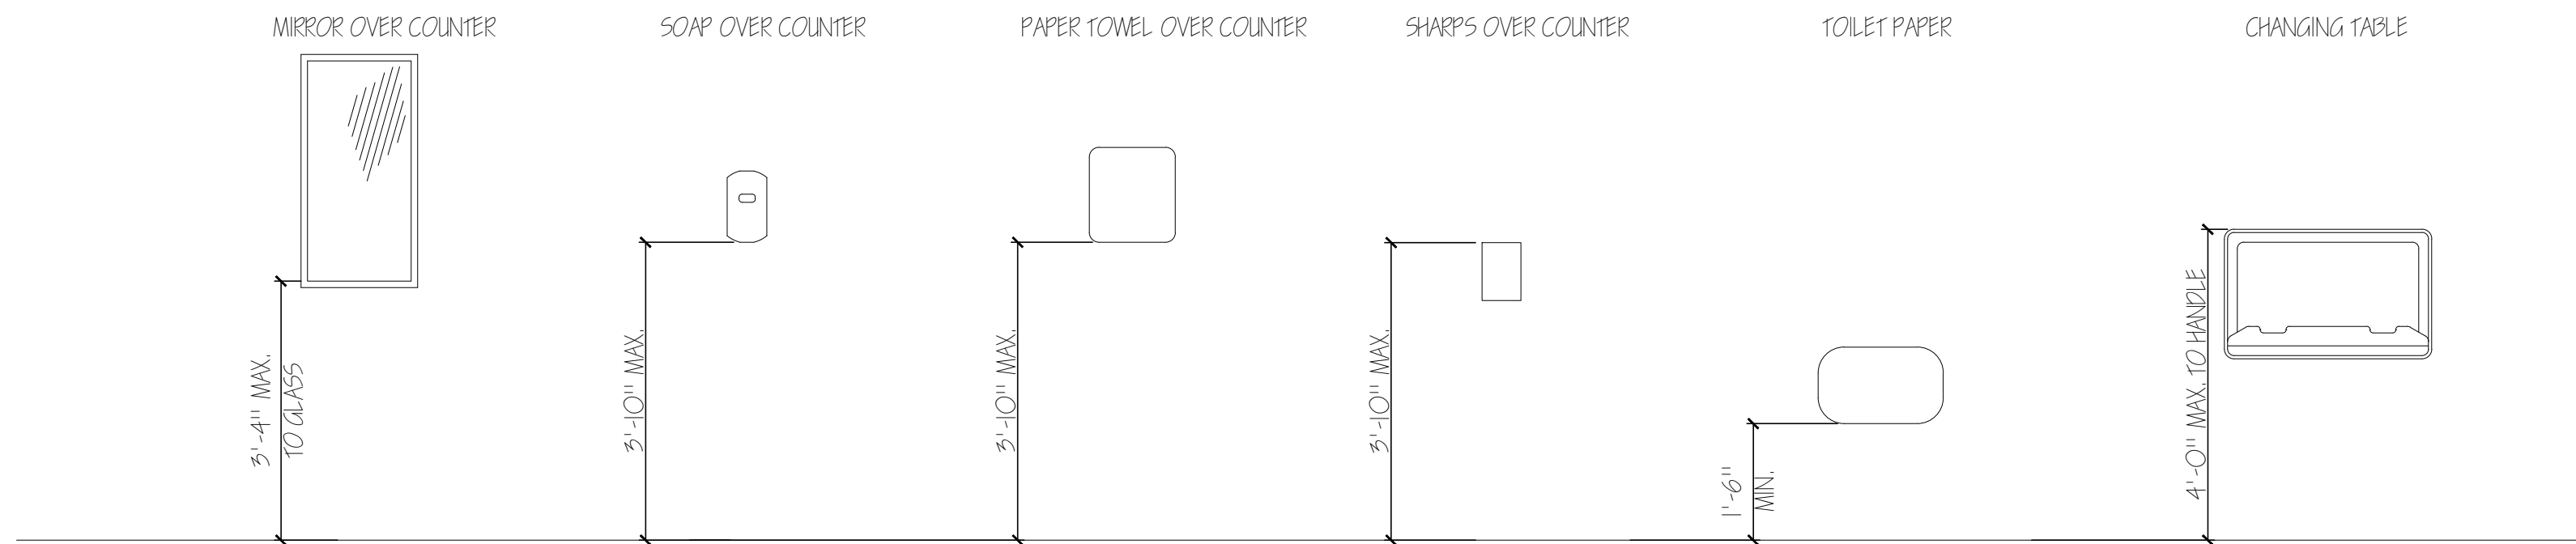

4 ADA RESTROOM ACCESSORIES TYP.
A-9 SCALE: 1/2" = 1'-0"

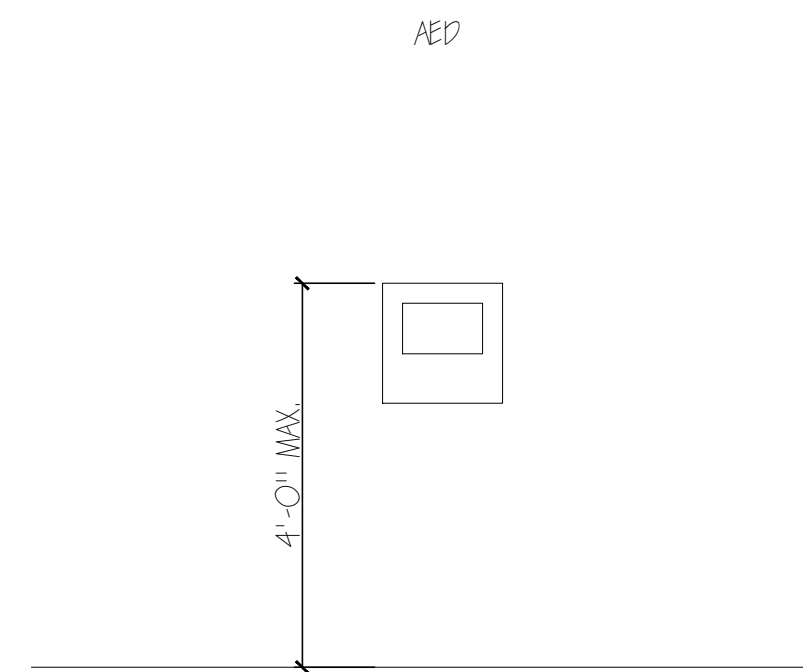

5 ADA DINING ROOM ACCESSORIES TYP.
A-9 SCALE: 1/2" = 1'-0"


WARNING: These plans are for the exclusive use of Culver Franchising Systems, Inc. and authorized franchise holders only. No part of these plans or the design they represent may be duplicated or reproduced without permission of Culver Franchising System, Inc.

Date	Revision	By

Culver Franchising System, Inc.
1240 Water Street
Prairie du Sac, WI 53578
608-643-7980

CULVER FRANCHISING SYSTEM, LLC
TYPICAL ACCESSIBILITY DETAILS

Sheet Contents
ACCESSIBILITY DETAILS
Project No.
Drawn By:
Date:

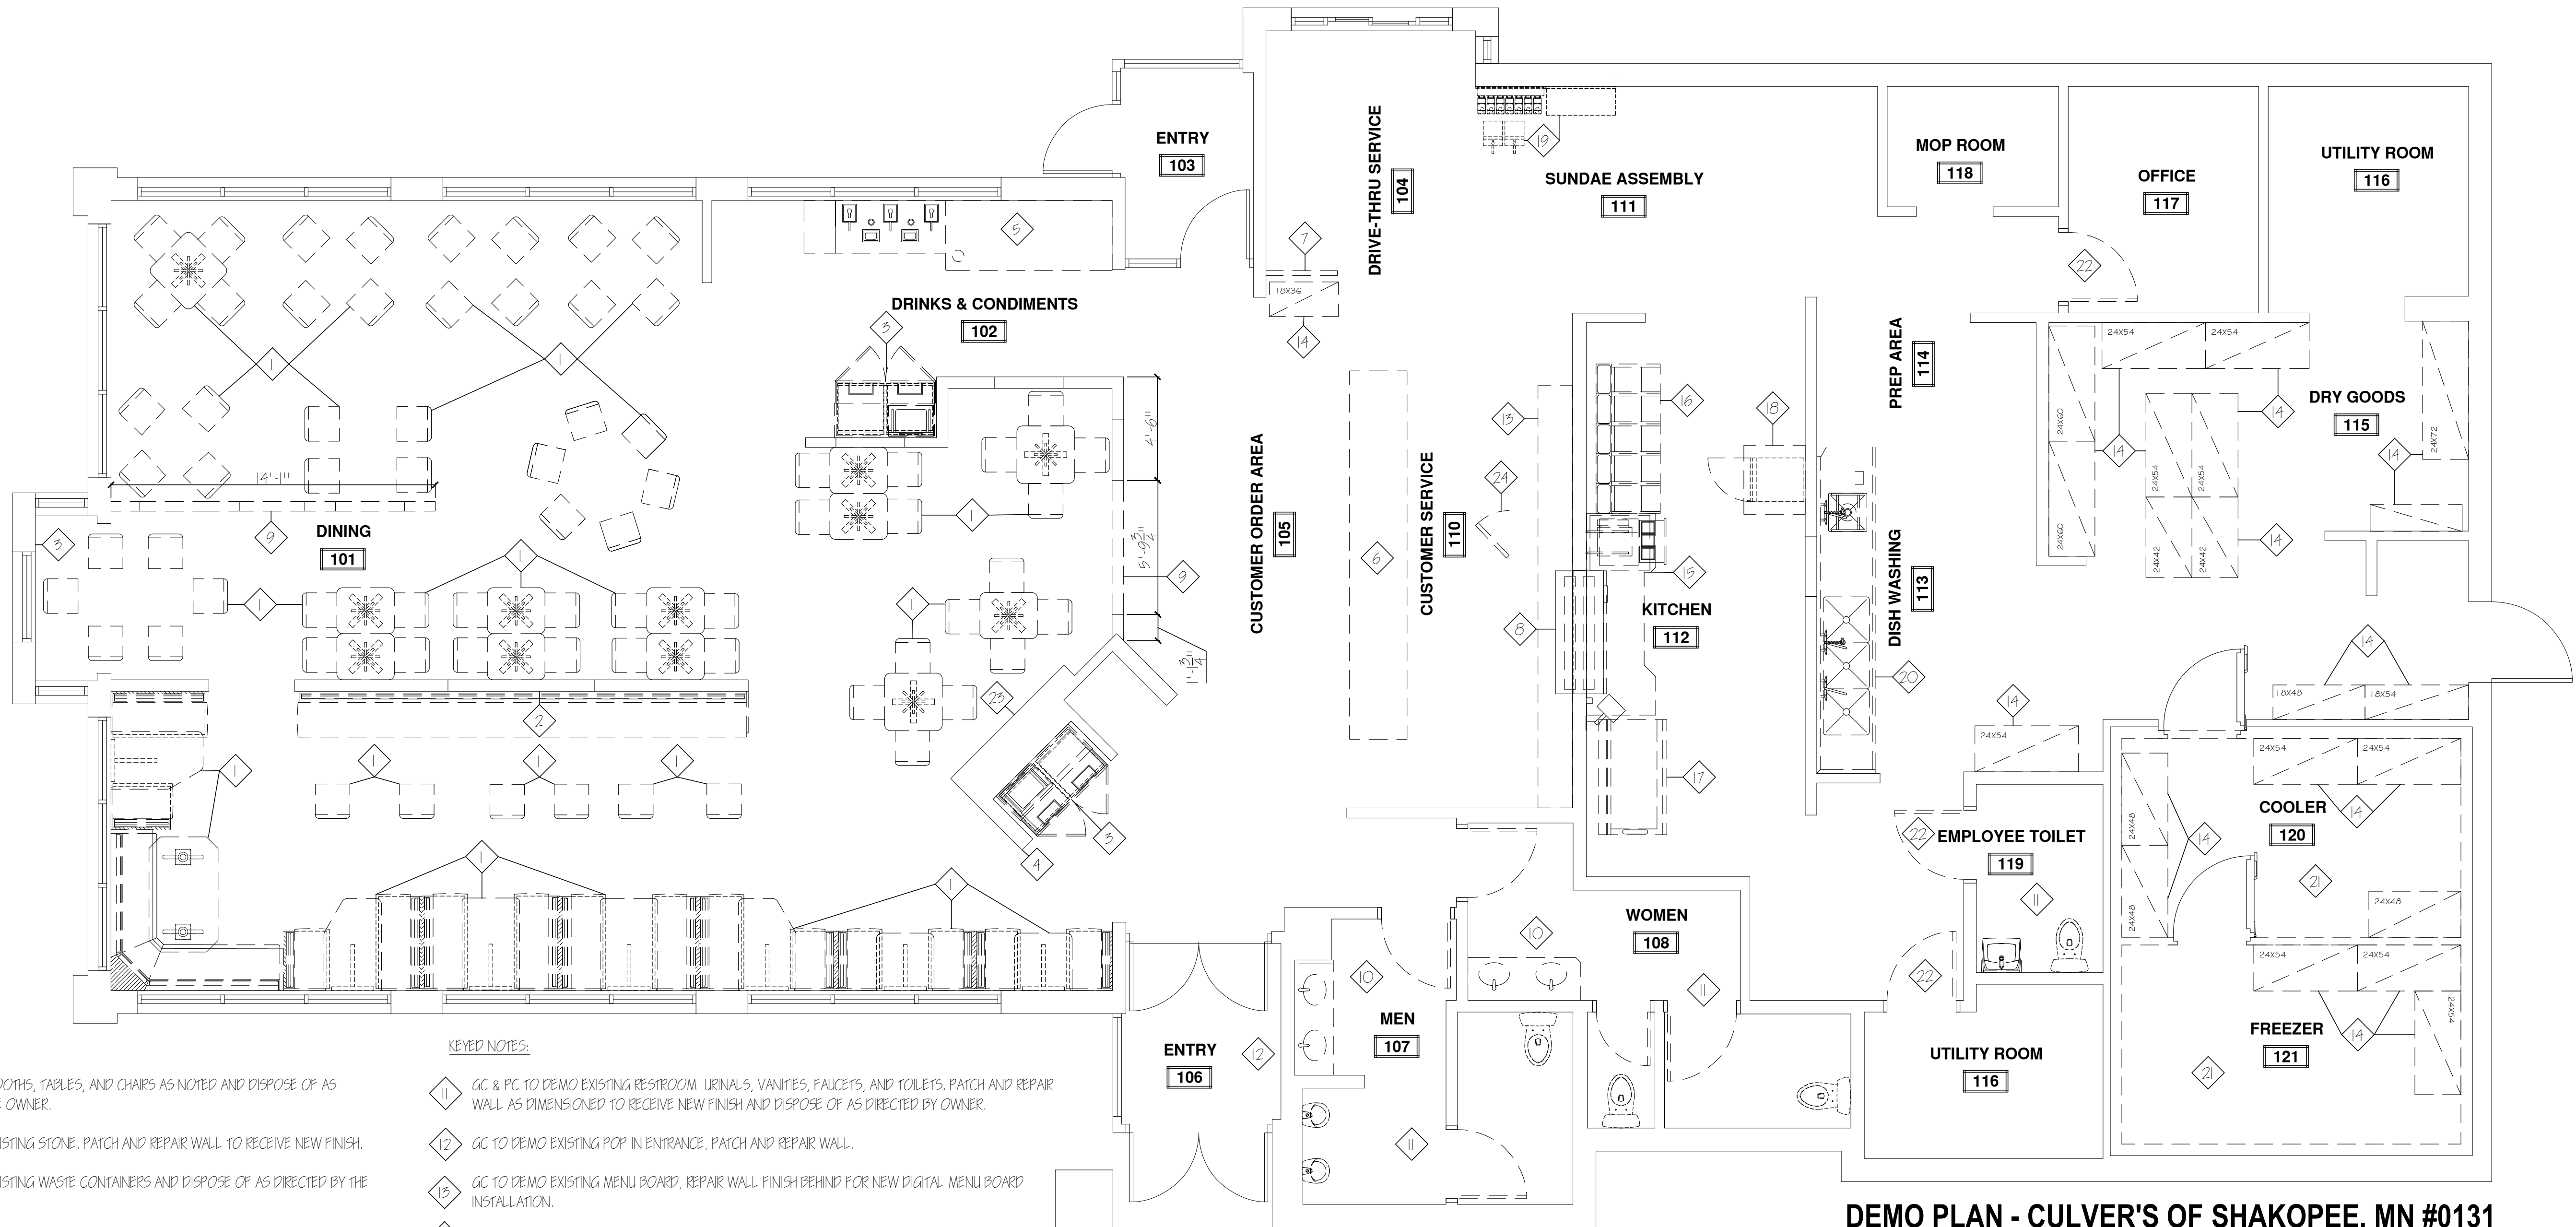

KEYED NOTES:

- GC TO DEMO BOOTHS, TABLES, AND CHAIRS AS NOTED AND DISPOSE OF AS DIRECTED BY THE OWNER.
- GC TO DEMO EXISTING STONE. PATCH AND REPAIR WALL TO RECEIVE NEW FINISH.
- GC TO DEMO EXISTING WASTE CONTAINERS AND DISPOSE OF AS DIRECTED BY THE OWNER.
- GC TO DEMO EXISTING MILLWORK AND RECESSED DISPLAY CASE AT EXISTING WALL. DISPOSE OF AS DIRECTED BY OWNER.
- GC TO DEMO EXISTING DRINKS AND CONDIMENTS COUNTERS AND DISPOSE OF AS DIRECTED BY THE OWNER.
- GC TO DEMO EXISTING CASHIER COUNTER AND DISPOSE OF AS DIRECTED BY THE OWNER. OWNER TO COORDINATE REMOVAL AND REINSTALLATION OF THE P.O.S. SYSTEM.
- GC TO DEMO EXISTING END PANEL AT DRIVE-THRU SODA COUNTER. DISPOSE OF AS DIRECTED BY OWNER.
- GC TO DEMO EXISTING PASS-THRU AND DISPOSE OF AS DIRECTED BY OWNER.
- GC TO DEMO EXISTING WALL AND ACCENT GLASS.
- GC TO DEMO RESTROOM ENTRANCE AND STALL DOORS AND FRAMES.


KEYED NOTES:

- GC & PC TO DEMO EXISTING RESTROOM URINALS, VANITIES, FAUCETS, AND TOILETS. PATCH AND REPAIR WALL AS DIMENSIONED TO RECEIVE NEW FINISH AND DISPOSE OF AS DIRECTED BY OWNER.
- GC TO DEMO EXISTING POP IN ENTRANCE. PATCH AND REPAIR WALL.
- GC TO DEMO EXISTING MENU BOARD. REPAIR WALL FINISH BEHIND FOR NEW DIGITAL MENU BOARD INSTALLATION.
- GC TO DEMO EXISTING SHELVING AND DISPOSE OF AS DIRECTED BY THE OWNER.
- GC TO DEMO EXISTING MIDDLE TABLE, FRY DUMP, AND HEAT LAMP AND DISPOSE OF AS DIRECTED BY OWNER.
- GC TO DEMO EXISTING FRYERS AND DISPOSE OF AS DIRECTED BY OWNER.
- GC TO DEMO EXISTING GRILL AND DISPOSE OF AS DIRECTED BY OWNER.
- GC TO DEMO EXISTING CHICKEN HOLDING CART AND DISPOSE OF AS DIRECTED BY OWNER.
- GC TO DEMO EXISTING SYRUP PUMPS AND SUNDAE TOPPING SYSTEM. DISPOSE OF AS DIRECTED BY OWNER.
- GC TO DEMO EXISTING DISH WASH LINE AND DISPOSE OF AS DIRECTED BY OWNER. VERIFY SCOPE WITH OWNER.
- GC TO DEMO EXISTING COOLER AND FREEZER. DISPOSE OF AS DIRECTED BY OWNER. VERIFY SCOPE WITH OWNER.
- GC TO DEMO OFFICE, UTILITY AND EMPLOYEE RESTROOM DOORS AND FRAMES. DISPOSE OF AS DIRECTED BY OWNER.
- GC TO DEMO EXISTING ELECTRIC FIREPLACE AND DISPOSE OF AS DIRECTED BY OWNER.
- GC TO DEMO EXISTING DOOR PANEL AT SET COUNTER AND DISPOSE OF AS DIRECTED BY OWNER.

GENERAL NOTES:

- Demo items indicated in plan by dashed lines.
- Demo wainscoting.
- Demo carpet, tile and tile base, and interior stone see sheet A-6 for new vs. existing locations.
- See reflected ceiling plan, sheet A-5 for ceiling demo information.

DEMO PLAN - CULVER'S OF SHAKOPEE, MN #0131
SCALE: 1/4" = 1'-0"

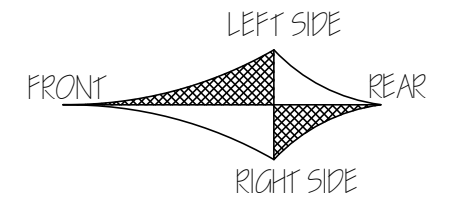

WARNING: These plans are for the exclusive use of Culver Franchising System, LLC and authorized franchise holders only. No part of these plans or the design they represent may be duplicated or reproduced without permission of Culver Franchising System, LLC

CULVER FRANCHISING SYSTEM, LLC

REIMAGE 2027

CULVER'S OF SHAKOPEE, MN #0131

Sheet Contents

DEMO
PLAN

Project No.
Shakopee, MN #0131
Drawn By:
E. ROCKWEILER
Date:
06/12/26


Sheet

D-1


Culver Franchising
System, LLC
1240 Water Street
Prairie du Sac, WI 53578
608-643-7980

By
Date
Revision

DOOR TYPES

 

TYPE "C"
MARLITE 36" X 84" HIGH PRESSURE
LAMINATE (HPL) DOOR FACED WITH
WILSONART WA 10776-60
KENSINGTON MAPLE

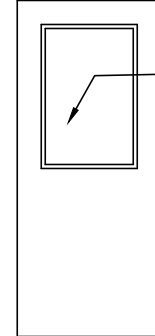


TYPE "D"
MARLITE 36" X 84" HIGH PRESSURE
LAMINATE (HPL) DOOR FACED WITH
WILSONART WA 10776-60
KENSINGTON MAPLE TEMPERED
CLEAR GLASS LITE BY GC.



TYPE "E"
MARLITE 36" X 84" HIGH
PRESSURE LAMINATE (HPL) DOOR
FACED WITH WILSONART WA
10776-60 KENSINGTON MAPLE

FRAME TYPES

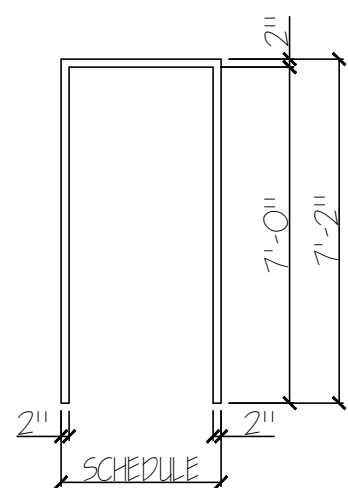

FRAME "E"
MARLITE MODEL AAA SATIN
ALUMINUM FRAME - 500 SERIES
W/ BEARING HINGES

DOOR SCHEDULE


DOOR:					FRAME:		HARDWARE	NOTES
NO.	WIDTH	HGT.	MAT'L	TYPE	MAT'L	TYPE	GROUP	
1	36"	84"	HPL	C	ALUM	E, 3'-4"	5	DOOR PRE-HUNG IN FRAME, OPTIONAL ARM PULL
2	36"	84"	HPL	C	ALUM	E, 3'-4"	5	DOOR PRE-HUNG IN FRAME, OPTIONAL ARM PULL
3	28"	60"	HPL	E	ALUM	E, 2'-8"	6	DOOR PRE-HUNG IN FRAME
4	36"	60"	HPL	E	ALUM	E, 3'-4"	6	DOOR PRE-HUNG IN FRAME
5	36"	60"	HPL	E	ALUM	E, 3'-4"	6	DOOR PRE-HUNG IN FRAME
6	36"	84"	HPL	D	ALUM	E, 3'-4"	7	GLASS PROVIDED BY GC
7	34"	84"	HPL	C	ALUM	E, 3'-4"	8	DOOR PRE-HUNG IN FRAME
8	34"	84"	HPL	C	ALUM	E, 3'-4"	9	DOOR PRE-HUNG IN FRAME

*NOTES - GC TO VERIFY ALL EXISTING DOOR/FRAME SIZES IN FIELD

PLUMBING FIXTURES:
*SEE INTERIOR FINISH SELECTIONS PACKET FOR REQUIRED FIXTURES


LAVATORY FAUCET:
TOTO T28551ET#CP COMMERCIAL SELF POWERED HYDROELECTRIC FAUCET 5 GPM.
INCLUDE TLE28002UI#CP SPOUT, TLE05503UI 5 GPM CONTROLLER,
TLE0570UIMV. ADA COMPLIANT.
TOILET: GC TO VERIFY WATER SUPPLY BEFORE SELECTING TOILET OPTION
OPTION 1: TOTO C51244EP ENTRADA CLOSE COUPLED TOILET
TOILET SEAT: TOTO SC5534
OPTION 2: TOTO C1725CLF#OI COMMERCIAL ADA COMPLAINT TOILET
TOILET FLUSH VALVE: TOTO TE11LB52#CP COMMERCIAL SELF POWERED
HYDROELECTRIC FLUSH VALVE SYTEM. 1.28. ADA COMPLIANT
TOILET SEAT: TOTO SC5534#OI COMMERCIAL TOILET SEAT

URINAL:
TOTO UN04E#OI COMMERCIAL WALL HUNG LOW CONSUMPTION WASHOUT URINAL.
INCLUDE TH15017 5/5 DRAIN COVER. ADA COMPLIANT.
URINAL FLUSH VALVE:
TOTO TE11LA12#CP COMMERCIAL SELF POWERED HYDROELECTRIC FLUSH VALVE SYSTEM.
5 GPF. ADA COMPLIANT

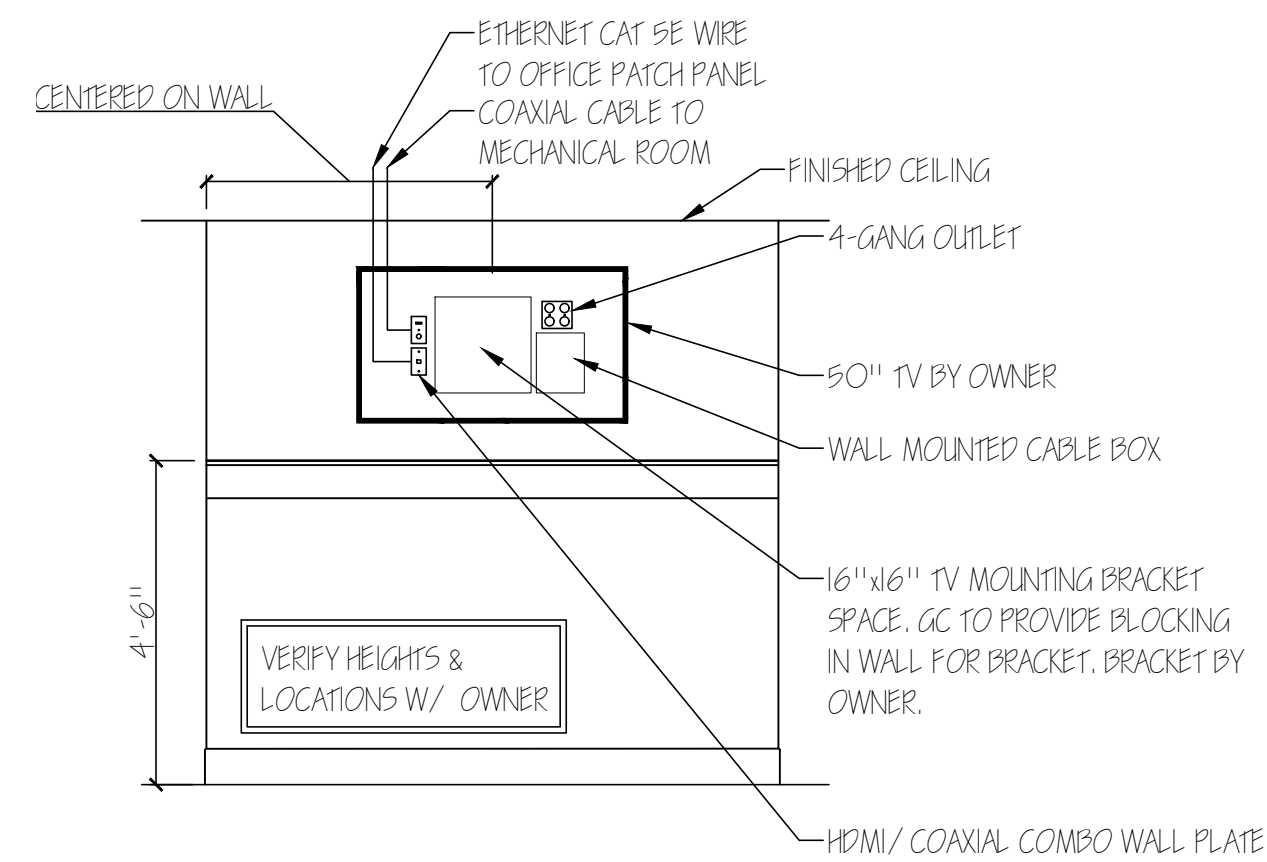

1 DINING ROOM TV

SCALE: 3/8" = 1'-0"

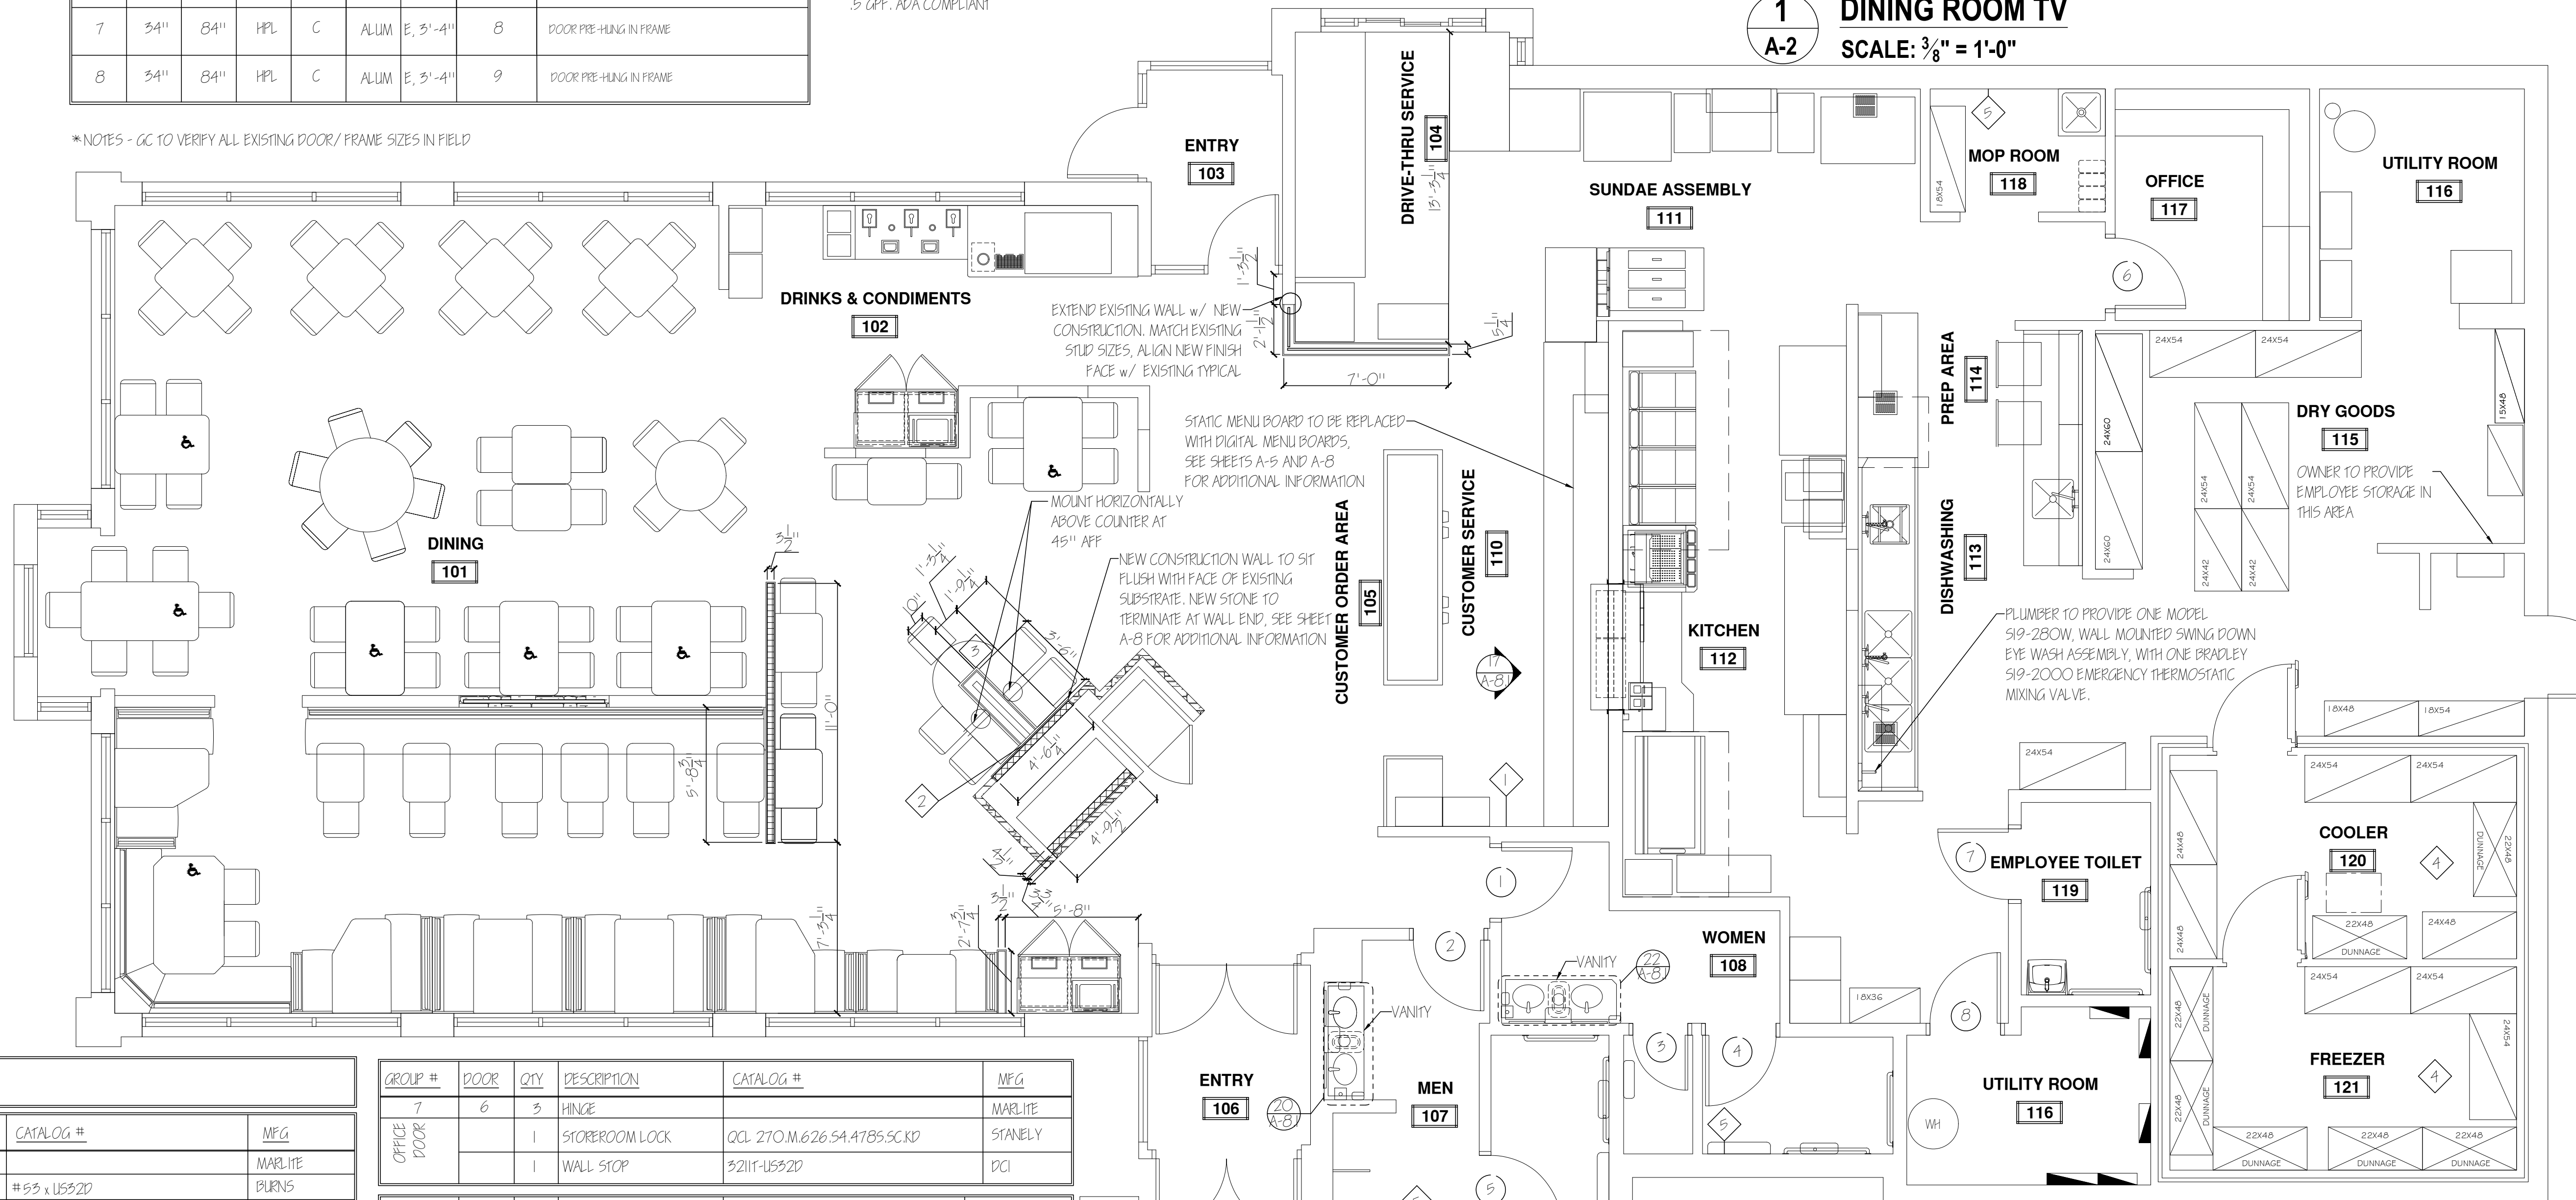

GENERAL NOTES:

- THIS FLOOR PLAN HAS NOT BEEN FIELD VERIFIED.
- UNLESS NOTED OTHERWISE, DIMENSIONS SHOWN ARE FACE OF FRAMING TO FACE OF FRAMING FOR NEW CONSTRUCTION. DIMENSIONS AT EXISTING CONSTRUCTIONS ARE FROM GYP. BOARD OR FINISH SURFACE.
- NEW WALLS RECEIVING WALL MOUNTED TABLES TO HAVE PLYWOOD SUBSTRATE. GC TO VERIFY SUBSTRATE OF EXISTING WALL TO BE PLYWOOD. SEE SHEET FS-1 FOR WALL MOUNTED TABLE LOCATIONS.

KEYED NOTES:

- DIGITAL FEATURE BOARD TO BE RELOCATED, ELIMINATE EXISTING ELECTRICAL, REPAIR WALL TO RECEIVE NEW FINISH.
- TV IS EXISTING, GC TO REMOVE AND REINSTALL, SEE 1/ A-2 FOR REQUIREMENTS
- SOLID SURFACE TO-GO COUNTER BY GC, MOUNTED 42" AFF TO BE HELD 1" OFF WALL.
- WALK-INS TO BE REPLACED. GC TO VERIFY THAT THE EXISTING WALK IN COOLER/ FREEZER FLOOR DETAILS MATCH THE EXISTING SHOP DRAWING AND COORDINATE ANY CHANGES WITH THE PEC AT AN EARLY DATE TO GET THE WALK IN ORDERED IN TIME FOR THE REIMAGE.
- GC TO PROVIDE OPTIONS TO REPLACE ELECTRIC HEATER COVER AT ROOMS 107, 108, AND 118

SEAT & TOP COUNT:

DESCRIPTION	TOPS	SEATS
2 PERSON TABLE	11	22
4 PERSON TABLE	10	40
6 PERSON TABLE	2	12
2 PERSON BOOTH	1	2
3 PERSON BOOTH	3	9
4 PERSON BOOTH	2	8
6 PERSON BOOTH	1	6
TO GO WAITING	1	5
TOTAL	31	104
ADA	6	

HARDWARE GROUPS

GROUP #	DOOR	QTY	DESCRIPTION	CATALOG #	MFG
PUBLIC RESTROOM DOOR	1, 2	3	HINGE		MARLITE
		1	PUSHPLATE	#53 x US32D	BURNS
		1	PULLPLATE	#5325B x US32D	BURNS
		1	SURFACE CLOSER	4011	LCN
		2	KICK PLATE	8" x 34" ALUM 62B	ROCKWOOD
PR SHAL DOOR	3, 4, 5	1	SPRING HINGE	SATIN 1502 SPRING 4.5x4	MCKINNEY
		1	PRIVACY LOCK	QCL240.M.626.54.4785.5C.6	STANLEY
		1	WALL STOP	3211T-US32D	DCI

*NOTES - ARM PULL OPTIONAL, VERIFY WITH FRANCHISEE.

GROUP #	DOOR	QTY	DESCRIPTION	CATALOG #	MFG
PR SHAL DOOR	3, 4, 5	2	HINGE		MARLITE
		1	SPRING HINGE	SATIN 1502 SPRING 4.5x4	MCKINNEY
		1	PRIVACY LOCK	QCL240.M.626.54.4785.5C.6	STANLEY
PR SHAL DOOR	3, 4, 5	1	WALL STOP	3211T-US32D	DCI

*NOTES - INSTALL SPRING HINGE TO HOLD DOOR SLIGHTLY OPEN.

GROUP #	DOOR	QTY	DESCRIPTION	CATALOG #	MFG
OFFICE DOOR	6	3	HINGE		MARLITE
		1	STOREROOM LOCK	QCL 270.M.626.54.4785.5C.KD	STANLEY
		1	WALL STOP	3211T-US32D	DCI

GROUP #	DOOR	QTY	DESCRIPTION	CATALOG #	MFG
UTILITY ROOM DOOR	7	3	HINGE		MARLITE
		1	PRIVACY LOCK	QCL240.M.626.5A.47B5.5C.6	STANLEY
		2	KICK PLATE	8" x 34" ALUM 62B	ROCKWOOD
		1	WALL STOP	3211T-US32D	DCI
*NOTE - ARM PULL IS OPTIONAL, VERIFY WITH FRANCHISEE					

GROUP #	DOOR	QTY	DESCRIPTION	CATALOG #	MFG
UTILITY DOOR	8	3	HINGE		MARLITE
		1	STOREROOM LOCK	QCL 270.M.626.54.4785.5C.KD	STANLEY
		1	WALL STOP	3211T-US32D	DCI
UTILITY DOOR	8	2	KICK PLATE	8" x 34" ALUM 62B	ROCKWOOD

WARNING: These plans are for the exclusive use of Culver Franchising System, LLC authorized franchise holders only. No part of these plans or the design they represent may be duplicated or reproduced without permission of Culver Franchising System, LLC

CULVER FRANCHISING SYSTEM, LLC
REIMAGE 2027
CULVER'S OF SHAKOPEE, MN #0131

Sheet Contents

FLOOR PLAN


Project No.
Shakopee, MN #0131
Drawn By:
E. ROCKWEILER
Date:
06/12/26

Sheet


A-2

By
Date
Revision

Culver Franchising
System, LLC
1240 Water Street
Prairie du Sac, WI 53578
608-643-7980

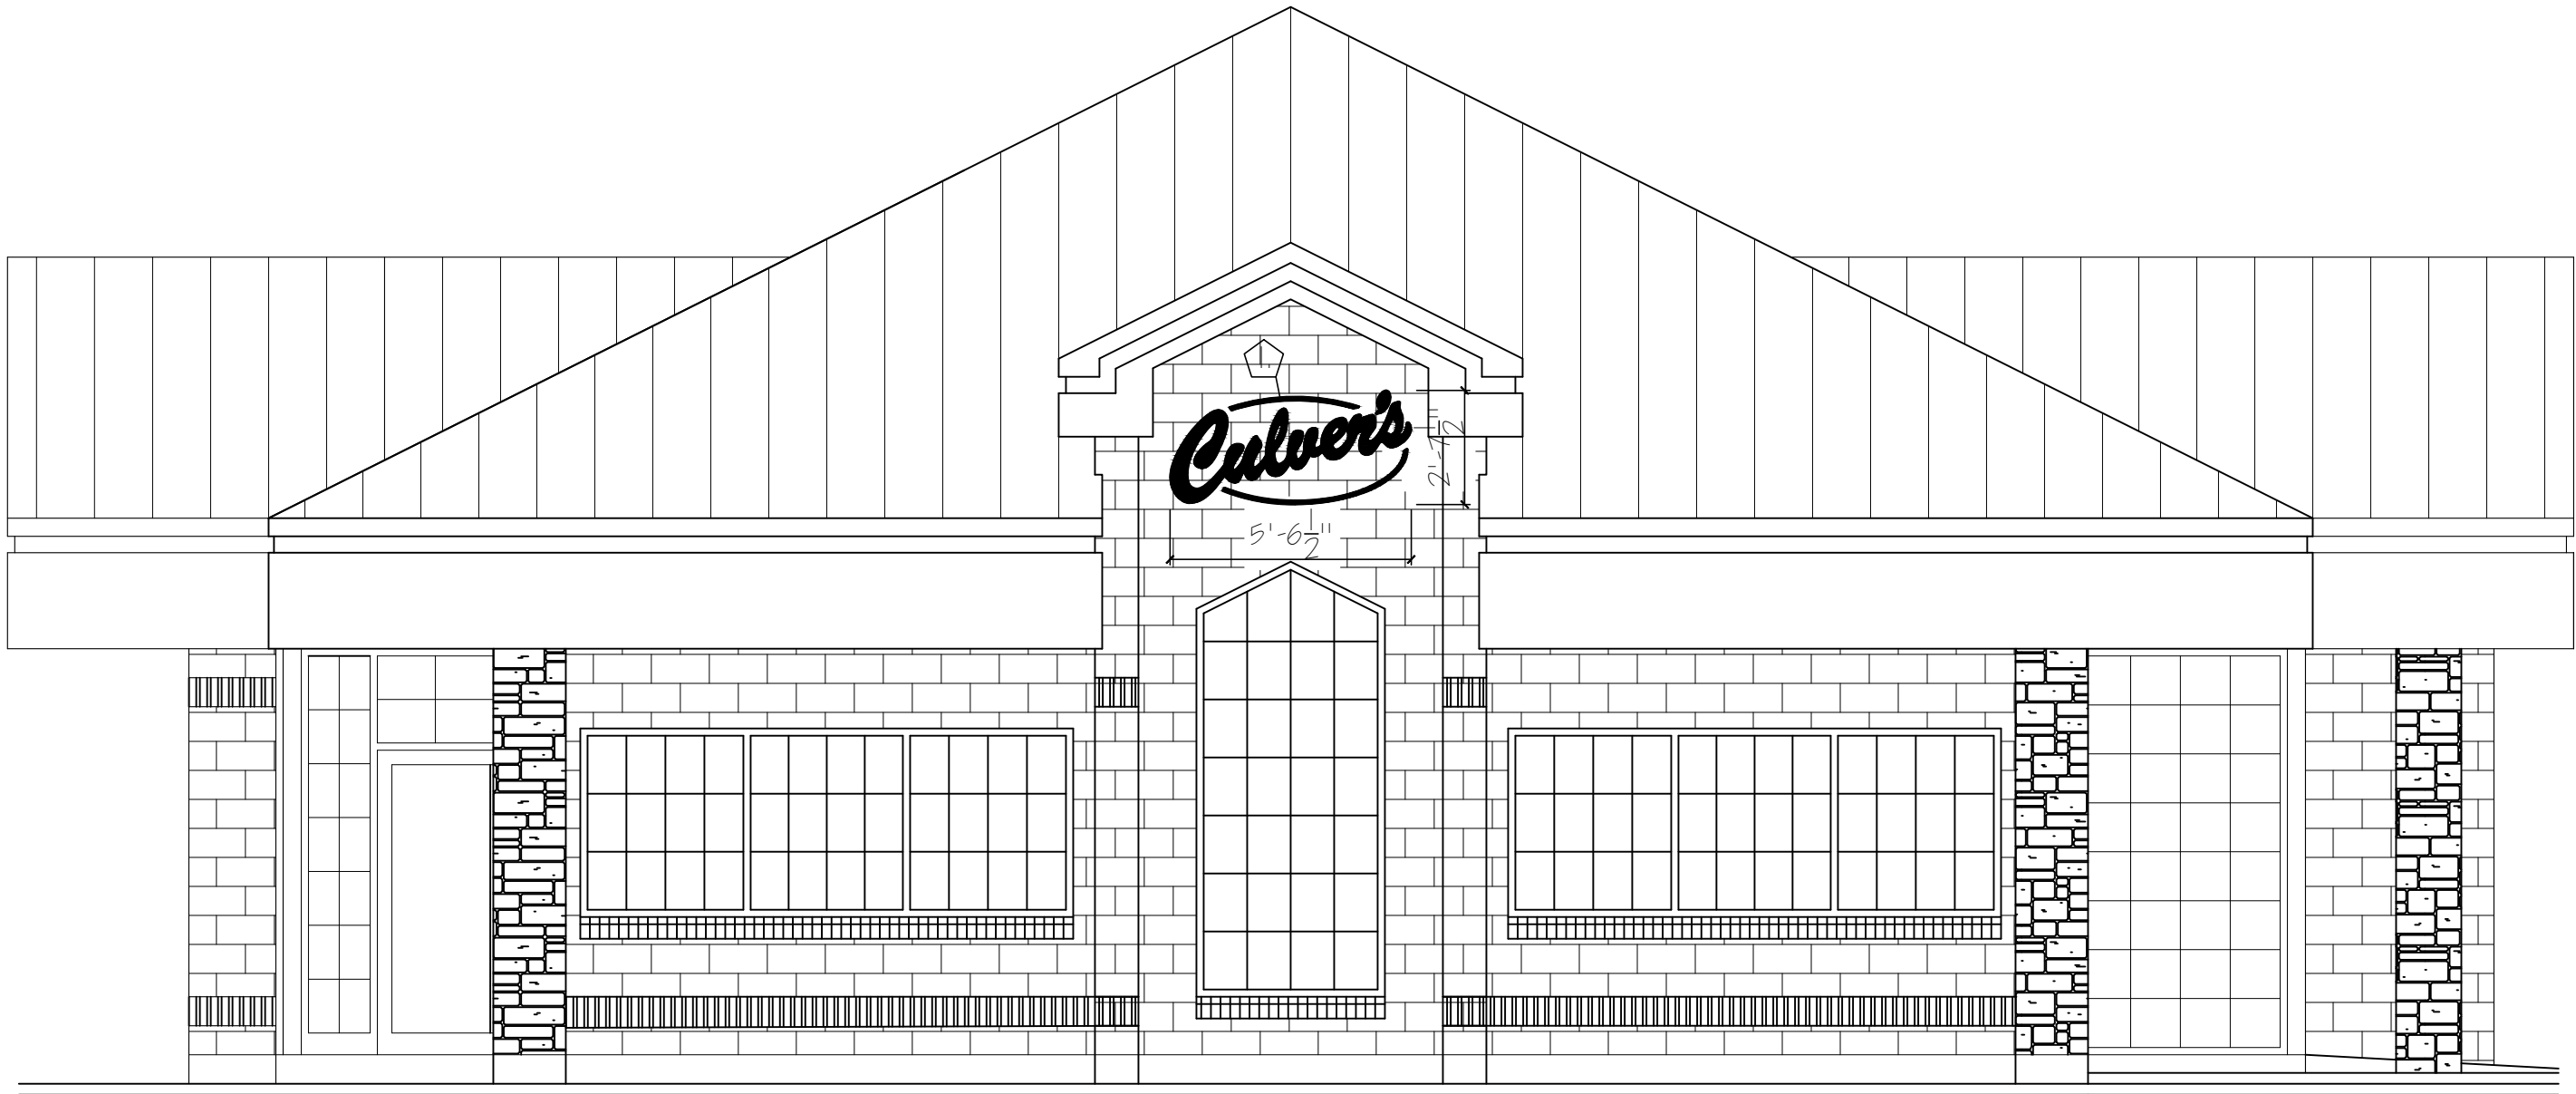

ELEV. - FRONT
SCALE: 1/4" = 1'-0"

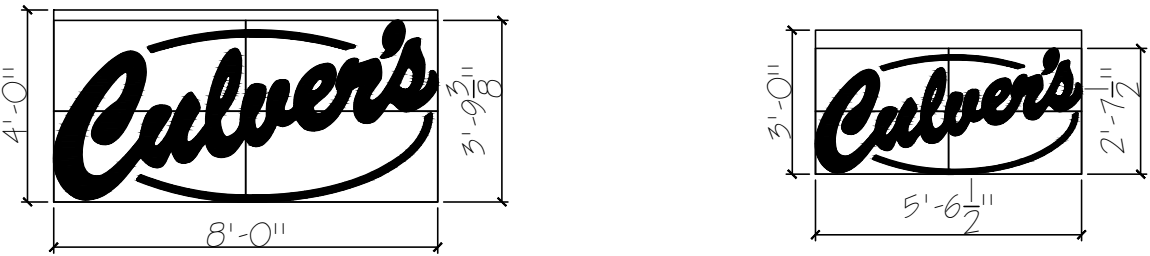

GENERAL NOTES:

1. THE EXTERIOR REFRESH SCOPE OF WORK DOCUMENT IS TO BE USED IN CONJUNCTION WITH CFS ISSUED EXTERIOR ELEVATIONS.
2. CFS DOES NOT GUARANTEE THE AVAILABILITY OF SELECTED PRODUCTS.
3. GC TO FIELD VERIFY DIMENSIONS PRIOR TO ORDERING MATERIALS.
4. IT IS THE GENERAL CONTRACTOR'S RESPONSIBILITY TO COORDINATE THE REMOVAL, DELIVERY, AND INSTALLATION OF ALL MATERIALS AND FINISHES UNLESS NOTED OTHERWISE.
5. IT IS THE GENERAL CONTRACTOR'S RESPONSIBILITY TO COORDINATE INSTALLATION OF MATERIALS WHEN THE TEMPERATURES AND DEW POINTS FALL WITHIN THE MANUFACTURE'S RECOMMENDATIONS FOR INSTALLATION.
6. ANY AREAS RECEIVING NEW MATERIALS MUST BE CLEANED PER THE MANUFACTURER'S RECOMMENDATIONS PRIOR TO INSTALL.
7. EXTERIOR BUILDING SIGNAGE AND INSTALLATION IS OWNER DIRECT PURCHASE FROM CFS APPROVED SIGNAGE PROVIDER.

KEYED NOTES:

- 1 NEW BUILDING SIGNS, GC TO COORDINATE ELECTRICAL



ELEV. - RIGHT SIDE
SCALE: 1/4" = 1'-0"

WARNING: These plans are for the exclusive use of Culver Franchising System, LLC. and authorized franchise holders only. No part of these plans or the design they represent may be duplicated or reproduced without permission of Culver Franchising System, LLC

Date	Revision	By


Culver Franchising System, LLC
1240 Water Street
Prairie du Sac, WI 53578
608-643-7980

CULVER FRANCHISING SYSTEM, LLC
REIMAGE 2027
CULVER'S OF SHAKOPEE, MN #0131


Sheet Contents
EXTERIOR
ELEV'S

Project No.
Shakopee, MN #0131
Drawn By:
E. ROCKWEILER
Date:
06/12/26

Sheet
A-3.0

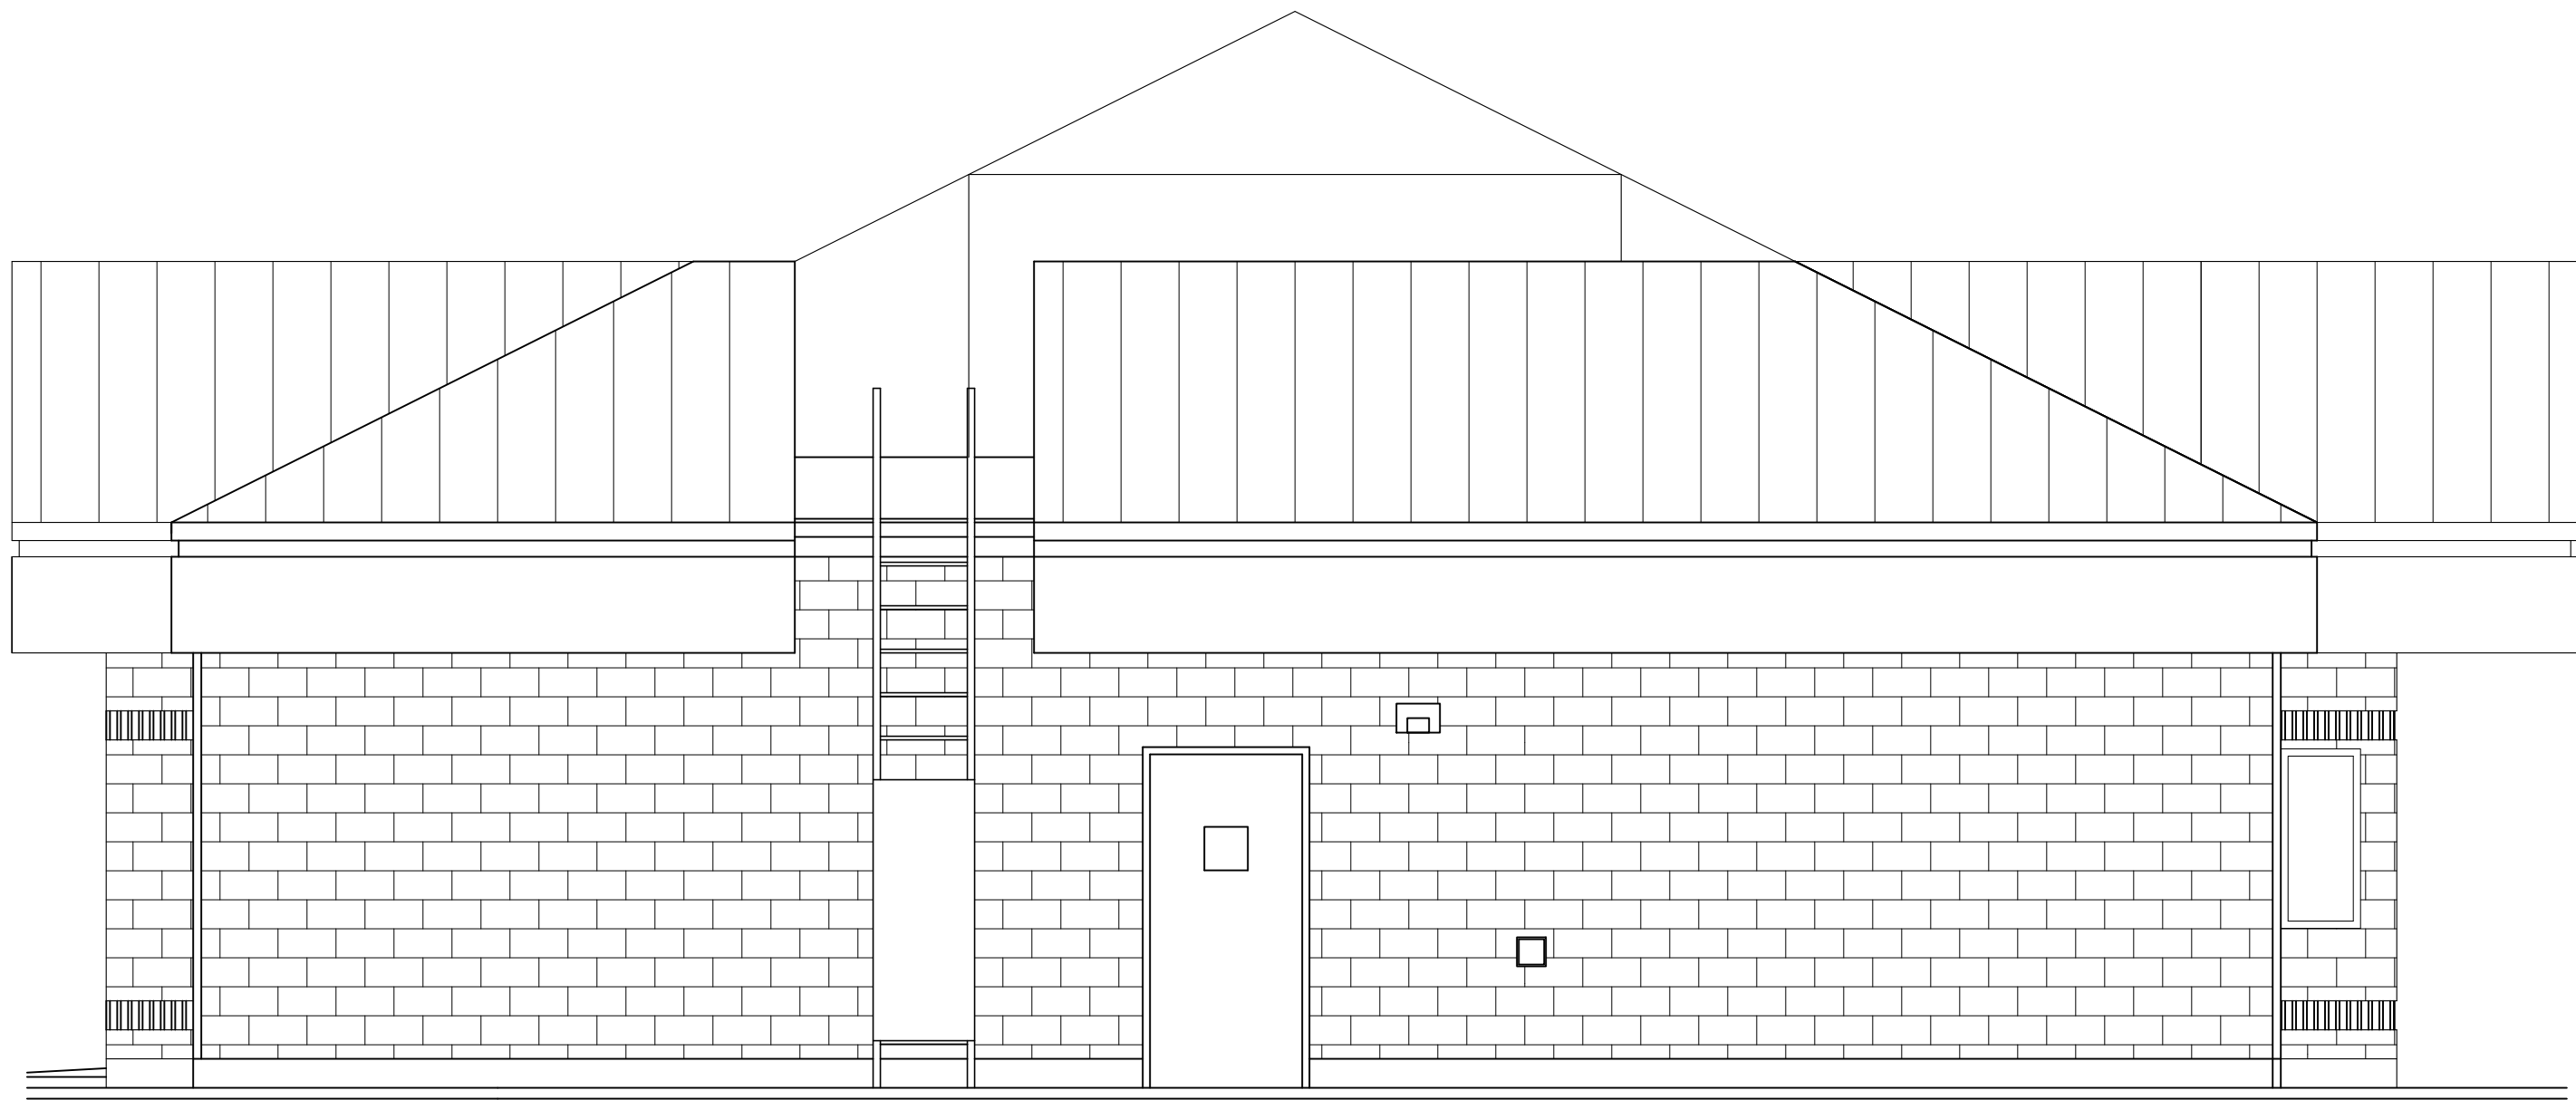

ELEV. - REAR
SCALE: 1/4" = 1'-0"

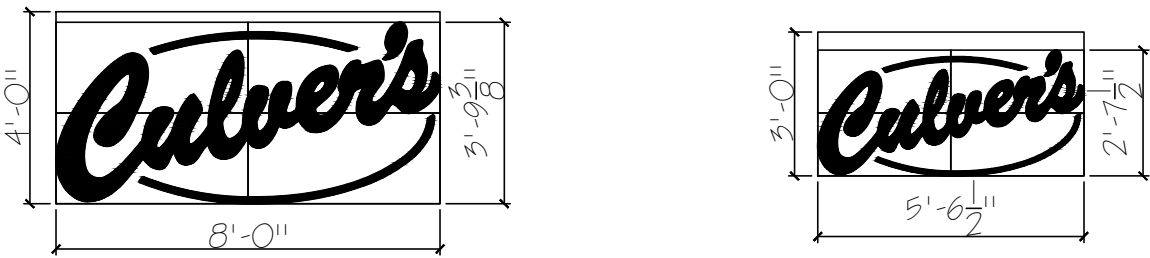

- GENERAL NOTES:
1. THE EXTERIOR REFRESH SCOPE OF WORK DOCUMENT IS TO BE USED IN CONJUNCTION WITH CFS ISSUED EXTERIOR ELEVATIONS.
 2. CFS DOES NOT GUARANTEE THE AVAILABILITY OF SELECTED PRODUCTS.
 3. GC TO FIELD VERIFY DIMENSIONS PRIOR TO ORDERING MATERIALS.
 4. IT IS THE GENERAL CONTRACTOR'S RESPONSIBILITY TO COORDINATE THE REMOVAL, DELIVERY, AND INSTALLATION OF ALL MATERIALS AND FINISHES UNLESS NOTED OTHERWISE.
 5. IT IS THE GENERAL CONTRACTOR'S RESPONSIBILITY TO COORDINATE INSTALLATION OF MATERIALS WHEN THE TEMPERATURES AND DEW POINTS FALL WITHIN THE MANUFACTURE'S RECOMMENDATIONS FOR INSTALLATION.
 6. ANY AREAS RECEIVING NEW MATERIALS MUST BE CLEANED PER THE MANUFACTURER'S RECOMMENDATIONS PRIOR TO INSTALL.
 7. EXTERIOR BUILDING SIGNAGE AND INSTALLATION IS OWNER DIRECT PURCHASE FROM CFS APPROVED SIGNAGE PROVIDER.

- KEYED NOTES:
- 1 NEW BUILDING SIGNS, GC TO COORDINATE ELECTRICAL



ELEV. - LEFT SIDE
SCALE: 1/4" = 1'-0"

WARNING: These plans are for the exclusive use of Culver Franchising System, LLC and authorized franchise holders only. No part of these plans or the design they represent may be duplicated or reproduced without permission of Culver Franchising System, LLC

Date	Revision	By

Culver Franchising System, LLC
1240 Water Street
Prairie du Sac, WI 53578
608-643-7980


CULVER FRANCHISING SYSTEM, LLC
REIMAGE 2027
CULVER'S OF SHAKOPEE, MN #0131


Sheet Contents
EXTERIOR ELEV'S
Project No. Shakopee, MN #0131
Drawn By: E. ROCKWEILER
Date: 06/12/26


Sheet
A-3.1

GENERAL NOTES:


- THIS FLOOR PLAN HAS NOT BEEN FIELD VERIFIED.
- UNLESS NOTED OTHERWISE, DIMENSIONS SHOWN ARE FACE OF FRAMING TO FACE OF FRAMING FOR NEW CONSTRUCTION. DIMENSIONS AT EXISTING CONSTRUCTIONS ARE FROM GYP. BOARD OR FINISH SURFACE.
- PROVIDE CONDUIT, WIRE AND TERMINATIONS FOR ETHERNET FOR DIGITAL MENU BOARDS. VERIFY LOCATIONS WITH OWNER. MAIN PATCH PANEL LOCATED IN OFFICE.
- REMOVE ALL CROWN MOLDING AND PENDANT FIXTURES. PATCH AND REPAIR SOFFIT AND CEILING GRID AS NEEDED.
- COORDINATE ALL PENDANT LOCATIONS IN DINING ROOM TO BE CENTERED OVER TABLES AT 6'-0" A.F.F.
- E.C. TO ENSURE PATH OF EGRESS IS MAINTAINED WHEN RELOCATING EXISTING FIXTURES.
- REPLACE EXISTING LAY-IN FIXTURES THROUGHOUT FRONT OF HOUSE. E.C. TO VERIFY QUANTITIES AND LOCATIONS. SEE LIGHTING SCHEDULE FOR SPECS.
- REPLACE ALL EMERGENCY EXIT FIXTURES IN FRONT OF HOUSE WITH NEW. REFER TO LIGHTING SCHEDULE FOR SPECIFICATIONS.
- E.C. TO VERIFY EXISTING EMERGENCY FIXTURE QUANTITIES, SIZES & LOCATIONS FOR REPLACEMENT. MUST MAINTAIN PATH OF EGRESS.
- EMERGENCY LIGHT LEVELS TO BE VERIFIED BY LOCAL CODES. IF ADDITIONAL EMERGENCY LIGHTS ARE REQUIRED CONTACT CRESCENT ELECTRIC.

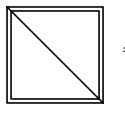
 = 2'x2' RETURN AIR GRILLE
RAYMON
F&C-121 RETURN
GRID MOUNTED

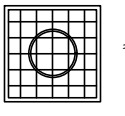
 = 2' x 2' LAY-IN PERFORATED DIFFUSER
RAYMON
RPR PERFORATED NON DIRECTIONAL
SUPPLY
GRID MOUNTED

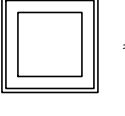 = 2' x 2' LAY-IN DIFFUSER
RAYMON
PR2 SUPPLY
GRID MOUNTED

NATIONAL ACCOUNTS PROGRAM:
ALL HVAC FOR CULVER'S PROJECTS TO BE
PURCHASED ONLY FROM THE NATIONAL
ACCOUNTS SUPPLIER CONTACT:
HUNZICKER LLC
MARIE WILSON
(608) 845-9551
marie@hunzickertllc.com

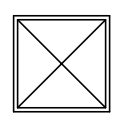 2 x 2 LED FLAT PANEL
LITHONIA
CPX 2x2 3200LM 80CRI 35K 5W. MINIO ZT
OR
2 x 2 LED FLAT PANEL - EMERGENCY
LITHONIA
CPX 2x2 3200LM 80CRI 35K 5W. MINIO ZT
CONNECTED TO INVERTER BATTERY BACK UP
OR
2 x 2 LED FLAT PANEL - 24 HRS
LITHONIA
CPX 2x2 3200LM 80CRI 35K 5W. MINIO ZT
CONNECTED TO INVERTER BATTERY BACK UP

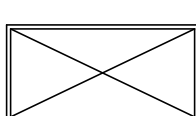 2 x 4 LED FLAT PANEL
LITHONIA
CPX 2x4 5000LM 80CRI 35K 5W. MINIO ZT
MVOLT
OR
2 x 4 LED FLAT PANEL - 24 HRS
LITHONIA
CPX 2x4 5000LM 80CRI 35K 5W. MINIO ZT
MVOLT
CONNECTED TO INVERTER BATTERY BACK UP

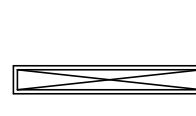 LBLA SURFACE MOUNTED
LITHONIA
5000LM 80CRI 35K MINIO GZT
MVOLT


 WAFER LED DOWNLIGHT
JUNO
WF6 5WWS 90CRI BN M6
OR
WAFER LED DOWNLIGHT - EMERGENCY
JUNO
WF6 5WWS 90CRI BN M6
CONNECTED TO INVERTER BATTERY BACK UP
OR
WAFER LED DOWNLIGHT - 24HRS
JUNO
WF6 5WWS 90CRI BN M6
CONNECTED TO INVERTER BATTERY BACK UP


 WAFER DOWNLIGHT - GIMBAL
JUNO
WF4 ADJ 5WWS 90CRI BN M6

 FLUSH MOUNT FIXTURE
LITHONIA VERSI LITE LED
FNMV-7830 LED


 PENDANT FIXTURE
SEE INTERIOR FINISH PACKET FOR SPECIFICATION
CONTROL W/ DIMMER SWITCH


 EXIT LIGHT
LITHONIA
EXR LED EL NABC

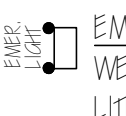 EMERGENCY LIGHT HEAD
WEATHER PROOF
LITHONIA
APB DEL DDBXD

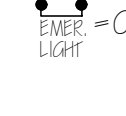 EVER LIGHT
= CEILING MOUNTED EMERGENCY LIGHT

 SOFFIT STRIP LIGHT - WET LOCATION
LITHONIA
CSVT LAB 4000LM MVOLT 5WWS 80CRI

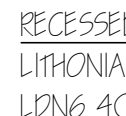 RECESSED CAN - WET LOCATION
LITHONIA
LDN6 40/15 LOGAR L5 MVOLT GZIO WL

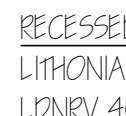 RECESSED CAN RETRO-FIT - WET LOCATION
LITHONIA
LDNRY 40/15 LR AR L5 MVOLT GZIO WL

 EXTERIOR WALL SCONCE
RA CD34FA6W-36-708-ZC
(UP / DOWN SWITCHABLE IF REQUIRED BY LOCAL
CODES)

 STONE BOLLARD LAMP
GE LIGHTING
LED12DPA21 / B50PE

 LED BOLLARD
LITHONIA
KBC8 LED
16C 700 40K 5W MVOLT DDBXD

DOCUMENTS TO VERIFY SCOPE OF WORK:

NATIONAL ACCOUNTS PROGRAM:
ALL LIGHT FIXTURES, LIGHTING CONTROLS, AND DISTRIBUTION
GEAR FOR CULVER'S PROJECTS TO BE PURCHASED ONLY
FROM THE NATIONAL ACCOUNTS SUPPLIER. CRESCENT
ELECTRIC SUPPLY CO. IN MADISON, WI. CONTACT DANA
MCCOOK AT CULVERS@CESCO.COM OR 1-608-241-2882.
FOR PRICING AND SUBMITTALS.

KEYED NOTES:





- SOFFIT TO BE REPAINTED, VERTICAL FACE TO BE PT-1,
REVEAL TO BE PT-1, HORIZONTAL FACE TO BE PT-2
- BULKHEAD TO BE REFINISHED, VERTICAL FACE TO BE PT-1,
HORIZONTAL FACE AND DT VERTICAL FACE TO BE TILE
PATTERN 1
- BULKHEAD TO BE REFINISHED, ALL SIDES TO BE TILE
PATTERN 1
- RELOCATE MEP IN THESE LOCATIONS TO ACCOMMODATE
ADDITION/REMOVAL OF FULL HEIGHT WALLS
- BULKHEAD TO BE REFINISHED, ALL SIDES TO BE PT-1
- EXISTING BULKHEAD FROM PUNCHED OPENING TO REMAIN,
EXTEND TO NEW CORNER OF FEATURE WALL, ALL SIDES TO
BE VWC-2
- EXISTING AIR RETURN GRATES TO BE REPLACED WITH NEW,
SEE HVAC LEGEND FOR SPECIFICATION.
- EXISTING 4-WAY SUPPLY DIFFUSERS TO BE REPLACED WITH
PERFORATED DIFFUSERS, SEE HVAC LEGEND FOR
SPECIFICATION.
- REPLACE EXISTING PENDANTS WITH NEW, MATCH EXISTING
LOCATIONS
- PATCH IN NEW CLG TILE AS NEEDED TO MATCH
SURROUNDING. PATCH CEILING TILE, GRID AND COMPASSO
AS NEEDED FROM WALL REMOVAL AND ADDITION
- REPLACE EXISTING LAY-IN AND SURFACE MOUNTED FIXTURES
WITH LED, SEE LEGEND FOR SPECIFICATION
- REPLACE VENT COVER AT BULKHEAD
- REPLACE GYP BOARD CLG AS NEEDED, VERIFY SCOPE WITH
OWNER.

CEILING LEGEND:

-  = SPRINKLER
-  = SPEAKER
-  = WIFI ROUTER
-  = CAMERA
-  = JUNCTION BOX - DIRECT
CONNECTION

-  = INT. DATA FOR DIGITAL MENU
BOARDS (# = NUMBER OF LINES,
HOME RUN ALL TO OFFICE)
-  = EXT. DATA FOR DIGITAL MENU
BOARDS (# EQUALS NUMBER OF
LINES, HOME RUN ALL TO OFFICE)
-  = DATA HOME RUN LOCATION

CEILING KEY:

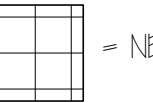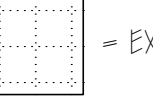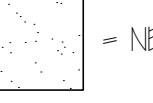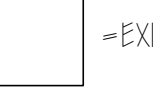-  = NEW CEILING TILE AND/ OR GRID
-  = EXISTING CEILING TILE / GRID - MEP WORK ONLY
-  = NEW GYP. BD. CEILING
-  = EXISTING GYP. BD. CEILING OR NO WORK - SEE NOTE ON PLAN

CEILING TYPE:


TYPE 1 SCS CLG: GRID: DONN DX SYSTEM - COLOR TO MATCH TILE
TILE: 2x2 USG "PROST CLIMA-PLUS" SANDSTONE - 090
TRIM: 6" COMPASSO COLOR "SILVER SATIN - 002"

TYPE 2 SCS CLG: GRID: DONN DX SYSTEM - COLOR TO MATCH TILE
TILE: 2x2 USG "PROST CLIMA-PLUS" MANILA - 246
TRIM: 6" COMPASSO COLOR "SILVER SATIN - 002"


TYPE 3 SCS CLG: GRID: DONN DXA SYSTEM - FLAT WHITE
TILE: 2x2 USG VINYL-FACED GYPSUM - #090 WHITE

TYPE 4 SCS CLG: GRID: DONN DXA SYSTEM - FLAT WHITE
TILE: 2x4 USG VINYL-FACED GYPSUM - #090 WHITE

TYPE 5 SCS CLG: GRID: DONN DX SYSTEM - COLOR TO MATCH TILE
TILE: 2x2 USG "PROST CLIMA-PLUS" FLAT BLACK - 205

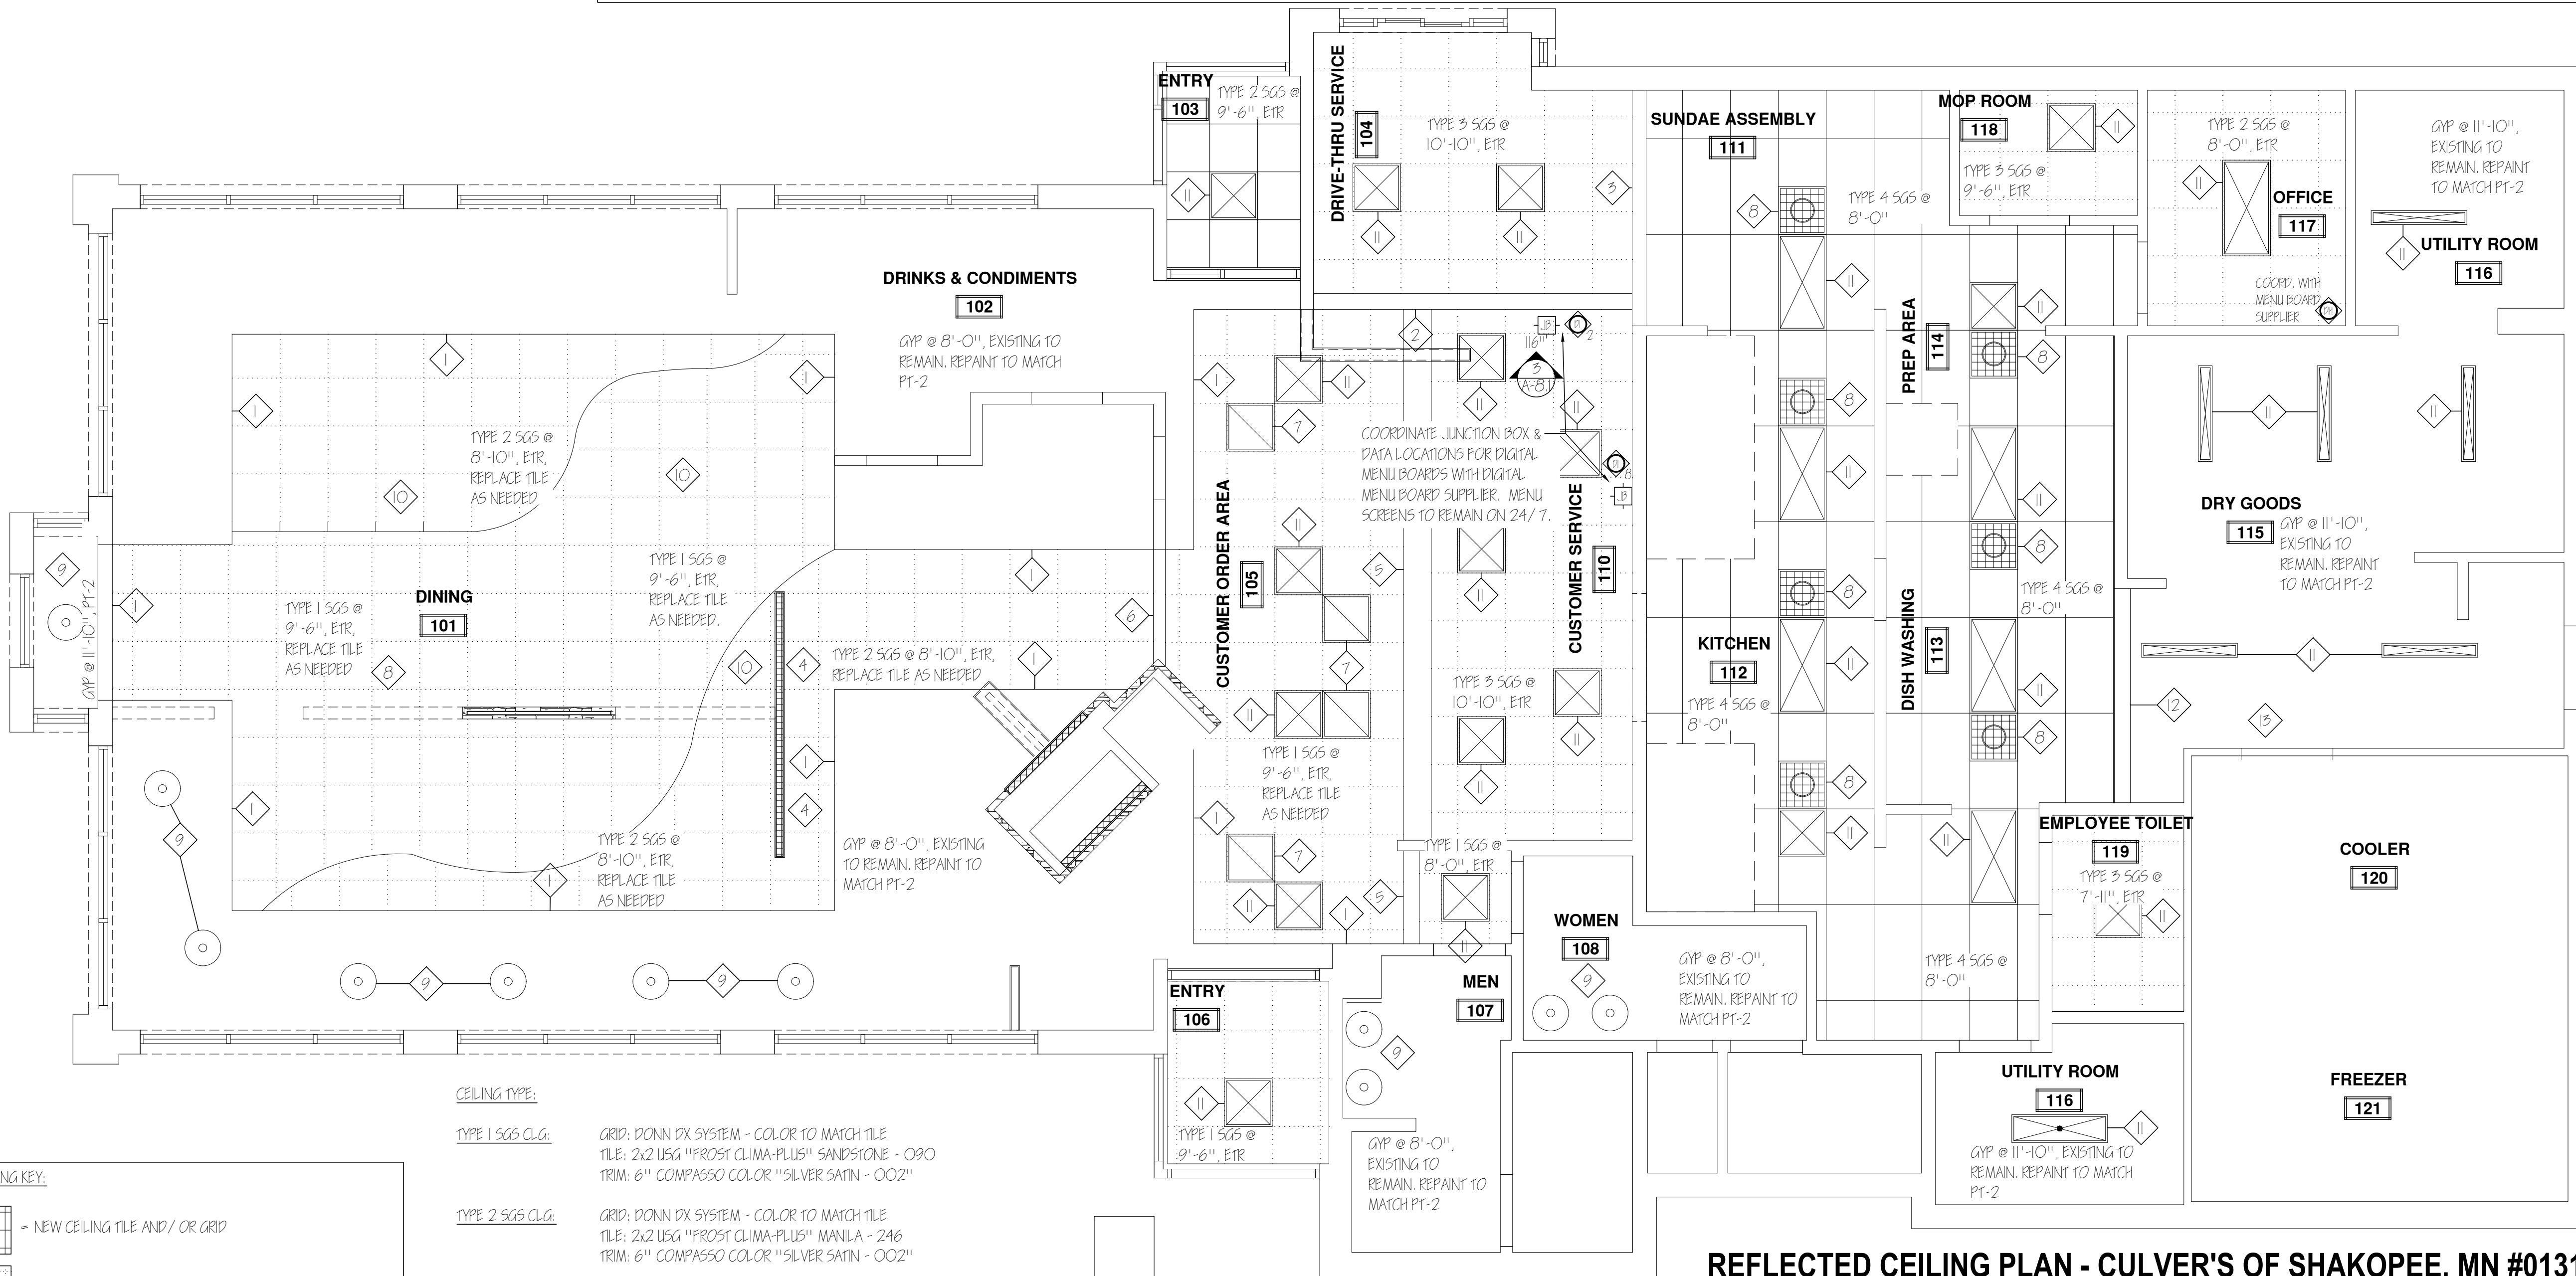

REFLECTED CEILING PLAN - CULVER'S OF SHAKOPEE, MN #0131
SCALE: 1/4" = 1'-0"

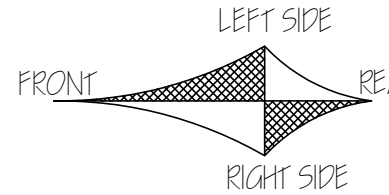

WARNING: These plans are for the exclusive use of Culver Franchising System, LLC and authorized franchise holders only. No part of these plans or the design they represent may be duplicated or reproduced without permission of Culver Franchising System, LLC

CULVER FRANCHISING SYSTEM, LLC
REIMAGE 2027
CULVER'S OF SHAKOPEE, MN #0131

Sheet Contents
REFLECTED
CEILING PLAN

Project No.
Shakopee, MN #0131
Drawn By:
E. ROCKWEILER
Date:
06/12/26

Sheet
A-5

Culver Franchising
System, LLC
1240 Water Street
Prairie du Sac, WI 53578
608-643-7980




By
Date
Revision

FINISH MATERIALS - BUILDING MATERIALS	
CARPET:	
OPT 2: Tardus, 6' Powerbond, Style: Corallary 11577, Color: Universal 59407	
FLOOR TILE:	
WATERPROOFING MEMBRANE:	
Custom Building Products, Red Gard Waterproofing and Crack Prevention Membrane	
SETTING MATERIAL:	
Custom Building Products, Pro-lite Medium Bed Tile and Stone Mortar RS	
GROUT:	
Standard: Custom Building Products, Prism Sure Color, Color: 540 Truffle	
Epoxy: Custom Building Products, CEG Lite 100% Solids Epoxy Grout, Color: 540 Truffle	
TILE 1:	
Datatile, Chord, Size: 12" x 24", Pattern: Running Bond 55% slipper	
Color: CH29 Rhythm Brown	
ACRYLIC FLOORING:	
RES-TEK:	
Hybrid MAC-Guard/ PUR-Guard HD-5L Colored Quartz Flooring System, MMA top coats w/ 6" MAC-Guard Cove Base, Color: CQ Blend No.1 (Gray)	
WALL TILE PATTERNS:	
Verify tile pattern selections with interior finish selection document. See sheet A-8 for tile pattern elevations	
TILE PRN 1:	
TILE 3	
TILE PRN 2:	
TILE 5; ACCENT: TILE 5	
WALL TILE:	
GROUT:	
Standard: Custom Building Products, Prism Sure Color, Color: 183 Chateau	
TILE 3:	
Datatile, Skybridge, Size: 10" X 14" Color: 5Y96 Beige	
TILE 5:	
Datatile, Crystal Shores, Size: 12" X 12", cut to 6" X 12"	
Color: CS95 Sapphire Lagoon	
WALL BASE:	
VINYL BASE:	
Johnsontite, Traditional Vinyl Toe 6", Color: 63 Bunt Umber	
ACRYLIC BASE:	
Res-Tek MAC-Guard 6" Cove Base, Color to match floor spec.	
TILE BS 1:	
Datatile, Chord, Size: 12" X 24", cut to 6" X 24", Color: CH29 Rhythm Brown	
TRANSITION STRIP:	
TR-1:	
Schluter Systems Inc, Reno-TK AET100, Satin Anodized Aluminum	
TR-2:	
Schluter Systems Inc, Jolly J100AE OR JBOAE, Satin Anodized Aluminum	
TR-3:	
Schluter Systems Inc, Jolly Outside Corner EV/ J100AE OR JBOAE	
TR-4:	
Schluter Systems Inc, Dilex-AHK, Cove Base AHK1500AE, Satin Anodized Aluminum	
TR-5:	
Schluter Systems Inc, Dilex-AHK, Cove Base Outside Corner E90Q/ AHK 15/ AE	
TR-6:	
Schluter Systems Inc, Dilex-AHK, Cove Base Inside Corner 190/ AHK 15/ AE	
TR-7:	
Schluter Systems Inc, Dilex-AHK, End Cap E/ AHK15/ AE	
TR-8:	
Schluter Systems Inc, Dilex-AHKA, Satin Anodized Aluminum, installer to verify size	
TR-9:	
Schluter Systems Inc, Dilex-AHKA, Cove Base Outside Corner E90/ AHKA/ AE	
TR-10:	
Schluter Systems Inc, Dilex-AHKA, Cove Base Inside Corner 190/ AHKA/ AE	
TR-11:	
Schluter Systems Inc, Dilex-AHKA, End Cap EL/ AHKA/ AE or ER/ AHKA/ AE	
TR-12:	
Schluter Systems Inc, Schlote-STEP, Satin Anodized Aluminum, installer to verify size	
TR-13:	
Zinc Transition by Res-Tek	
VINYL WALLCOVERING:	
VWC-1:	
Momentum, Style: NA-11-CUL9 Omni Linen River Rock	
VWC-2:	
Momentum, Style: NA-31-CUL10 Lithic Texture - Admiral	
VWC-3:	
Momentum, Style: DLP-OA03 VESTIBULE Custom Printed Wallcovering Mural	
VWC-4:	
Momentum, Style: DLP-OA03 DINING Custom Printed Wallcovering Mural	
PAINT:	
See interior finish selection packet for coating specifications	
PT-1:	
Sherwin Williams, SW7015 Repose Gray	
PT-2:	
Sherwin Williams, SW7009 Pearly White	
WAINSCOTING:	
WNSCT:	
Marlite Allure ACM, Color: Pionite Appears Likeatre WP115, Size: 4' x 10' Cross-Grained	
Outside Corner - AP-34; 3" x 3" Aluminum Finish	
Inside Corner - AP-32; Aluminum Finish	
Slim Division Bar - AP-101; Aluminum Finish	
APPLIED TRIM:	
See sheet A-8 for sizes and locations	
FIBER REINFORCED PLASTIC PANELS:	
FRP:	
Marlite, 4' x 10' Pebbled White	
STAINLESS STEEL PANELS:	
S/S:	
304 Stainless Steel, 18 GA, #4 Finish	
INTERIOR STONE:	
STONE 1:	
Westlake Royal Stone: Cultured Stone - Country LedgeStone - Echo Ridge	
LAMINATES:	
LAMINATE 1:	
Wilsonart 10776-60 Kensington Maple	
LAMINATE 2:	
Pionite AG611 Suede Graycave of the Atlantic (Table Top Option)	
SOLID SURFACE:	
SS-1:	
Wilsonart Beige Tempest 1550 TM	
Note:	
1LT RM Lavatory Bowls to be Wilsonart Antique White	
UPHOLSTERY:	
UPH-1:	
Momentum, Vanguard, Color:Pebble	
VINYL:	
Nauquahde Spirit Millennium, Color: US 429 Graphite	


- KEYED NOTES:
- 1 PUNCHED OPENINGS, FROSTED TEMPERED GLASS AT DRINKS & CONDIMENTS AND CUSTOMER ORDER AREA ONLY. SEE DETAIL 5/ A-8.
 - 2 GC TO PROVIDE CONCRETE CURBS, COORDINATE HEIGHTS, SIZES AND DRAIN LOCATIONS w/ FOODSERVICE EQUIPMENT SUPPLIER, CURB TO RECEIVE TILE BASE OR ACRYLIC BASE TO COORDINATE WITH FLOOR FINISH IN THAT AREA.
 - 3 PIN LETTER SIGN, BY SIGNAGE COMPANY, CENTER OF SIGN TO BE AT 6'-2" AFF.
 - 4 TILE BASE TO BE INSTALLED FLUSH w/ FACE OF INTERIOR STONE.
 - 5 NO RES-TEK AT CUSTARD MACHINE.
 - 6 GC TO VERIFY w/ TILE CONTRACTOR WHERE WATERPROOFING MEMBRANE SHOULD START AND STOP.
 - 7 TR-13 AT FLOOR TILE TO ACRYLIC FLOORING TRANSITION.
 - 8 GC TO INSTALL RES-TEK IN THESE AREAS. INSTALL ADDITIONAL FLOOR DRAINS AS NEEDED TO ACCOMMODATE. EXISTING FLOOR DRAINS SHOWN, ADD NEW AS NEEDED.

ROOM FINISH SCHEDULE										
NO.	ROOM TYPE	LEFT SIDE	FRONT	RIGHT SIDE	REAR	FLOOR	FLOOR BASE	CEILING MATERIAL	CEILING FINISH	NOTES
101	DINING ROOM	WNSCT, VWC-1	WNSCT, VWC-1	WNSCT, VWC-1	WNSCT, VWC-2	CARPET & TILE 1	VINYL BASE	TYPE-1, TYPE-2, GYP	PT-1, PT-2	
102	DRINKS & CONDIMENTS	WNSCT, VWC-1	WNSCT, VWC-1	WNSCT, VWC-2	WNSCT, VWC-1	TILE 1	TILE BASE 1	GYP	PT-1, PT-2	
103	ENTRY	WNSCT, VWC-1	WNSCT, VWC-1	WNSCT, VWC-1	WNSCT, VWC-1	TILE 1	TILE BASE 1			
104	DRIVE THRU SERVICE	TILE PATTERN 1	TILE PATTERN 1	-	TILE PATTERN 1	RES-TEK	ACRYLIC		-	
105	CUSTOMER ORDER AREA	-	WNSCT, VWC-2	-	TILE PATTERN 1	TILE 1	TILE BASE 1	TYPE-1, GYP	PT-1, PT-2	
106	ENTRY	WNSCT, VWC-2	WNSCT, VWC-2	WNSCT, VWC-2	WNSCT, VWC-3	TILE 1	TILE BASE 1			
107	MEN	TILE PATTERN 2	TILE PATTERN 2	TILE PATTERN 2	TILE PATTERN 2	TILE 1	-	GYP	PT-2	
108	WOMEN	TILE PATTERN 2	TILE PATTERN 2	TILE PATTERN 2	TILE PATTERN 2	TILE 1	-	GYP	PT-2	
109	HALL	WNSCT, VWC-1	-	WNSCT, VWC-1	WNSCT, VWC-1	TILE 1	TILE BASE 1	TYPE-1	-	
110	CUSTOMER SERVICE	-	-	TILE PATTERN 1	TILE PATTERN 1	TILE 1	TILE BASE 1		-	
111	SUNDAE ASSEMBLY	TILE PATTERN 1	-	TILE PATTERN 1	TILE PATTERN 1	RES-TEK	ACRYLIC	TYPE-4	-	
112	KITCHEN	-	-	-	FRP	RES-TEK	ACRYLIC	TYPE-4	-	
113	DISHWASHING	-	-	-	-	RES-TEK	ACRYLIC	TYPE-4	-	
114	PREP	-	-	-	-	RES-TEK	ACRYLIC	TYPE-4	-	
115	DRY GOODS	-	-	-	-	RES-TEK	ACRYLIC	GYP, PT-2	GYP, PT-2	
116	UTILITY ROOM	-	-	-	-	RES-TEK	ACRYLIC	GYP, PT-2	GYP, PT-2	
117	OFFICE	-	-	-	-	-	-	-	-	
118	MOP ROOM	FRP	FRP	FRP	FRP	RES-TEK	ACRYLIC	-	-	
119	EMPLOYEE TOILET	-	-	-	-	RES-TEK	ACRYLIC	-	-	
120	COOLER	-	-	-	-	RES-TEK	-	-	-	
121	FREEZER	-	-	-	-	RES-TEK	-	-	-	

- GENERAL NOTES:
- SEE ADDITIONAL WALL FINISH INFORMATION/ TILE PATTERN ELEVATIONS ON SHEET A-8
 - SEE CEILING INFORMATION ON SHEET A-5
 - SEE INTERIOR SELECTIONS DOCUMENT FOR FINAL MATERIAL AND FINISH SELECTIONS & NATIONAL ACCOUNT REP INFORMATION. NATIONAL ACCOUNT REPS CAN ASSIST IN NATIONAL ACCOUNT MATERIAL PRICING.
 - BASE: 6" VINYL BASE ON CARPET, 6" TILE BASE ON TILE, 6" MAC-Guard BASE AT ACRYLIC FLOORING.
 - ALL CARPET TO TILE TRANSITIONS, INCLUDING CURVED TRANSITIONS TO BE TR-1
 - ALL WALL TILE/ TILE BASE TO FLOOR TILE TRANSITIONS TO BE TR-4 OR TR-8. SEE DETAIL 2/ A-6.
 - ALL OUTSIDE CORNER AND WALL TILE TO GYP BOARD TRANSITIONS TO BE TR-2. USE COORDINATING TRIM CAPS WHERE TRIM DOES NOT MEET CEILING.
 - GC TO VERIFY w/ TILE CONTRACTOR WHERE WATERPROOFING/ CRACK PREVENTION MEMBRANE IS NEEDED.
 - ALL WALL COVERINGS TO BE INSTALLED REVERSE HUNG, STARTING FIRST WITH THE VWC MURALS. REFER TO ADDITIONAL MURAL INSTALLATION NOTES ON A-7.
- FLOORING KEY:
- + + + = NEW CARPET
 - + + = NEW TILE 1
 - + = NEW RES-TEK
 - = EXISTING FLOORING TO REMAIN OR PATCH/ REPAIR ONLY

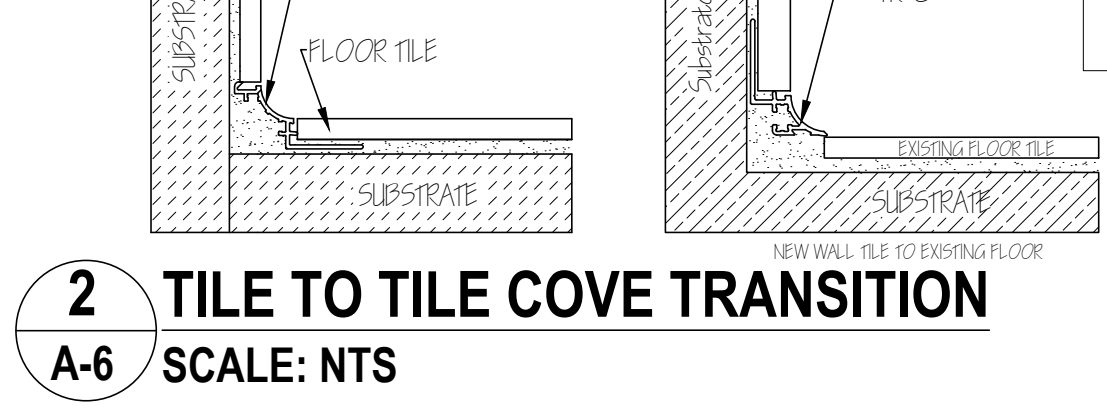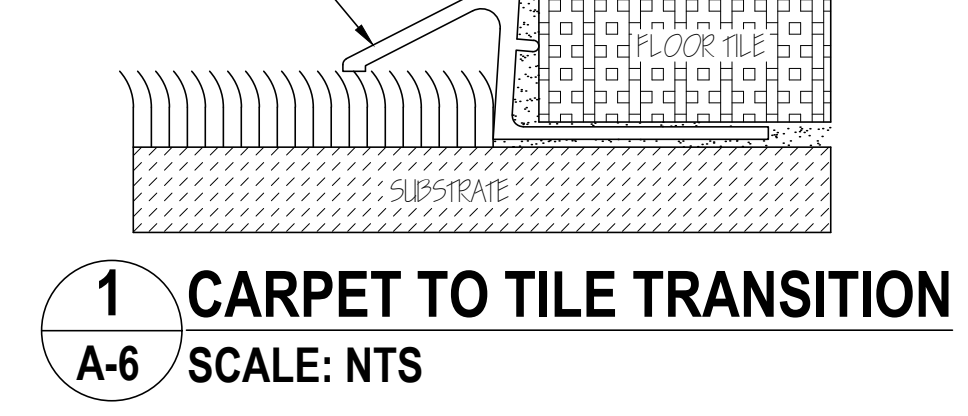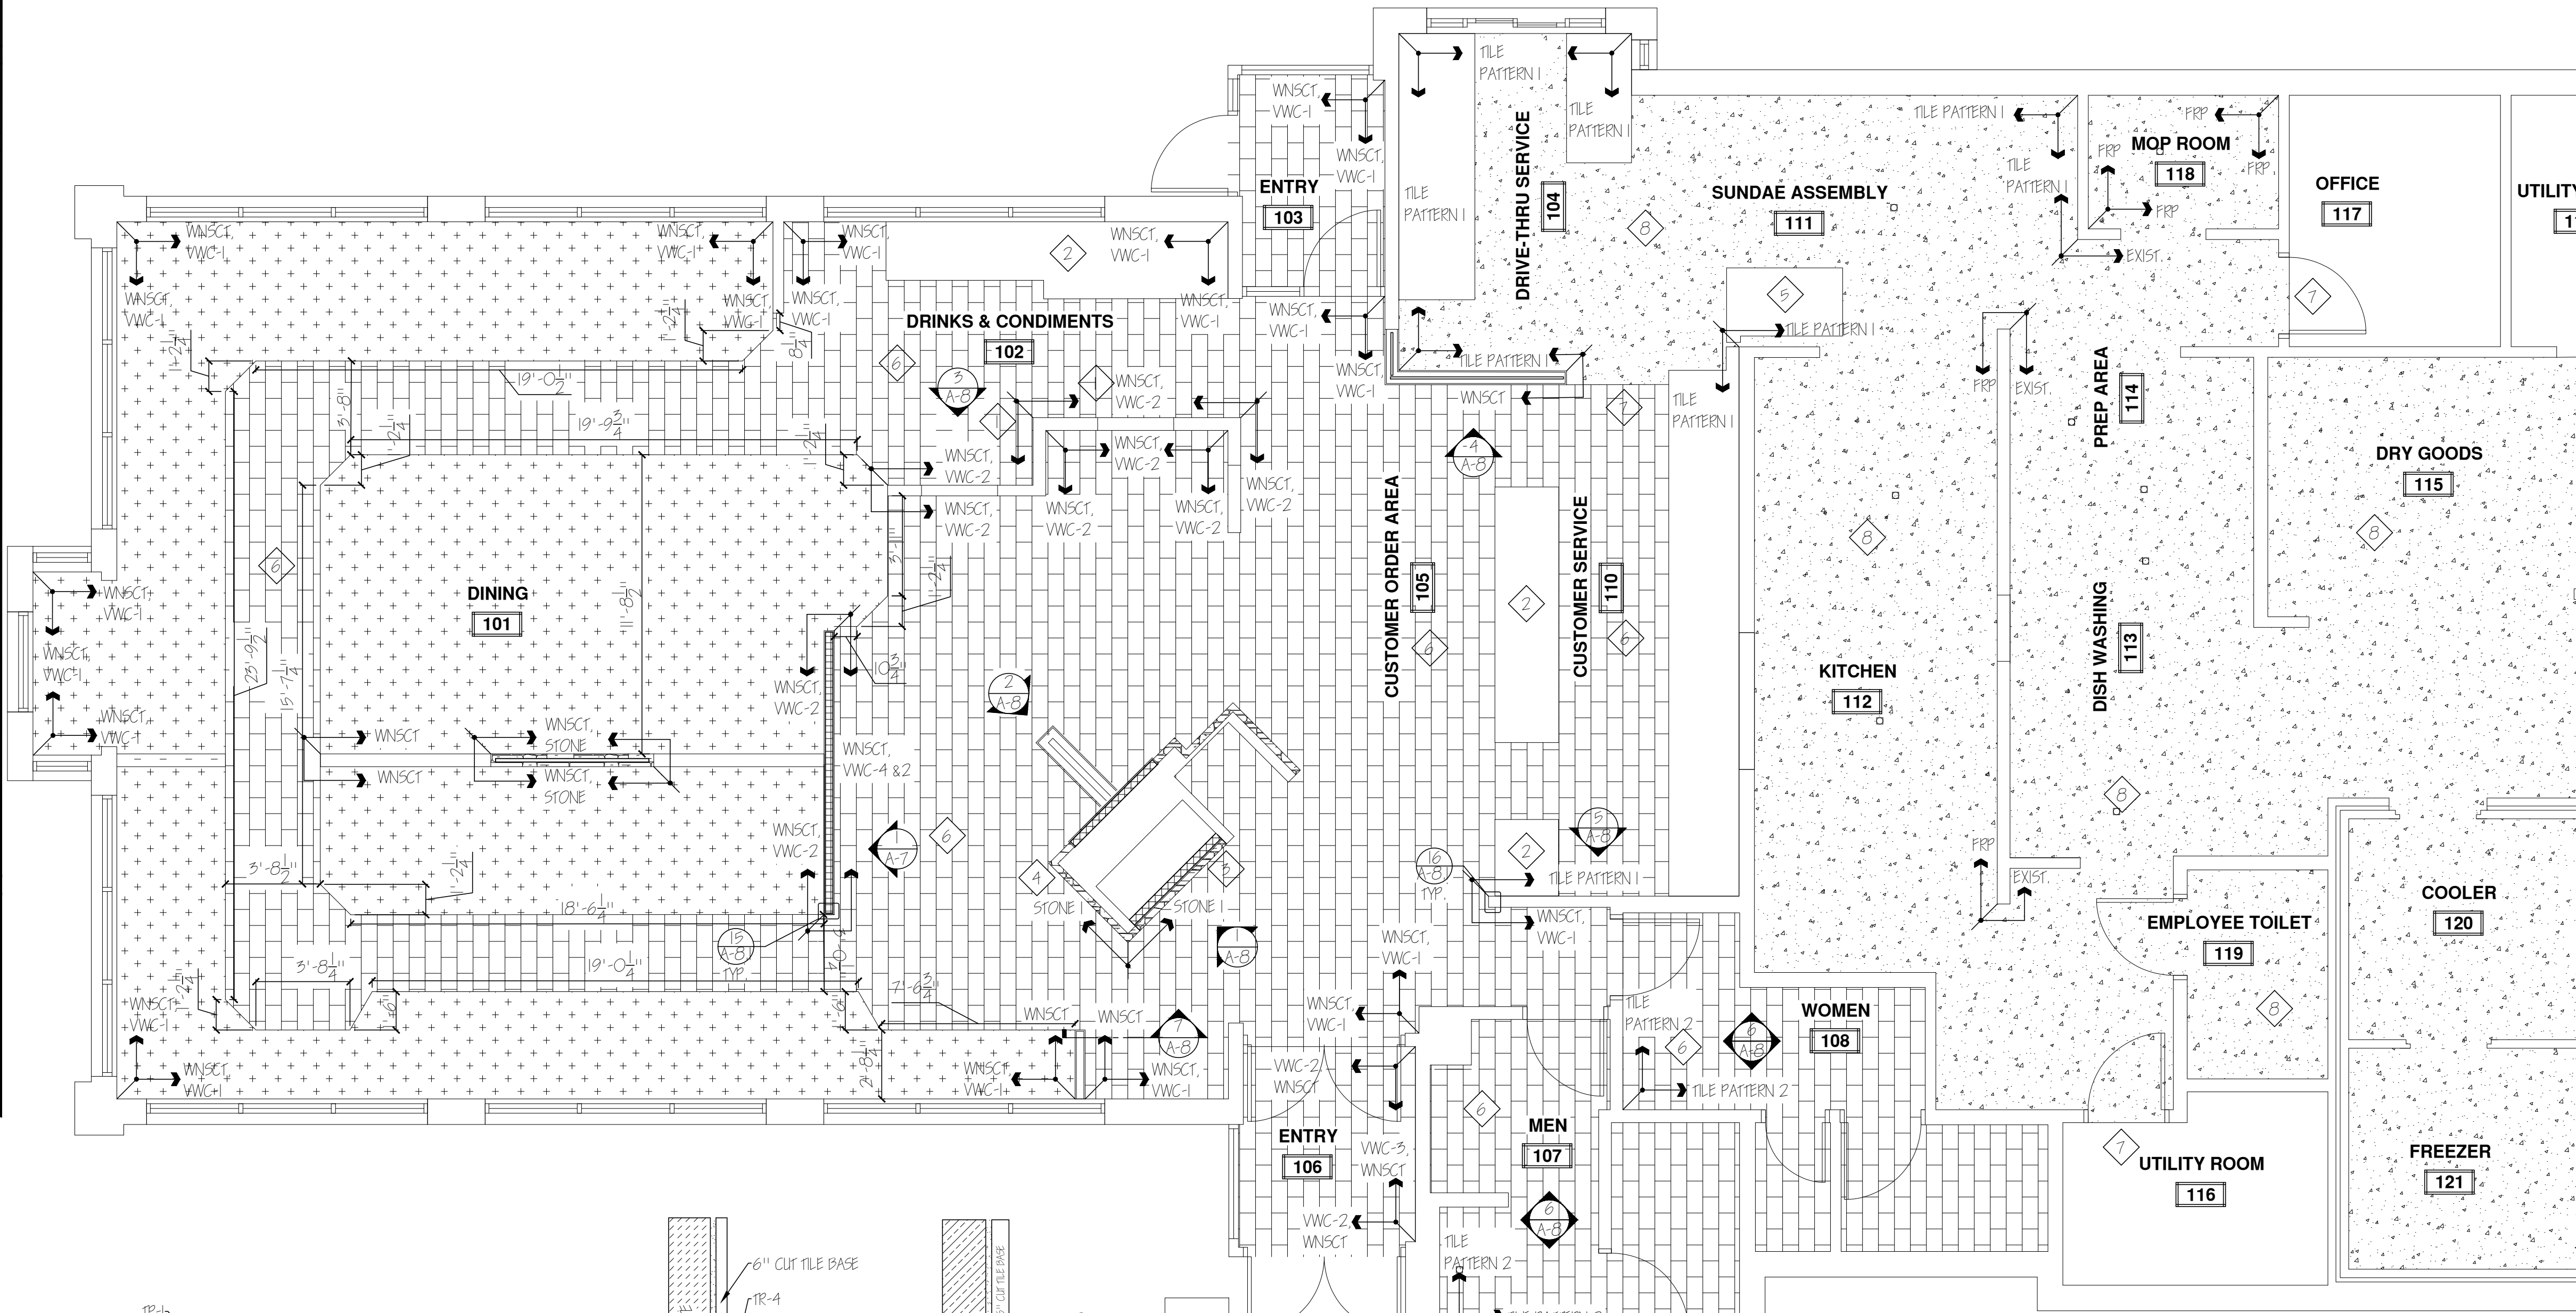

FINISH PLAN - CULVER'S OF SHAKOPEE, MN #0131
SCALE: 1/4" = 1'-0"

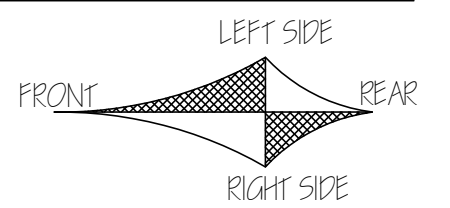

WARNING: These plans are for the exclusive use of Culver Franchising System, LLC and authorized franchise holders only. No part of these plans or the design they represent may be duplicated or reproduced without permission of Culver Franchising System, LLC


By	
Date	
Revision	

Culver Franchising System, LLC
1240 Water Street
Prairie du Sac, WI 53578
608-643-7980


CULVER FRANCHISING SYSTEM, LLC
REIMAGE 2027
CULVER'S OF SHAKOPEE, MN #0131

Sheet Contents	
FINISH PLAN	
Project No.	Shakopee, MN #0131
Drawn By:	E. ROCKWEILER
Date:	06/12/26


- STORY WALL NOTES:
- SCOOP AND SPATULA MURAL SHOULD APPEAR CENTERED ON THE WALL BETWEEN WAINSCOTING TRIM AND CEILING, TOP AND BOTTOM OF CIRCLE MAY CUT OFF
 - SCOOP AND SPATULA SHOULD APPEAR ON STORY WALL IN FULL.
 - OUTER CIRCLE WILL WRAP TO BACK OF WALL.
 - INSTALL ACRYLIC FRAME WITH NON-GLARE ACRYLIC FACING OUT.

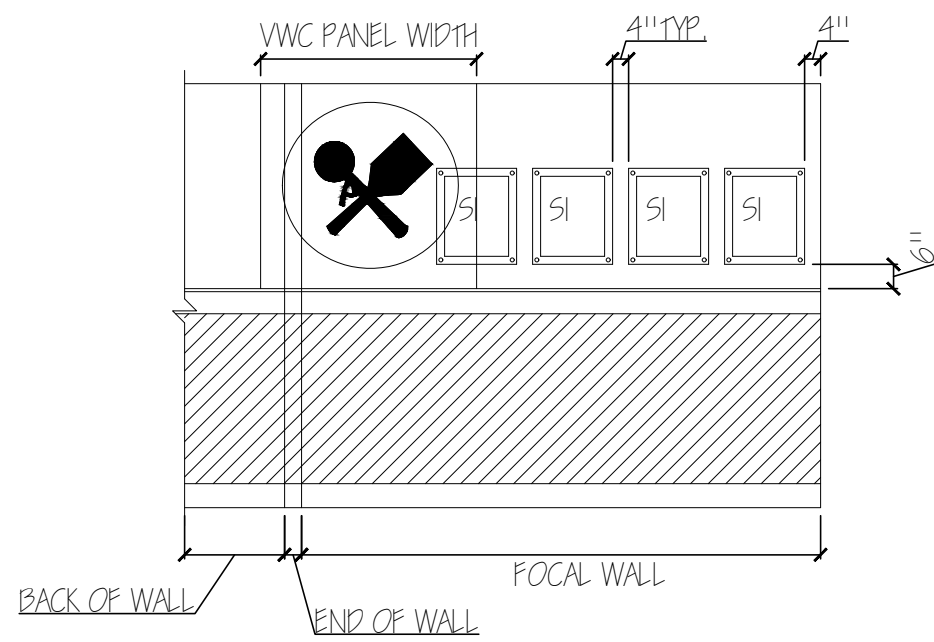


1 ELEV. - STANDARD STORY WALL & DINING MURAL VWC
SCALE: 1/4" = 1'-0"

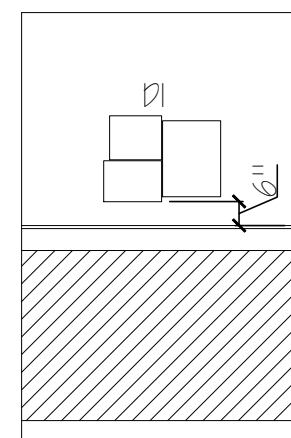


4 ELEV. - DELICIOUS ON SO MANY LEVELS TYP.
SCALE: 1/4" = 1'-0"

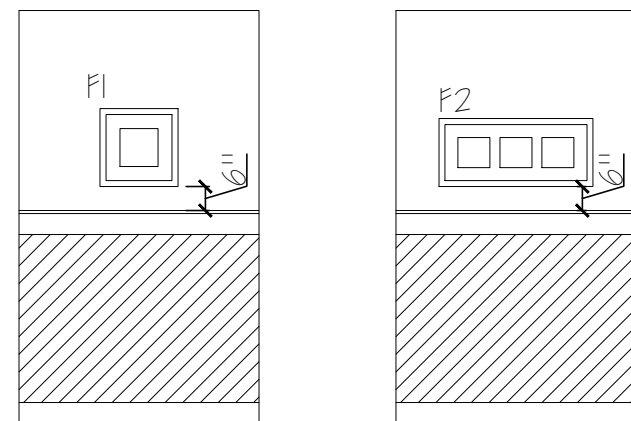


2 ELEV. - FRAMED ART TYP.
SCALE: 1/4" = 1'-0"

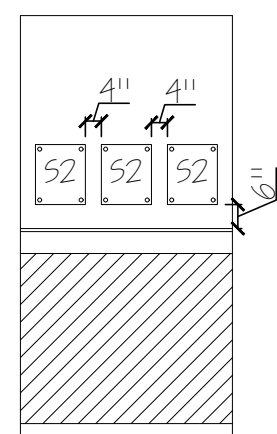


5 ELEV. - LAYERS OF DELICIOUS FUN TYP.
SCALE: 1/4" = 1'-0"

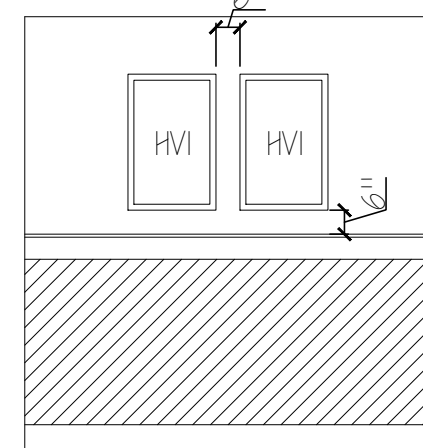


3 ELEV. - HEART OF FRESHNESS TYP.
SCALE: 1/4" = 1'-0"

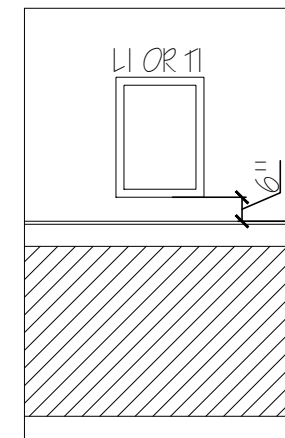

6 ELEV. - CULVER'S PRIDE: STATE ART OR TRAVEL POSTER TYP.
SCALE: 1/4" = 1'-0"

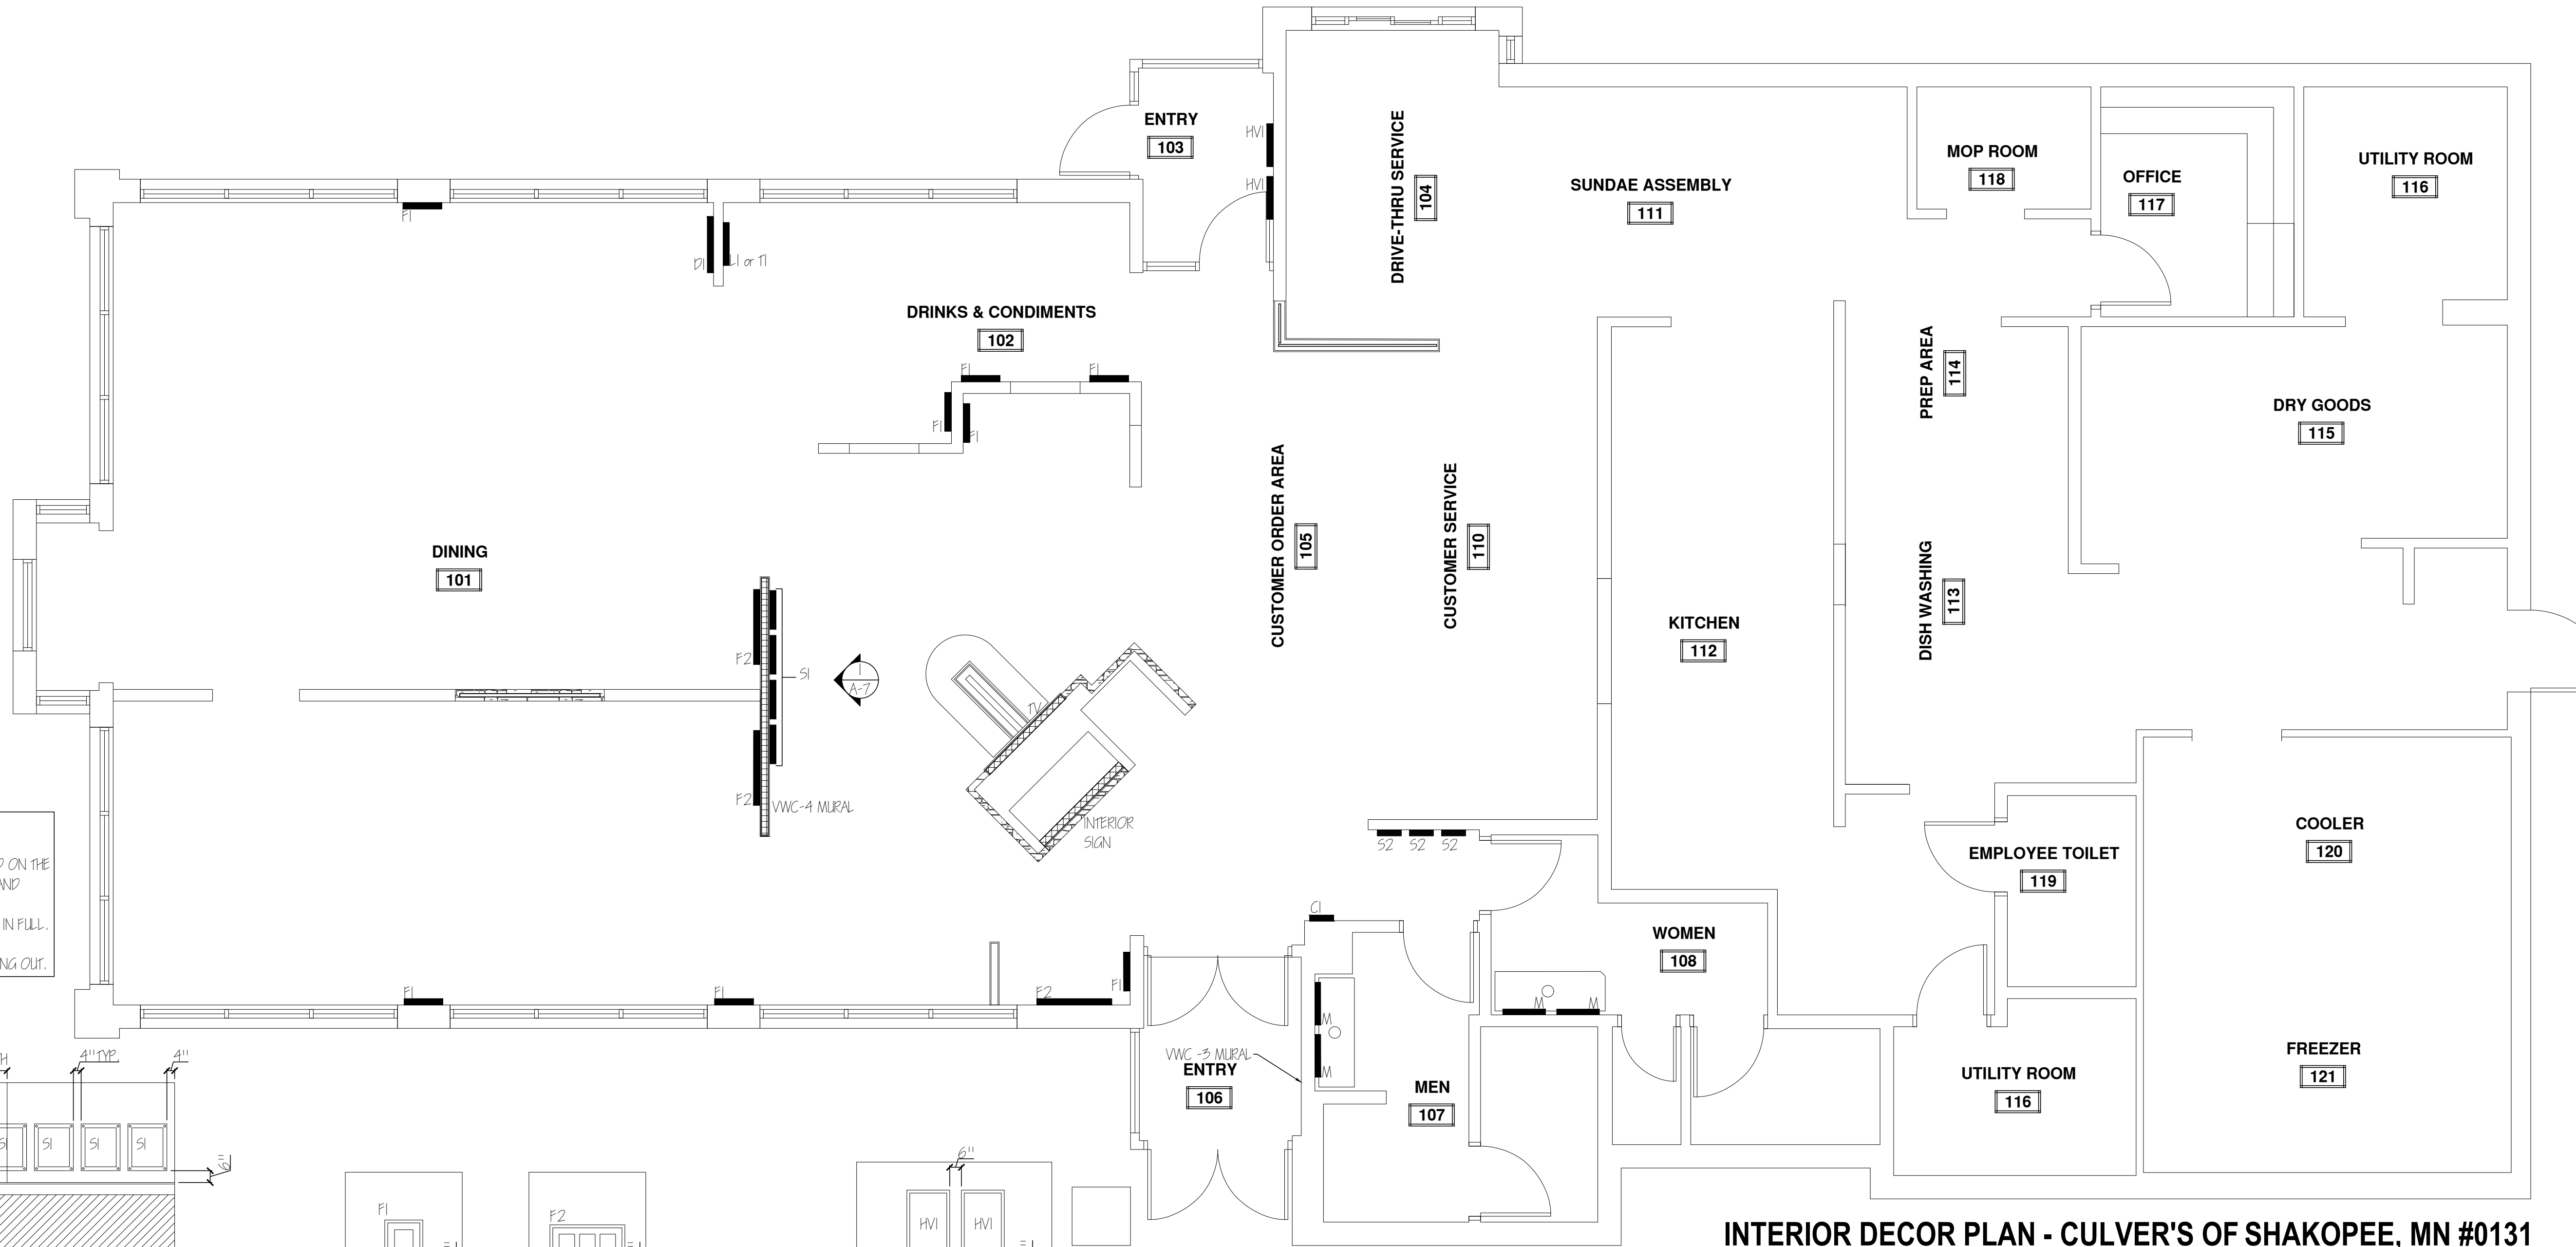

INTERIOR DECOR PLAN - CULVER'S OF SHAKOPEE, MN #0131
SCALE: 1/4" = 1'-0"

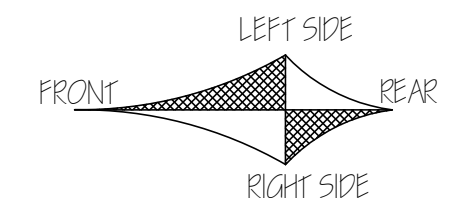

INTERIOR DECOR SCHEDULE				
TYPE	SIZE (WIDTH X HEIGHT)	QUANTITY	COLLECTION	TYPE
D1	13 X 11, 14.5 X 10.25, 14.5 X 19	1 NEW	DELICIOUS ON SO MANY LEVELS	PRINTED METAL 3-PIECE COLLAGE
F1	19.5 X 19.5	8 NEW	FRAMED	FRAMED AND MATED PRINTS, NON-GLARE ACRYLIC
F2	38.5 X 17	3 NEW	FRAMED	FRAMED AND MATED PRINTS, NON-GLARE ACRYLIC
HVI	22 X 34	2 NEW	VERTICAL HEART OF FRESHNESS	WOOD FRAME W/ PRINTED PVC INSERTS
SI	20 X 24	4 NEW	STORY WALL	ACRYLIC FRAME W/ METAL STAND OFFS
S2	12.5 X 15	3 NEW	LAYERS OF DELICIOUS FUN	ACRYLIC FRAME W/ METAL STAND OFFS
LI	22 X 30	1*	CULVER'S PRIDE: STATE ART	FRAMED AND MATED PRINT, NON-GLARE ACRYLIC
TI	22 X 30	1*	TRAVEL POSTER	FRAMED AND MATED PRINT, NON-GLARE ACRYLIC
CI	12.5 X 15	1	GUEST COMMUNICATIONS	ACRYLIC FRAME W/ METAL STAND OFFS
M	22X 36	4	RESTROOM MIRROR	POLYSTYRENE FRAME W/ GLASS MIRROR

*FRANCHISEE TO SELECT LI OR TI.

- GENERAL NOTES:
- ALL ARTWORK IS OWNER PROVIDED, GC INSTALLED
 - ARTWORK COMES WITH SECURITY HARDWARE
 - BOTTOM OF ARTWORK SHOULD BE INSTALLED 6" ABOVE THE TOP OF WAINSCOTING
 - INSTALL MURAL FIRST. SURROUNDING PANELS MUST BE REVERSE HUNG, REFER TO MANUFACTURER INSTALLATION INSTRUCTIONS PROVIDED WITH ORDER.

WARNING: These plans are for the exclusive use of Culver Franchising System, LLC and authorized franchise holders only. No part of these plans or the design they represent may be duplicated or reproduced without permission of Culver Franchising System, LLC

Sheet Contents
INTERIOR DECOR PLAN




Project No.
Shakopee, MN #0131
Drawn By:
E. ROCKWEILER
Date:
06/12/26

Sheet
A-7

CULVER FRANCHISING SYSTEM, LLC
REIMAGE 2027
CULVER'S OF SHAKOPEE, MN #0131

Culver Franchising System, LLC
1240 Water Street
Prairie du Sac, WI 53578
608-643-7980










By	Date	Revision

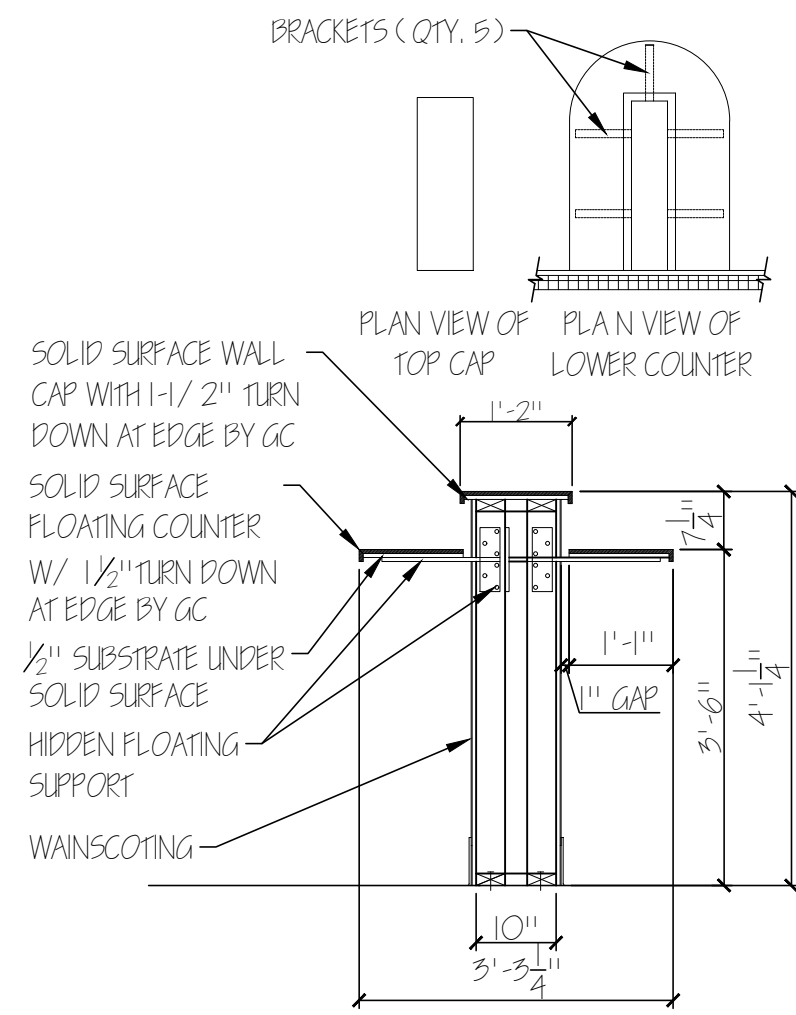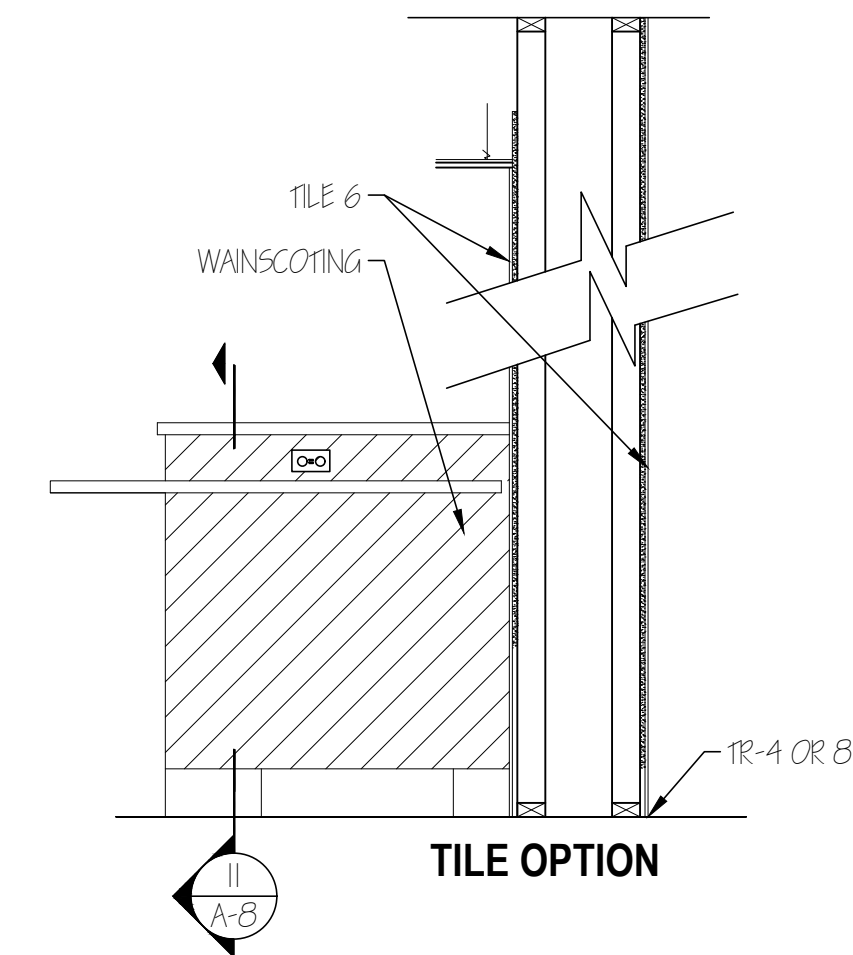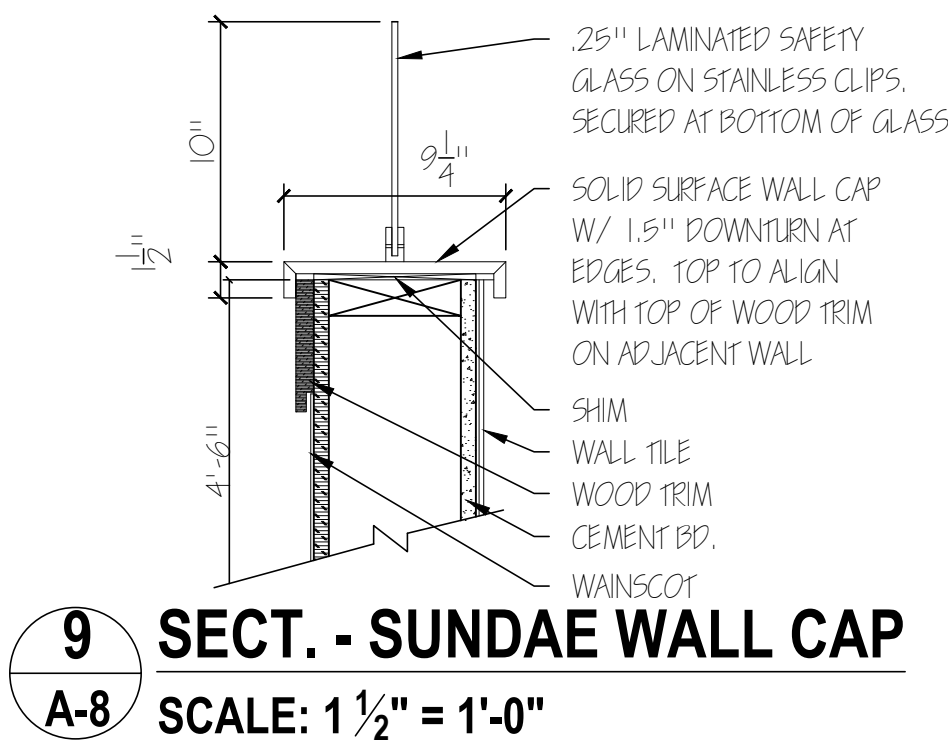

WAINSCOTING INSTALLATION GENERAL NOTES:

1. USE MANUFACTURER RECOMMENDED ADHESIVES AND INSTALLATION METHODS
2. GC TO VERIFY INSTALLATION FOR EXTERIOR WALLS w/ MARLITE MANUFACTURERS REP
3. TILE BASE AT TILE FLOOR
4. VINYL BASE AT CARPET
5. EASE ALL OUTSIDE CORNERS OF MAPLE TRIM
6. MAPLE TRIM PACKAGE BY PEC, INSTALLED BY GC

MAPLE TRIM PACKAGE:	
DESCRIPTION	SIZE
FULL WALL TOP CAP	3/4" x 1 1/4"
HALF WALL TOP CAP	3/4" x 7/8"
WAINSCOTING CAP	3/4" x 5 1/2"

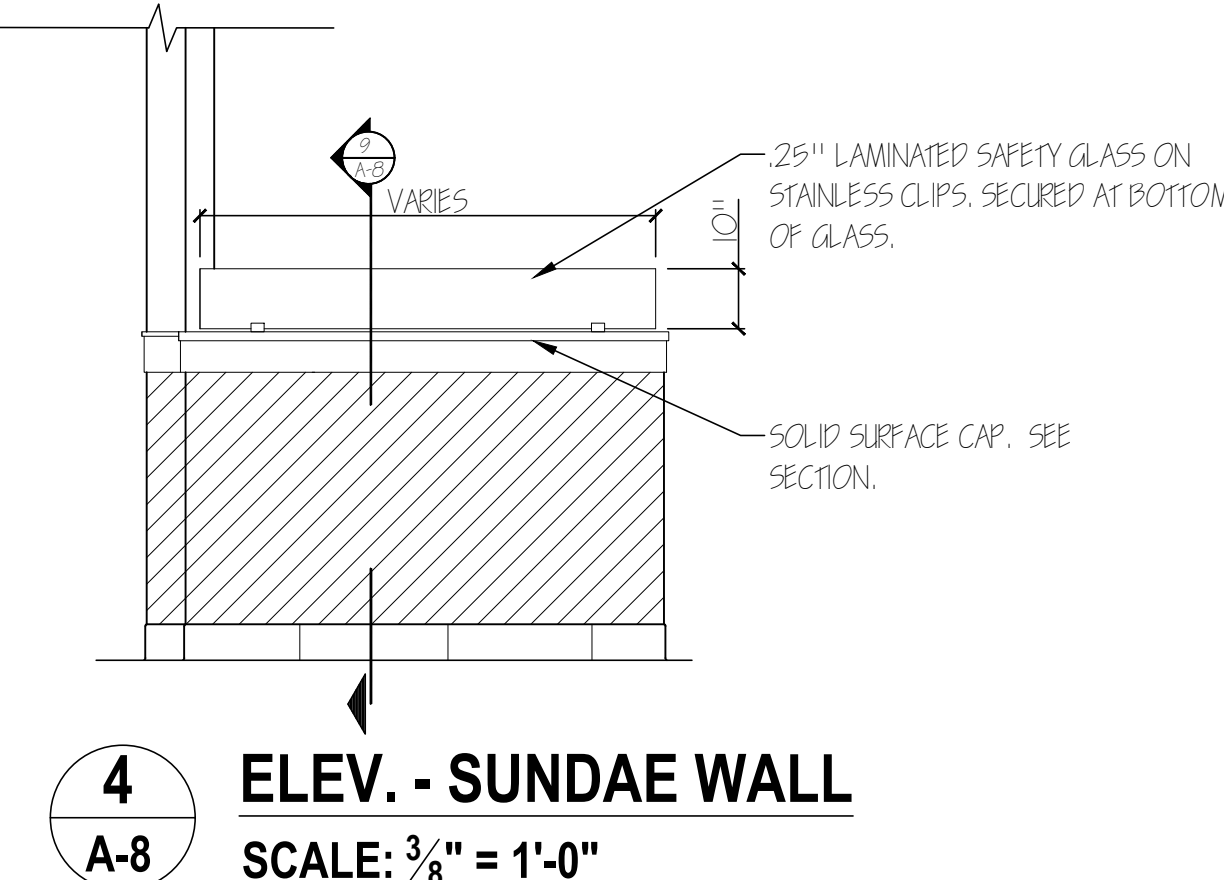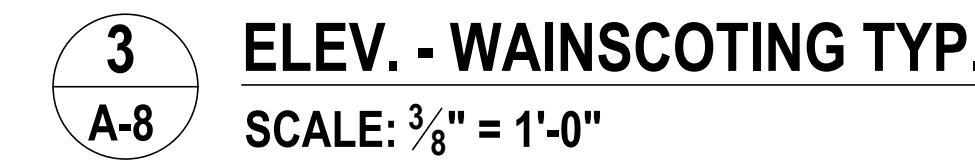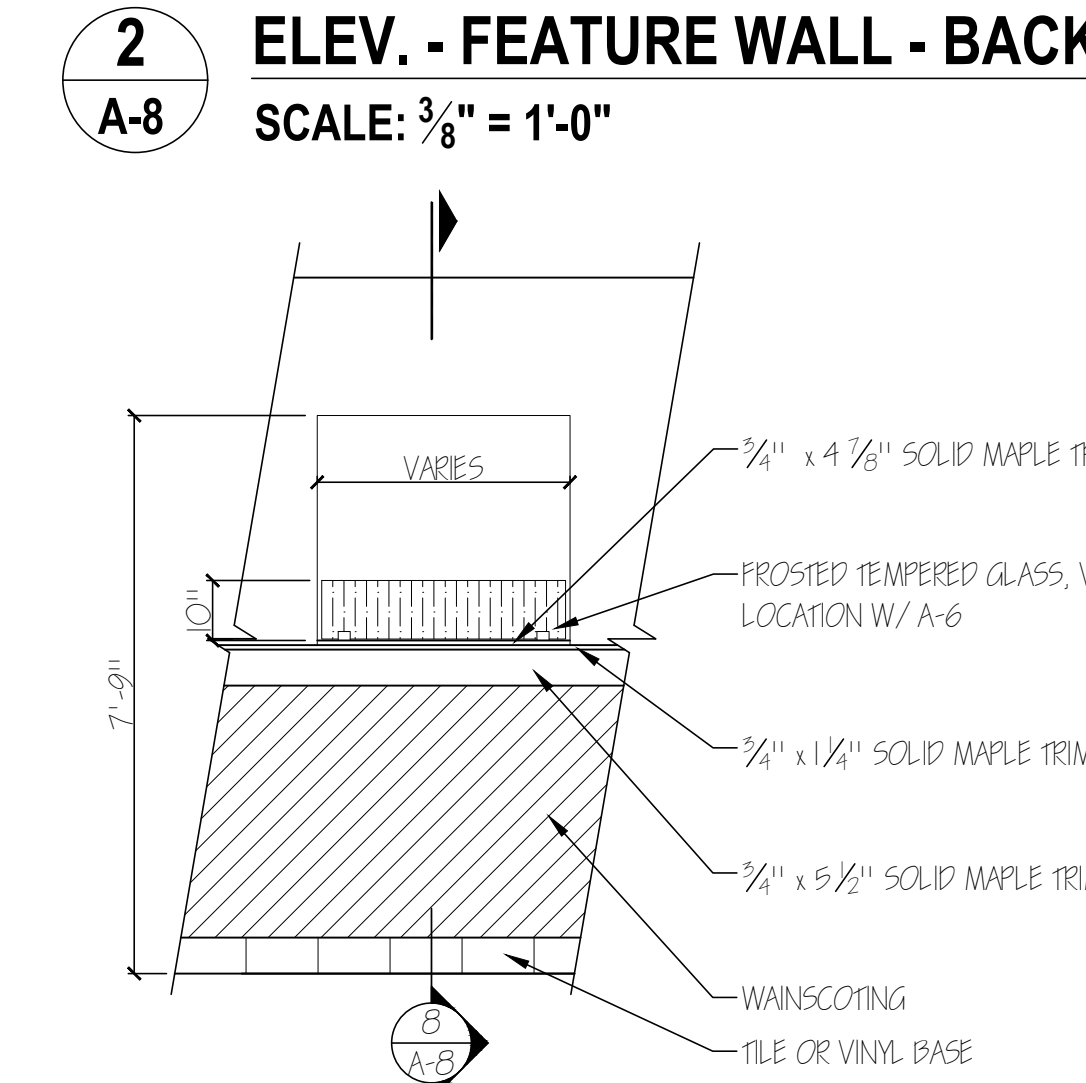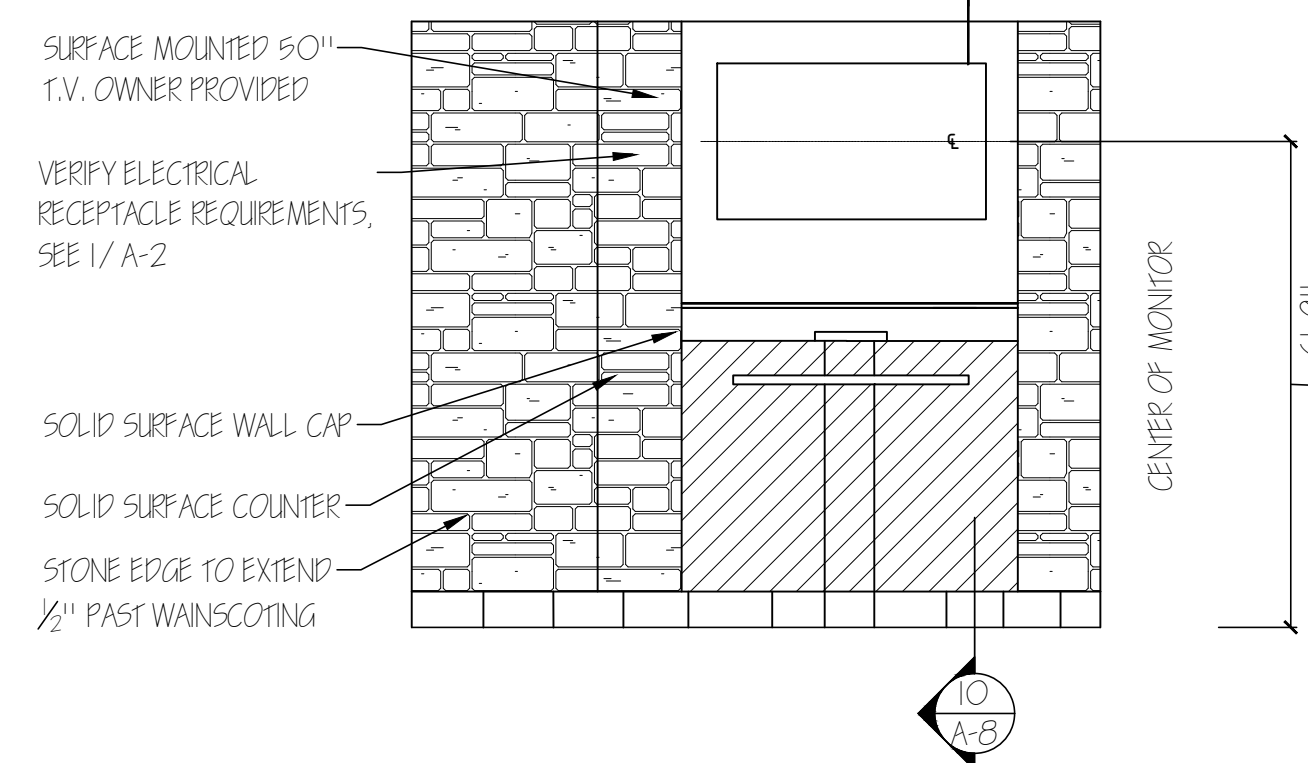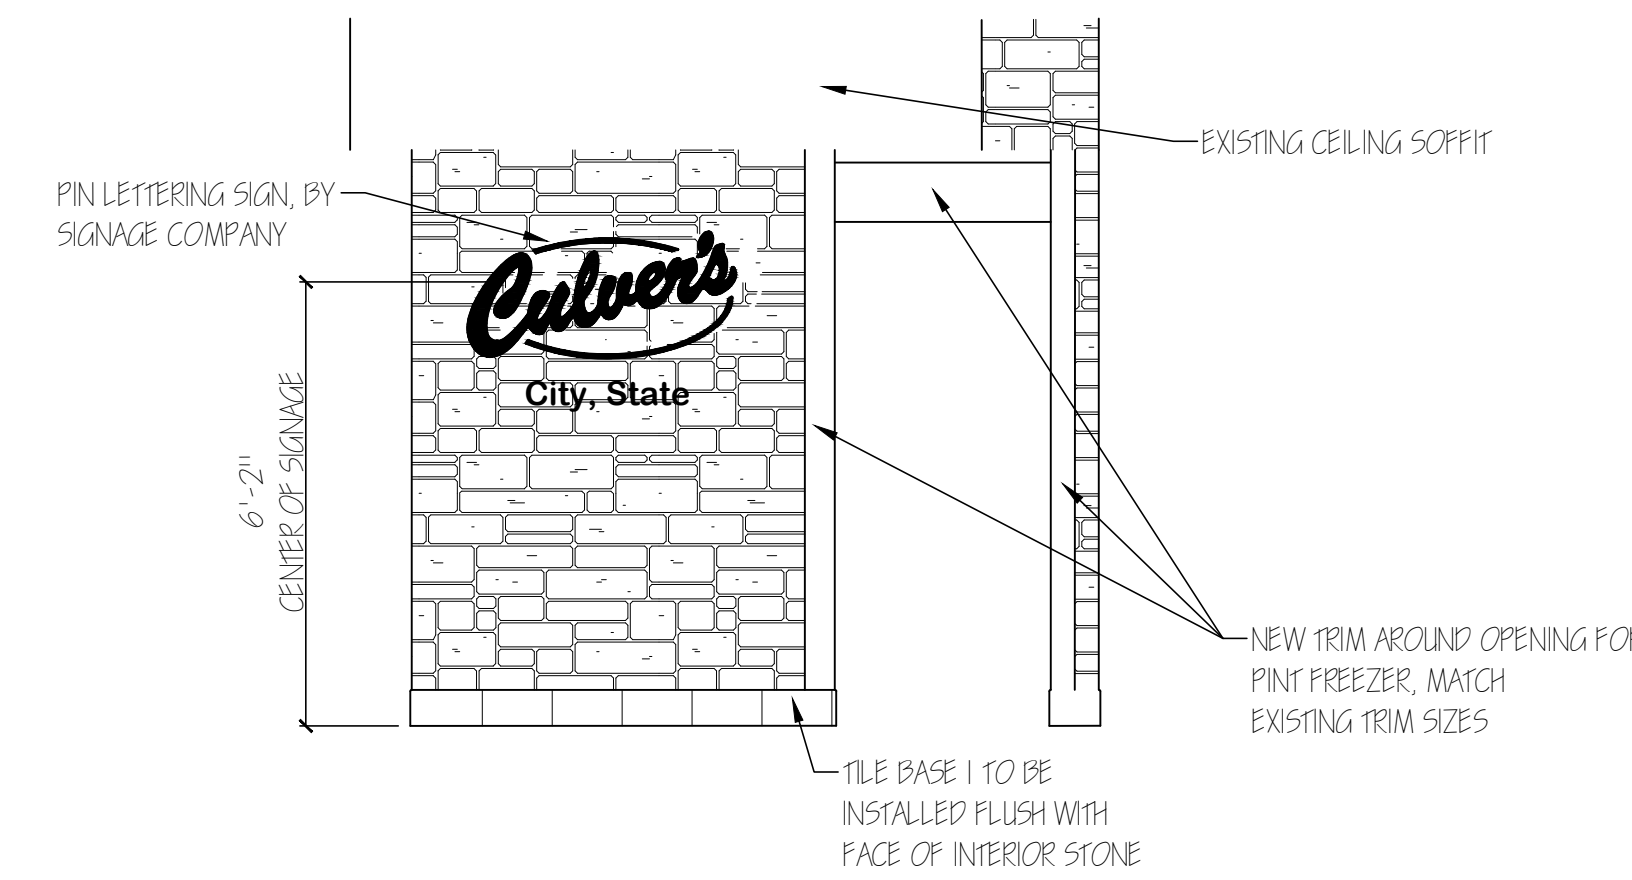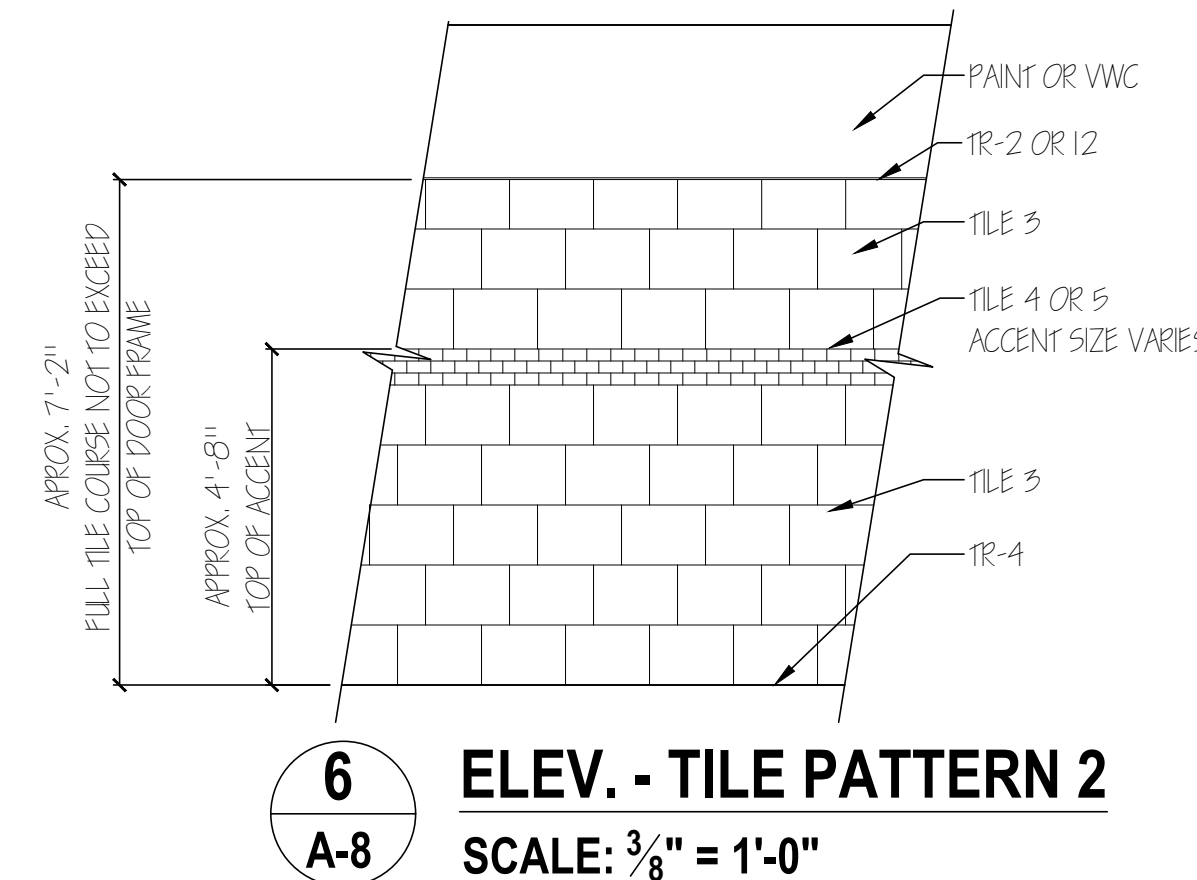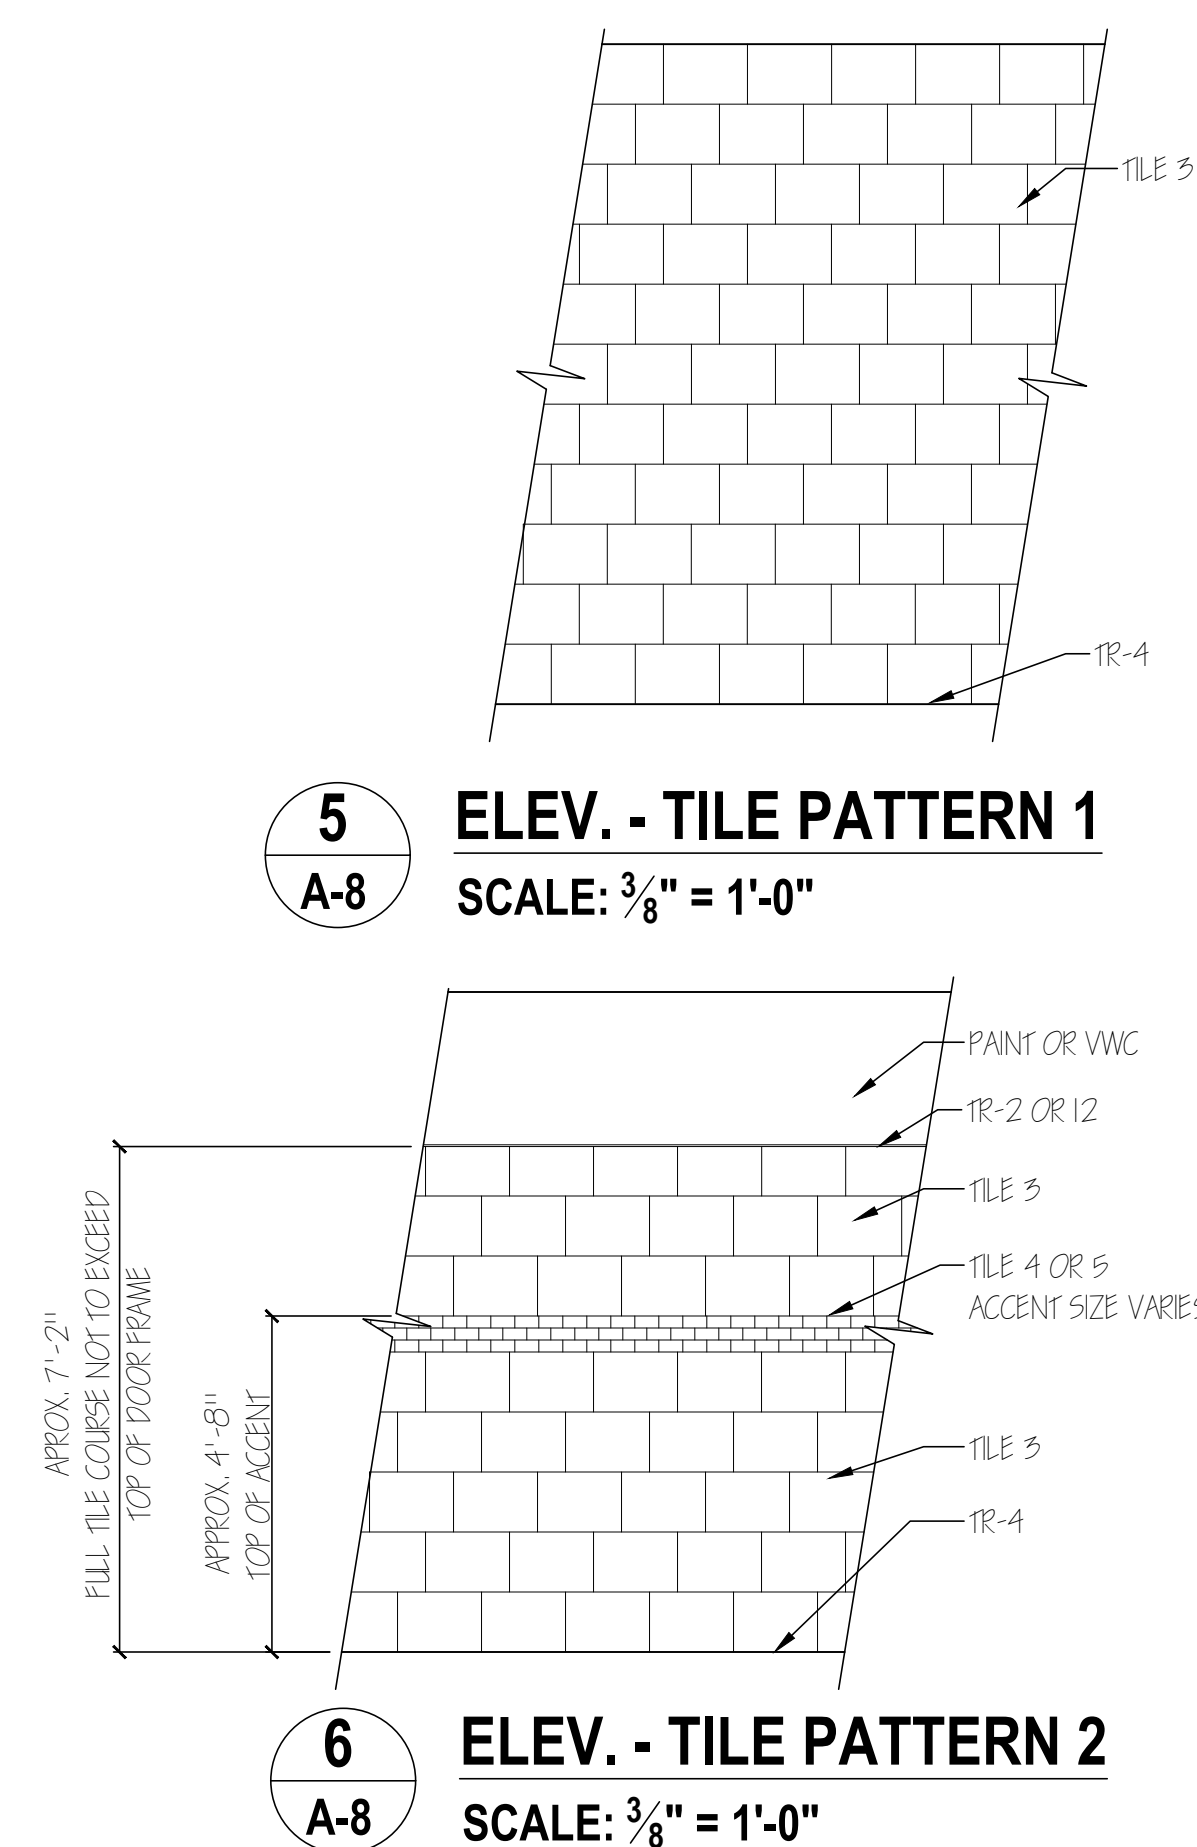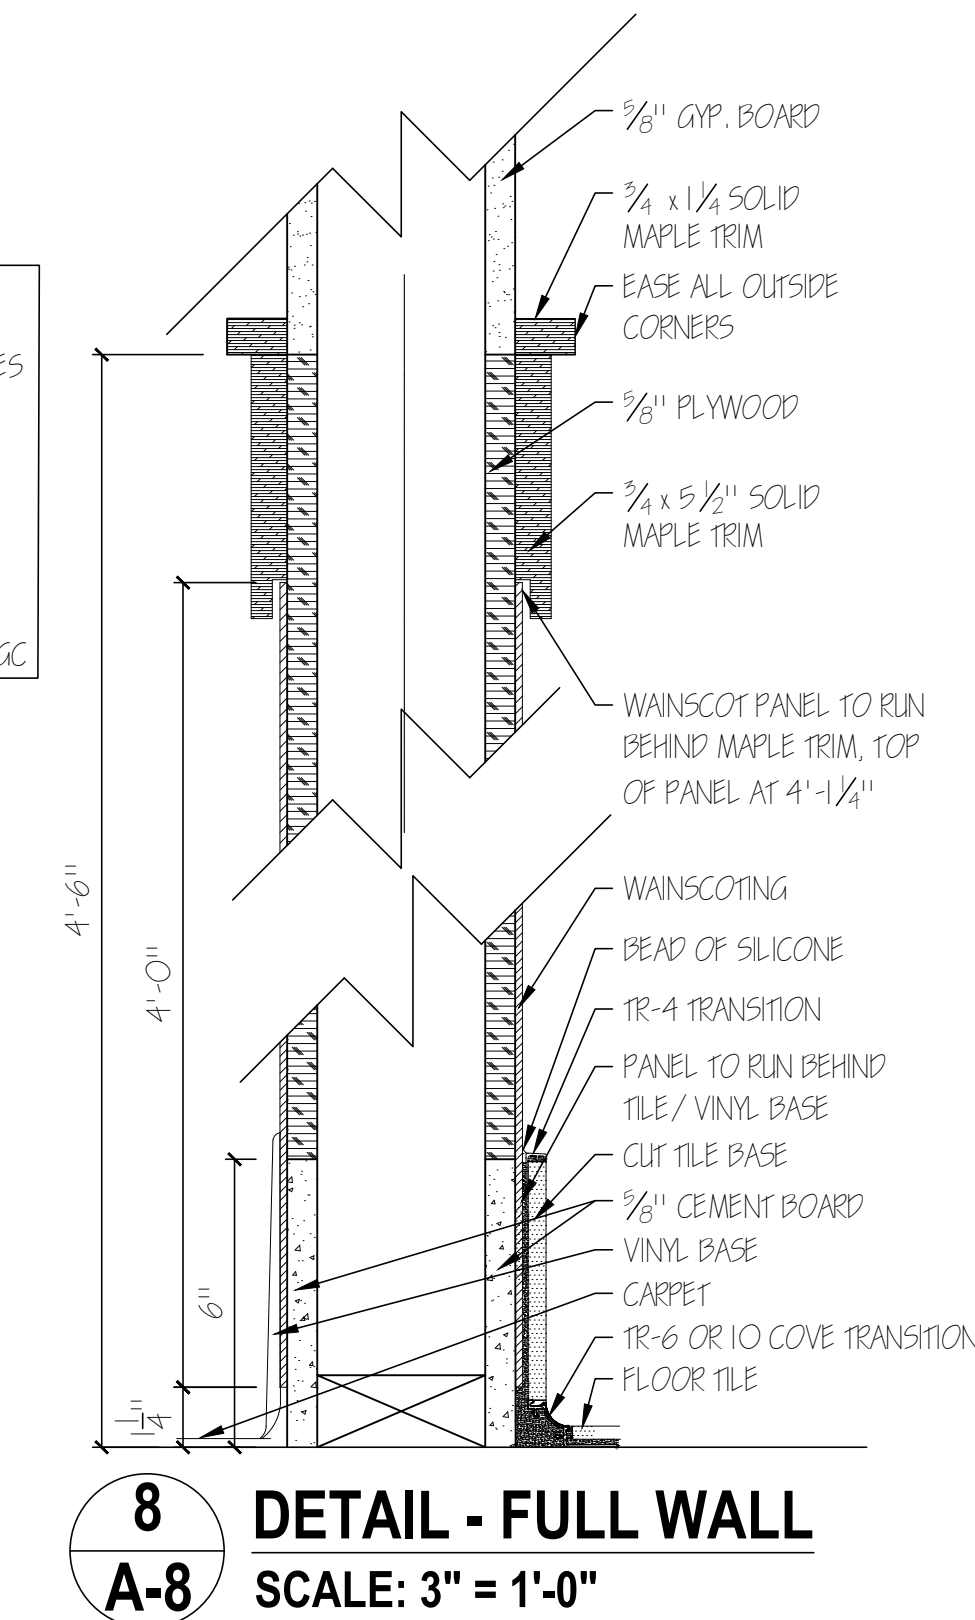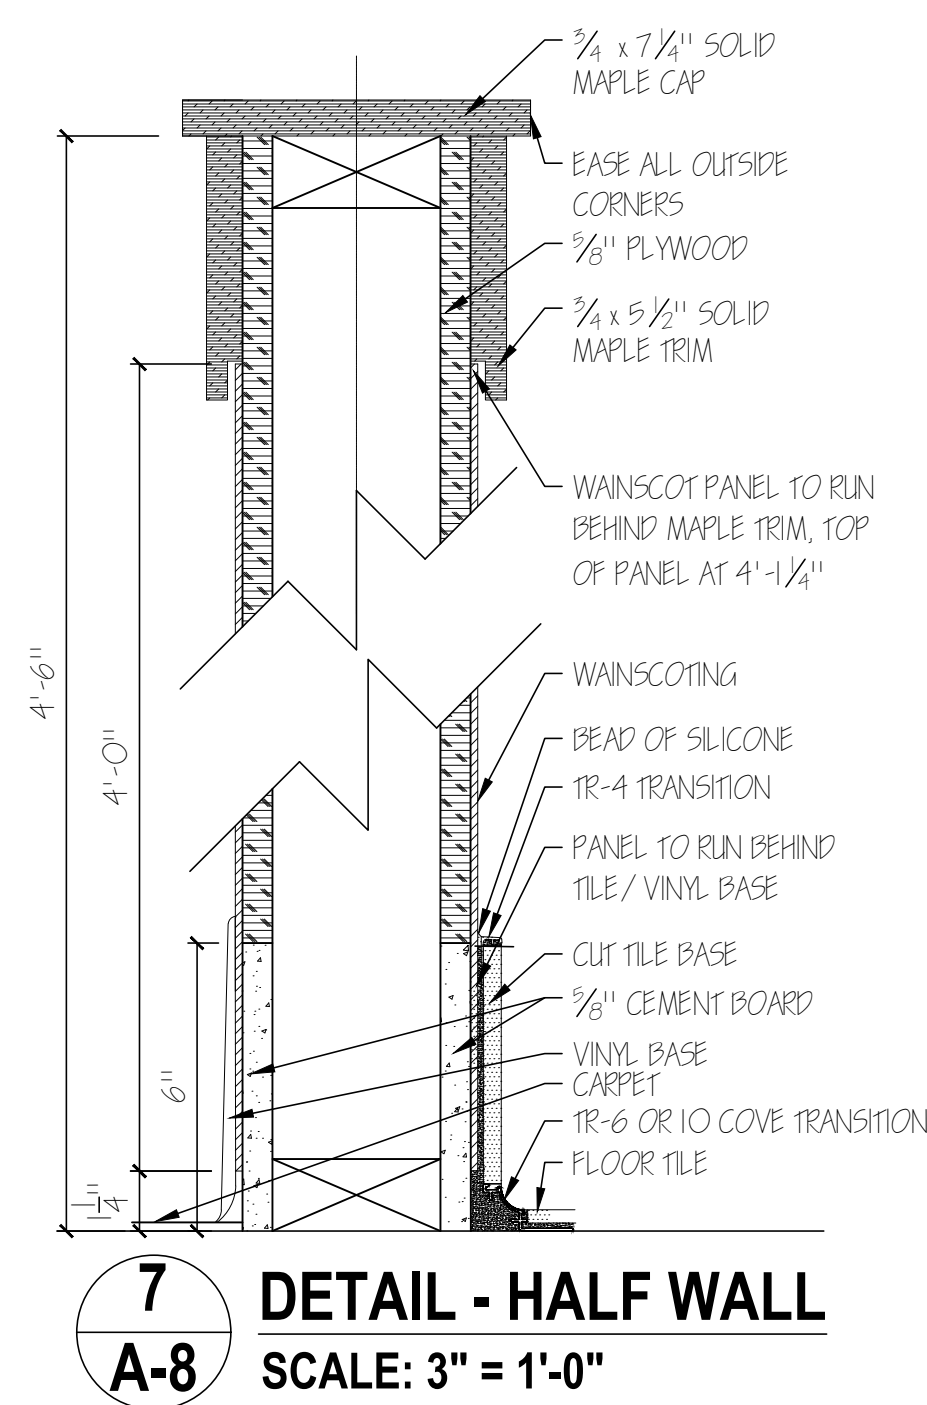

WARNING: These plans are for the exclusive use of Culver Franchising System, LLC and authorized franchise holders only. No part of these plans or the design they represent may be duplicated or reproduced without permission of Culver Franchising System, LLC


By	
Date	
Revision	

Culver Franchising System, LLC.
1240 Water Street
Prairie du Sac, WI 53578
608-643-7980

CULVER FRANCHISING SYSTEM, LLC
REIMAGE 2027
CULVER'S OF SHAKOPEE, MN #0131


Sheet Contents
ELEV'S & DETAILS
Project No. Shakopee, MN #0131
Drawn By: E. ROCKWEILER
Date: 06/12/26

Sheet
A-8

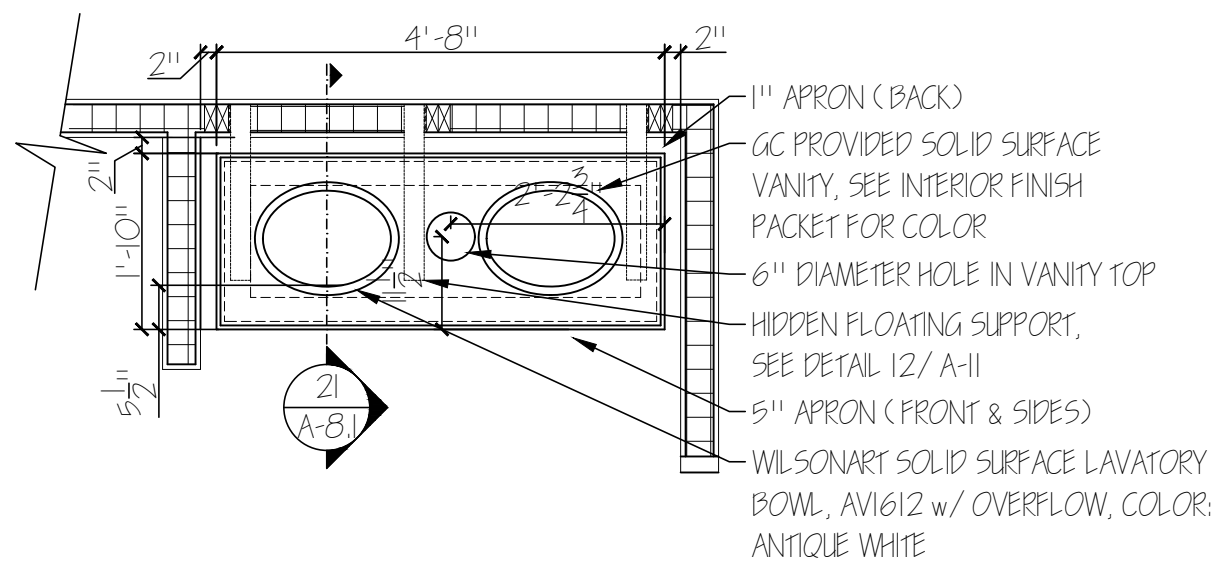


20 FLOATING VANITY - 107

A-8.1 SCALE: 1/2" = 1'-0"

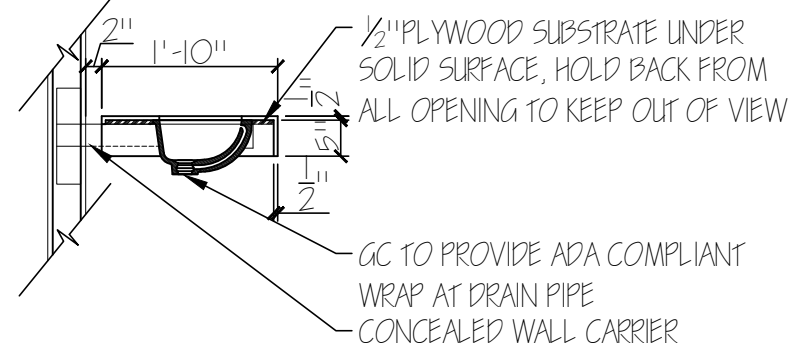

21 SECT. - FLOATING VANITY


A-8.1 SCALE: 1/2" = 1'-0"

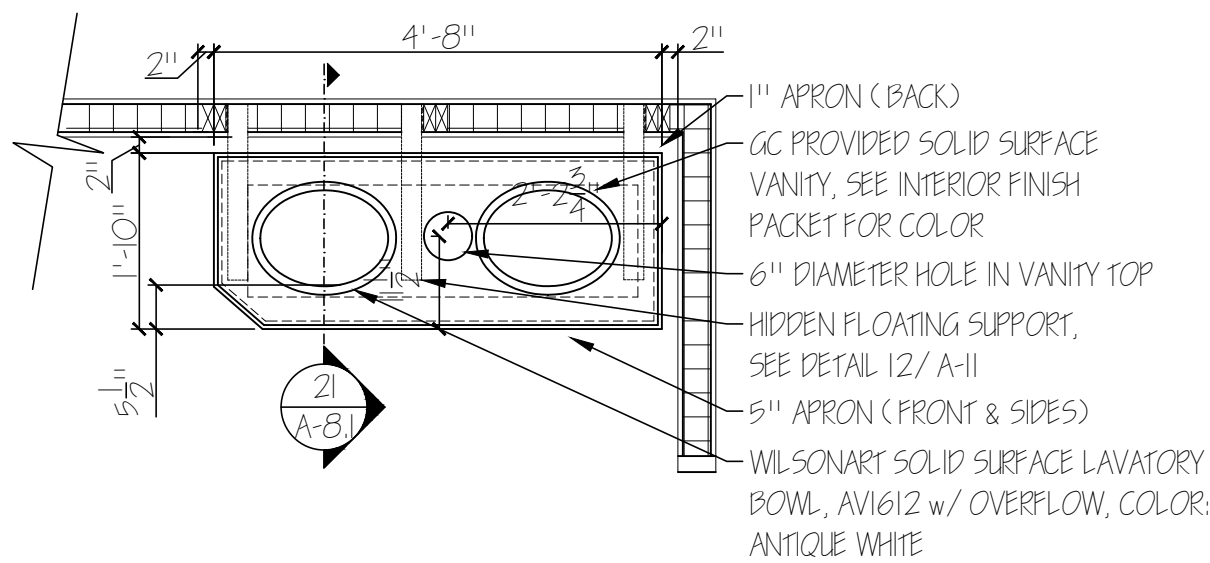

22 FLOATING VANITY - 108


A-8.1 SCALE: 1/2" = 1'-0"

LOWER EXISTING BULKHEAD AS NEEDED TO ACCOMMODATE NEW SCREEN. SCREEN SHOULD NOT HANG BELOW BULKHEAD. PREFERRED HEIGHT TO BE 8'-2" AFF FOR THE BULKHEAD AND 8'-4" AFF TO BOTTOM OF TV.

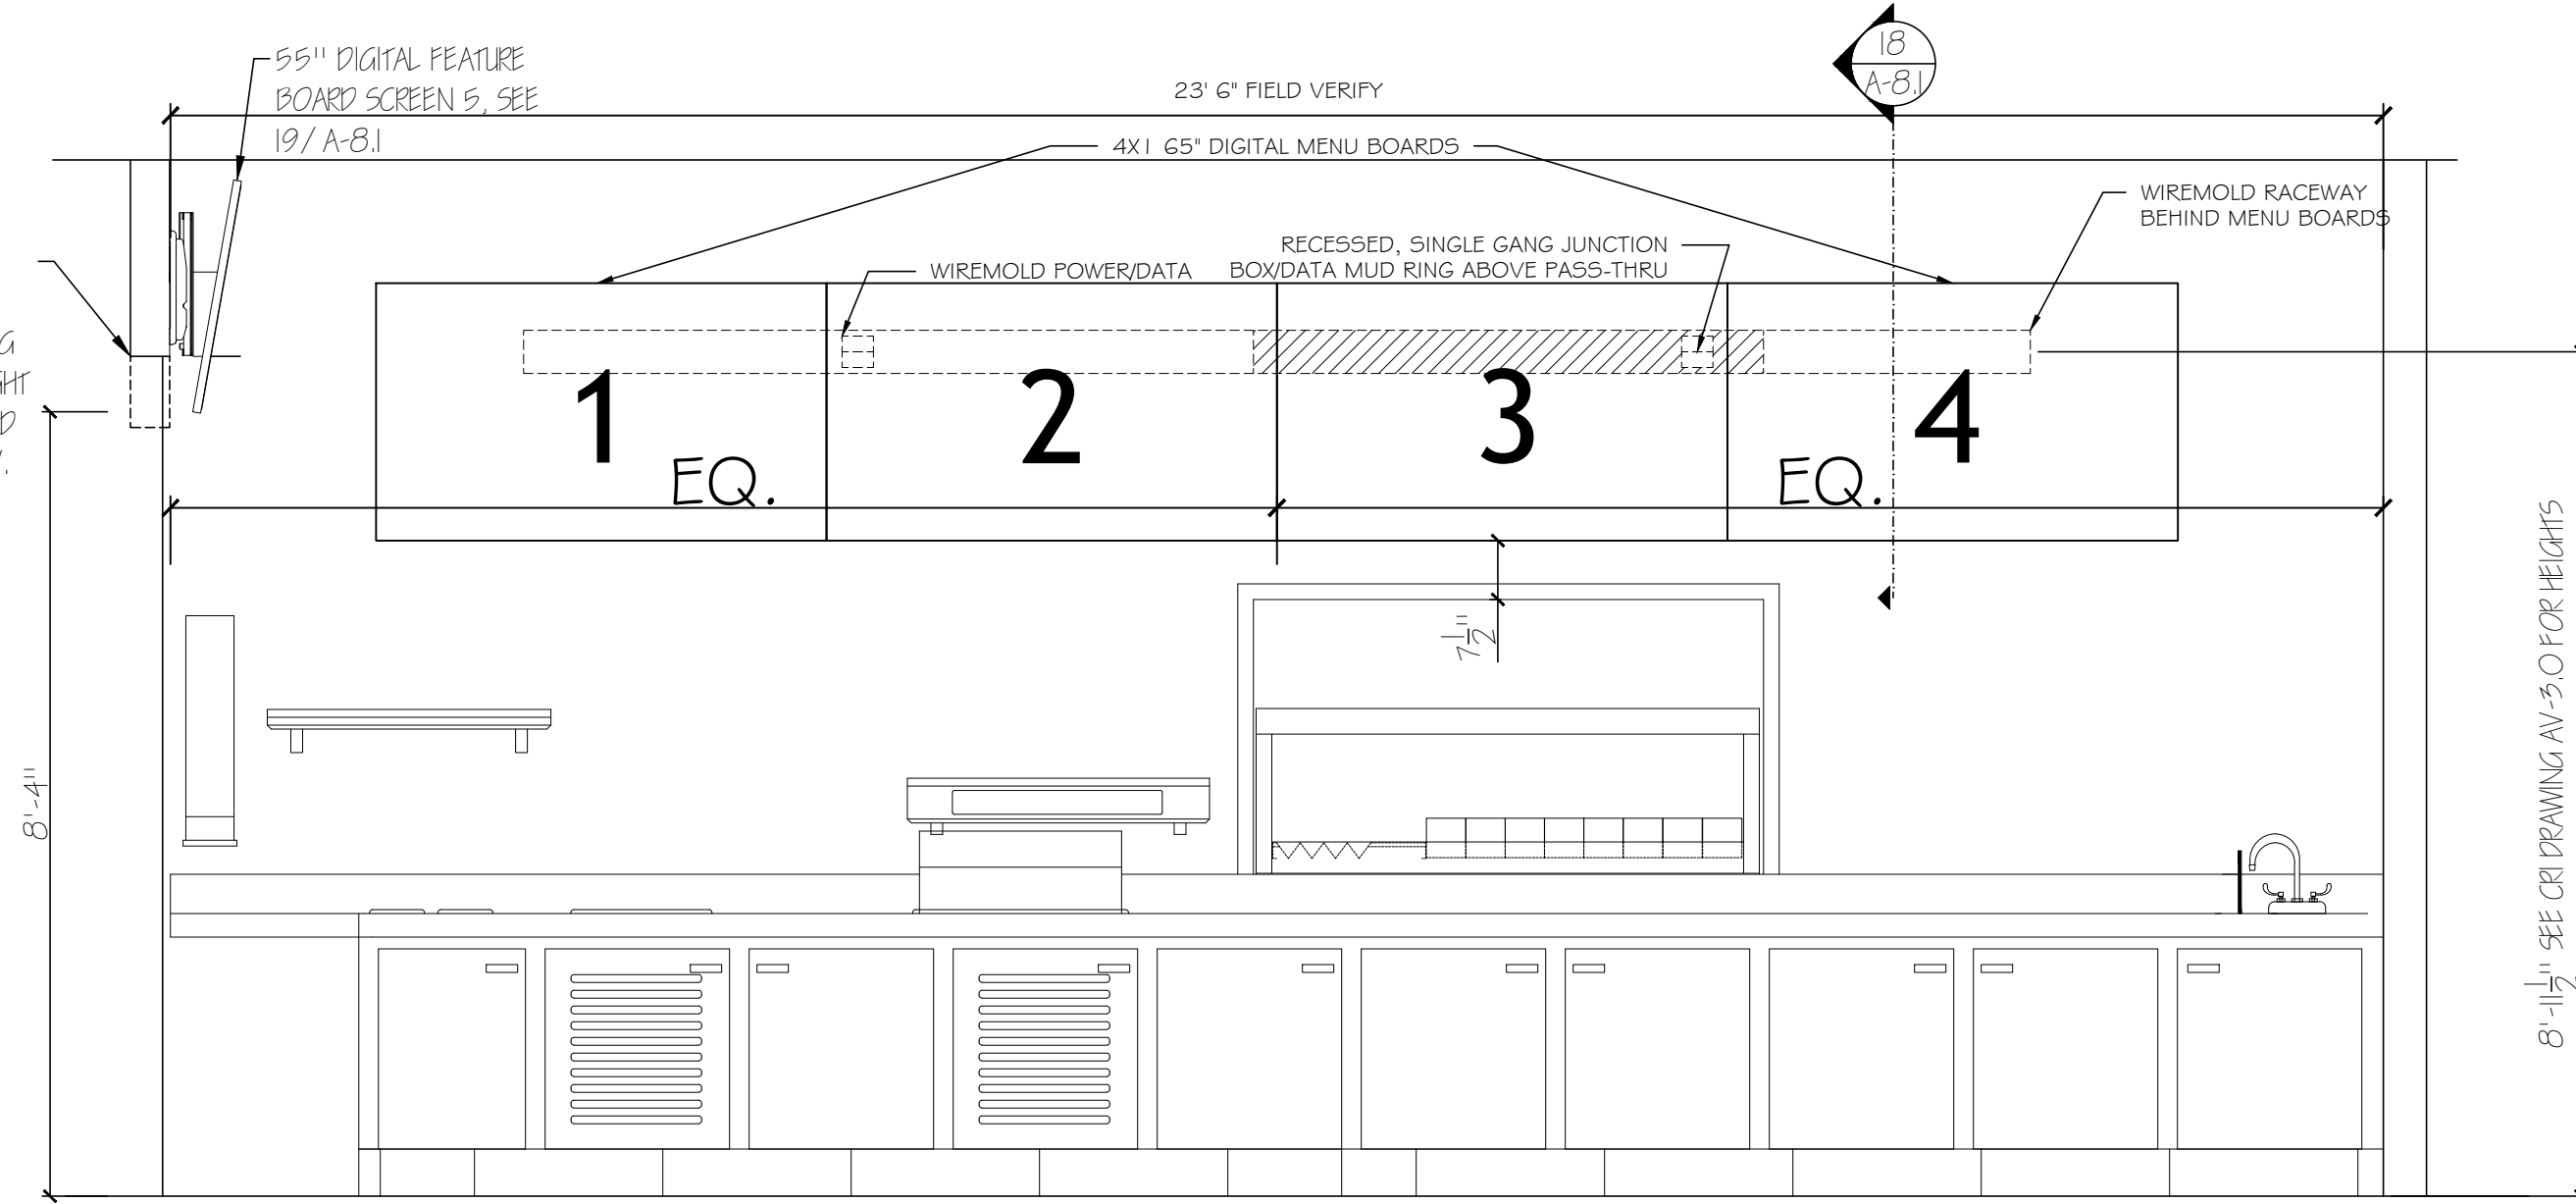


17 ELEV. - INTERIOR DIGITAL MENU BOARD

A-8.1 SCALE: 1/2" = 1'-0"

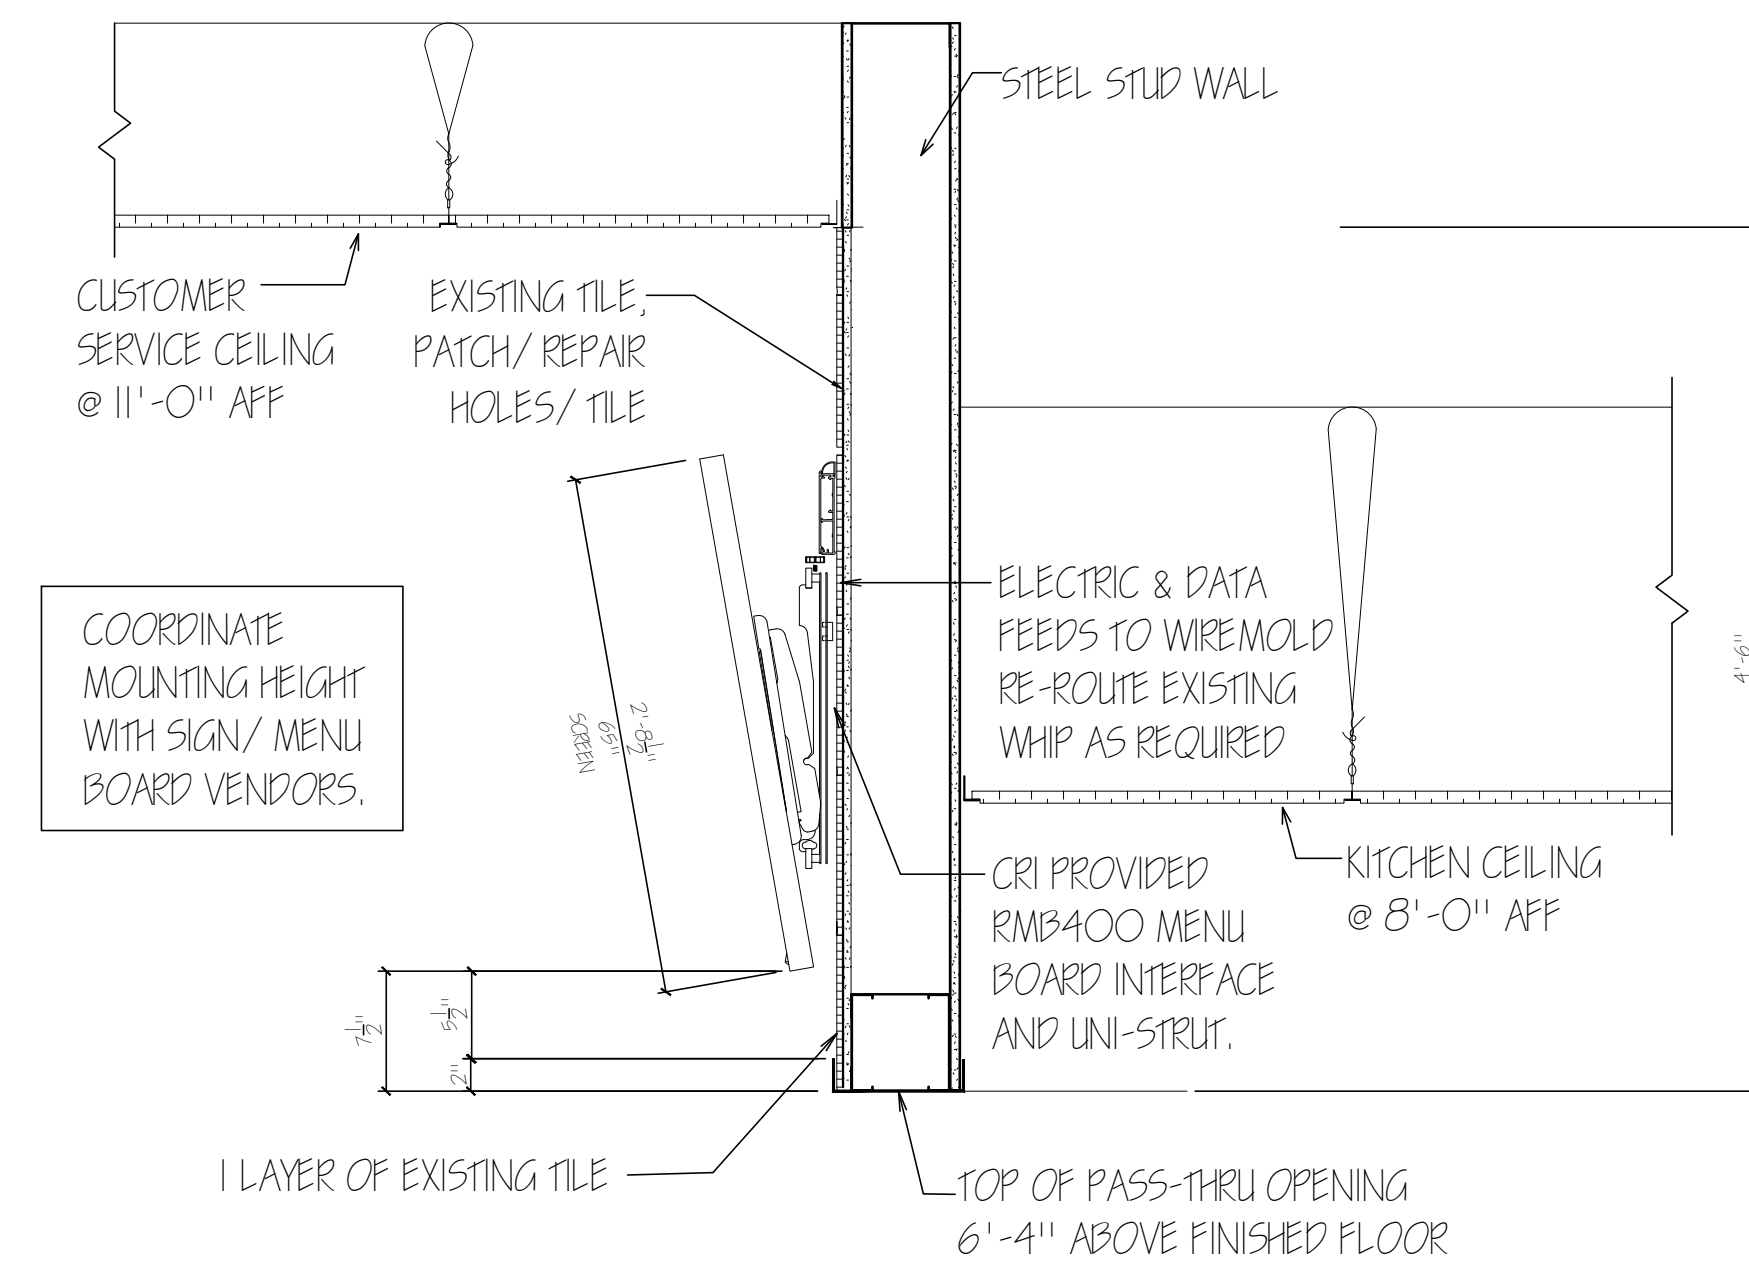

18 INTERIOR DIGITAL MENU BOARD DETAIL

A-8.1 SCALE: 1" = 1'-0"

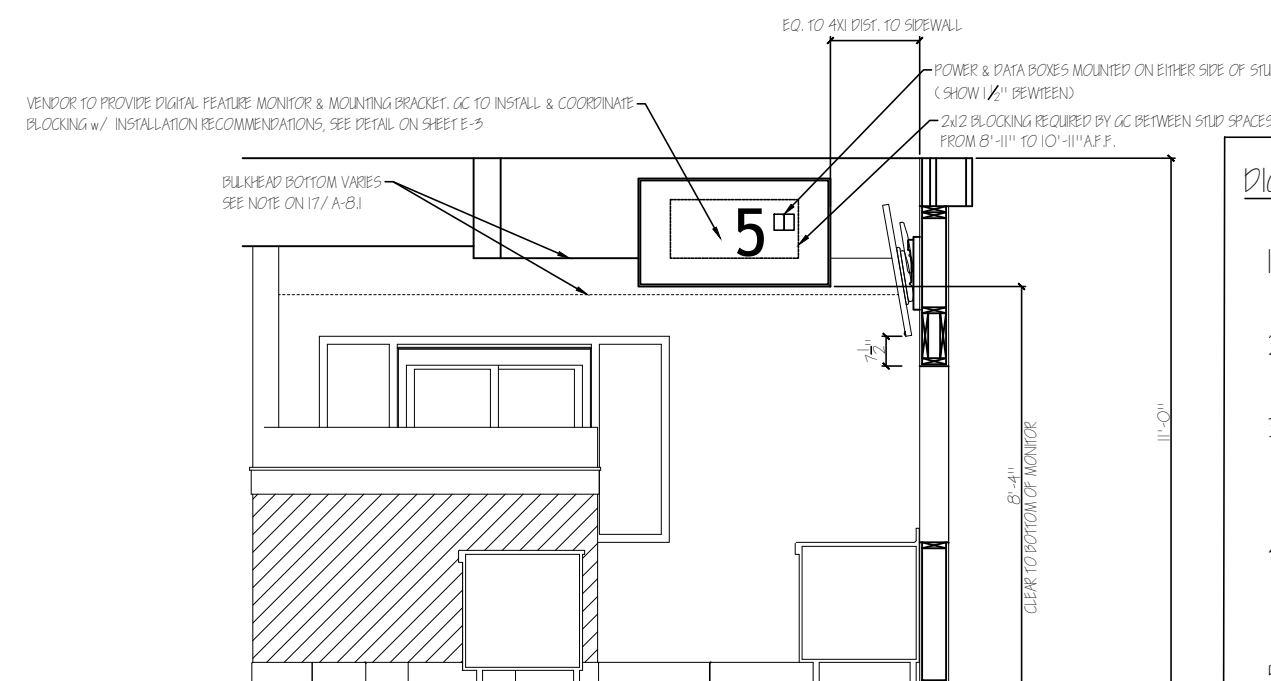


19 ELEV. - DIGITAL FEATURE BOARD

A-8.1 SCALE: 1/4" = 1'-0"


DIGITAL FEATURE BOARD INSTALL NOTES:

1. DIAGRAM RELATES TO STANDARD PROTOTYPE 11'-0" CEILING HEIGHT ONLY. GC TO VERIFY WITH OWNER FOR LOCATION ON NON TYPICAL CEILING HEIGHTS.
2. MONITOR AND MOUNTING BRACKET PROVIDED BY DIGITAL MENU BOARD SUPPLIER. 55" MONITOR REQUIRED.
3. GC TO VERIFY BRACKET MOUNTING HEIGHT W/ DIGITAL MENU BOARD SUPPLIER. PROVIDE BLOCKING AS NECESSARY.
4. BRACKET MOUNT AND ANCHOR LOCATION MAY VARY. VERIFY WITH OWNER.

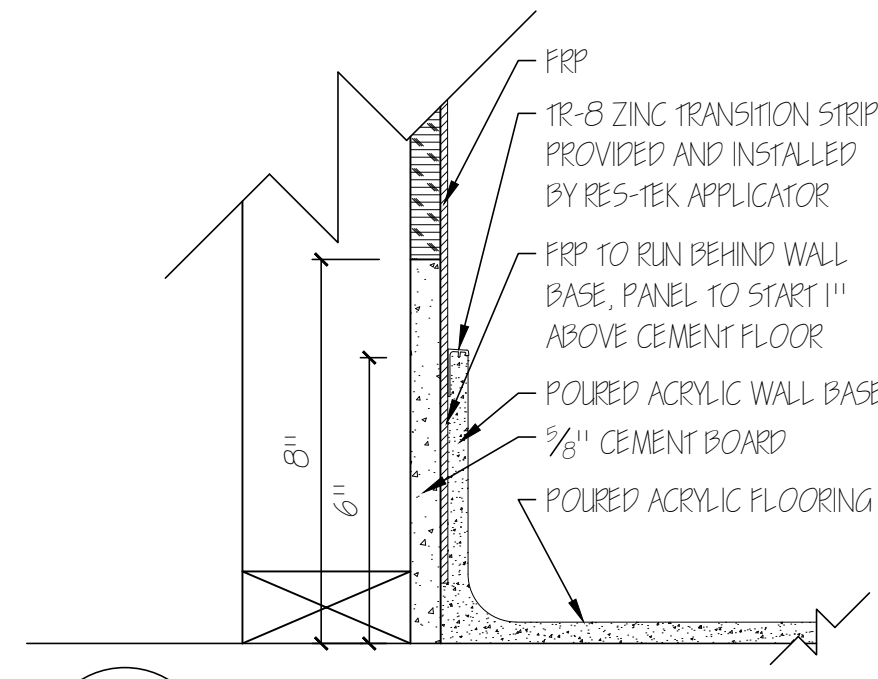


12 DETAIL - ACRYLIC WALL BASE TO FRP

A-8.1 SCALE: 3" = 1'-0"

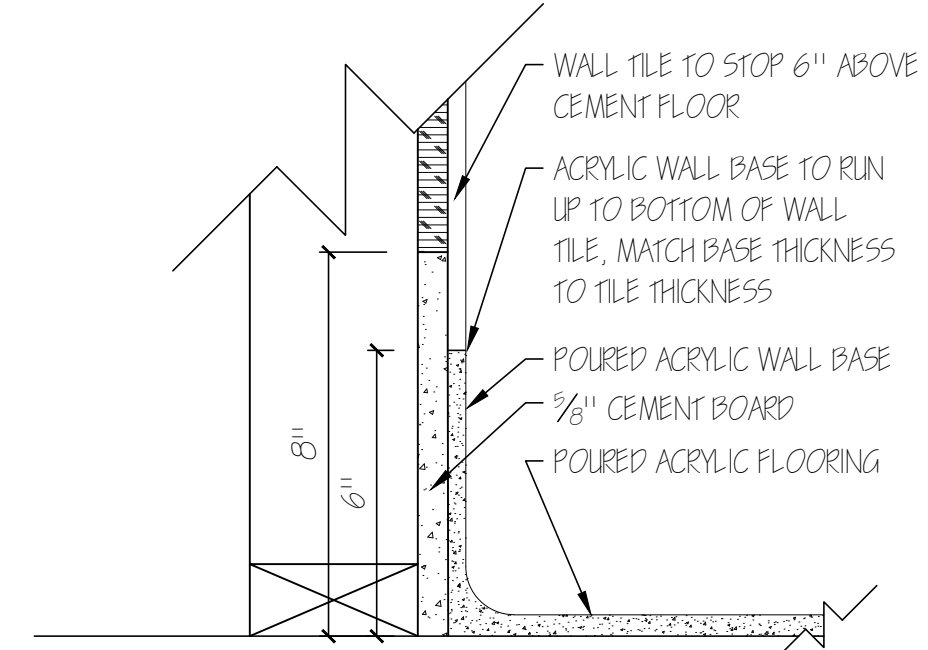


13 DETAIL - ACRYLIC WALL BASE TO TILE

A-8.1 SCALE: 3" = 1'-0"

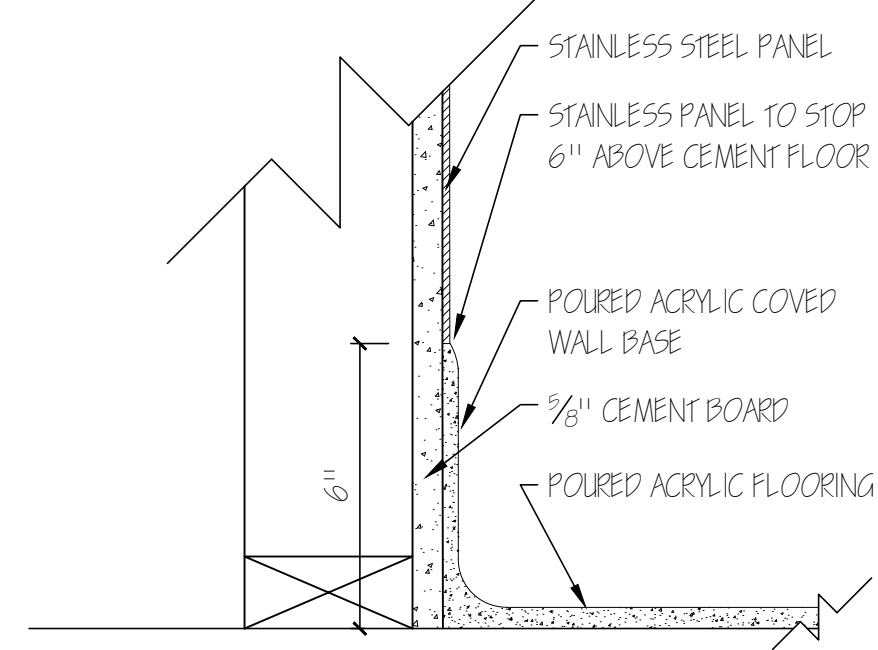


14 DETAIL - ACRYLIC WALL BASE AT S/S

A-8.1 SCALE: 3" = 1'-0"

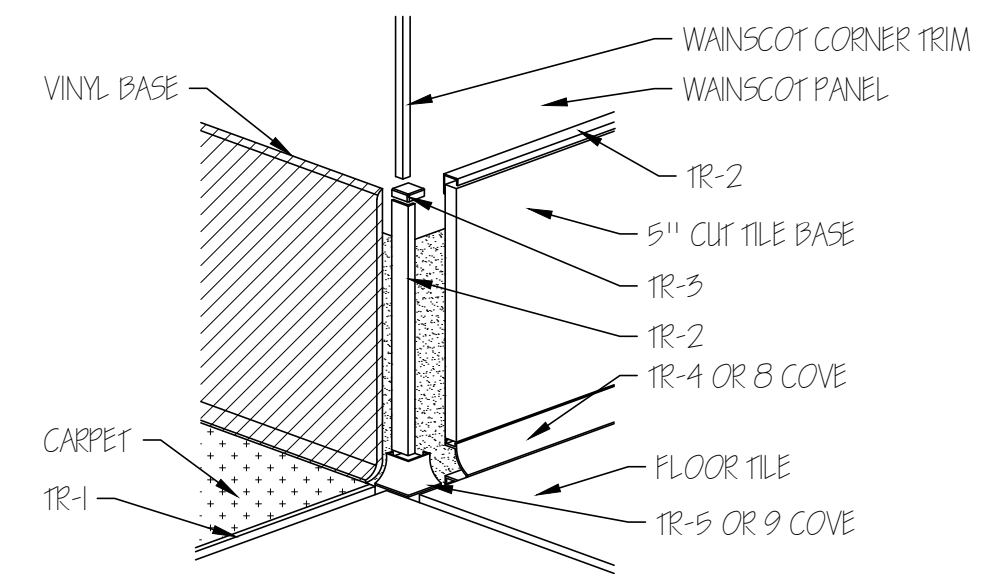

15 DETAIL - CORNER TRANSITION

A-8.1 SCALE: 3" = 1'-0"

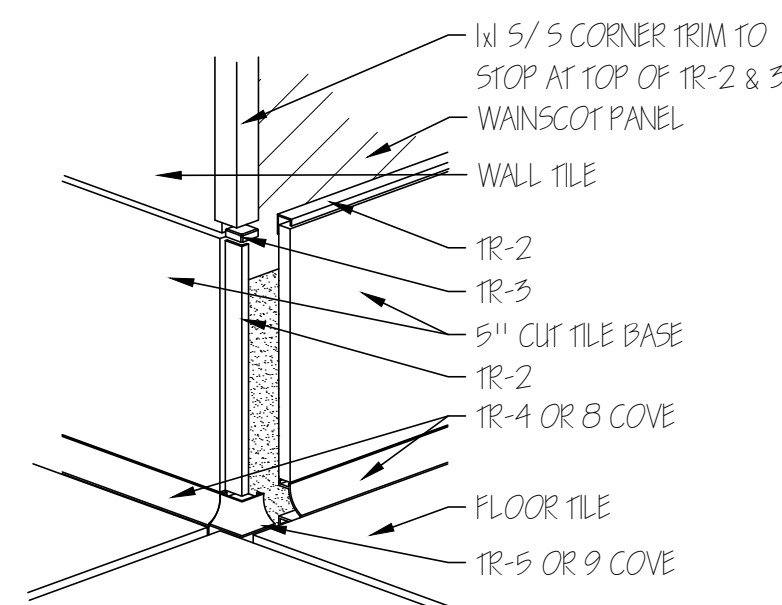

16 DETAIL - WALL TILE TO WAINSCOTING

A-8.1 SCALE: 3" = 1'-0"

WARNING: These plans are for the exclusive use of Culver Franchising System, LLC and authorized franchise holders only. No part of these plans or the design they represent may be duplicated or reproduced without permission of Culver Franchising System, LLC

CULVER FRANCHISING SYSTEM, LLC

REIMAGE 2027

CULVER'S OF SHAKOPEE, MN #0131

Sheet Contents

ELEV'S & DETAILS


Project No. Shakopee, MN #0131
Drawn By: E. ROCKWEILER
Date: 06/12/26

Sheet


A-8.1

By
Date
Revision

Culver Franchising System, LLC.
1240 Water Street
Prairie du Sac, WI 53578
608-643-7980

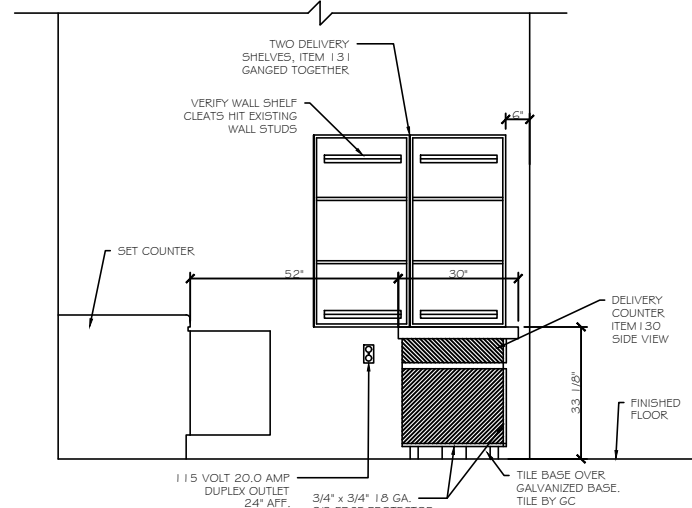

1 ELEV. - ITEM 130 AND 131
FS-1 SCALE: 1/4" = 1'-0"

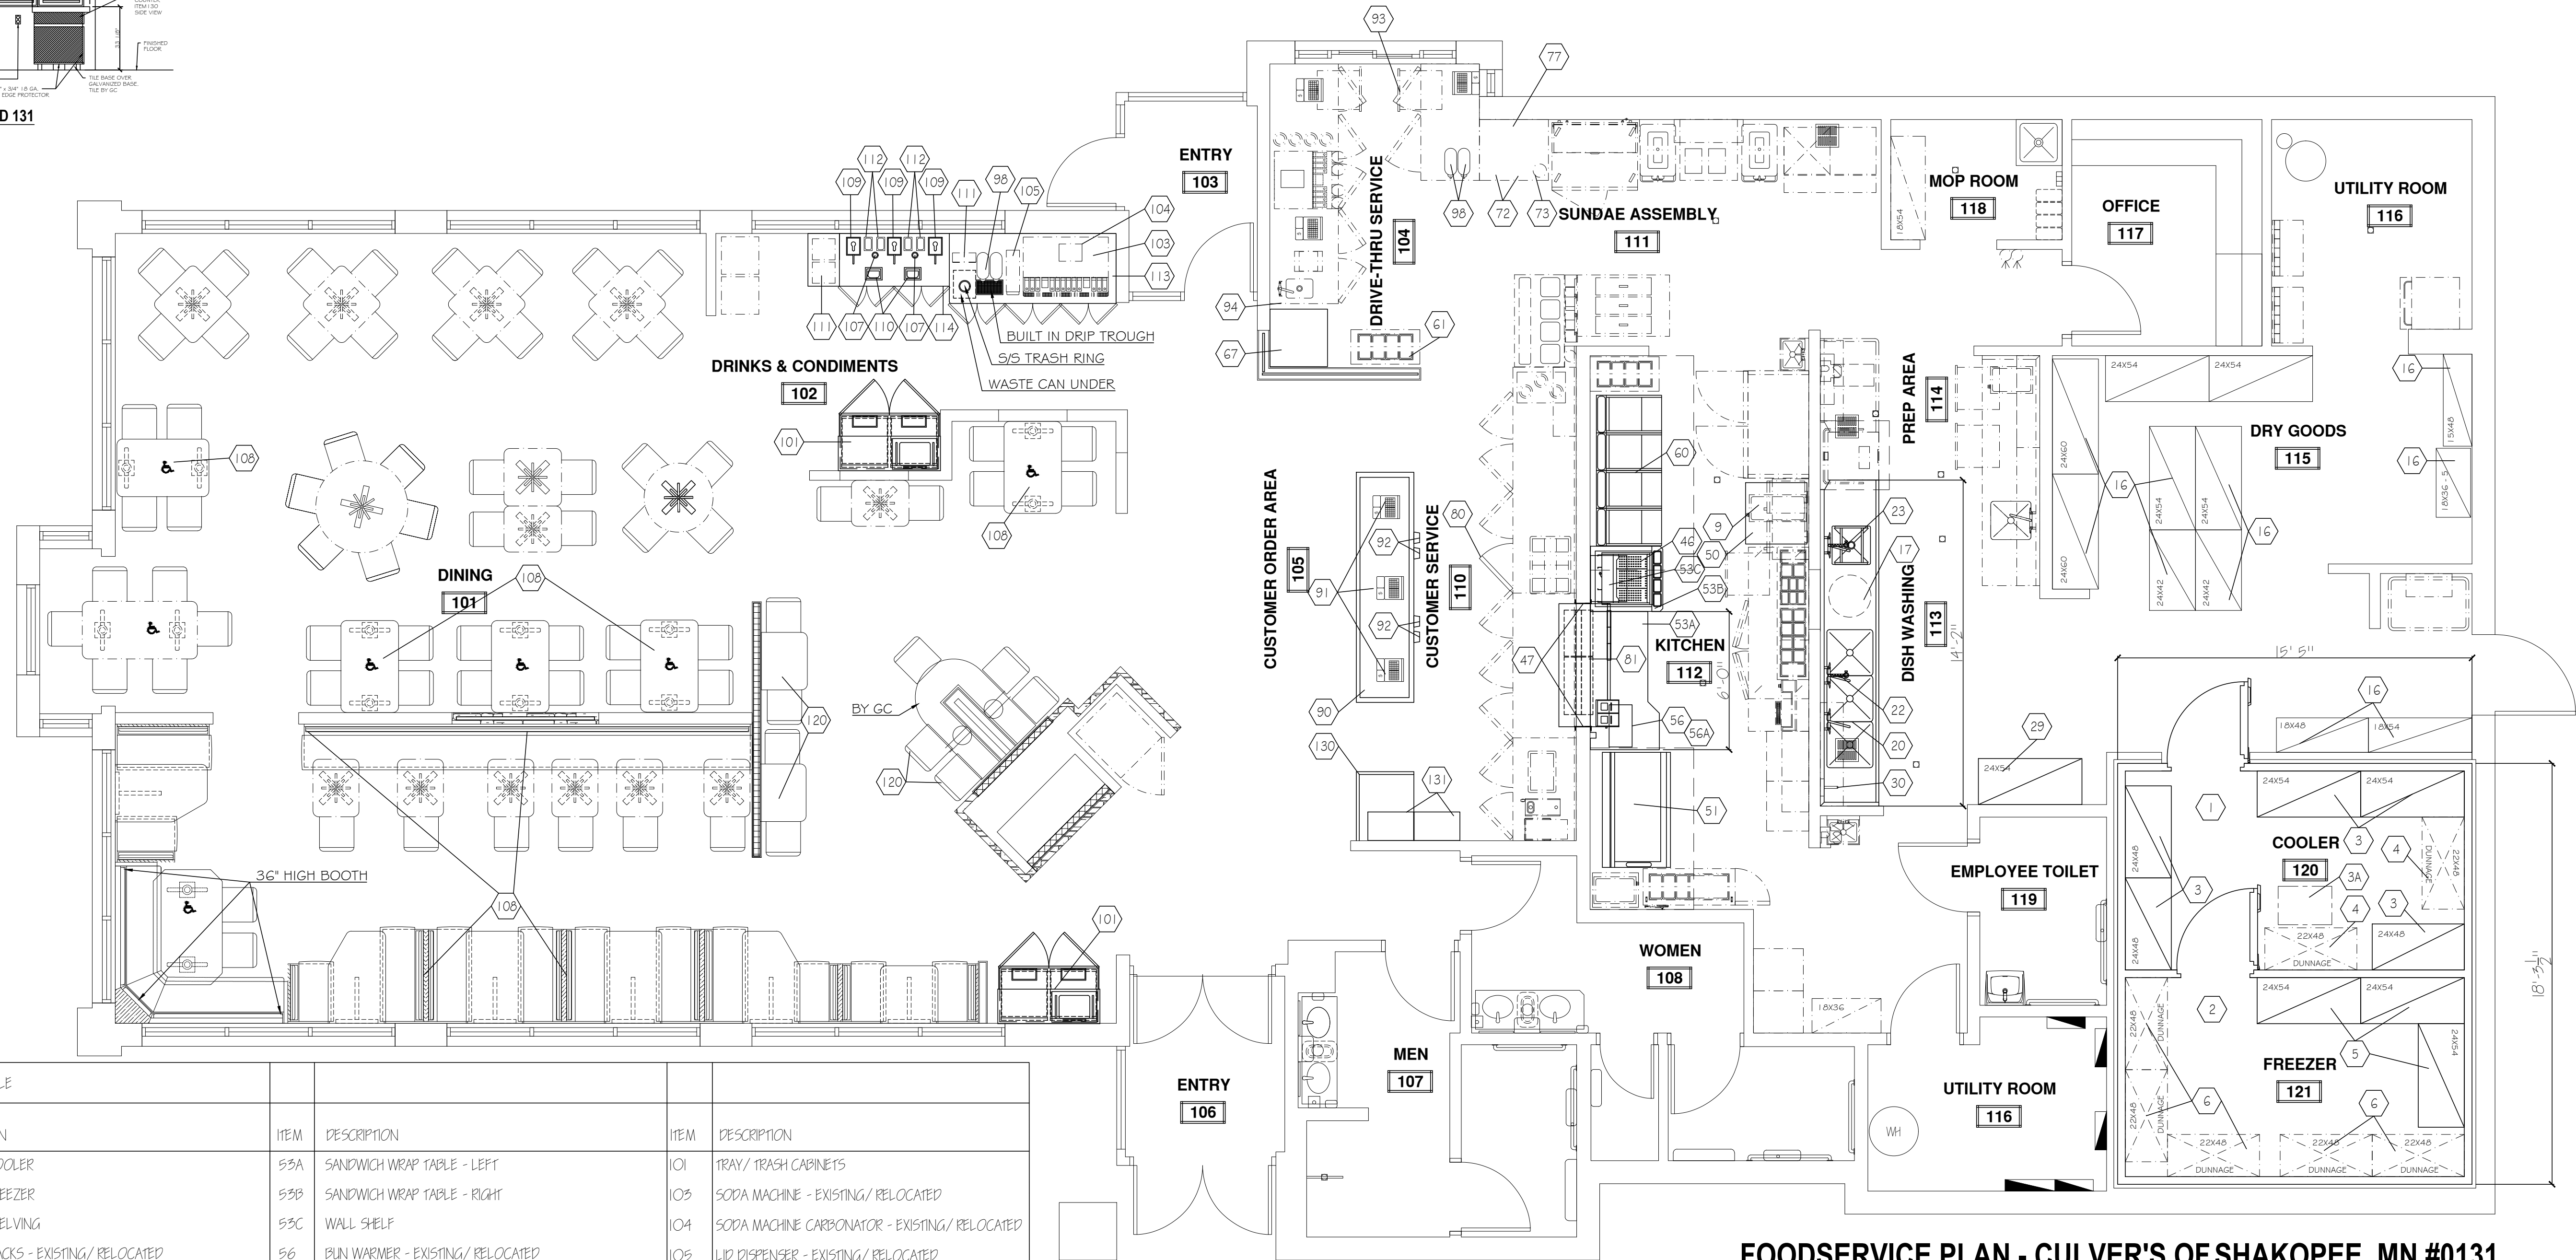

FOODSERVICE PLAN - CULVER'S OF SHAKOPEE, MN #0131
SCALE: 1/8" = 1'-0"

LINE TYPE KEY:

- - - - - EXISTING EQUIPMENT / SEATS
- NEW EQUIPMENT / SEATS
- HIDDEN LINES

EQUIPMENT SCHEDULE		
ITEM	DESCRIPTION	ITEM
1	WALK-IN COOLER	53A
2	WALK-IN FREEZER	53B
3	COOLER SHELVING	53C
3A	THAWING RACKS - EXISTING/ RELOCATED	56
4	COOLER DUNNAGE RACKS - EXISTING/ RELOCATED	56A
5	FREEZER SHELVING	60
6	FREEZER DUNNAGE RACKS - EXISTING/ RELOCATED	61
9	COOKER/ WARMER - EXISTING/ RELOCATED	67
16	DRY STORAGE SHELVING	72
17	TRASH BIN - EXISTING/ RELOCATED	73
20	DISH/ TABLES AND UTENSIL SINKS - NEW/ EXISTING	77
22	PRE-RINSE SPRAY ASSEMBLY	80
23	PRE-RINSE SPRAY ASSEMBLY	81
29	CLEAN PAN SHELVING	90
30	EYE WASH STATION	91
46	BOTTOM HEATED FRY BIN	92
47	S/ S PASS THRU TRIM	93
50	WORKTABLE	94
51	GRILL AND GRILL STAND	98
		DESCRIPTION
		101
		103
		104
		105
		107
		108
		109
		110
		111
		112
		113
		114
		120
		130
		131
		300

WARNING: These plans are for the exclusive use of Culver Franchising System, LLC and authorized franchise holders only. No part of these plans or the design they represent may be duplicated or reproduced without permission of Culver Franchising System, LLC


By	Date	Revision

Culver Franchising System, LLC
1240 Water Street
Prairie du Sac, WI 53578
608-643-7980

CULVER FRANCHISING SYSTEM, LLC
REIMAGE 2027
CULVER'S OF SHAKOPEE, MN #0131

Sheet Contents	
FOODSERVICE PLAN	
Project No.	Shakopee, MN #0131
Drawn By:	V. Young
Date:	06/12/26

Sheet
FS-1

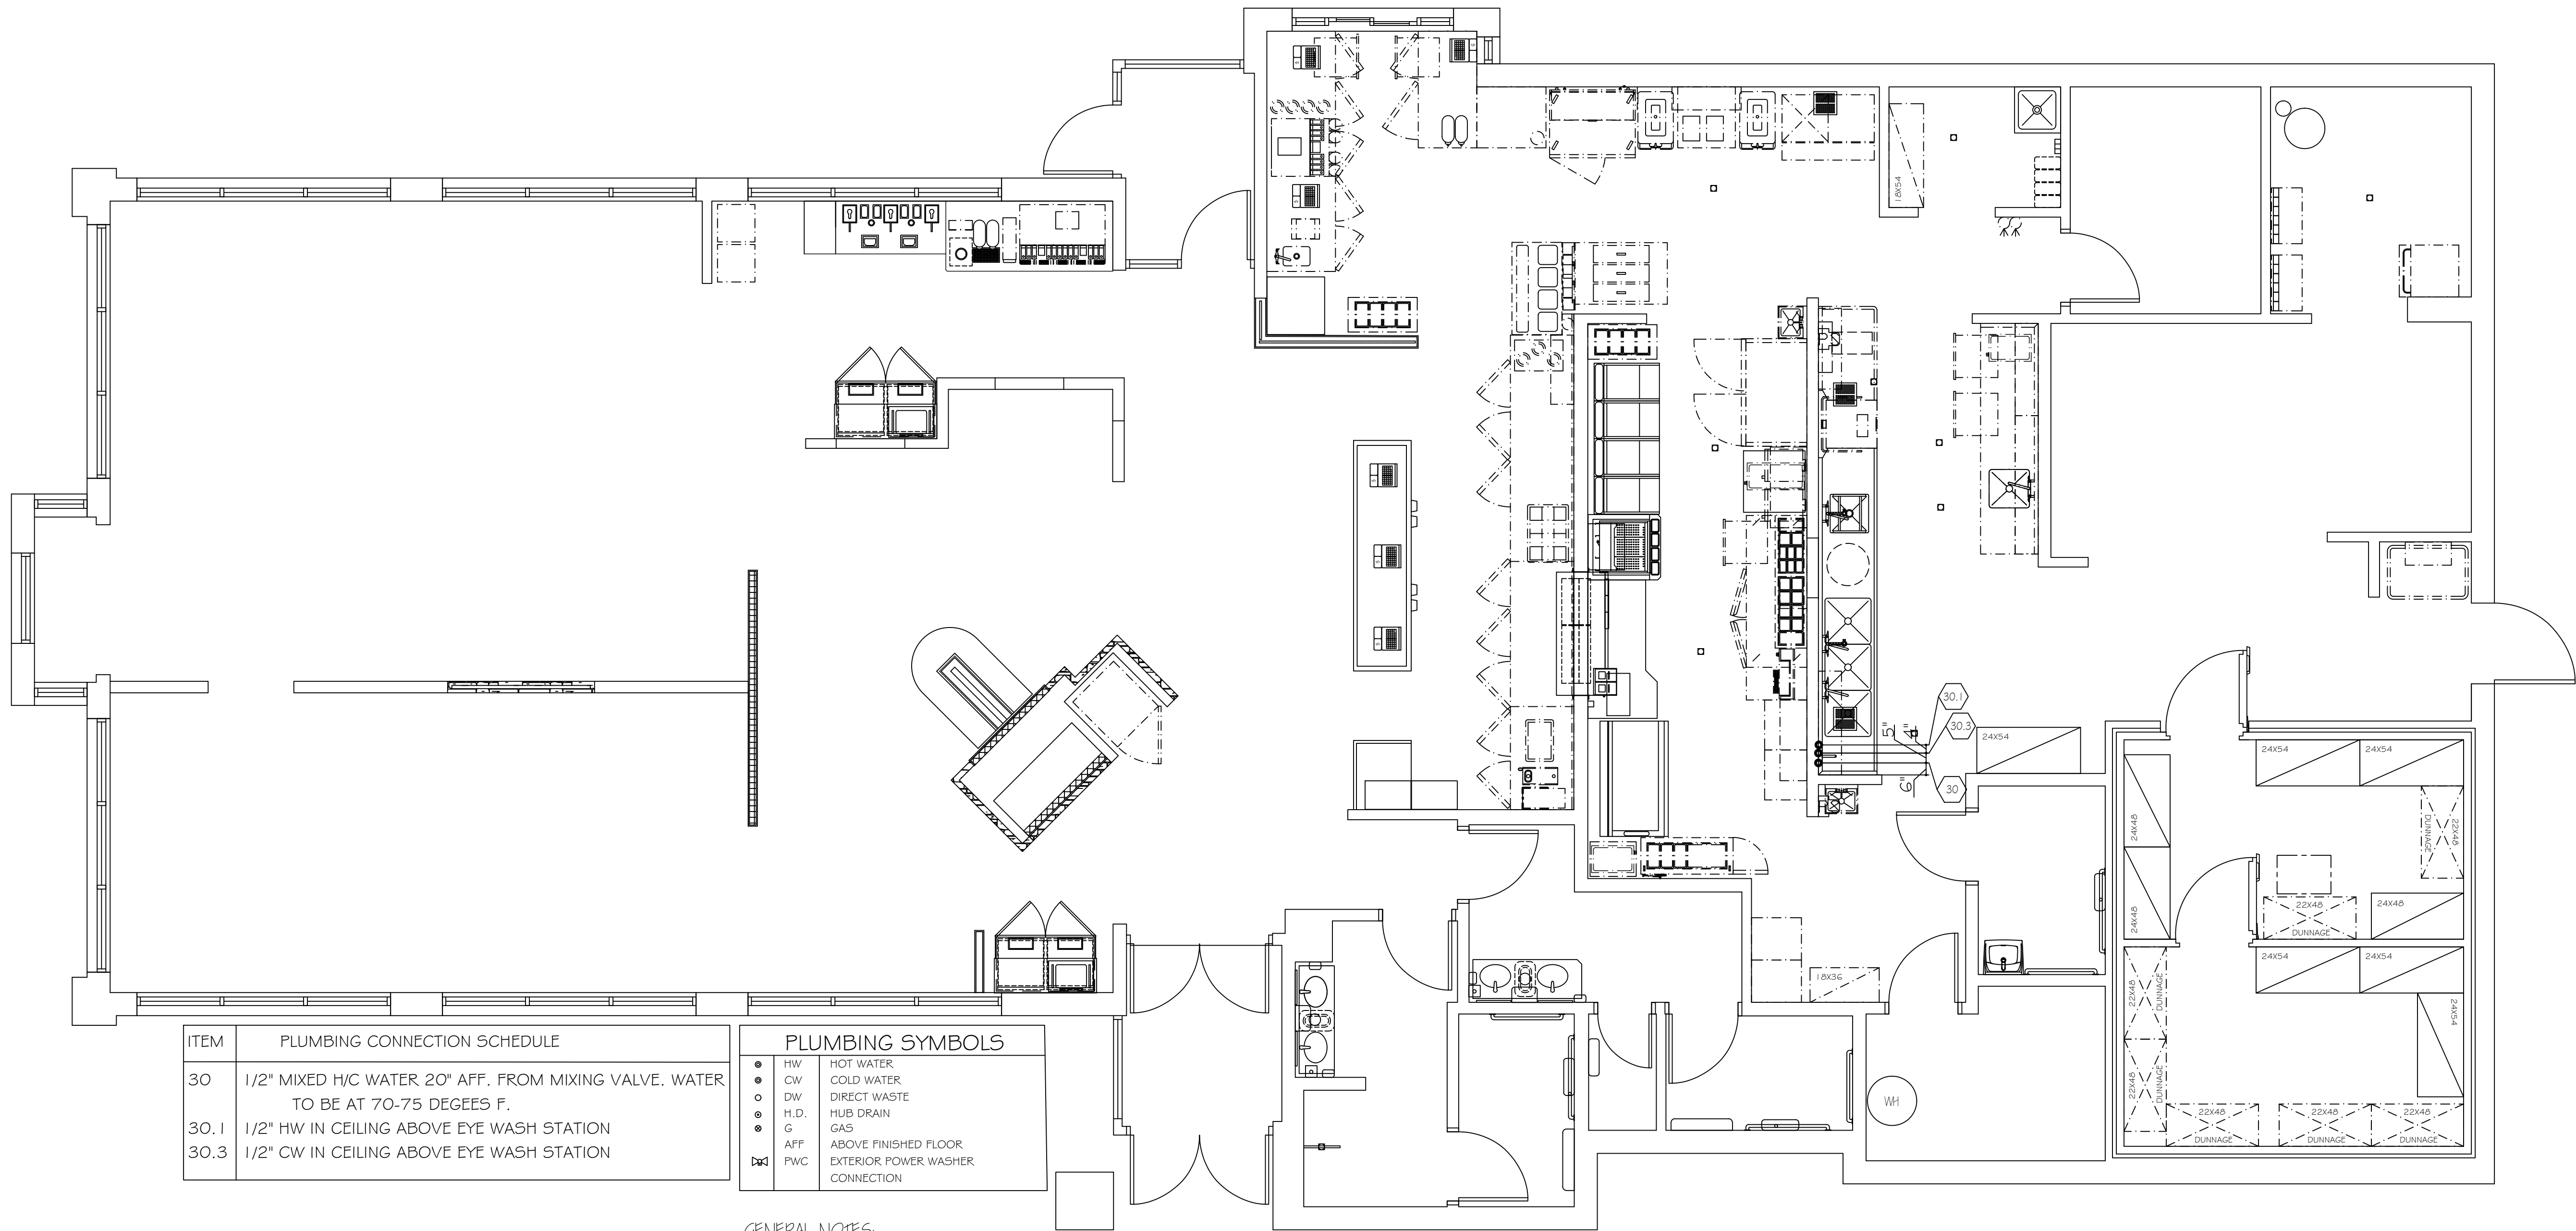


ITEM	PLUMBING CONNECTION SCHEDULE
30	1/2" MIXED H/C WATER 20" AFF. FROM MIXING VALVE. WATER TO BE AT 70-75 DEGEES F.
30.1	1/2" HW IN CEILING ABOVE EYE WASH STATION
30.3	1/2" CW IN CEILING ABOVE EYE WASH STATION

PLUMBING SYMBOLS	
• HW	HOT WATER
• CW	COLD WATER
• DW	DIRECT WASTE
• H.D.	HUB DRAIN
• G	GAS
• AFF	ABOVE FINISHED FLOOR
• FWC	EXTERIOR POWER WASHER CONNECTION

GENERAL NOTES:

- ALL EXISTING ROUGH-INS NEED TO BE FIELD VERIFIED. REUSE EXISTING ROUGH-INS WHERE POSSIBLE.
- ALL EXISTING FLOOR DRAINS TO REMAIN IN EXISTING LOCATIONS.

FOODSERVICE PLUMBING PLAN - CULVER'S OF SHAKOPEE, MN #0131
SCALE: 1/4" = 1'-0"

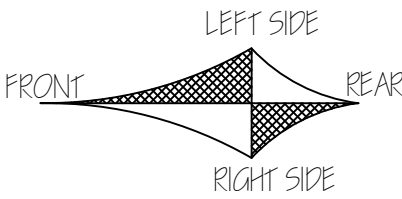

WARNING: These plans are for the exclusive use of Culver Franchising System, LLC and authorized franchise holders only. No part of these plans or the design they represent may be duplicated or reproduced without permission of Culver Franchising System, LLC


CULVER FRANCHISING SYSTEM, LLC
REIMAGE 2027
CULVER'S OF SHAKOPEE, MN #0131

Sheet Contents
FOODSERVICE PLUMBING PLAN
Project No. Shakopee, MN #0131
Drawn By: V. Young
Date: 06/12/26

Sheet
FS-2

Date	Revision	By

Culver Franchising System, LLC
1240 Water Street
Prairie du Sac, WI 53578
608-643-7980

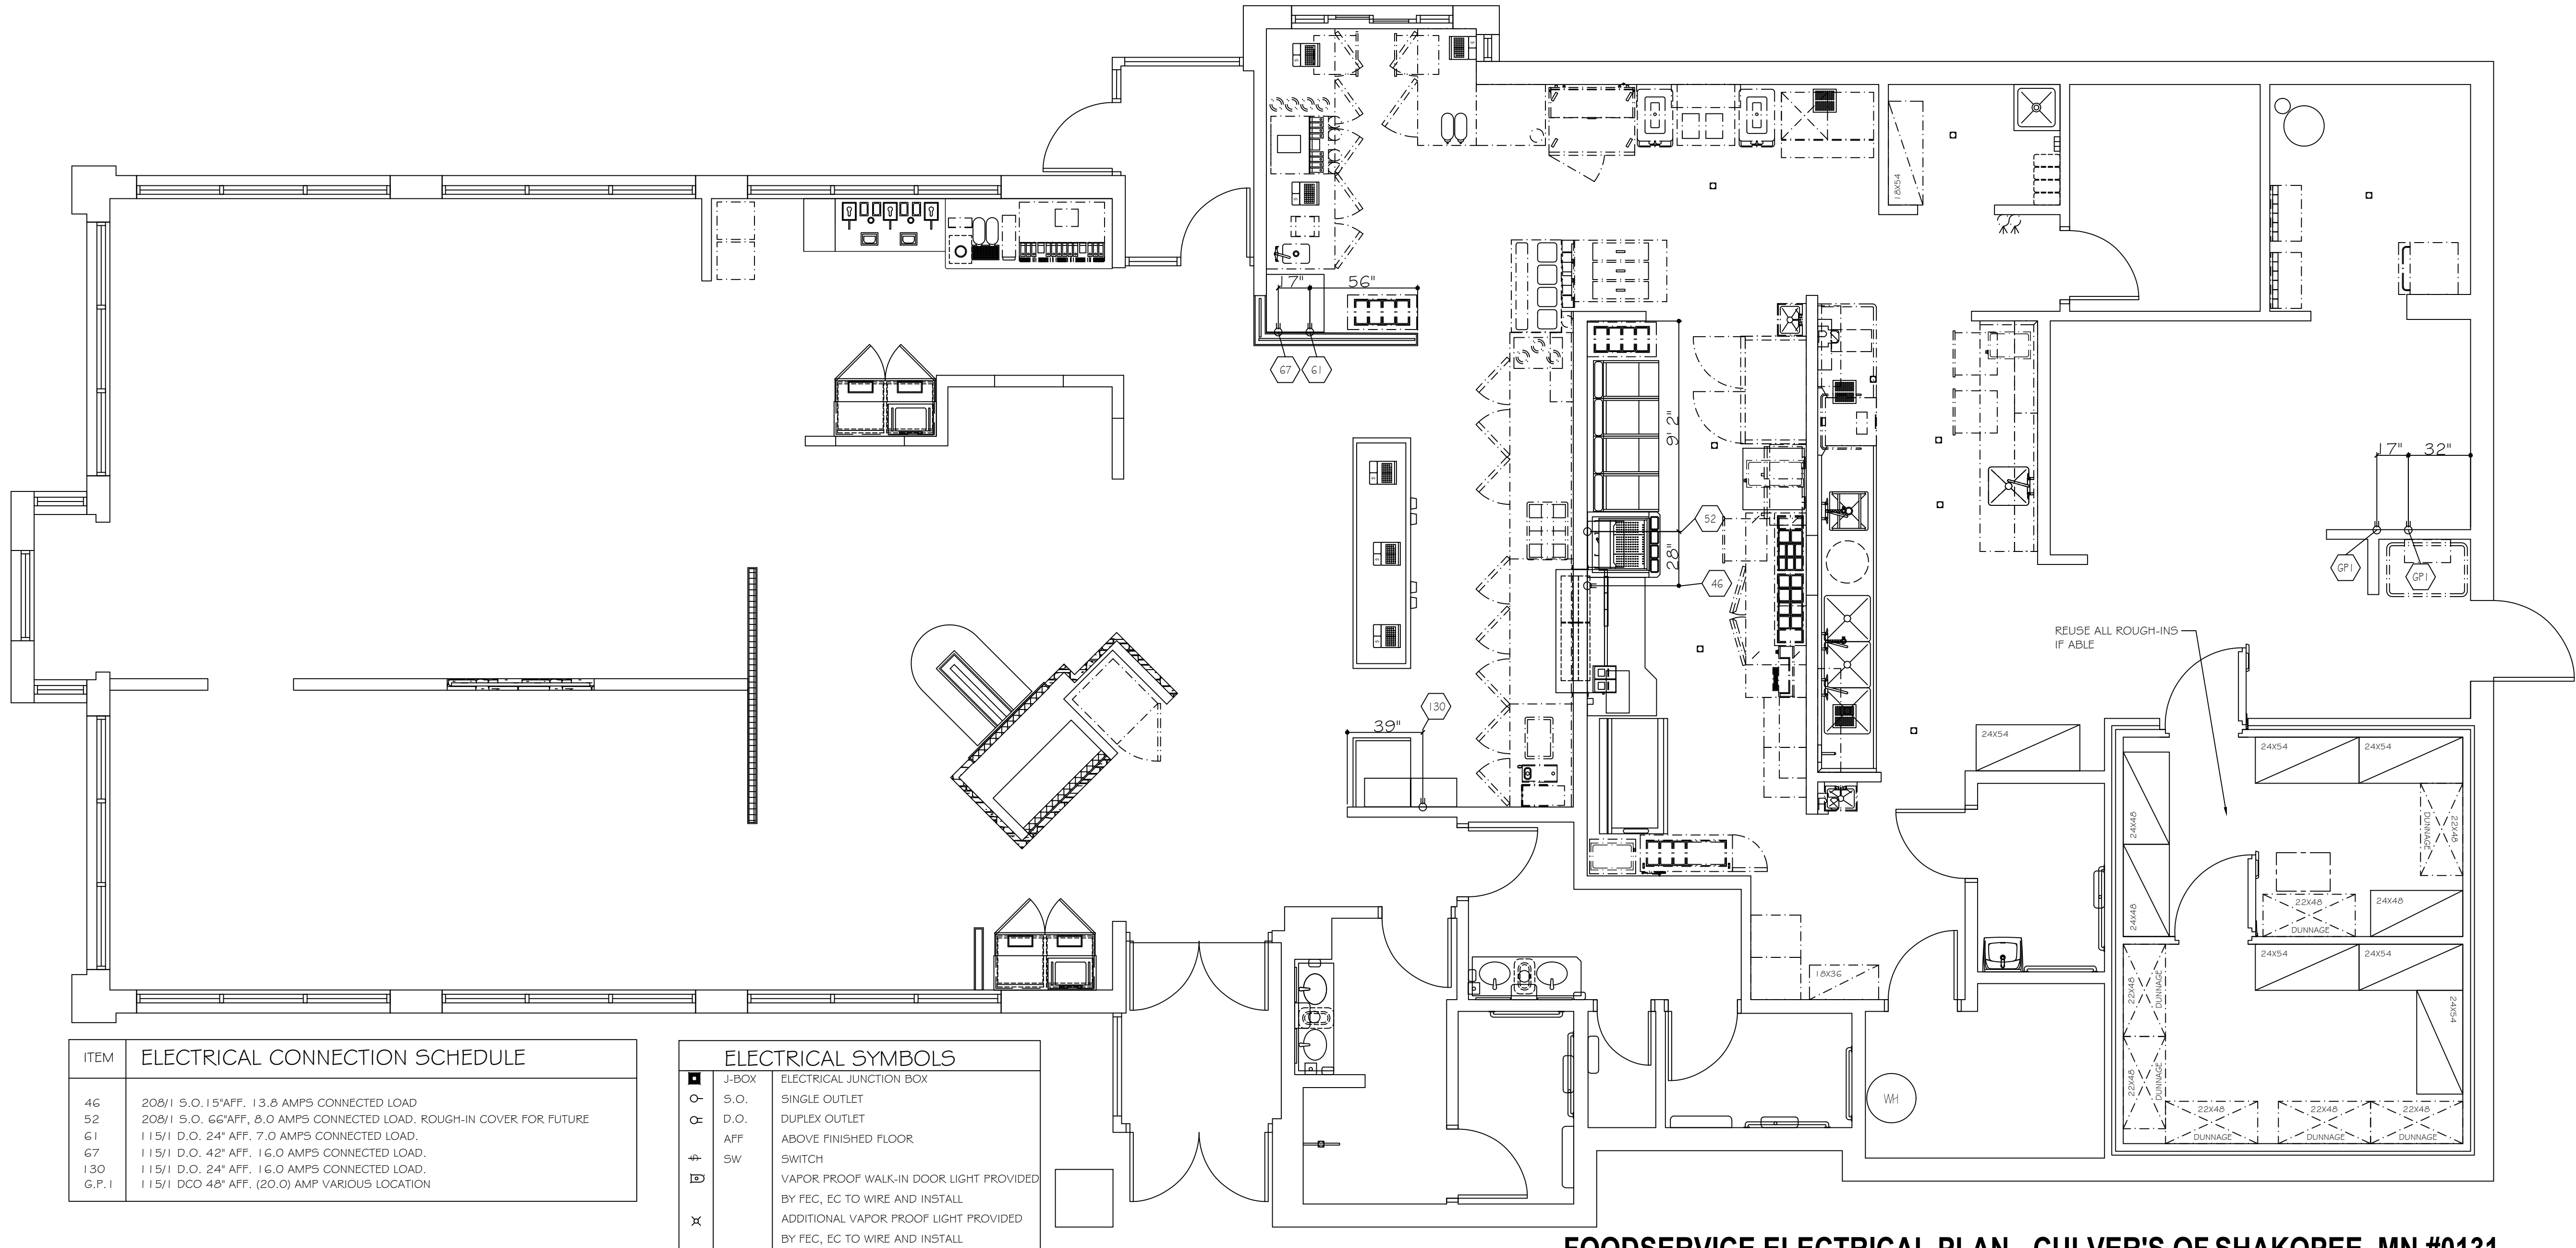


ITEM	ELECTRICAL CONNECTION SCHEDULE
46	208/1 S.O. 15" AFF. 13.8 AMPS CONNECTED LOAD
52	208/1 S.O. 66" AFF. 8.0 AMPS CONNECTED LOAD. ROUGH-IN COVER FOR FUTURE
61	115/1 D.O. 24" AFF. 7.0 AMPS CONNECTED LOAD.
67	115/1 D.O. 42" AFF. 16.0 AMPS CONNECTED LOAD.
130	115/1 D.O. 24" AFF. 16.0 AMPS CONNECTED LOAD.
G.P.1	115/1 DCO 48" AFF. (20.0) AMP VARIOUS LOCATION

ELECTRICAL SYMBOLS	
J-BOX	ELECTRICAL JUNCTION BOX
S.O.	SINGLE OUTLET
D.O.	DUPLEX OUTLET
AFF	ABOVE FINISHED FLOOR
SW	SWITCH
VAPOR PROOF WALK-IN DOOR LIGHT PROVIDED BY FEC, EC TO WIRE AND INSTALL	
ADDITIONAL VAPOR PROOF LIGHT PROVIDED BY FEC, EC TO WIRE AND INSTALL	

GENERAL NOTES:
1. ALL EXISTING ROUGH-INS NEED TO BE FIELD VERIFIED.
REUSE EXISTING ROUGH-INS WHERE POSSIBLE.

FOODSERVICE ELECTRICAL PLAN - CULVER'S OF SHAKOPEE, MN #0131
SCALE: 1/4" = 1'-0"

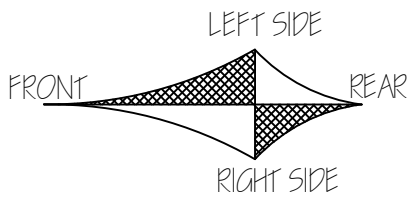

WARNING: These plans are for the exclusive use of Culver Franchising System, LLC and authorized franchise holders only. No part of these plans or the design they represent may be duplicated or reproduced without permission of Culver Franchising System, LLC

CULVER FRANCHISING SYSTEM, LLC
REIMAGE 2027
CULVER'S OF SHAKOPEE, MN #0131

Sheet Contents
FOODSERVICE ELECTRICAL PLAN
Project No. Shakopee, MN #0131
Drawn By: V. Young
Date: 06/12/26

Sheet
FS-3

Culver Franchising System, LLC
1240 Water Street
Prairie du Sac, WI 53578
608-643-7980

By			
Date			
Revision			